GUARANTEED FENCE CORP

FIN. PROJ. ID 441234-1-52-01

SHEET 1 OF 120

SHEET NO. 101

ROADWAY PLAN SCALE: 1" = 20'

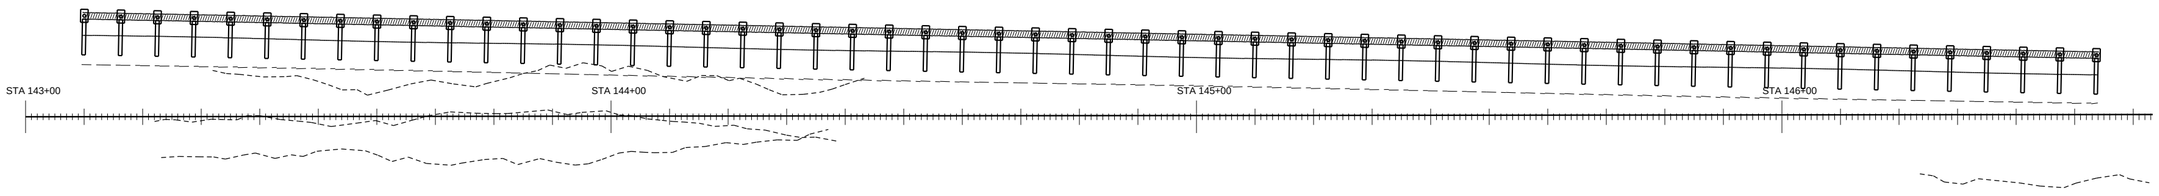


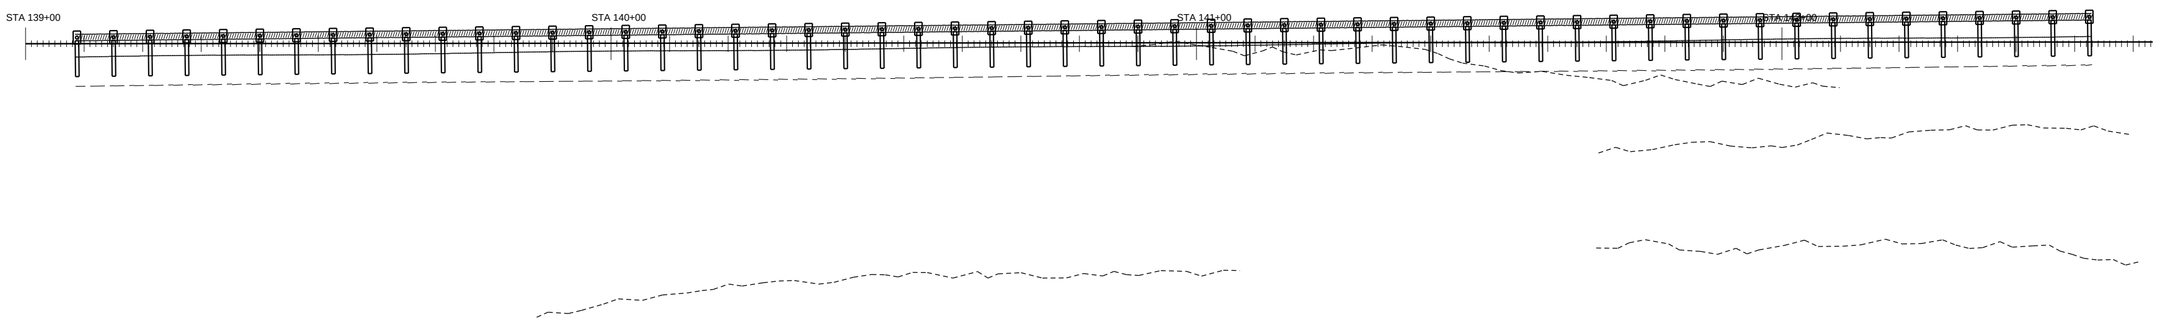


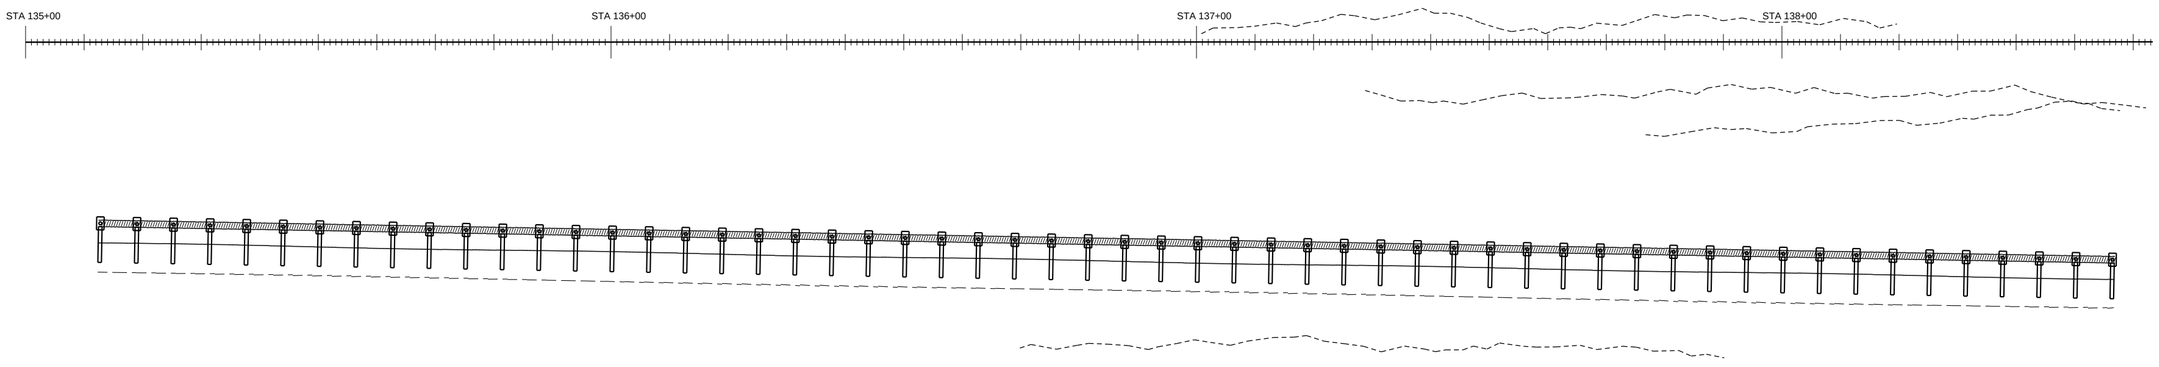


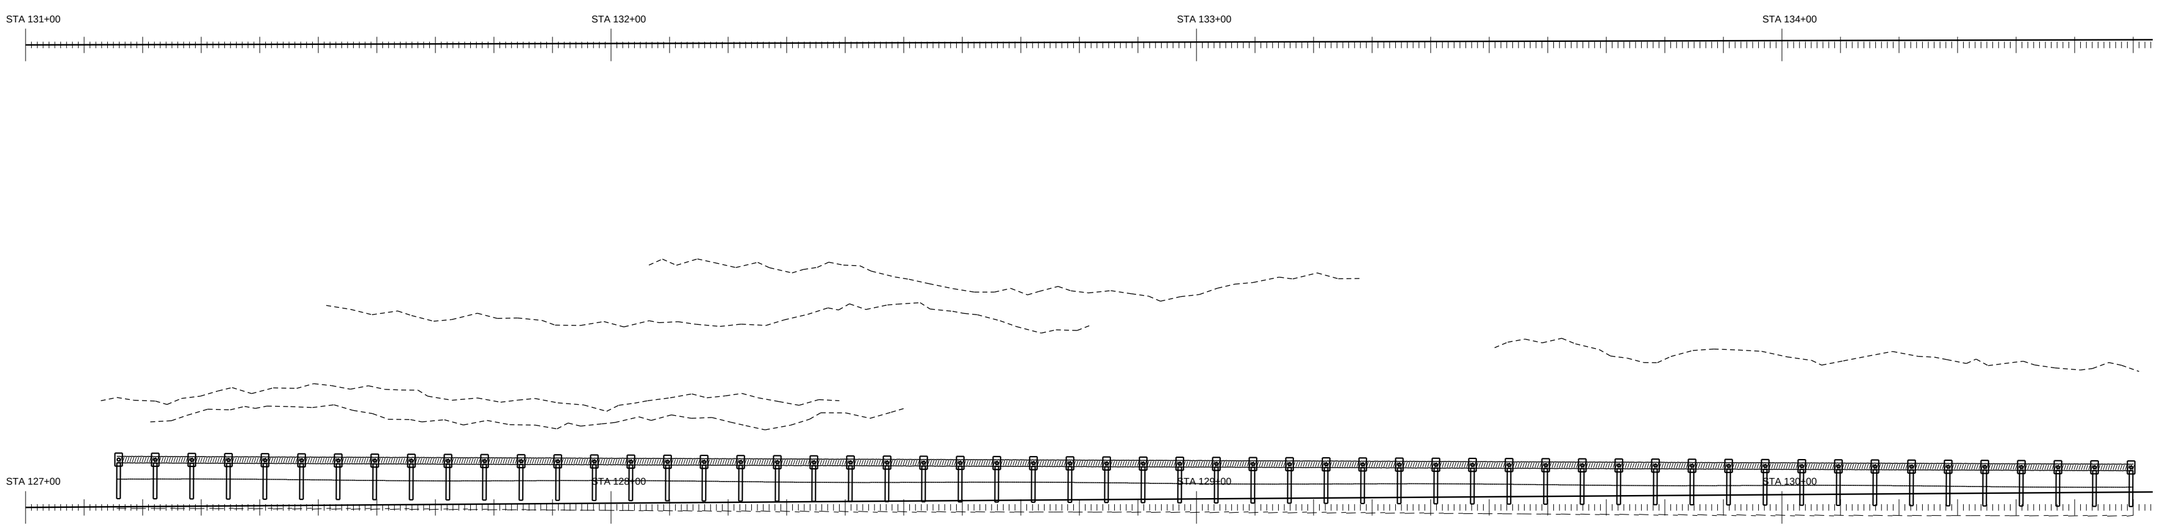


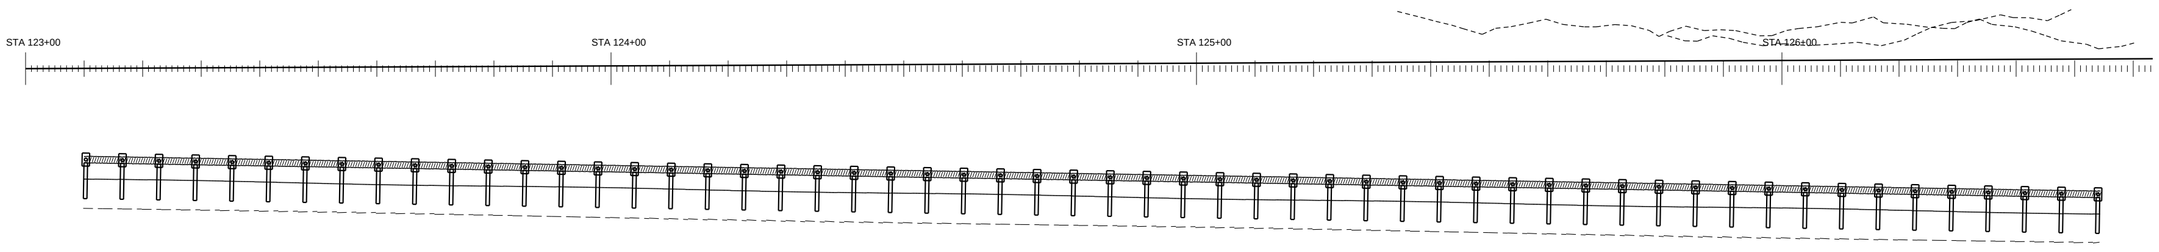


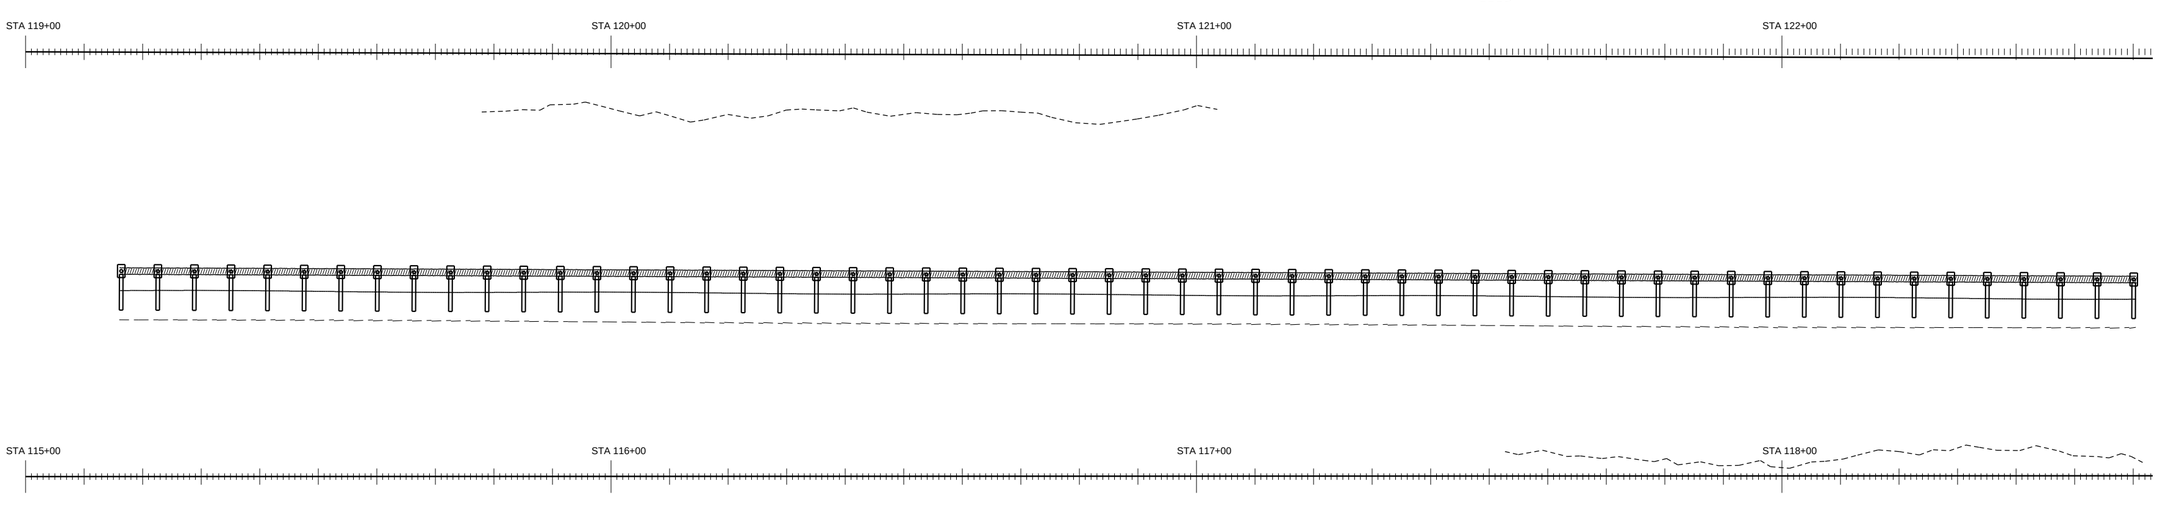


PAY ITEM 536-1-1 GUARDRAIL ROADWAY (TL-3)

PAY ITEM 536-85-24 END TREATMENT

GUARANTEED FENCE CORP

FIN. PROJ. ID 441234-1-52-01

SHEET 2 OF 120

SHEET NO. 102

ROADWAY PLAN SCALE: 1" = 20'

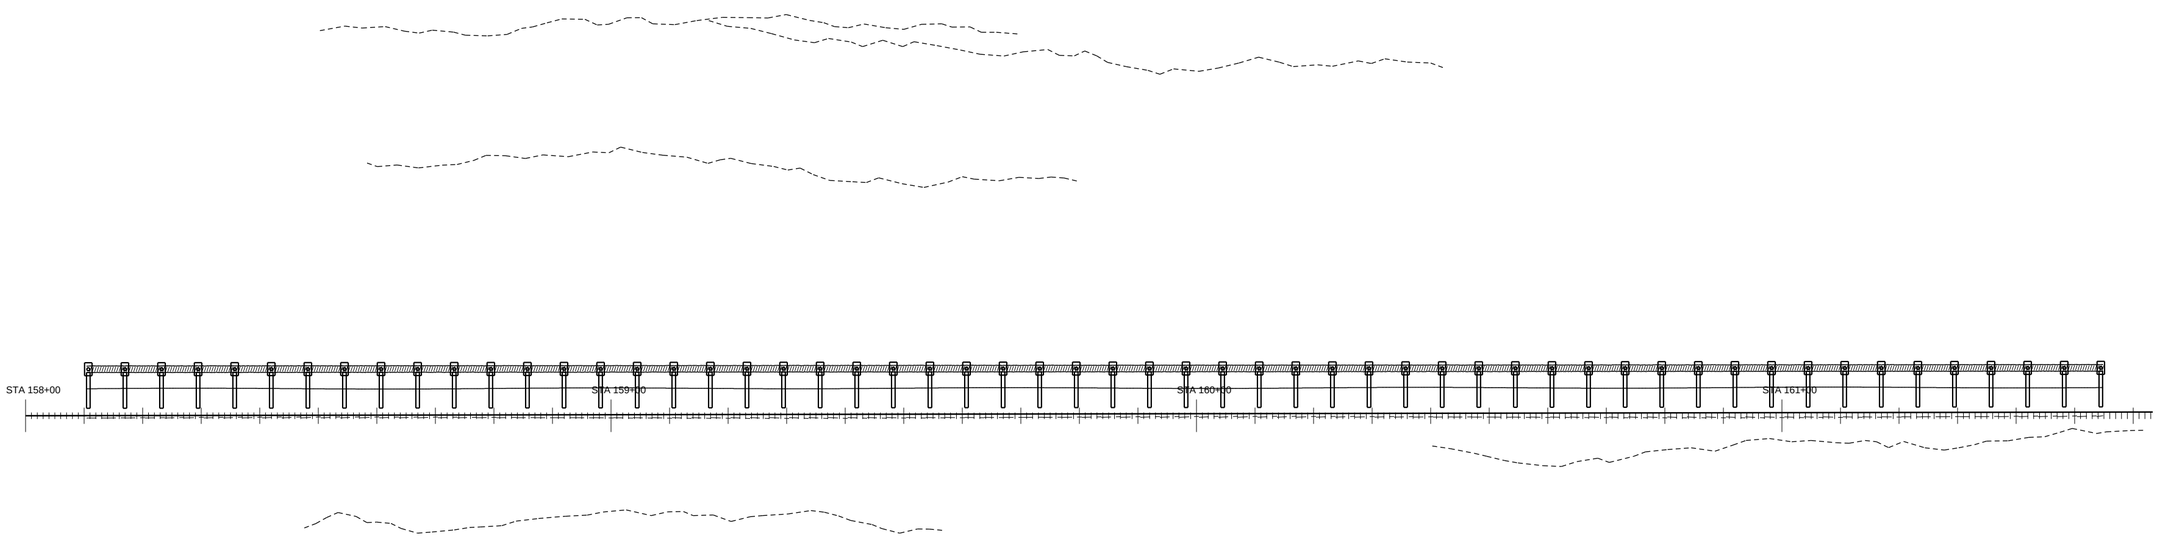


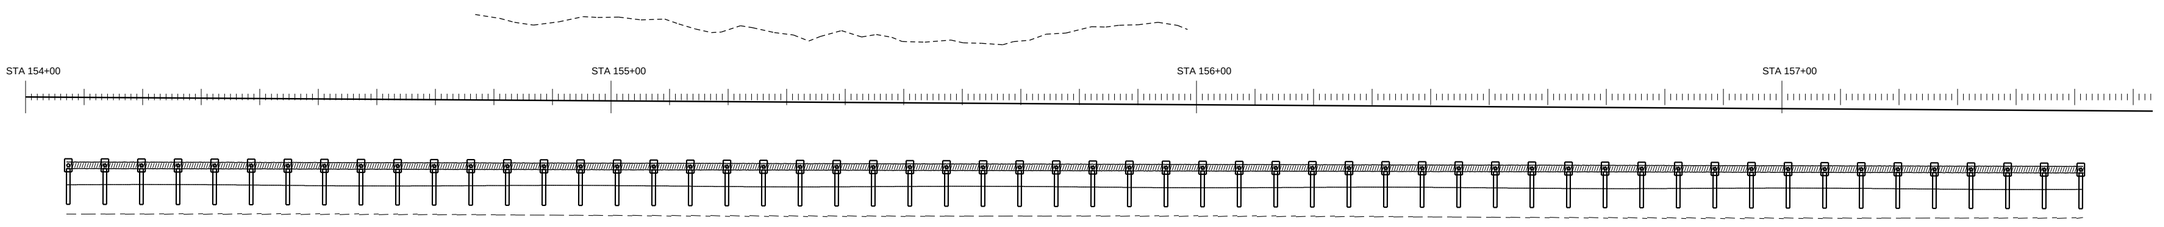


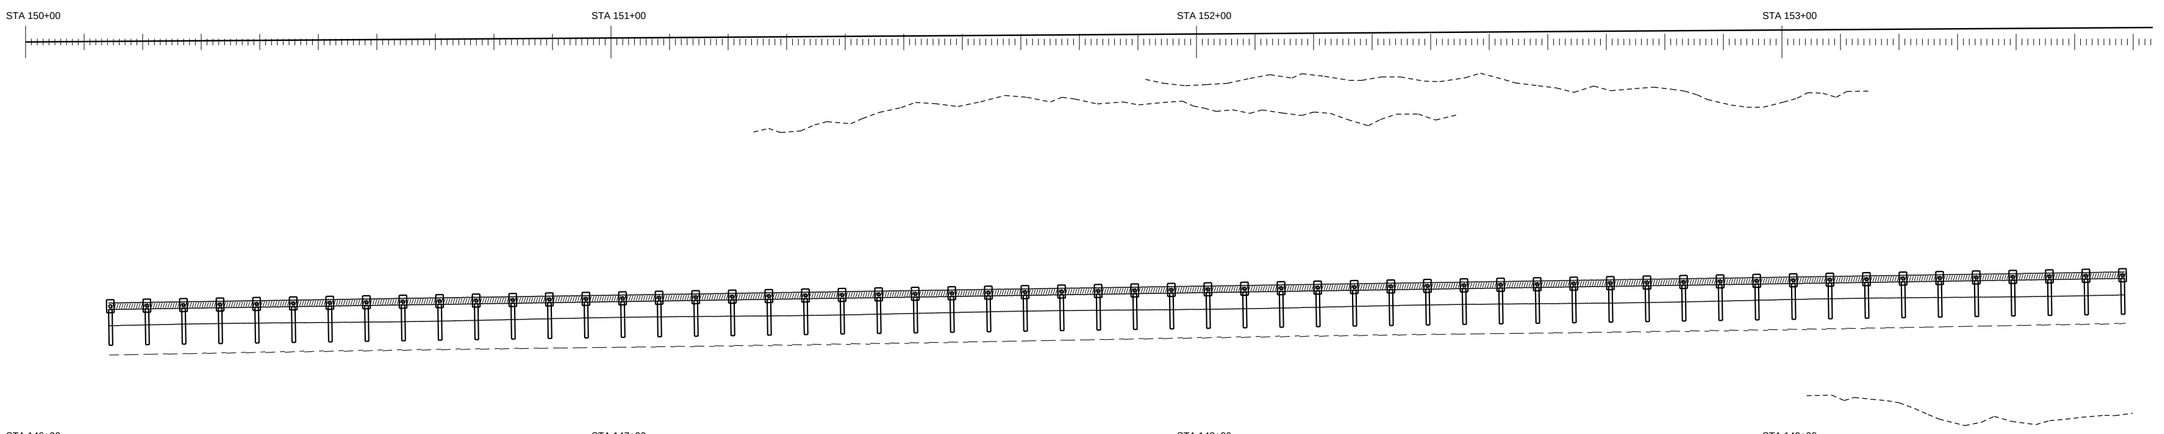


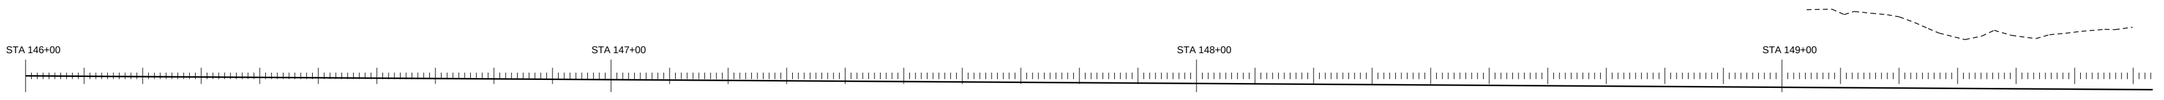


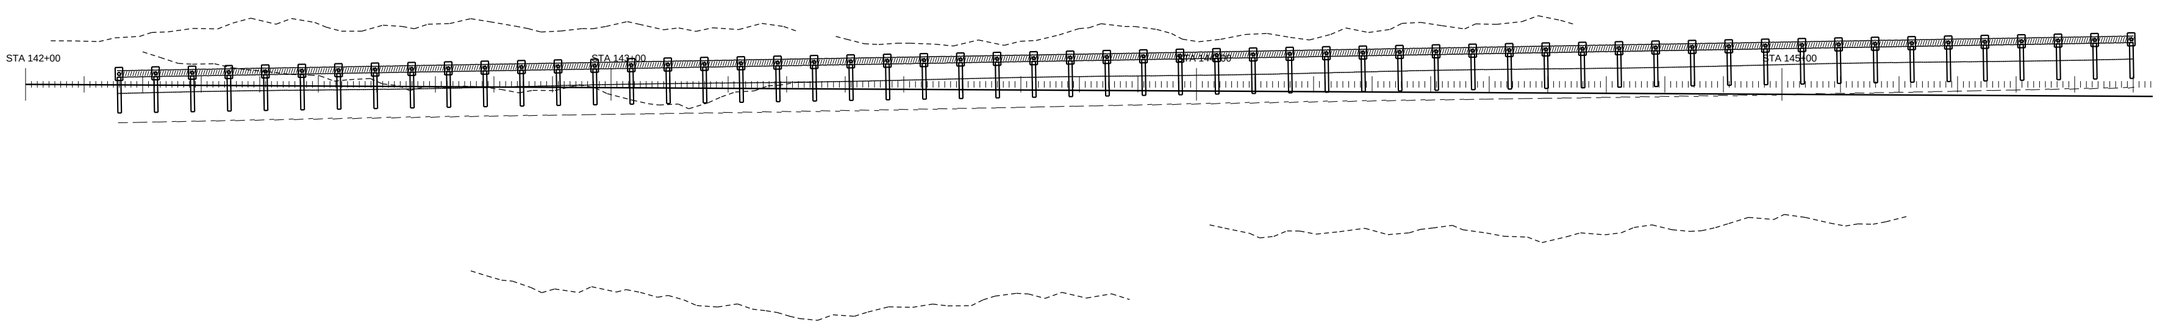


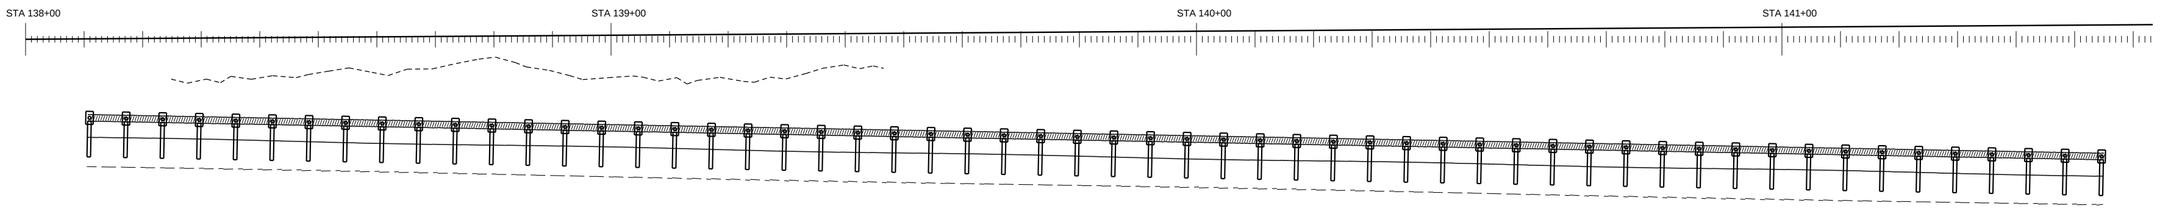


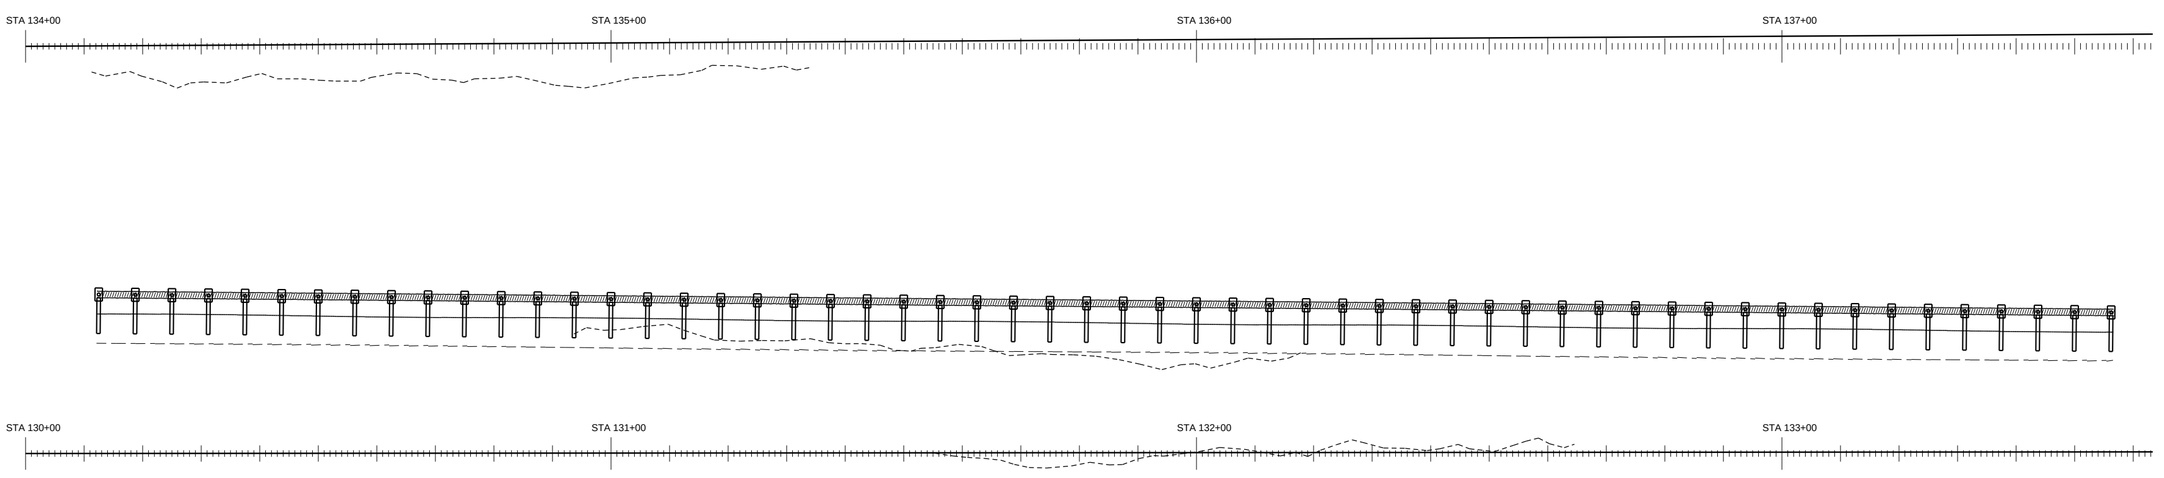





PAY ITEM 536-1-1 GUARDRAIL ROADWAY (TL-3)

PAY ITEM 536-85-24 END TREATMENT

GUARANTEED FENCE CORP

FIN. PROJ. ID 441234-1-52-01

SHEET 3 OF 120

SHEET NO. 103

ROADWAY PLAN SCALE: 1" = 20'




PAY ITEM 536-1-1 GUARDRAIL ROADWAY (TL-3)

PAY ITEM 536-85-24 END TREATMENT

GUARANTEED FENCE CORP

FIN. PROJ. ID 441234-1-52-01

SHEET 4 OF 120

SHEET NO. 104

ROADWAY PLAN SCALE: 1" = 20'

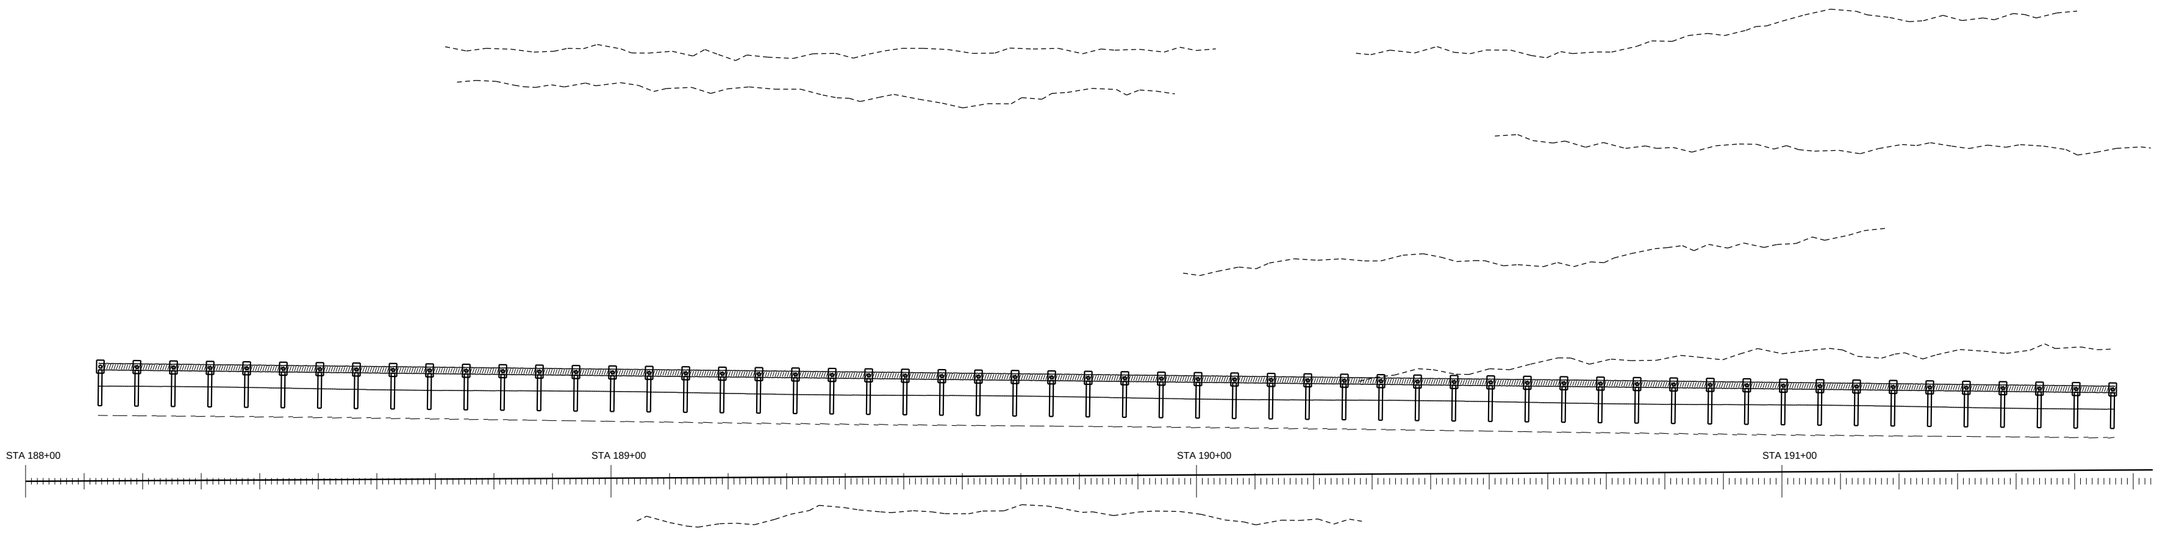


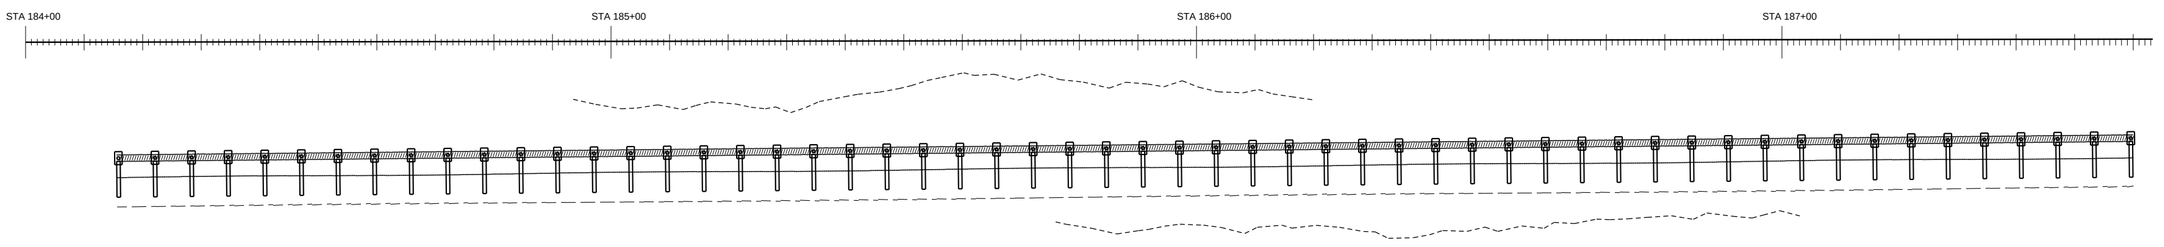


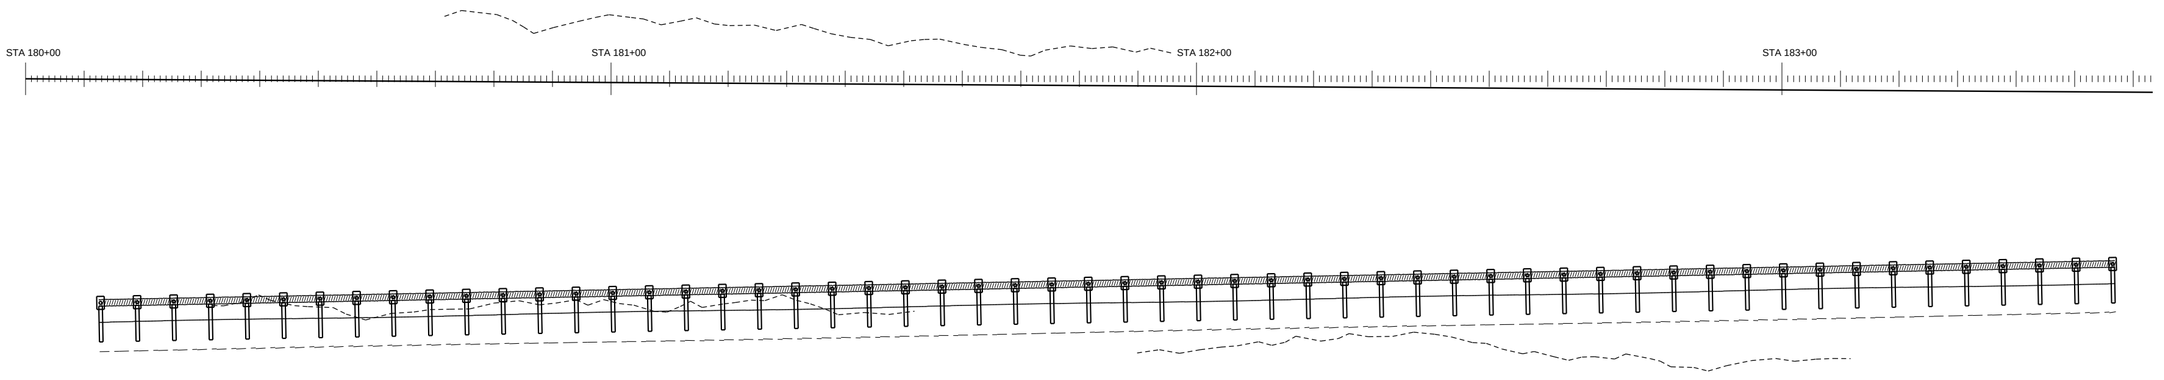


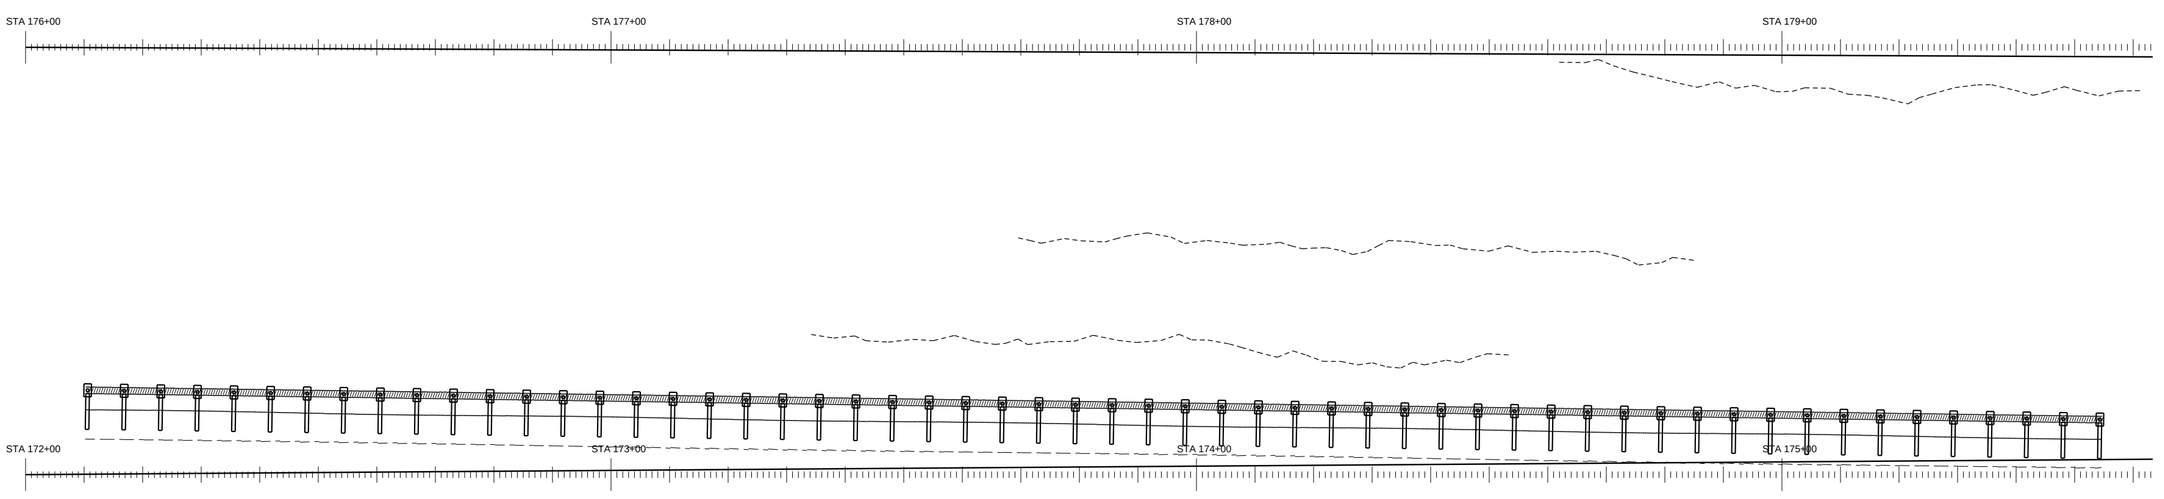


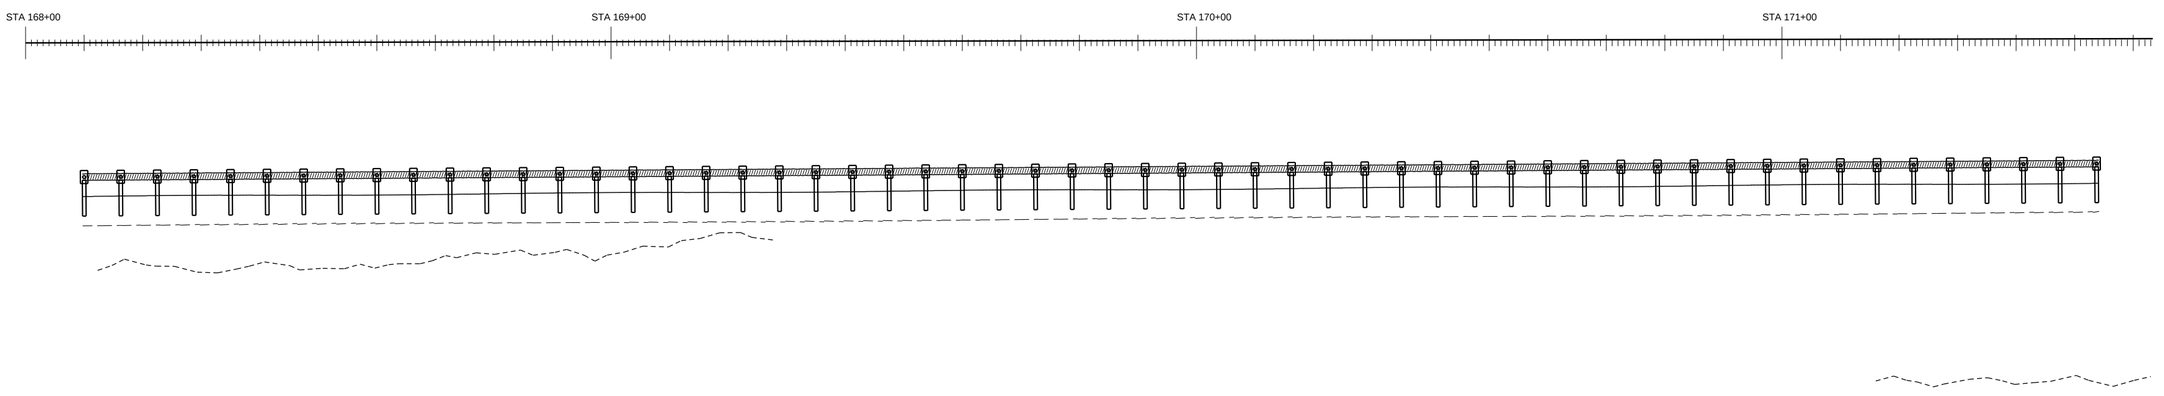


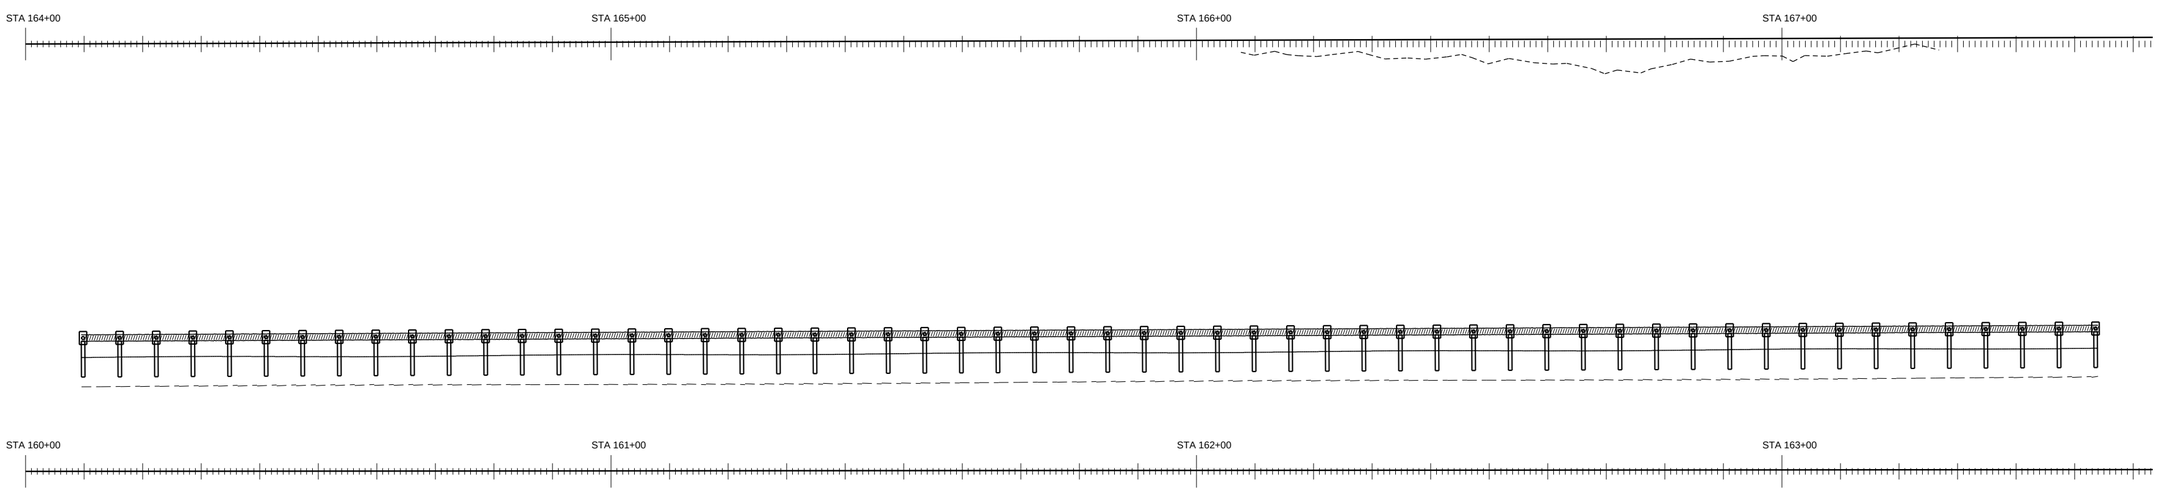


PAY ITEM 536-1-1 GUARDRAIL ROADWAY (TL-3)

PAY ITEM 536-85-24 END TREATMENT

GUARANTEED FENCE CORP

FIN. PROJ. ID 441234-1-52-01

SHEET 5 OF 120

SHEET NO. 105

ROADWAY PLAN SCALE: 1" = 20'

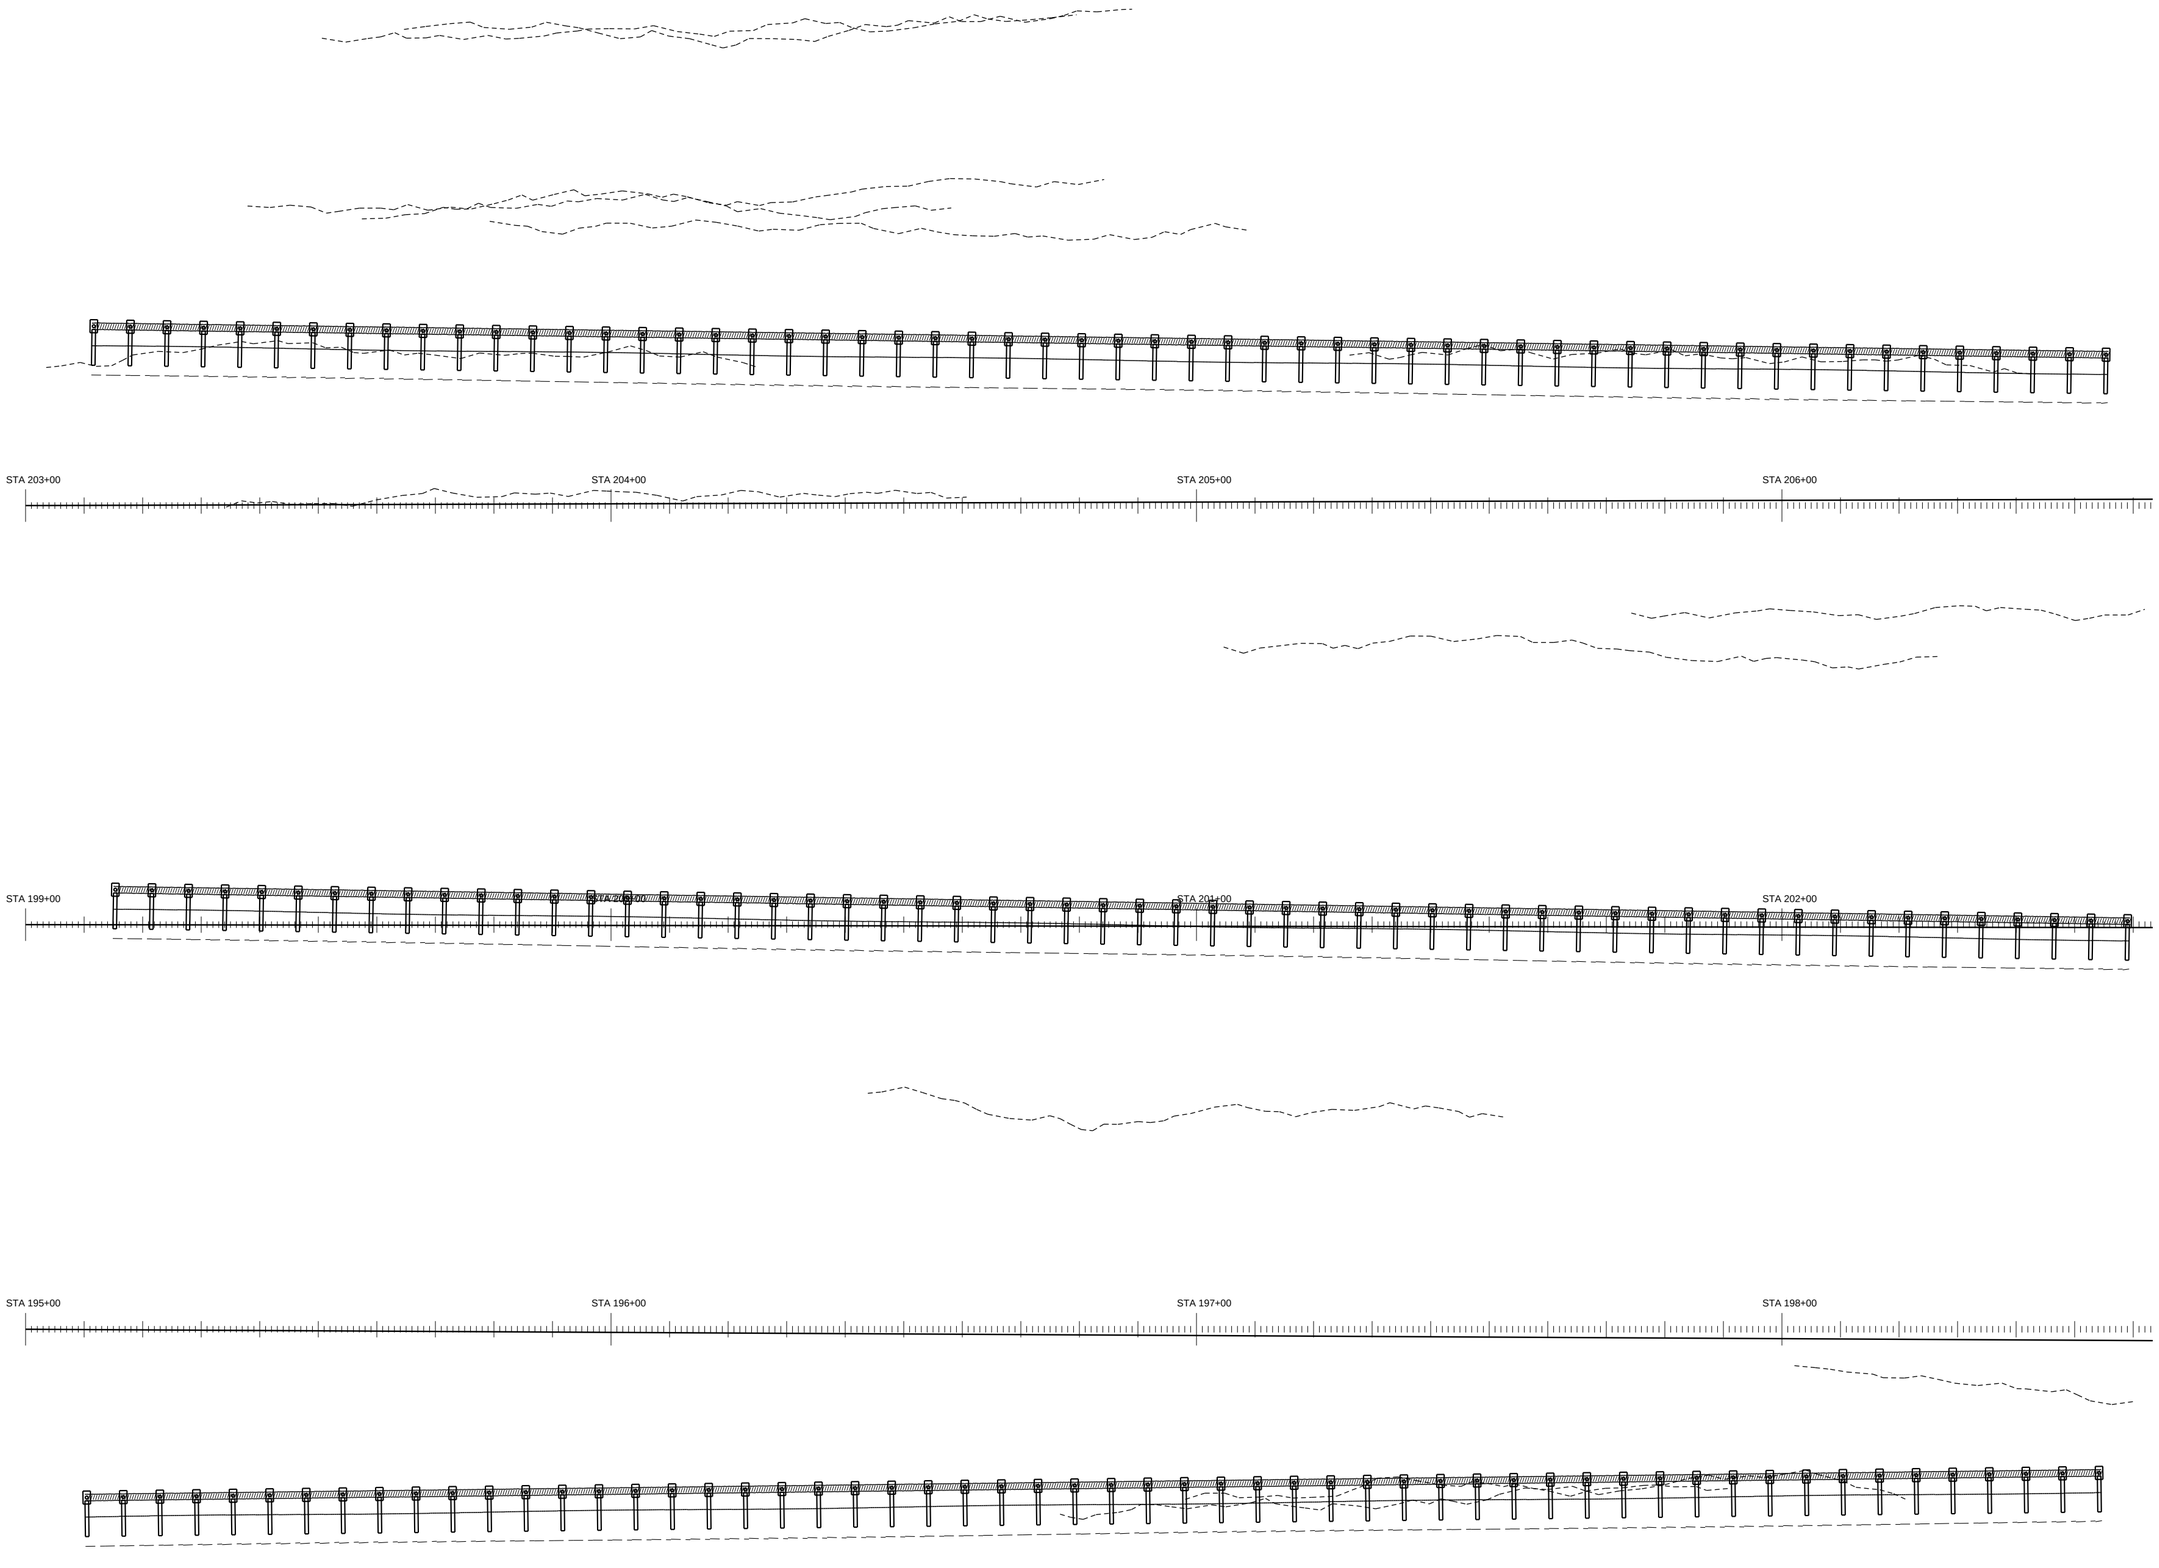


PAY ITEM 536-1-1 GUARDRAIL ROADWAY (TL-3)

PAY ITEM 536-85-24 END TREATMENT

GUARANTEED FENCE CORP

FIN. PROJ. ID 441234-1-52-01

SHEET 6 OF 120

SHEET NO. 106

ROADWAY PLAN SCALE: 1" = 20'

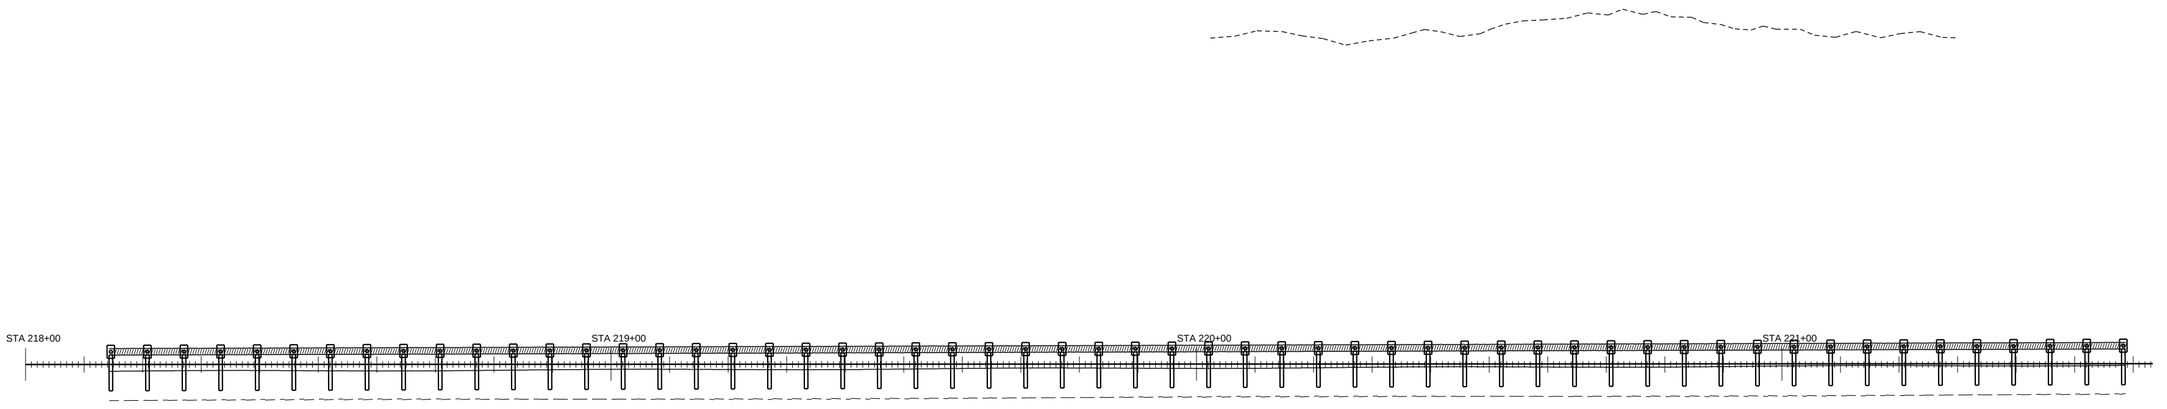


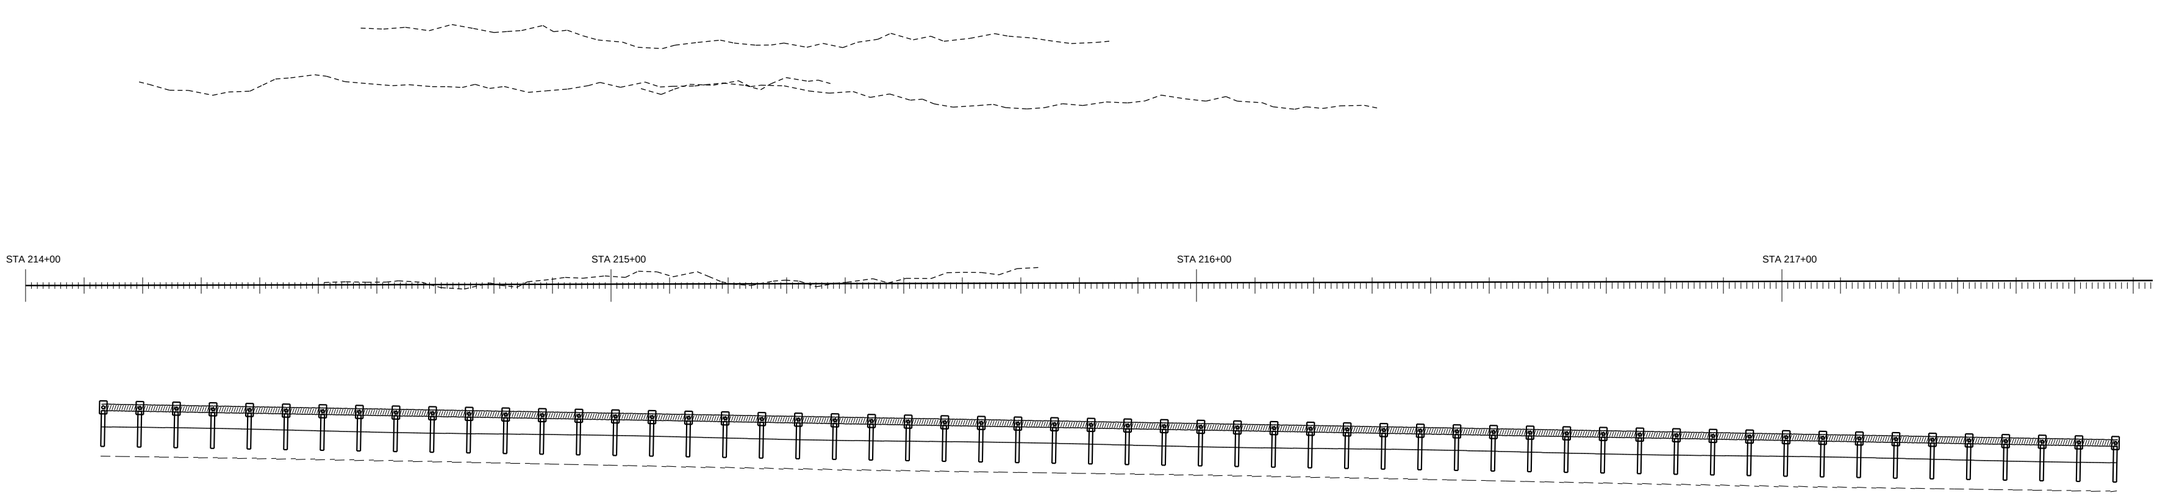


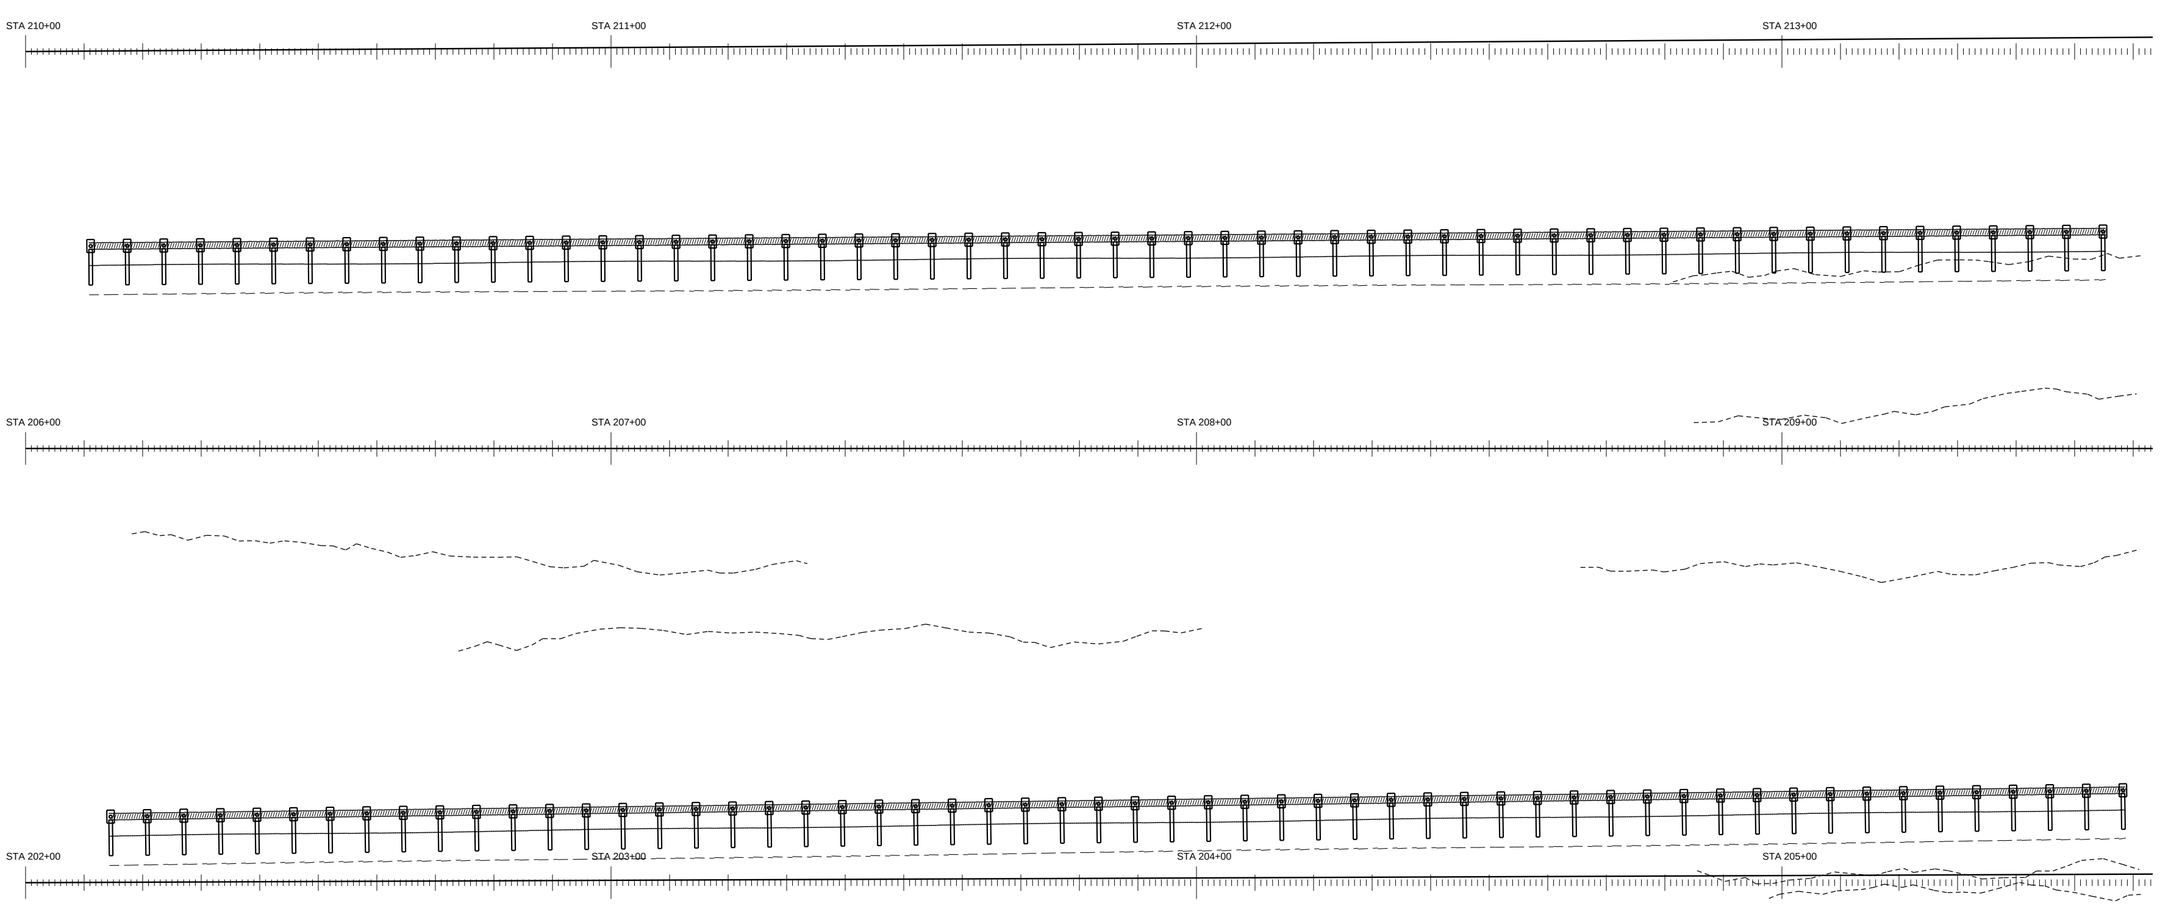








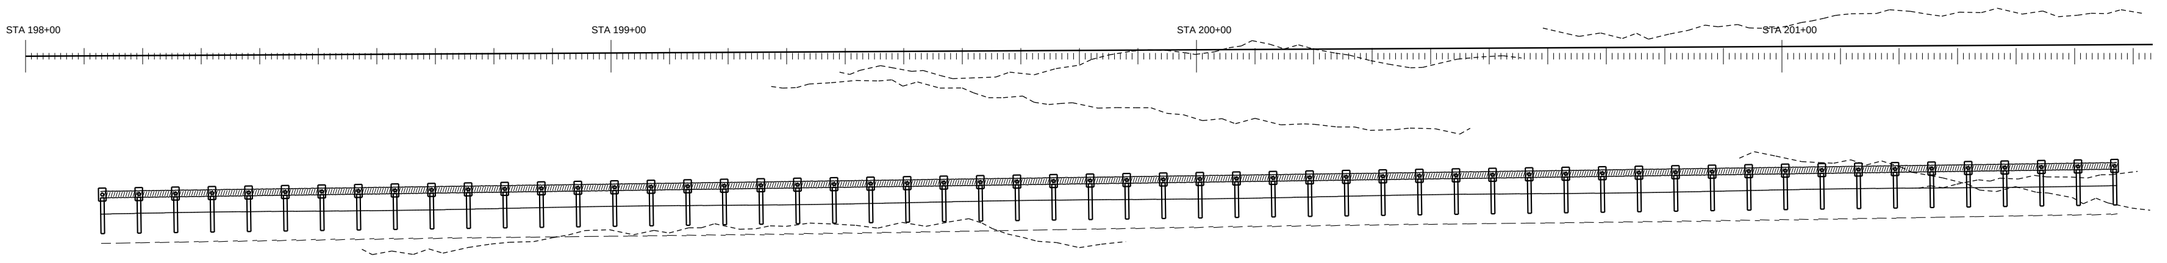


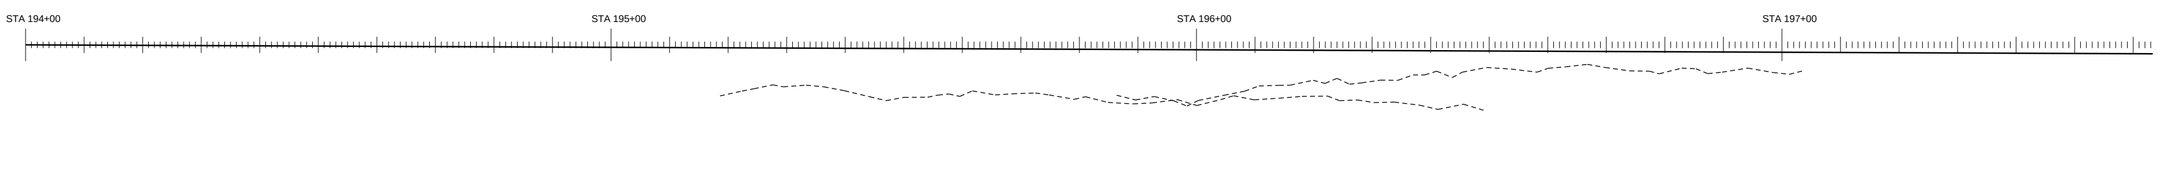

PAY ITEM 536-1-1 GUARDRAIL ROADWAY (TL-3)

PAY ITEM 536-85-24 END TREATMENT

GUARANTEED FENCE CORP

FIN. PROJ. ID 441234-1-52-01

SHEET 7 OF 120

SHEET NO. 107

ROADWAY PLAN SCALE: 1" = 20'

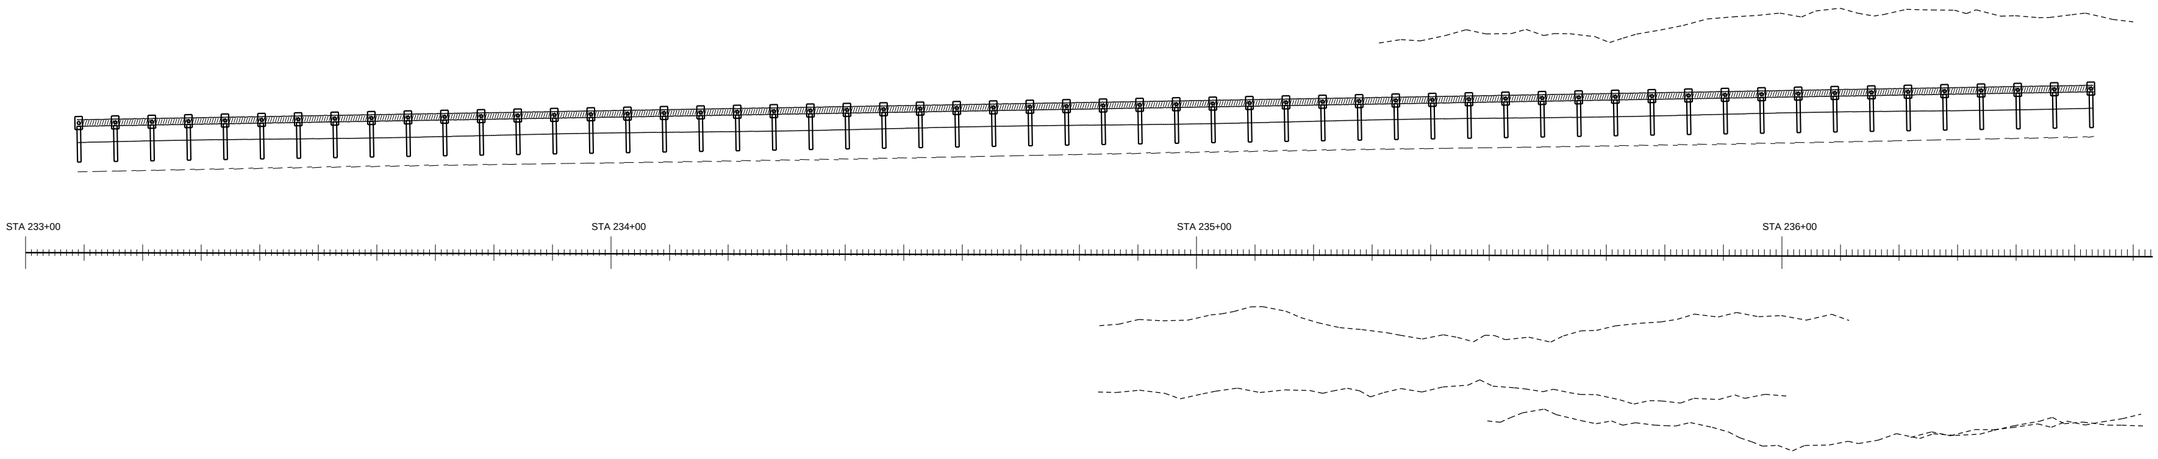


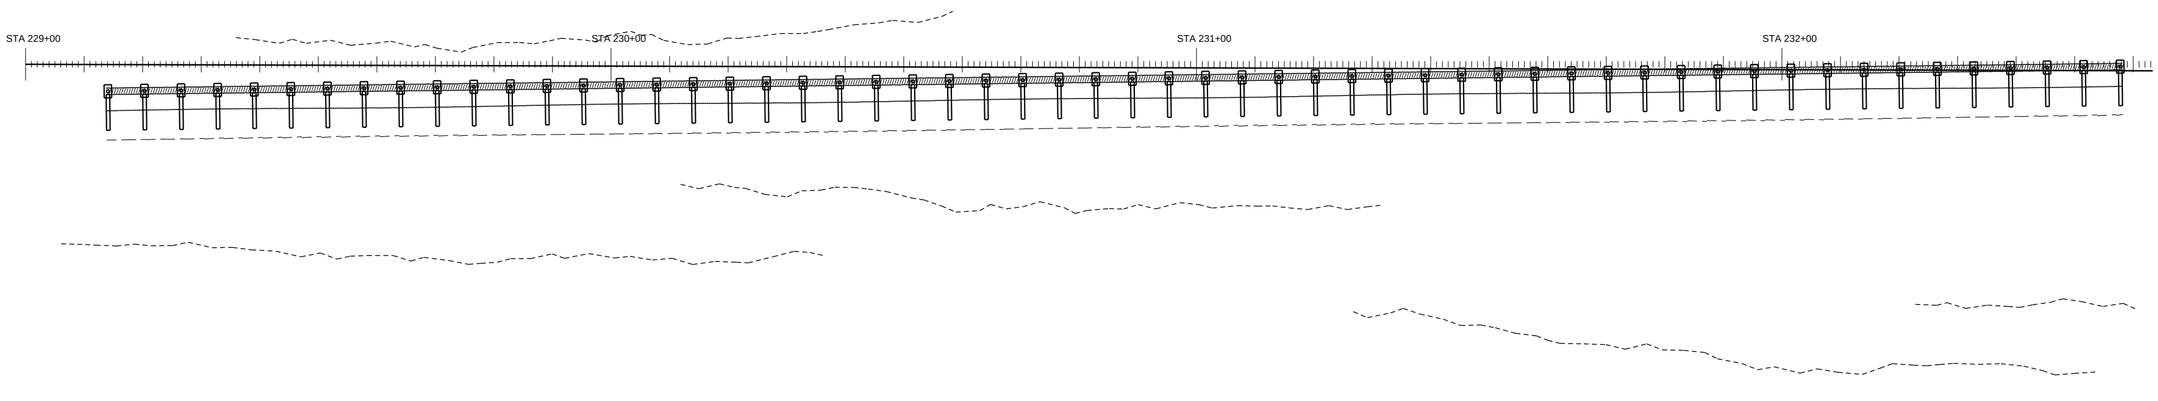


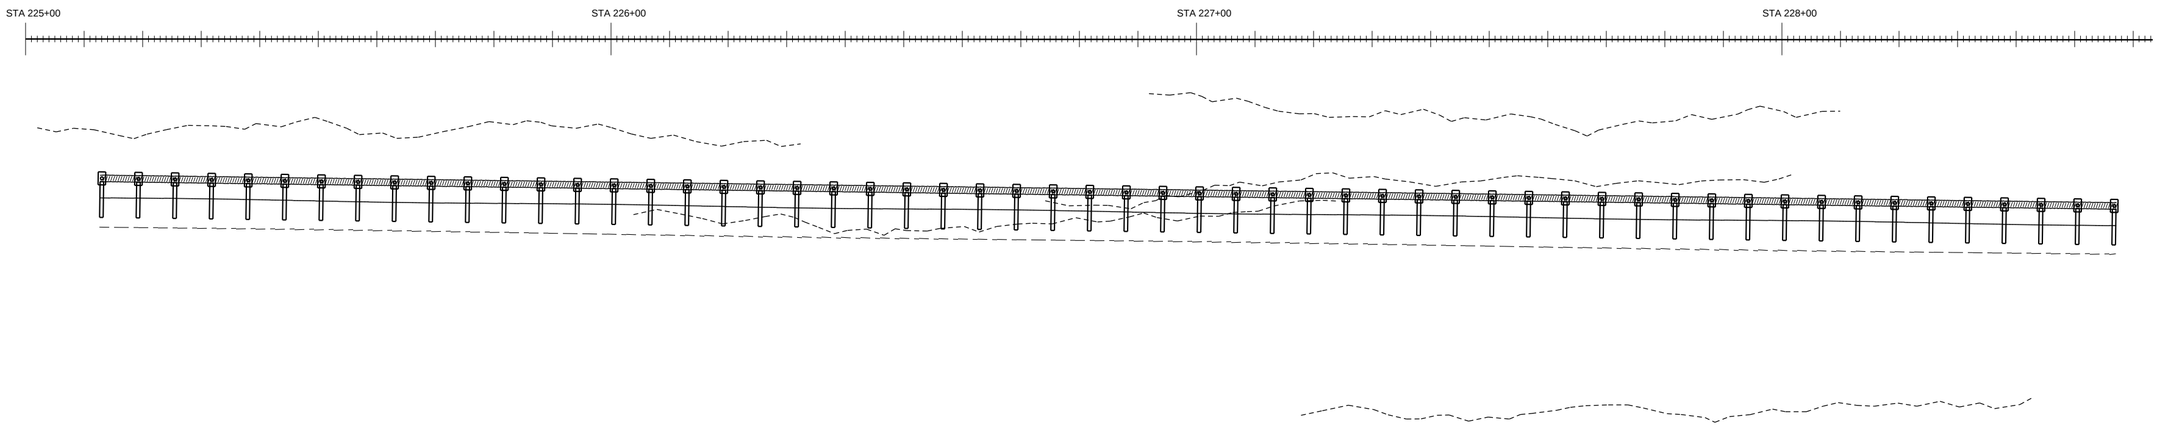


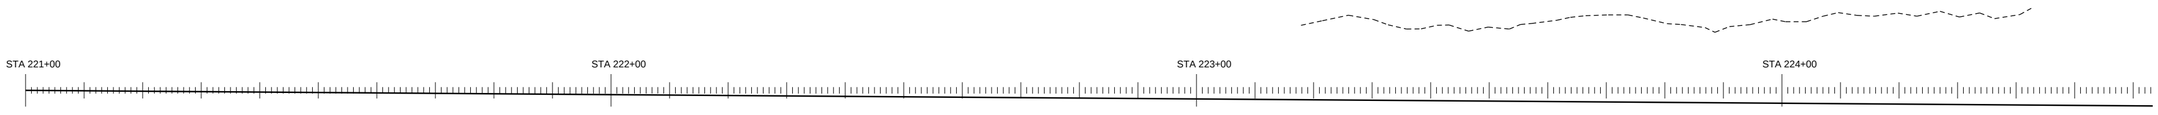


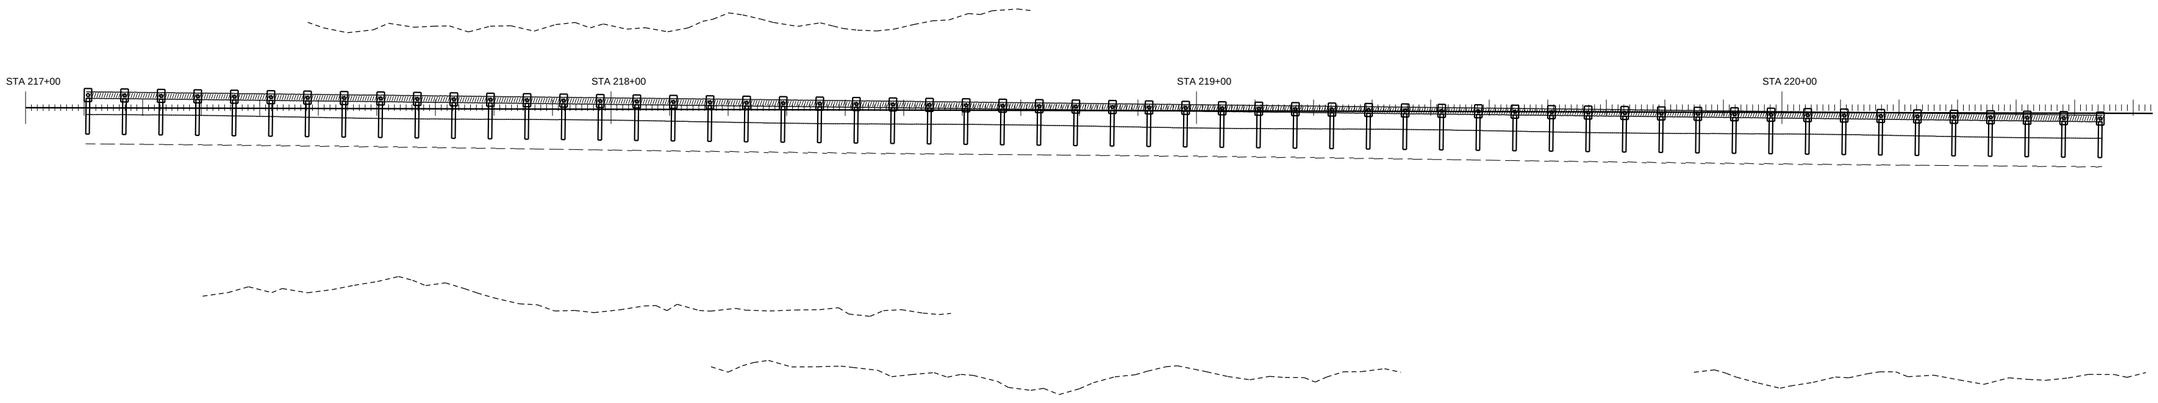


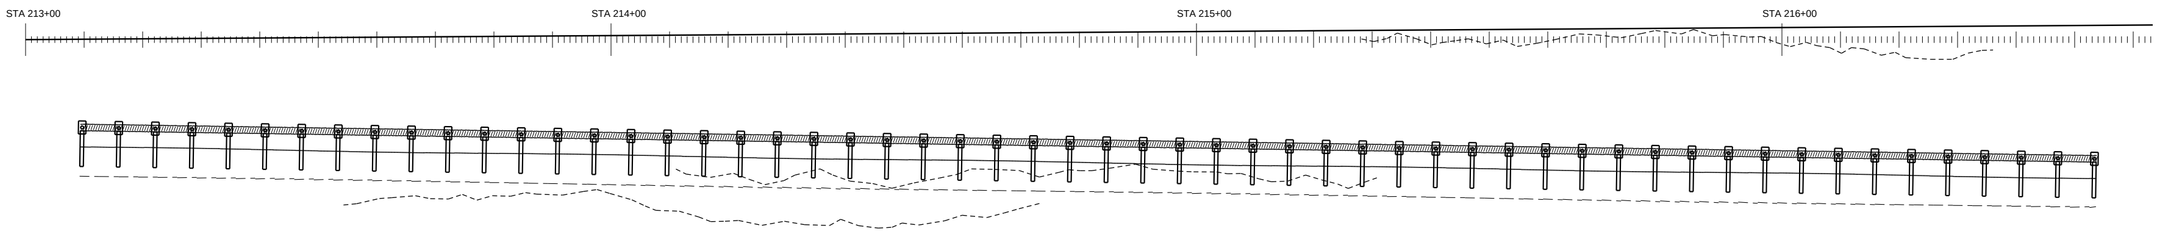


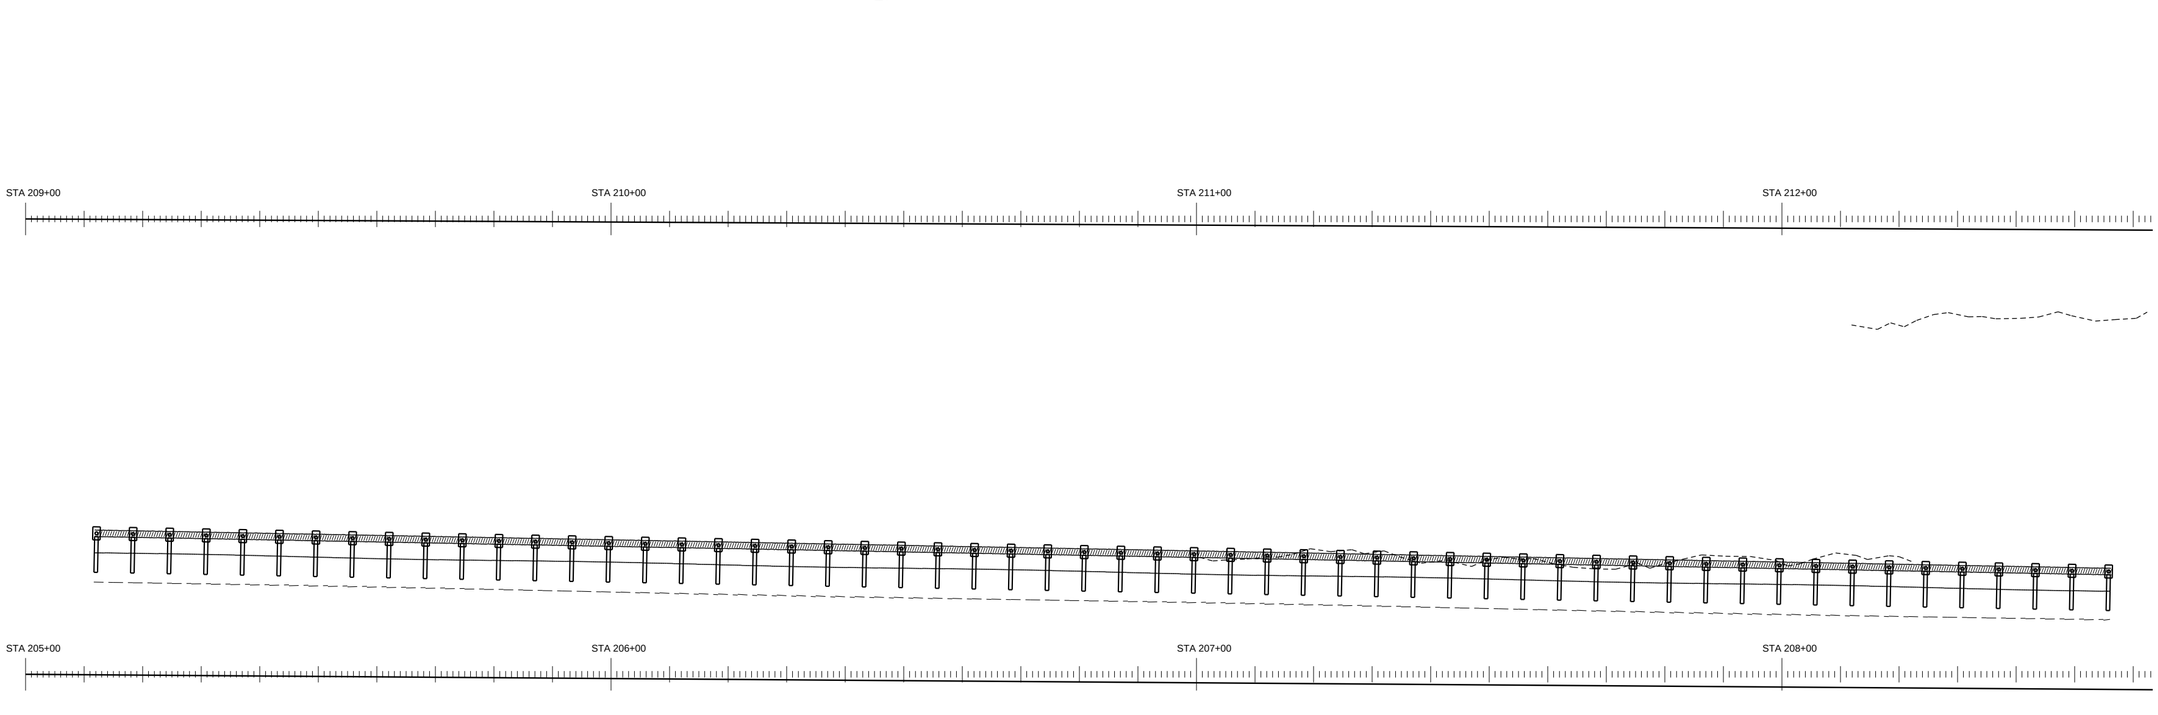


PAY ITEM 536-1-1 GUARDRAIL ROADWAY (TL-3)

PAY ITEM 536-85-24 END TREATMENT

GUARANTEED FENCE CORP

FIN. PROJ. ID 441234-1-52-01

SHEET 8 OF 120

SHEET NO. 108

ROADWAY PLAN SCALE: 1" = 20'

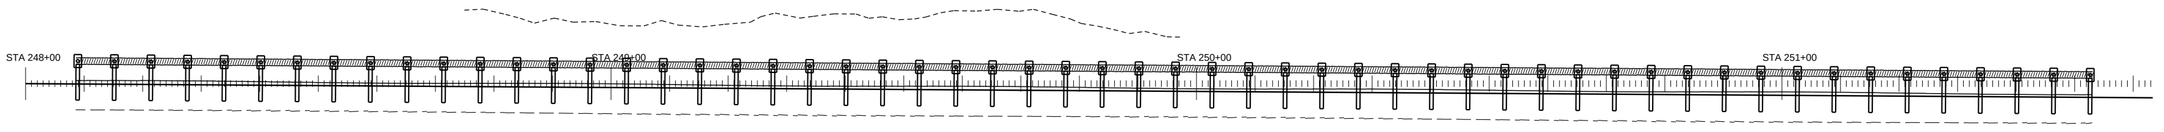


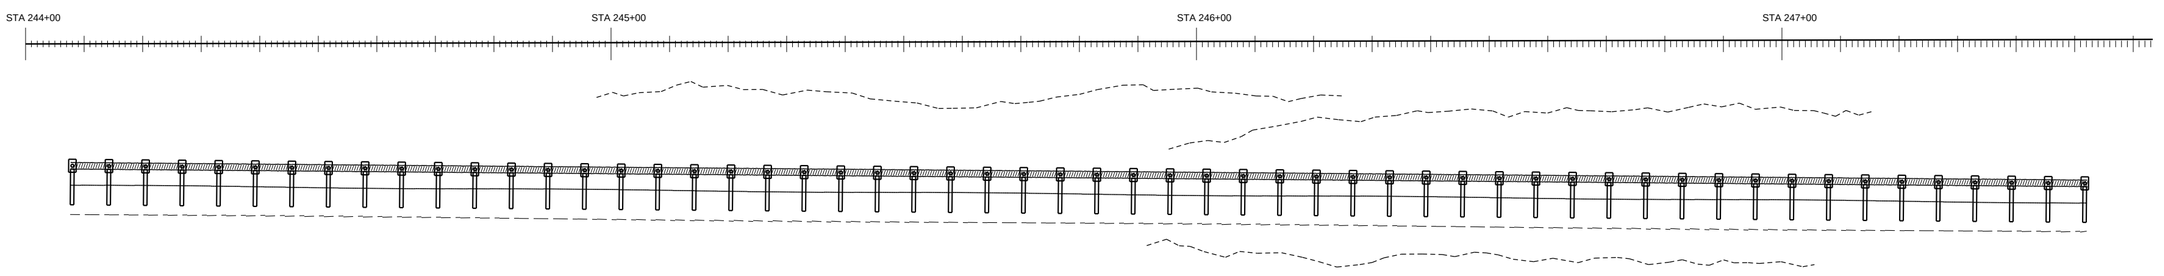


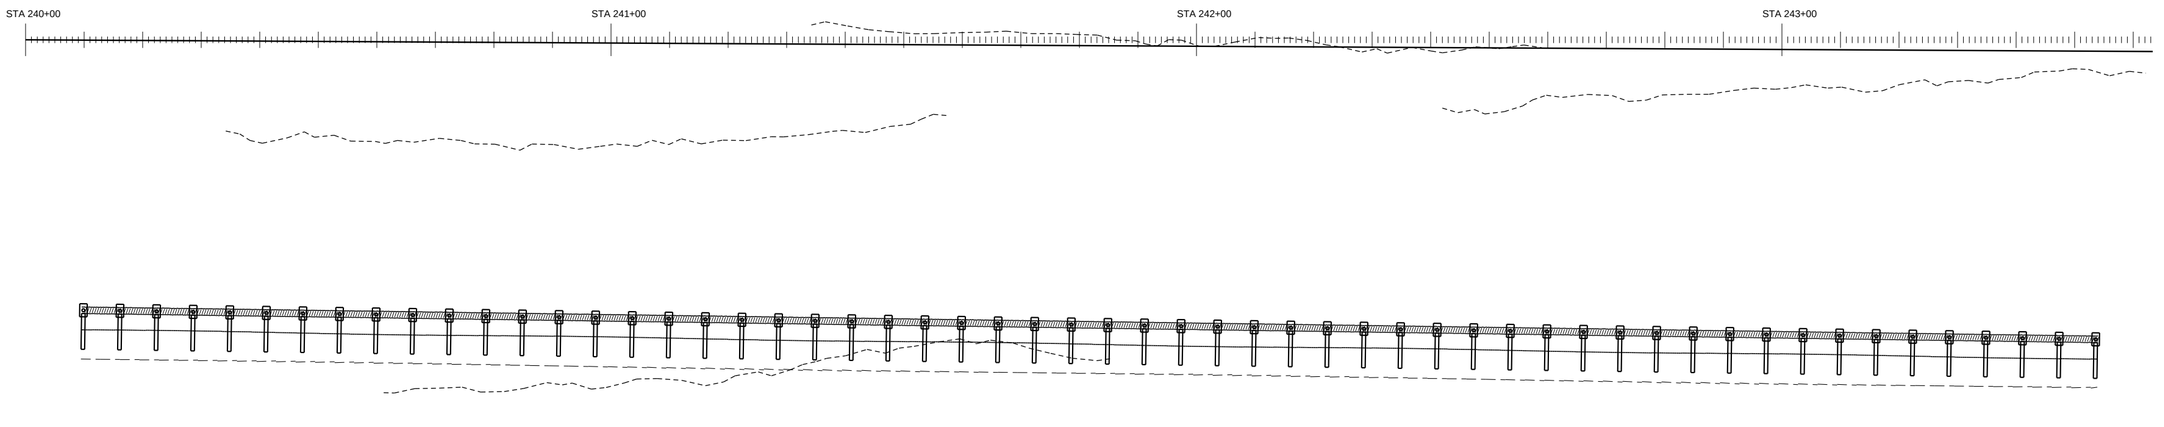


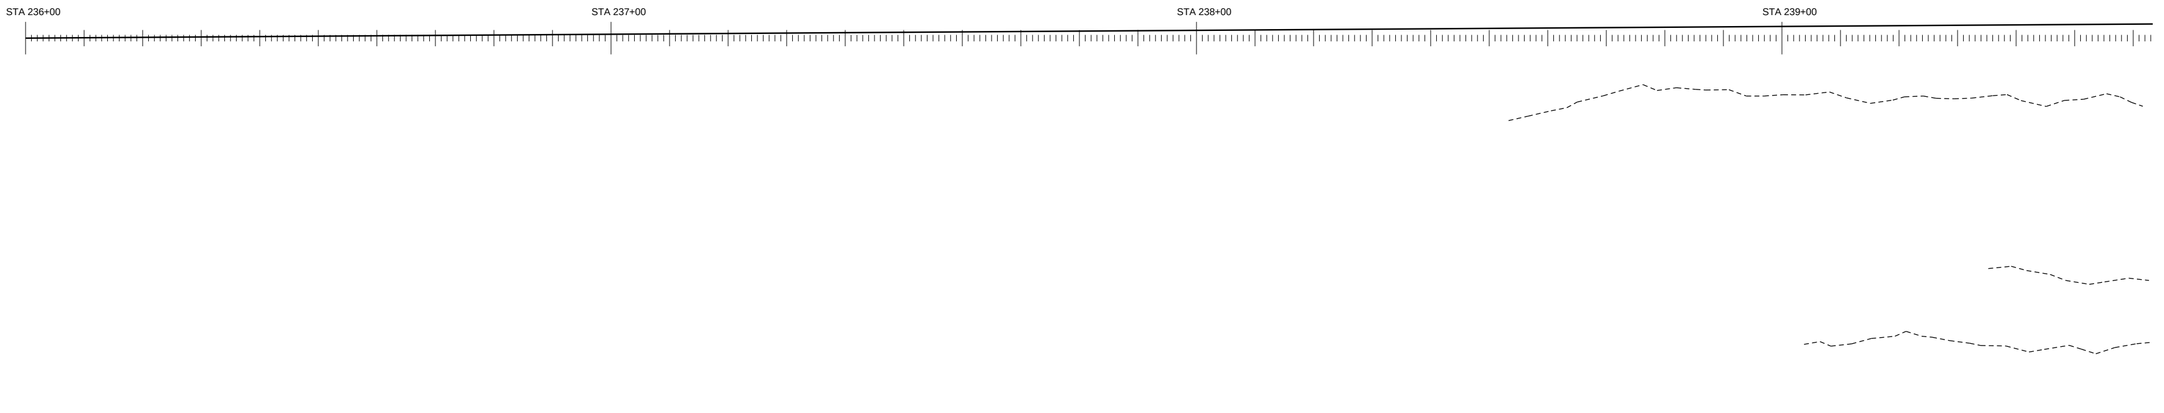


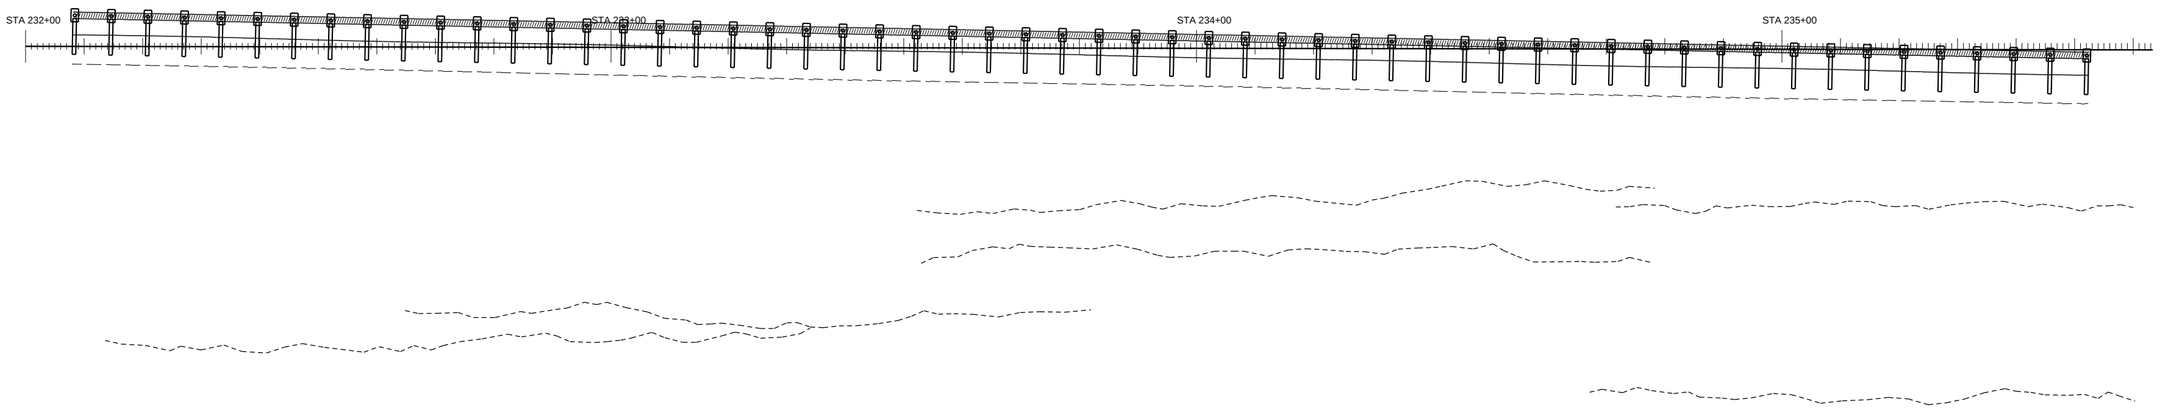


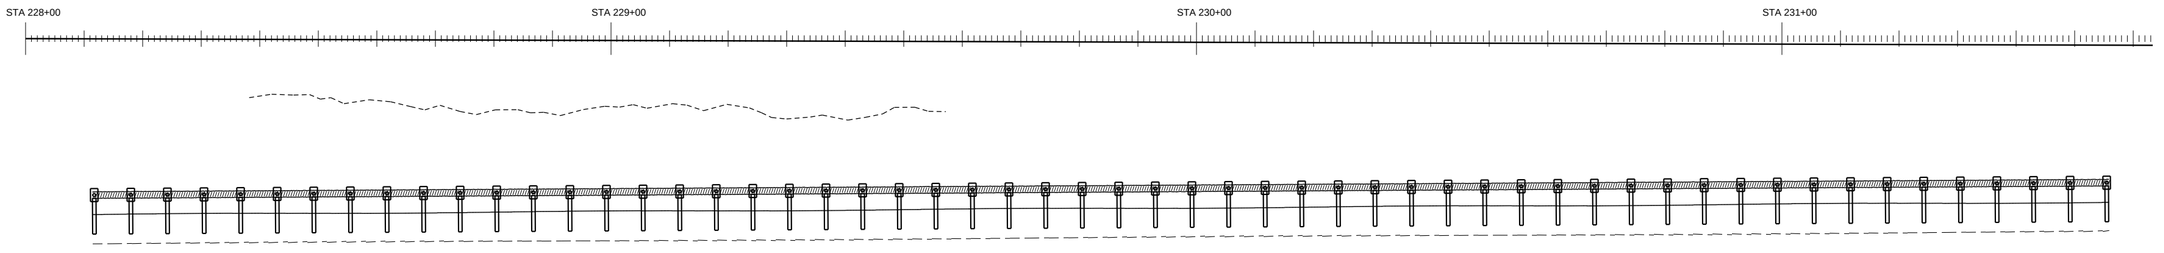


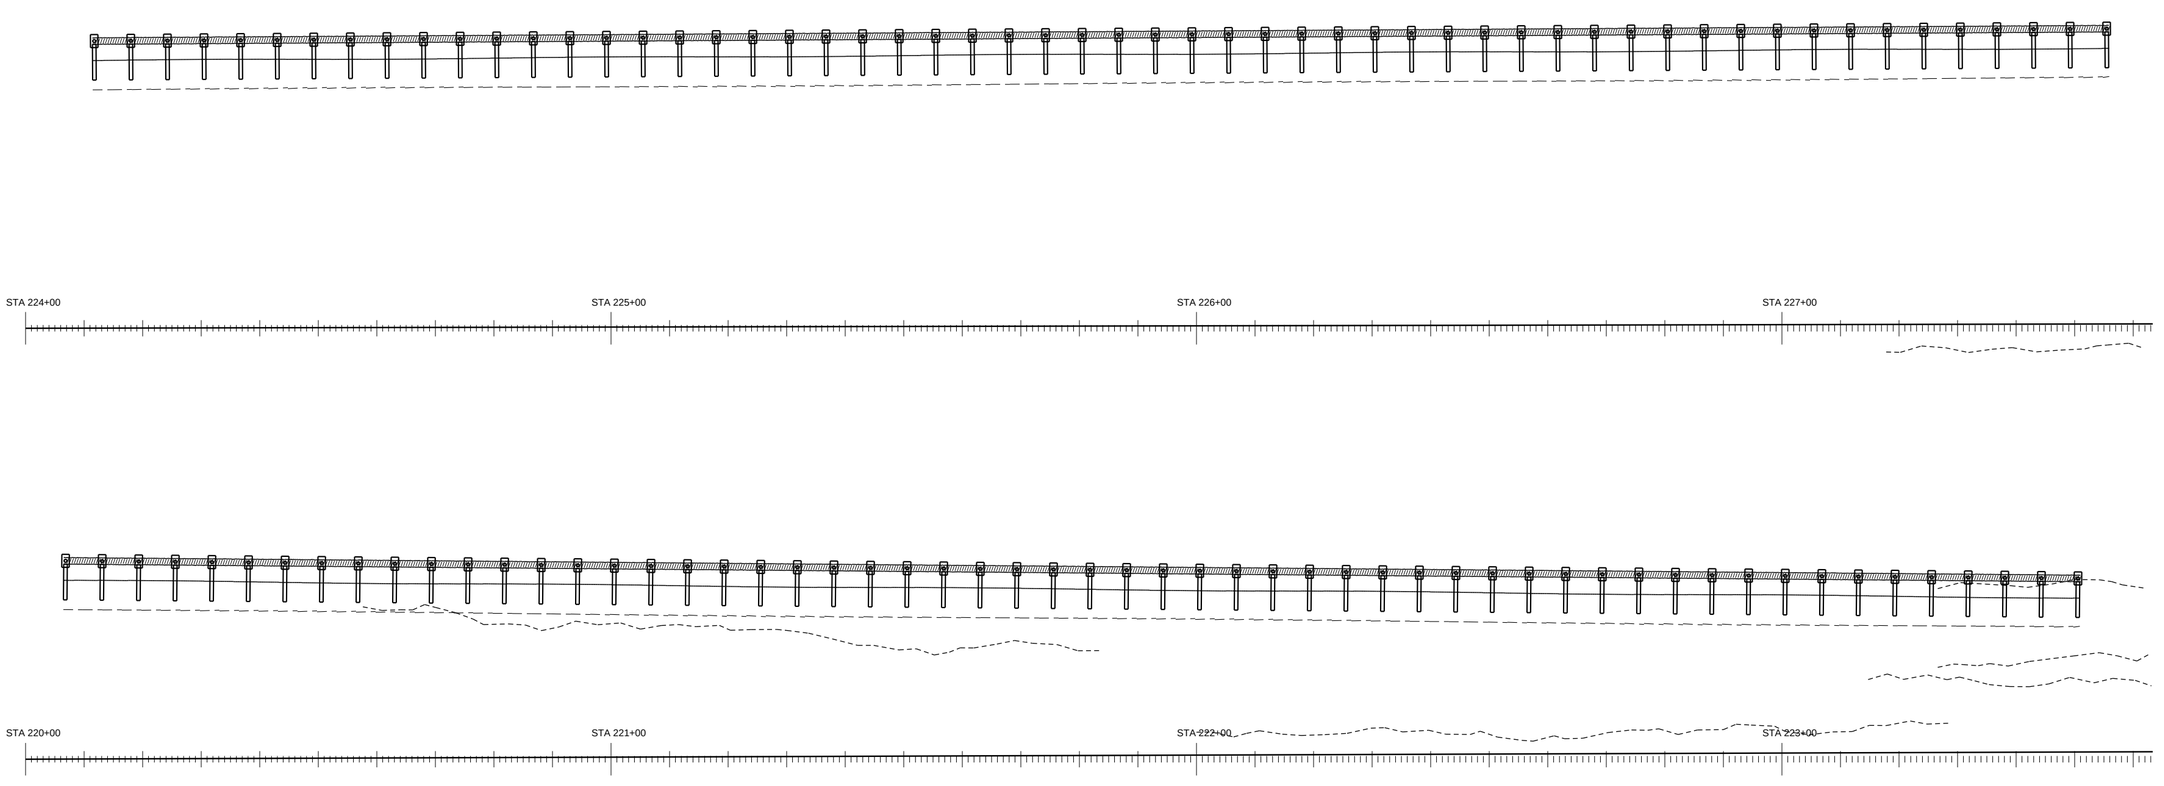


PAY ITEM 536-1-1 GUARDRAIL ROADWAY (TL-3)

PAY ITEM 536-85-24 END TREATMENT

GUARANTEED FENCE CORP

FIN. PROJ. ID 441234-1-52-01

SHEET 9 OF 120

SHEET NO. 109

ROADWAY PLAN SCALE: 1" = 20'




PAY ITEM 536-1-1 GUARDRAIL ROADWAY (TL-3)

PAY ITEM 536-85-24 END TREATMENT

GUARANTEED FENCE CORP

FIN. PROJ. ID 441234-1-52-01

SHEET 10 OF 120

SHEET NO. 110

ROADWAY PLAN SCALE: 1" = 20'




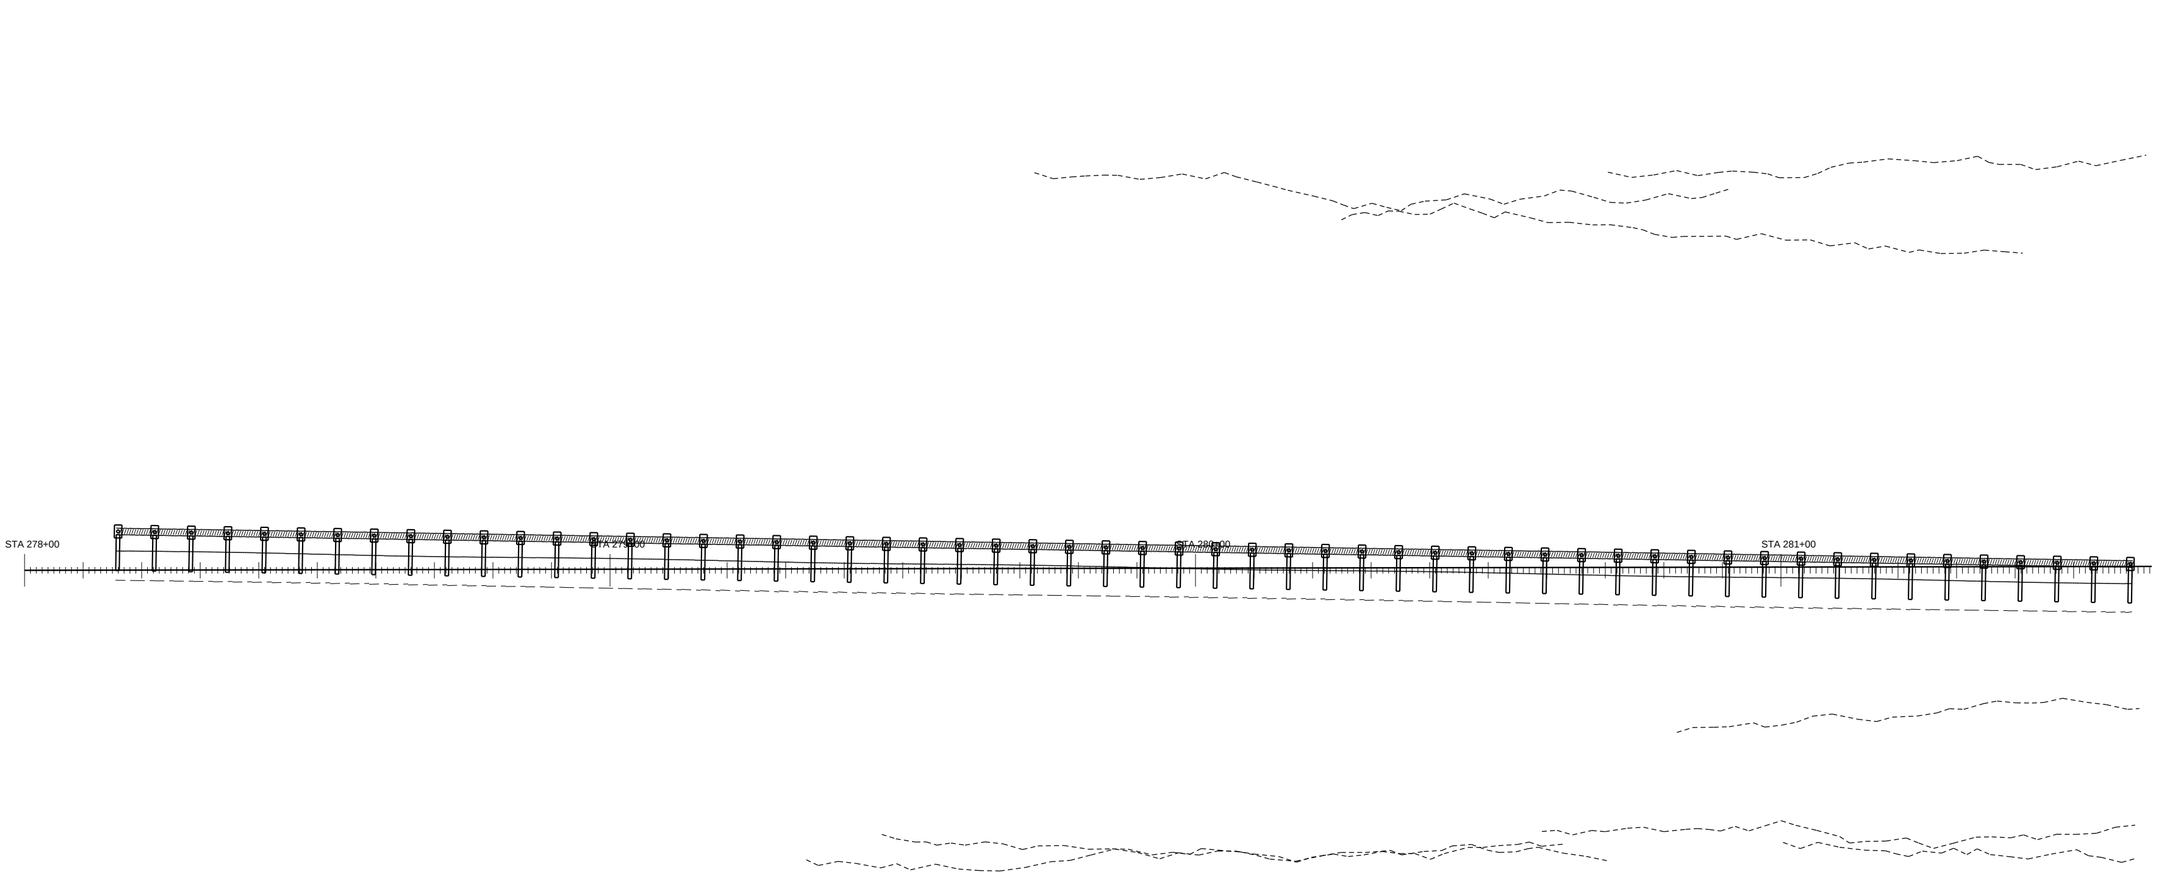


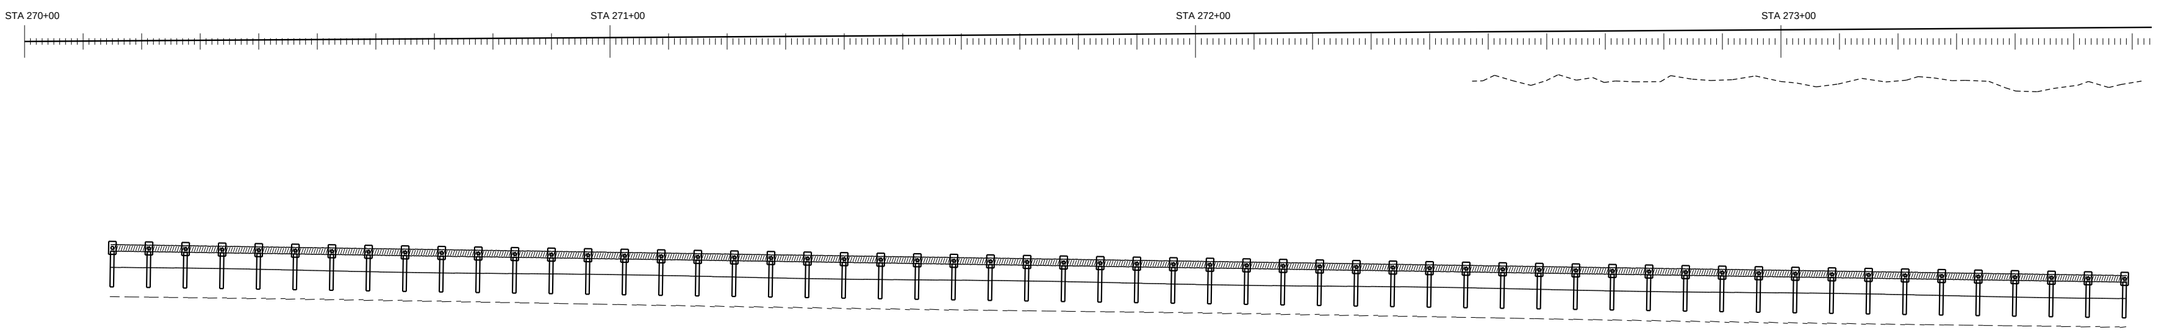


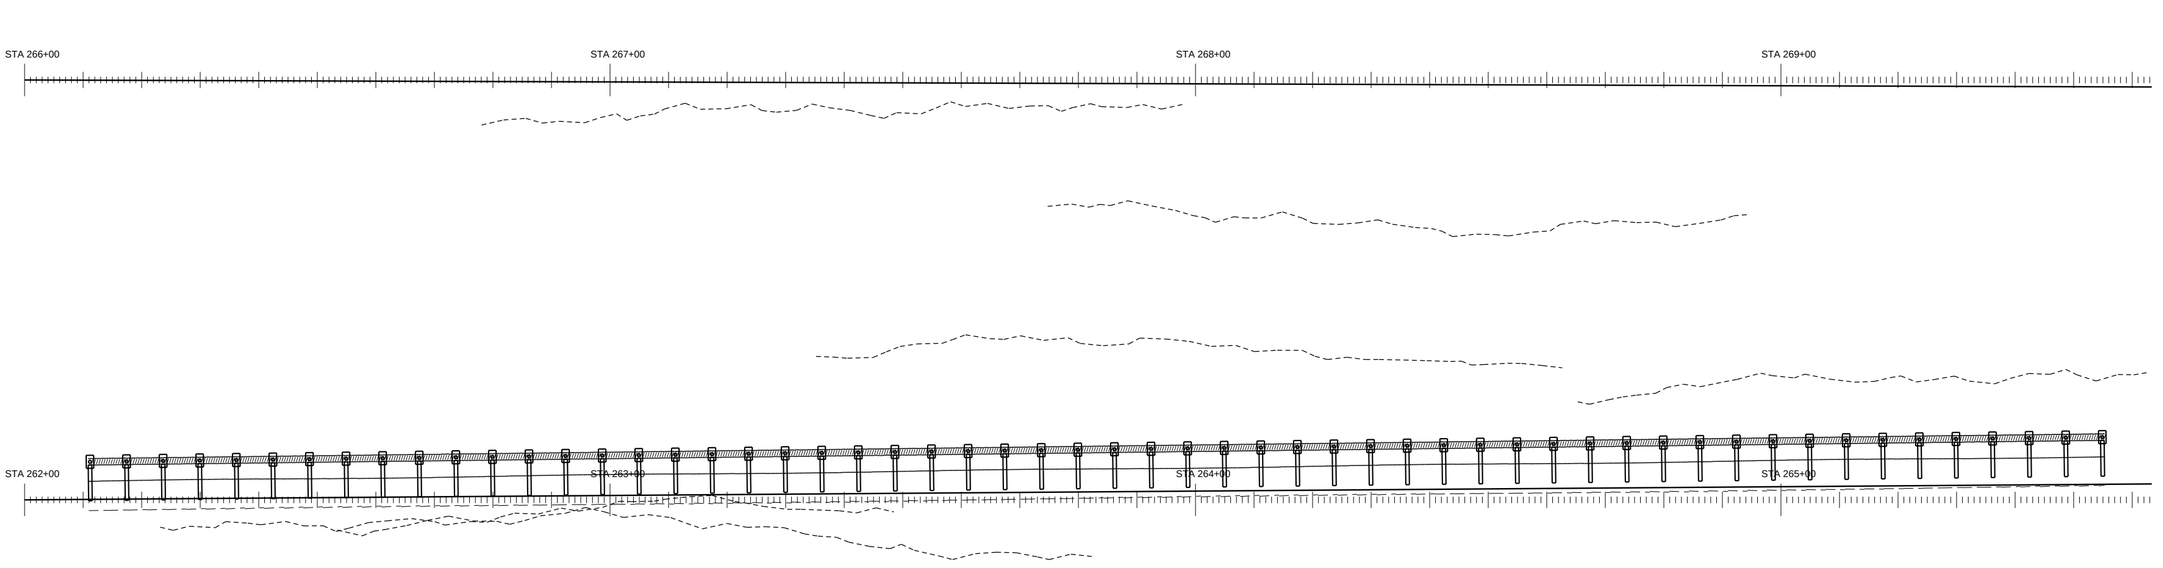


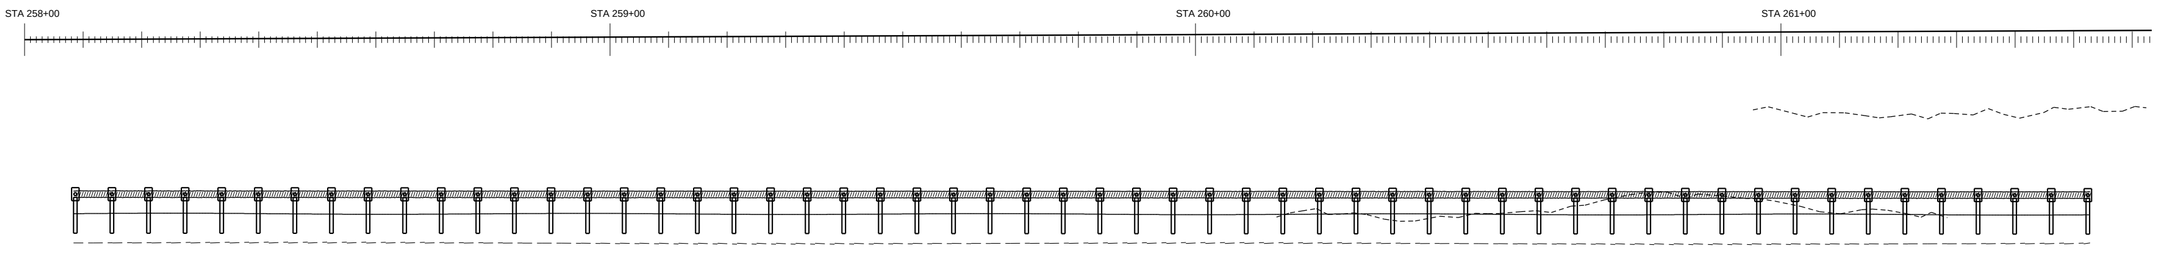


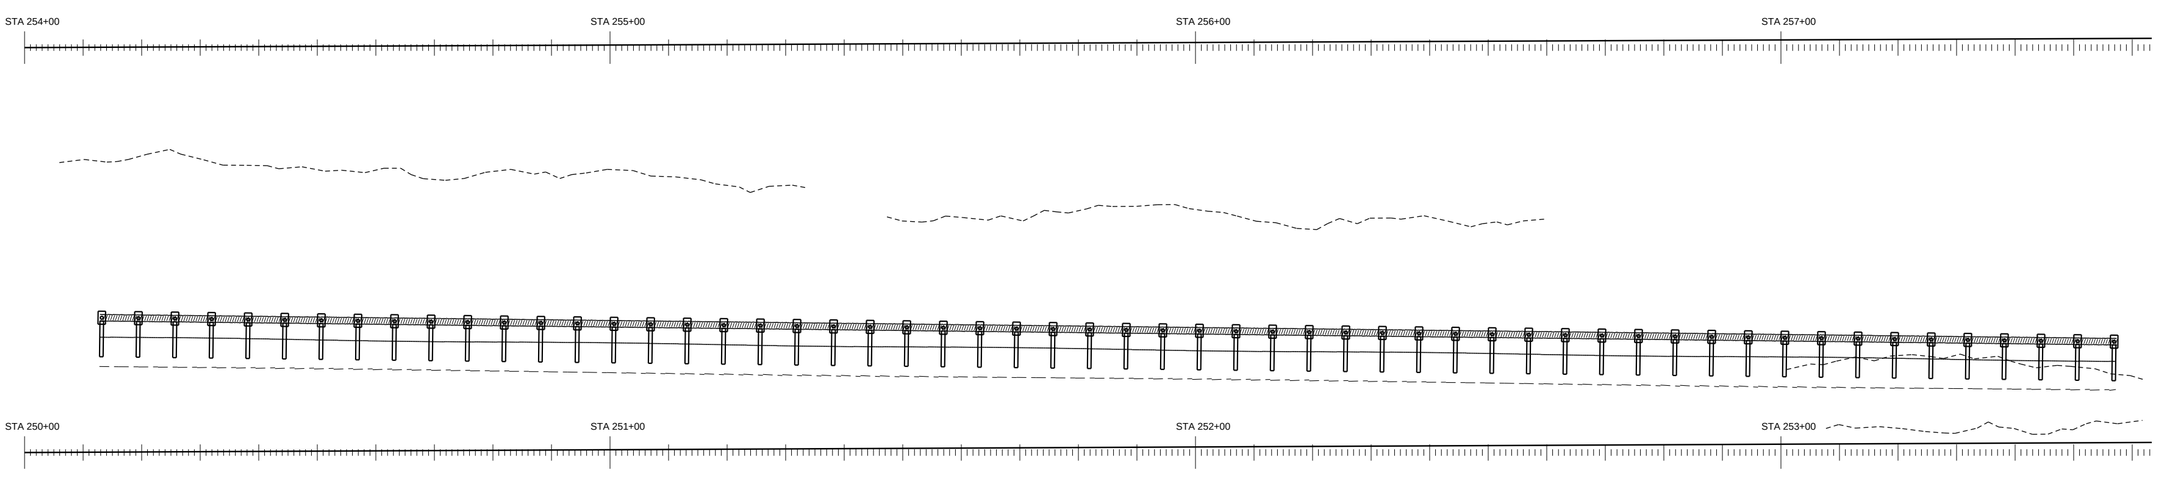


PAY ITEM 536-1-1 GUARDRAIL ROADWAY (TL-3)

PAY ITEM 536-85-24 END TREATMENT

GUARANTEED FENCE CORP

FIN. PROJ. ID 441234-1-52-01

SHEET 11 OF 120

SHEET NO. 111

ROADWAY PLAN SCALE: 1" = 20'




PAY ITEM 536-1-1 GUARDRAIL ROADWAY (TL3)

PAY ITEM 536-85-24 END TREATMENT

GUARANTEED FENCE CORP

FIN. PROJ. ID 441234-1-52-01

SHEET 12 OF 120

SHEET NO. 112

ROADWAY PLAN SCALE: 1" = 20'

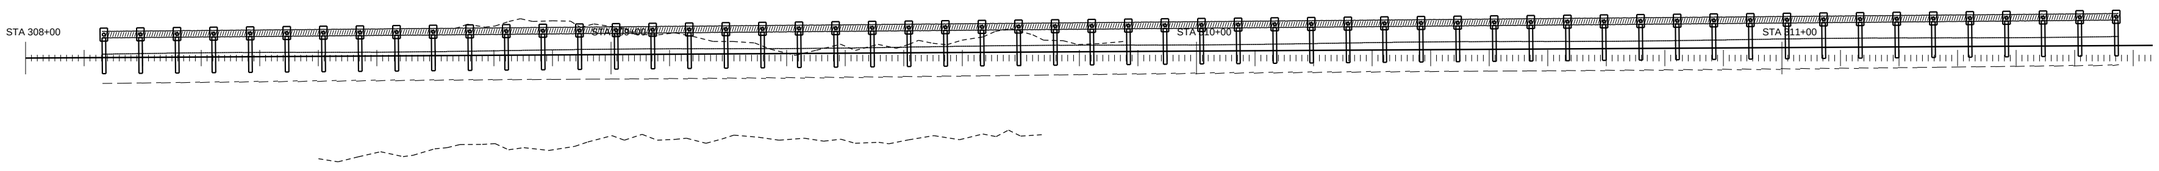


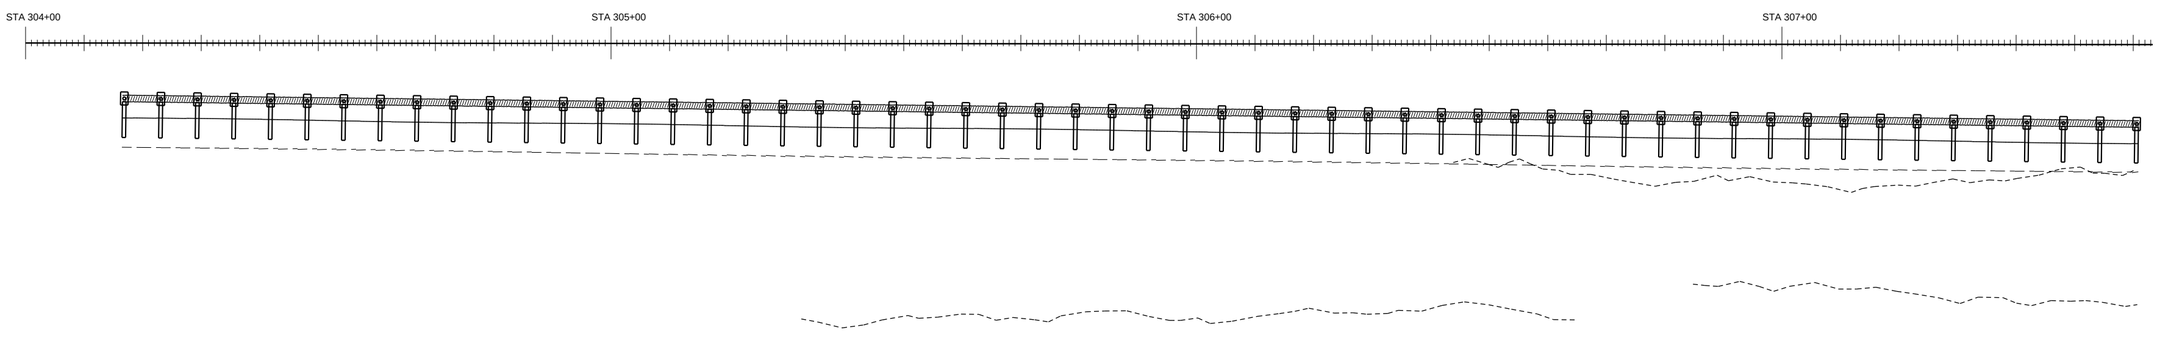


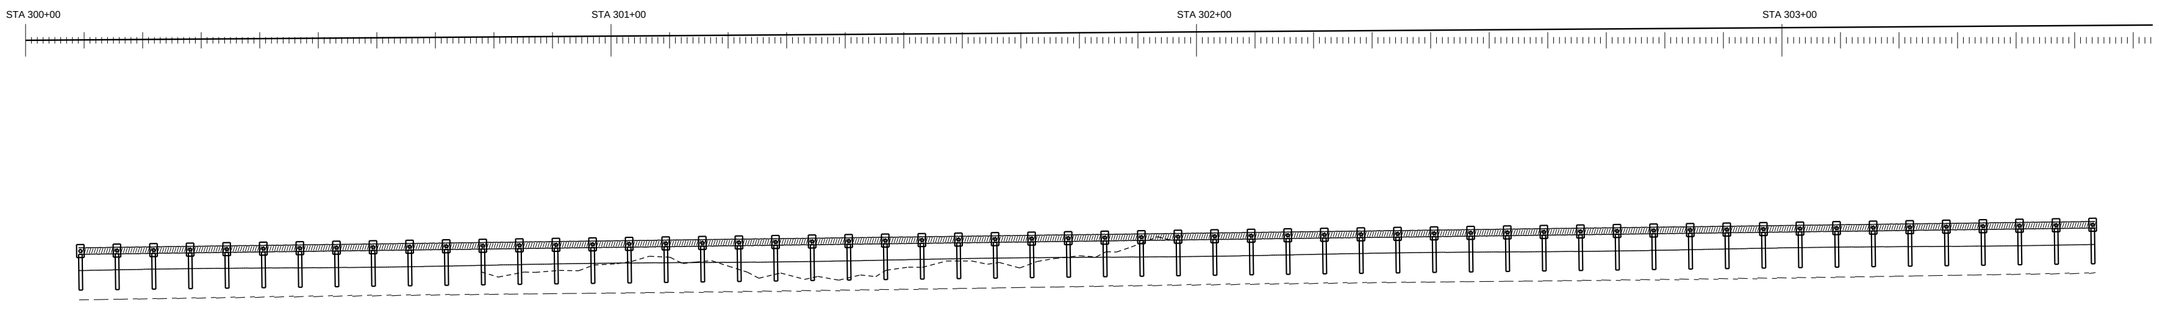


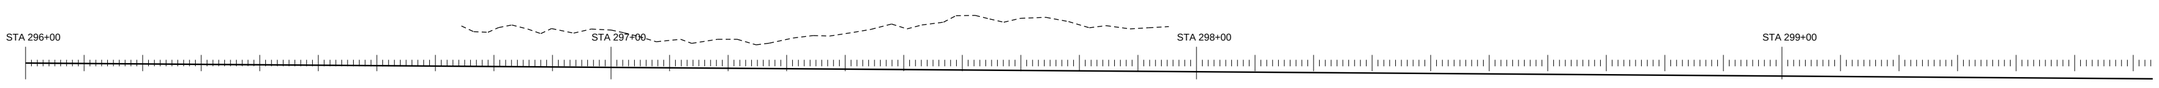


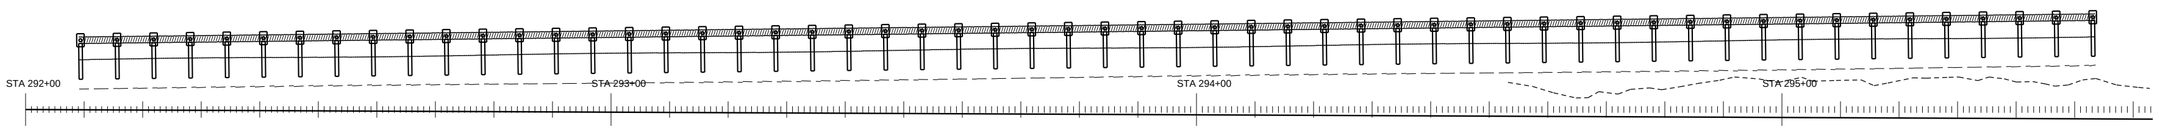


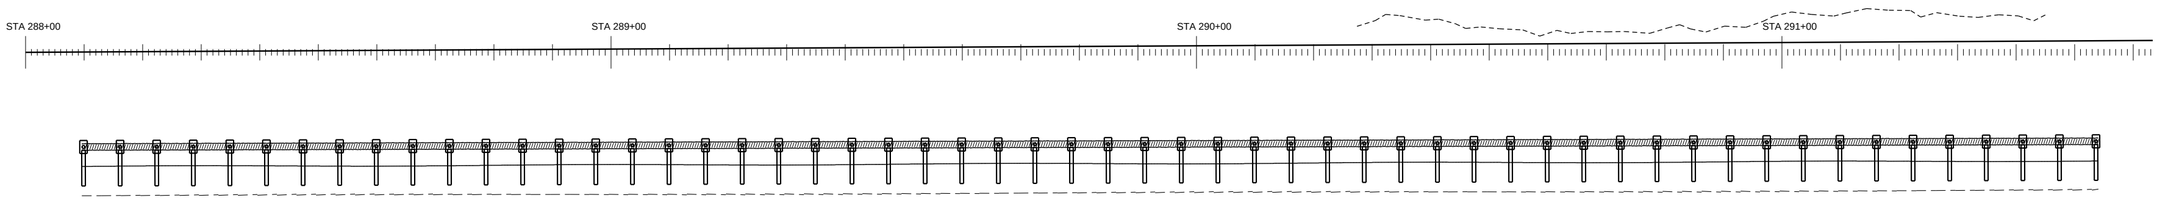


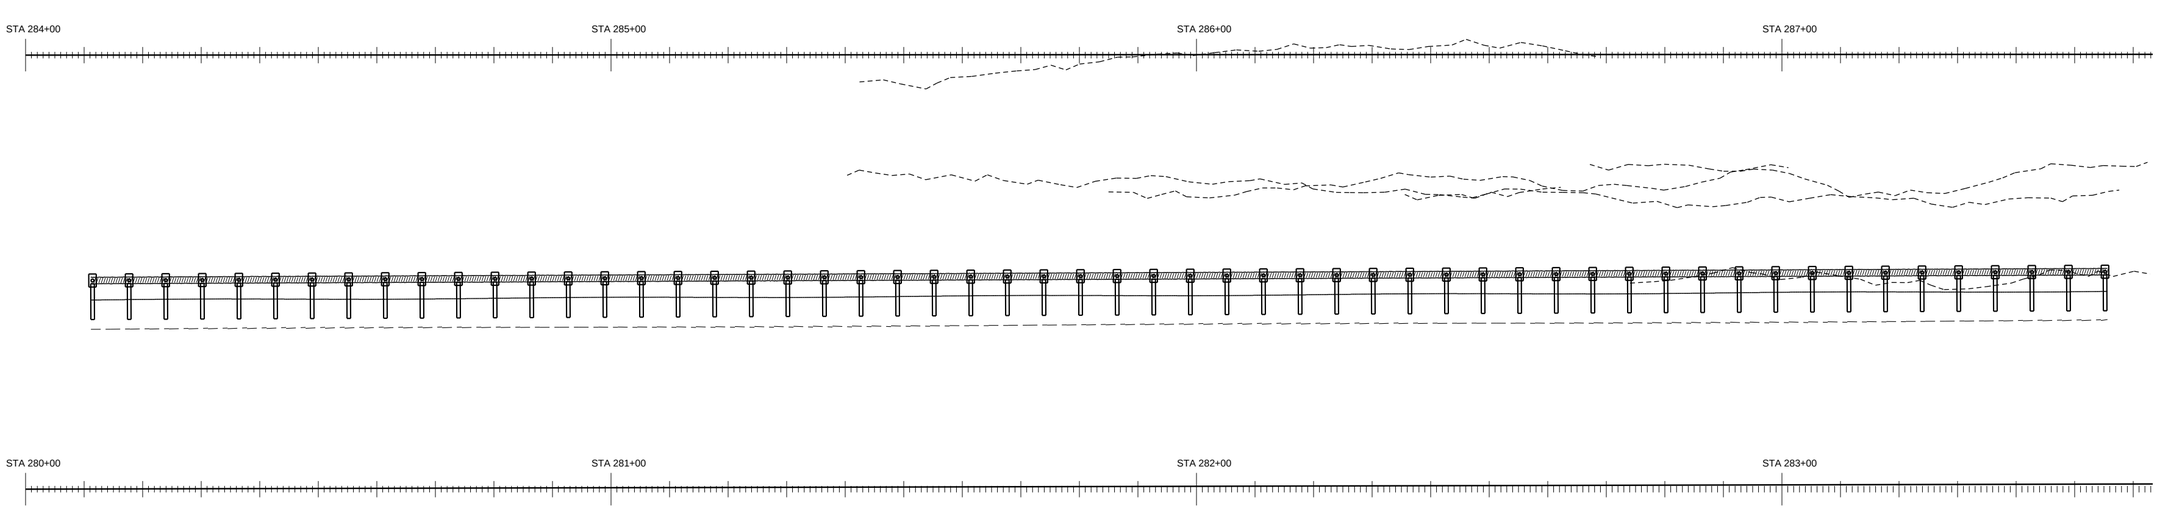





PAY ITEM 536-1-1 GUARDRAIL ROADWAY (TL-3)

PAY ITEM 536-85-24 END TREATMENT

GUARANTEED FENCE CORP

FIN. PROJ. ID 441234-1-52-01

SHEET 13 OF 120

SHEET NO. 113

ROADWAY PLAN SCALE: 1" = 20'




PAY ITEM 536-1-1 GUARDRAIL ROADWAY (T-3)

PAY ITEM 536-85-24 END TREATMENT

GUARANTEED FENCE CORP

FIN. PROJ. ID 441234-1-52-01

SHEET 14 OF 120

SHEET NO. 114

ROADWAY PLAN SCALE: 1" = 20'




PAY ITEM 536-1-1 GUARDRAIL ROADWAY (TL-3)

PAY ITEM 536-85-24 END TREATMENT

GUARANTEED FENCE CORP

FIN. PROJ. ID 441234-1-52-01

SHEET 15 OF 120

SHEET NO. 115

ROADWAY PLAN SCALE: 1" = 20'




PAY ITEM 536-1-1 GUARDRAIL ROADWAY (TL-3)

PAY ITEM 536-85-24 END TREATMENT

GUARANTEED FENCE CORP

FIN. PROJ. ID 441234-1-52-01

SHEET 16 OF 120

SHEET NO. 116

ROADWAY PLAN SCALE: 1" = 20'




PAY ITEM 536-1-1 GUARDRAIL ROADWAY (TL-3)

PAY ITEM 536-85-24 END TREATMENT

GUARANTEED FENCE CORP

FIN. PROJ. ID 441234-1-52-01

SHEET 17 OF 120

SHEET NO. 117

ROADWAY PLAN SCALE: 1" = 20'




PAY ITEM 536-1-1 GUARDRAIL ROADWAY (TL-3)

PAY ITEM 536-85-24 END TREATMENT

GUARANTEED FENCE CORP

FIN. PROJ. ID 441234-1-52-01

SHEET 18 OF 120

SHEET NO. 118

ROADWAY PLAN SCALE: 1" = 20'

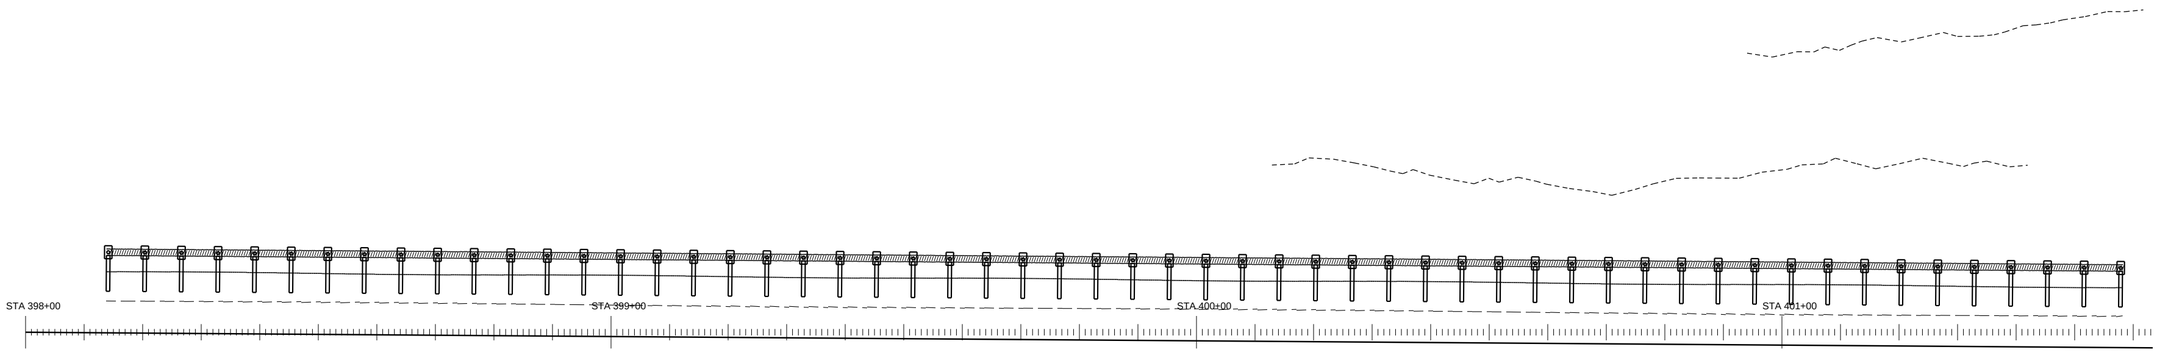


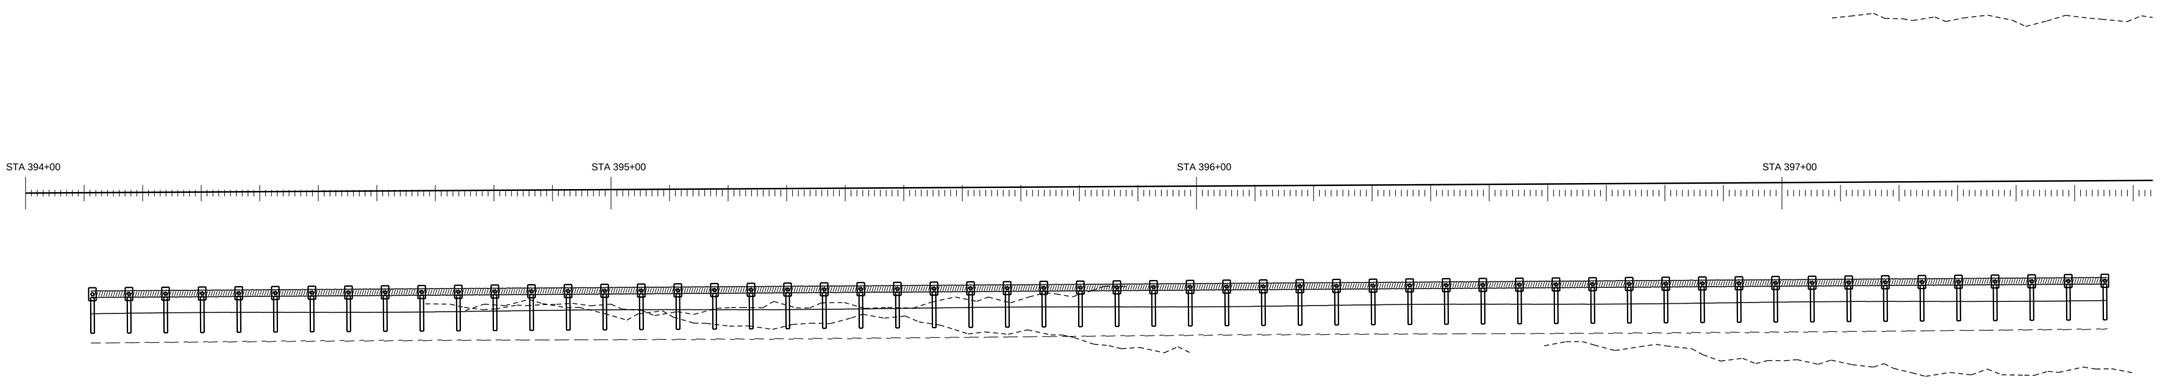


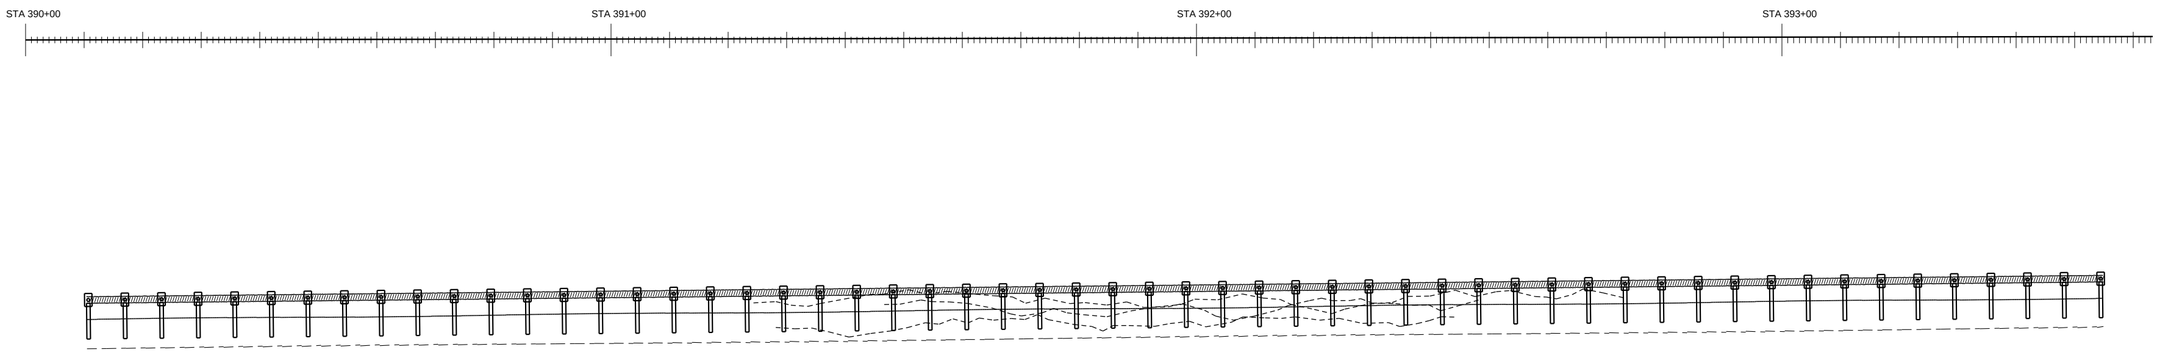


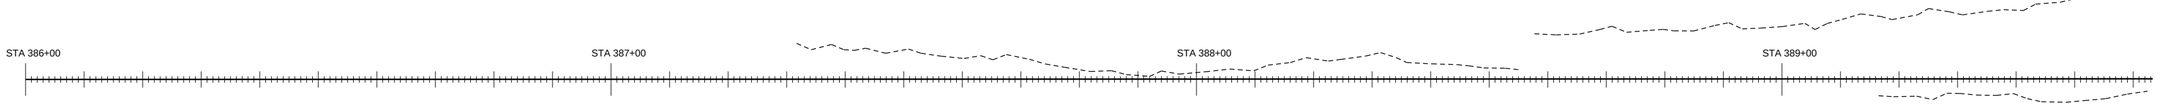


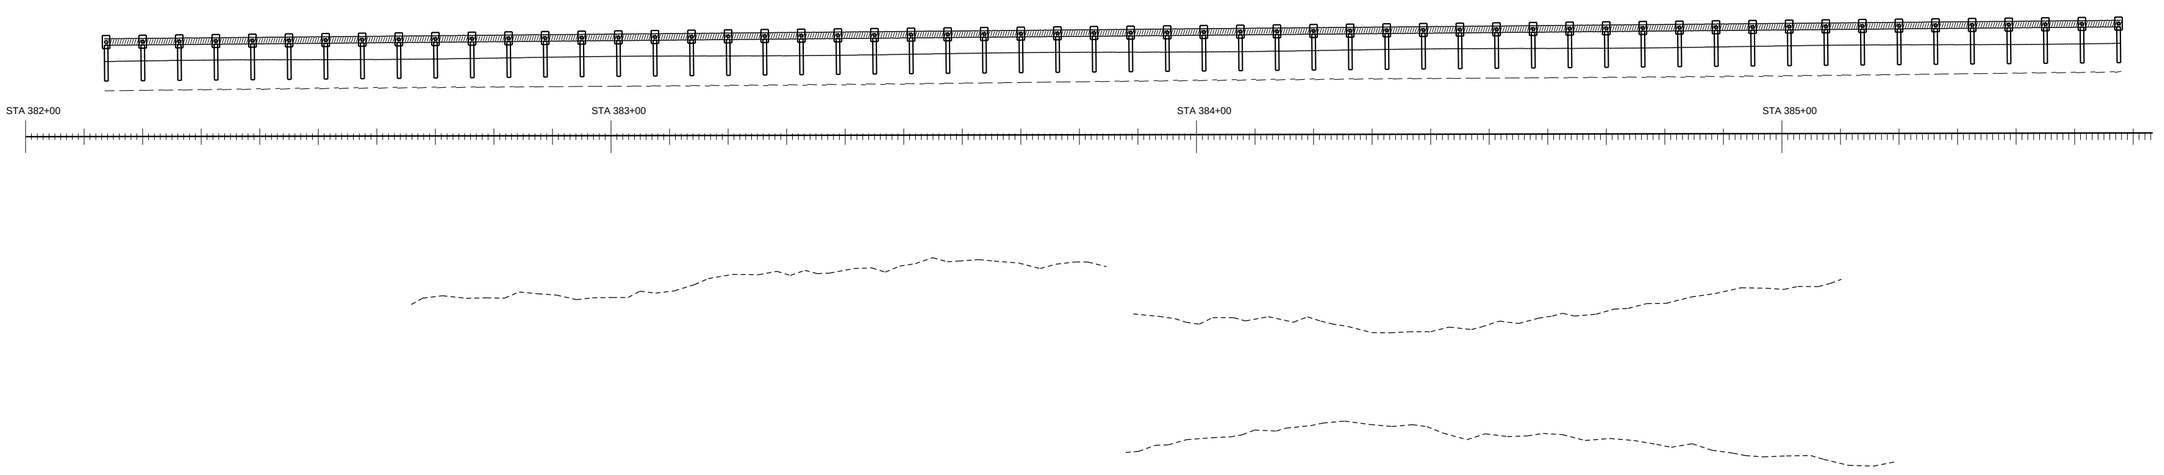


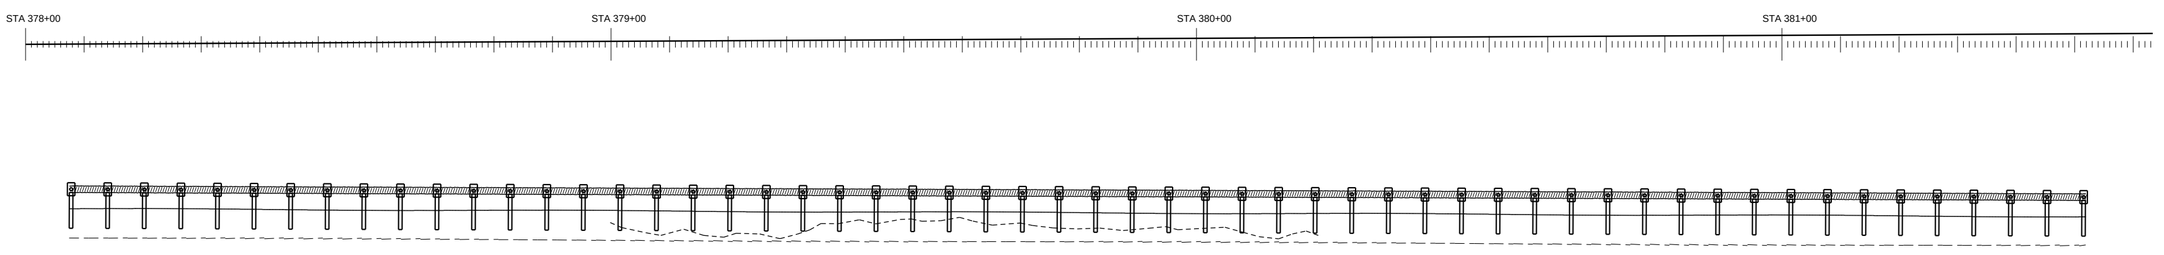


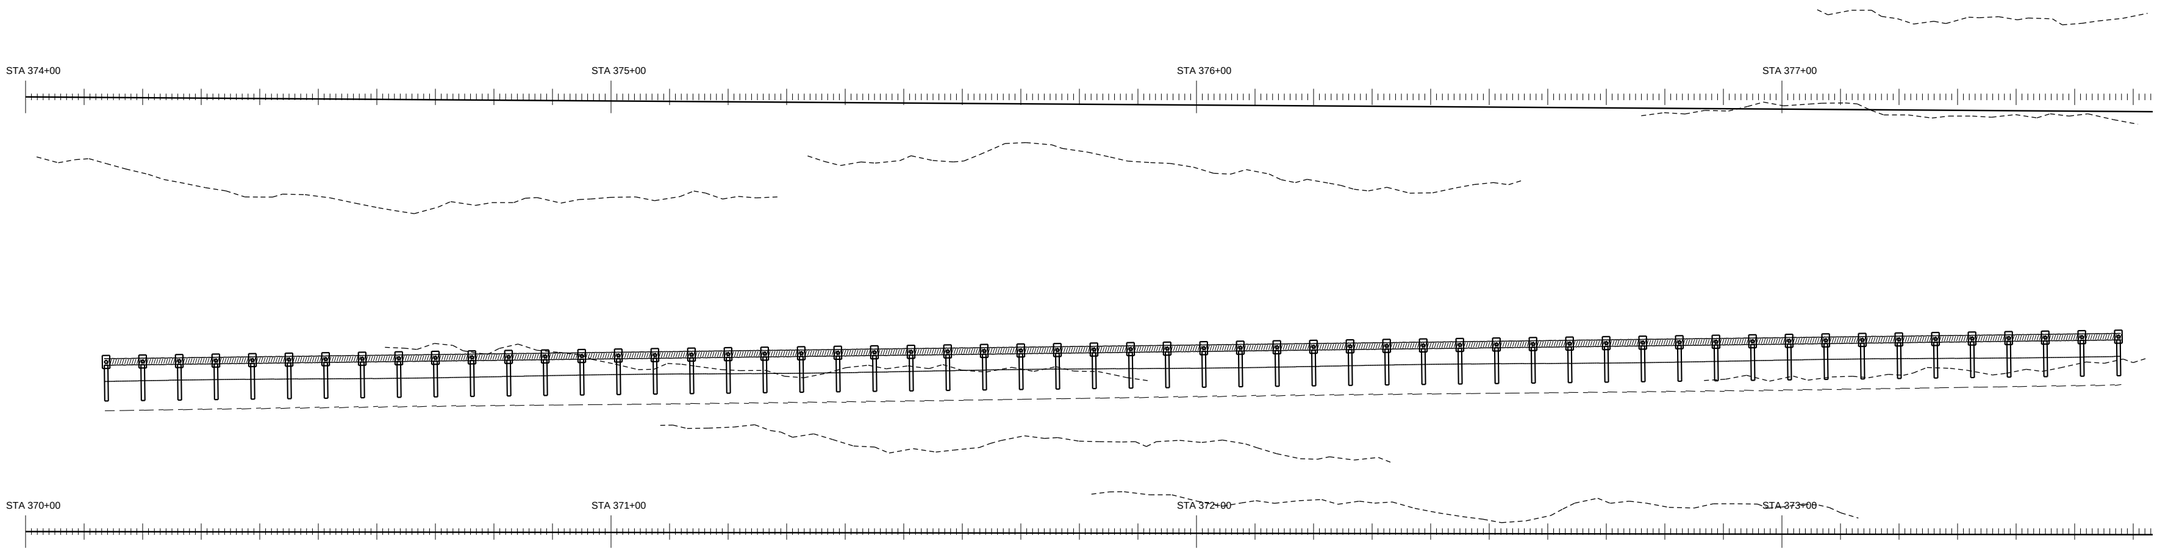


PAY ITEM 536-1-1 GUARDRAIL ROADWAY (TL-3)

PAY ITEM 536-85-24 END TREATMENT

GUARANTEED FENCE CORP

FIN. PROJ. ID 441234-1-52-01

SHEET 19 OF 120

SHEET NO. 119

ROADWAY PLAN SCALE: 1" = 20'




PAY ITEM 536-1-1 GUARDRAIL ROADWAY (TL-3)

PAY ITEM 536-85-24 END TREATMENT

GUARANTEED FENCE CORP

FIN. PROJ. ID 441234-1-52-01

SHEET 20 OF 120

SHEET NO. 120

ROADWAY PLAN SCALE: 1" = 20'

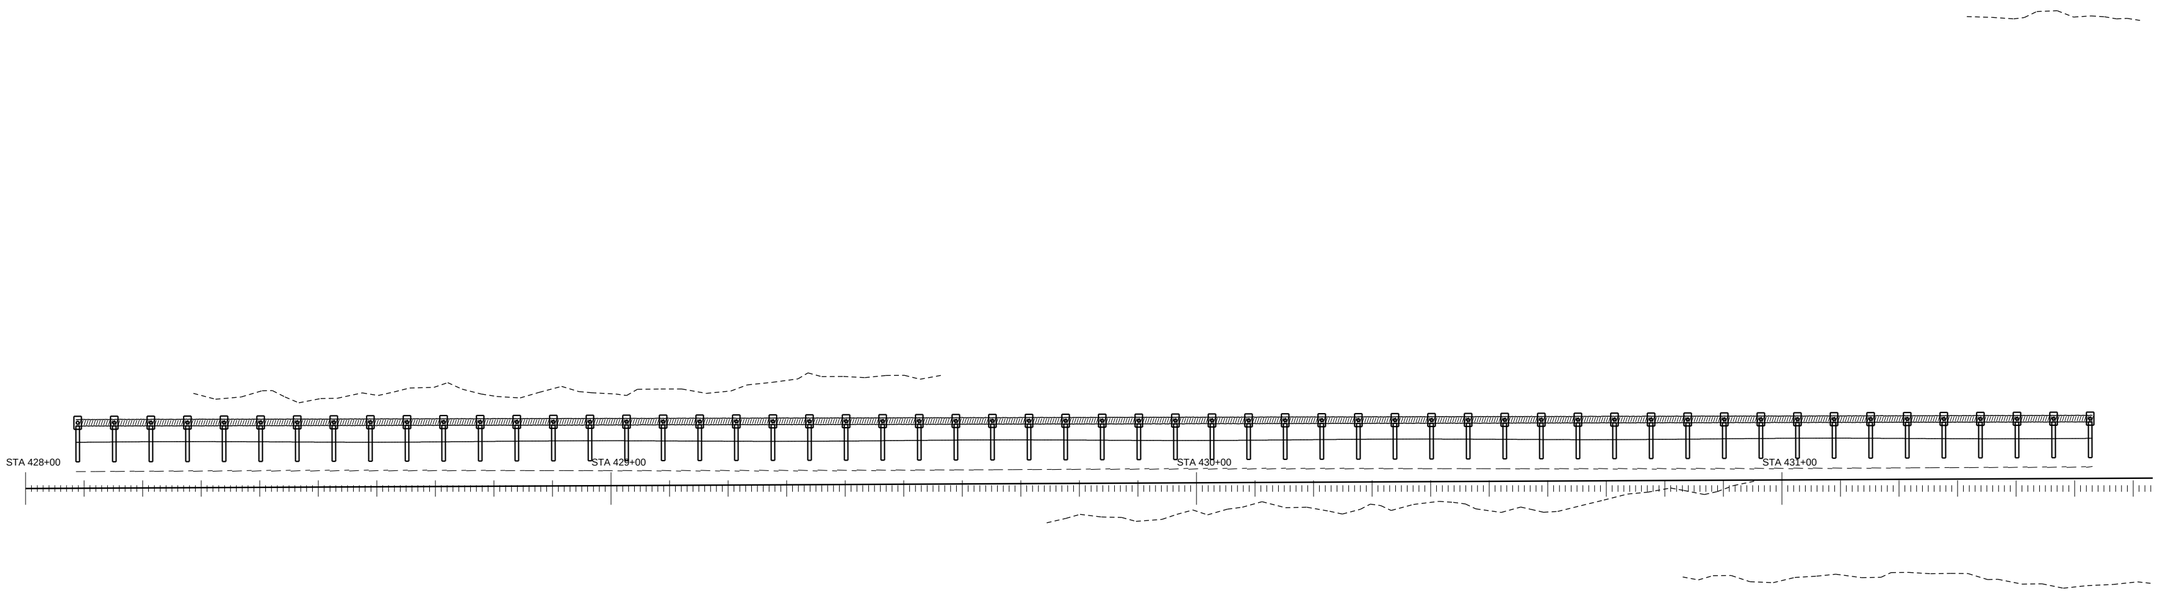


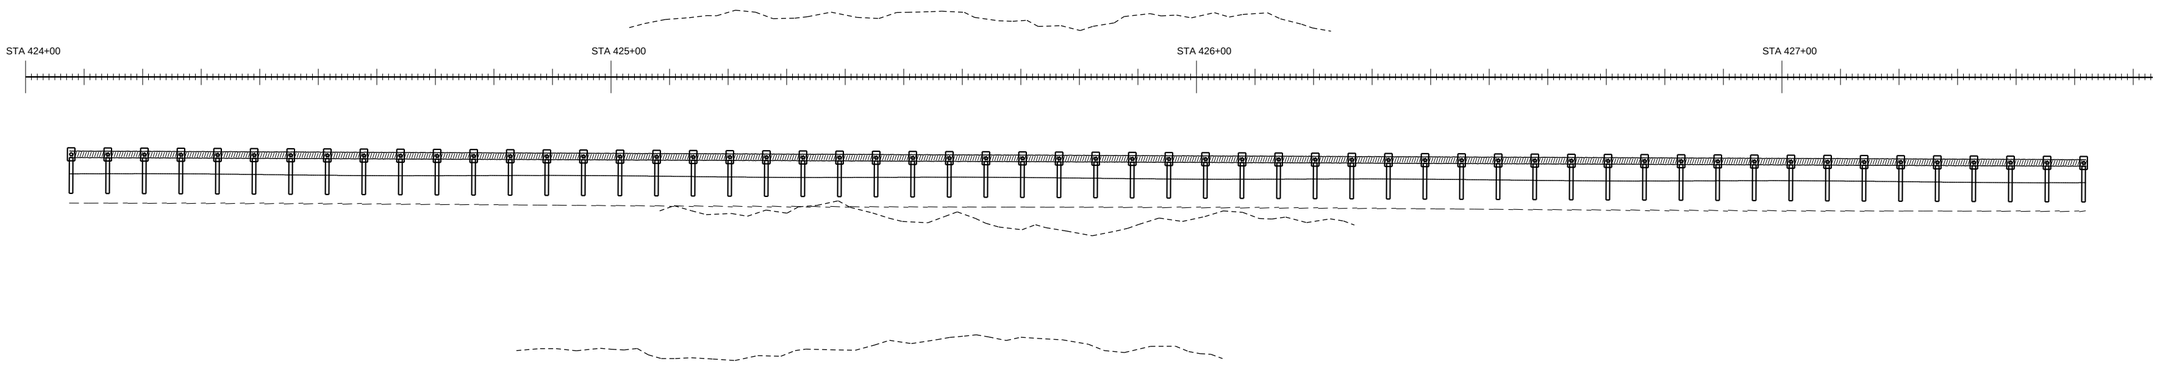


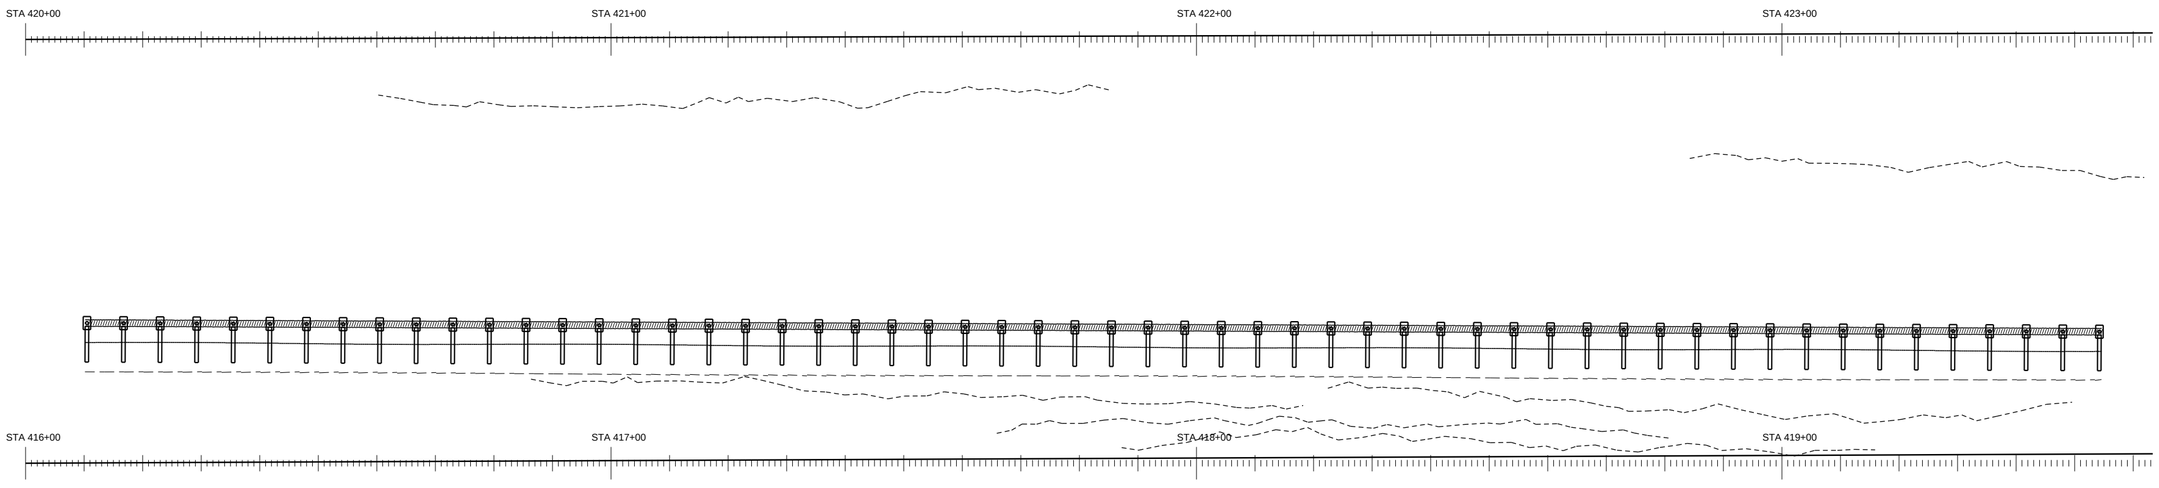


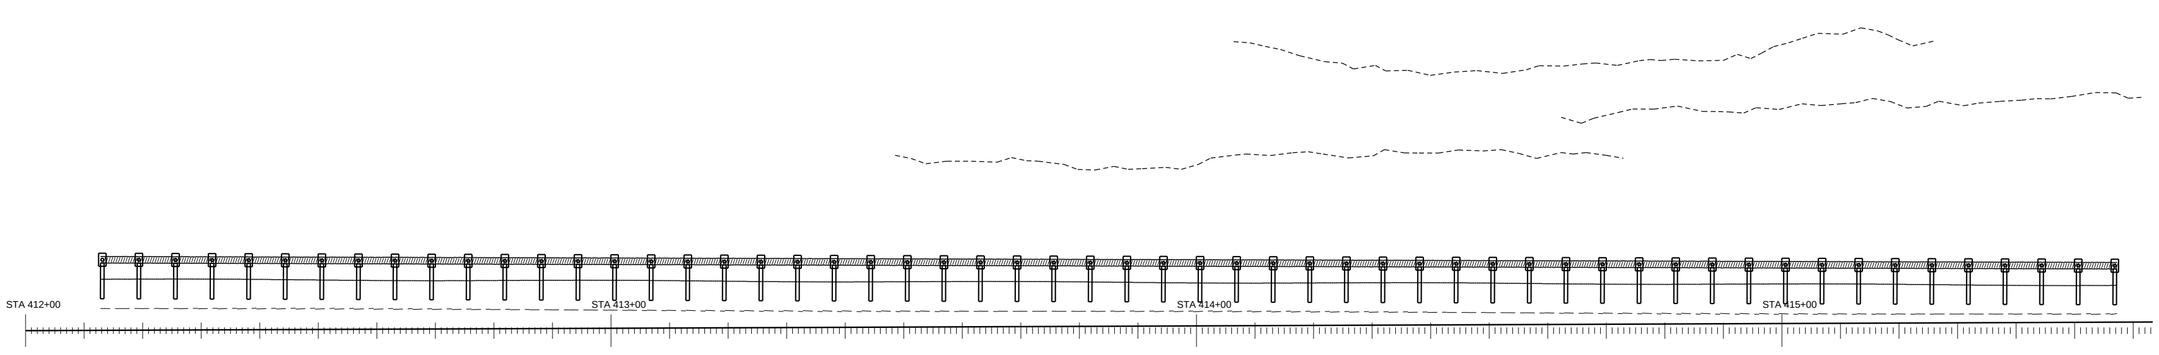


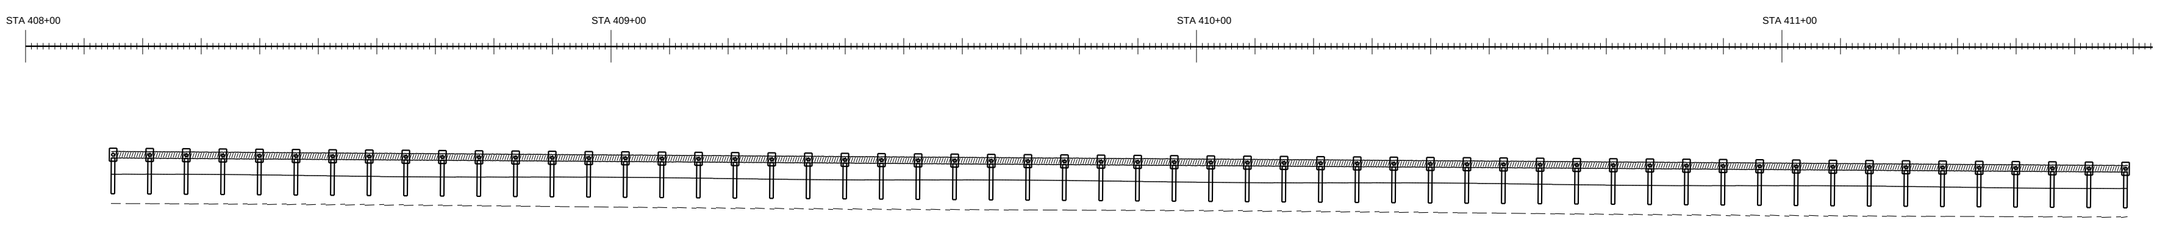


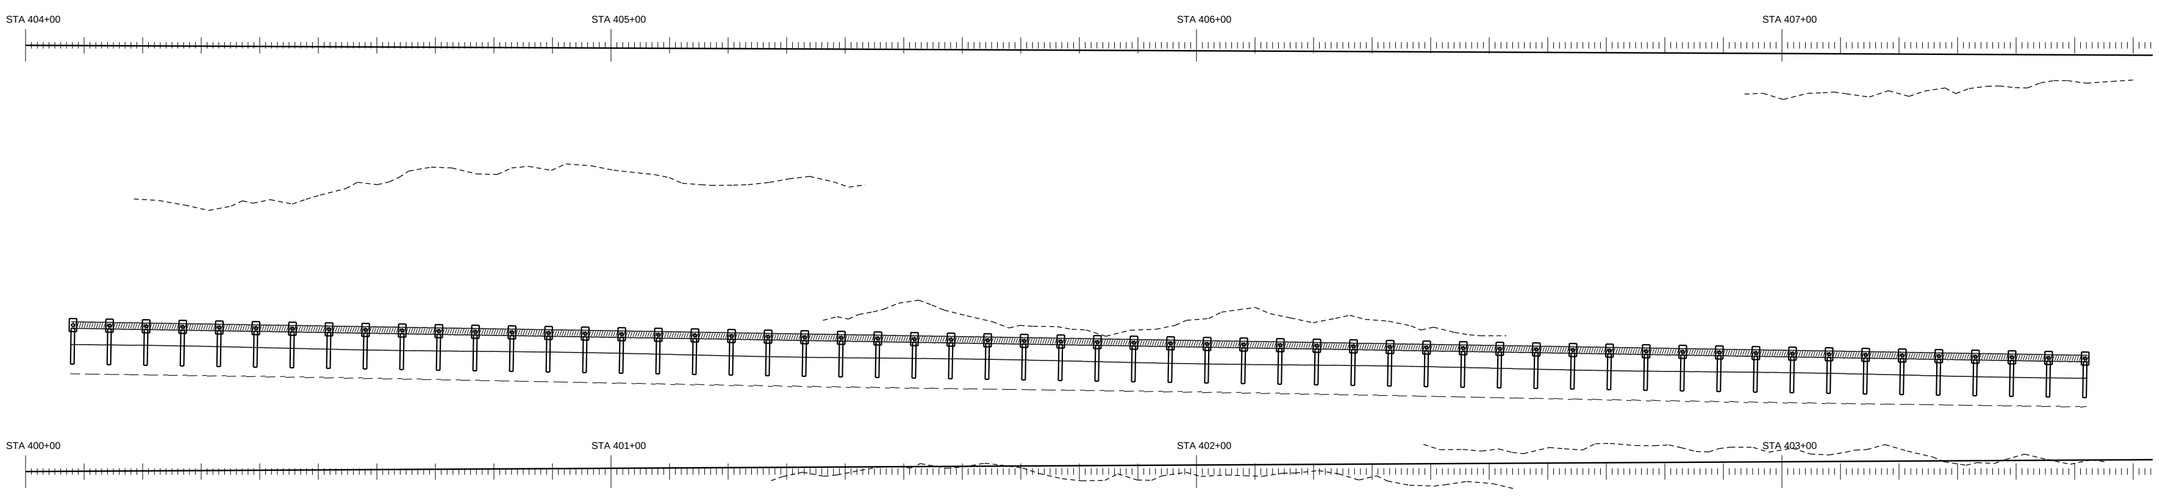


PAY ITEM 536-1-1 GUARDRAIL ROADWAY (TL-3)

PAY ITEM 536-85-24 END TREATMENT

GUARANTEED FENCE CORP

FIN. PROJ. ID 441234-1-52-01

SHEET 21 OF 120

SHEET NO. 121

ROADWAY PLAN SCALE: 1" = 20'




PAY ITEM 536-1-1 GUARDRAIL ROADWAY (TL-3)

PAY ITEM 536-85-24 END TREATMENT

GUARANTEED FENCE CORP

FIN. PROJ. ID 441234-1-52-01

SHEET 22 OF 120

SHEET NO. 122

ROADWAY PLAN SCALE: 1" = 20'




PAY ITEM 536-1-1 GUARDRAIL ROADWAY (TL-3)

PAY ITEM 536-85-24 END TREATMENT

GUARANTEED FENCE CORP

FIN. PROJ. ID 441234-1-52-01

SHEET 23 OF 120

SHEET NO. 123

ROADWAY PLAN SCALE: 1" = 20'

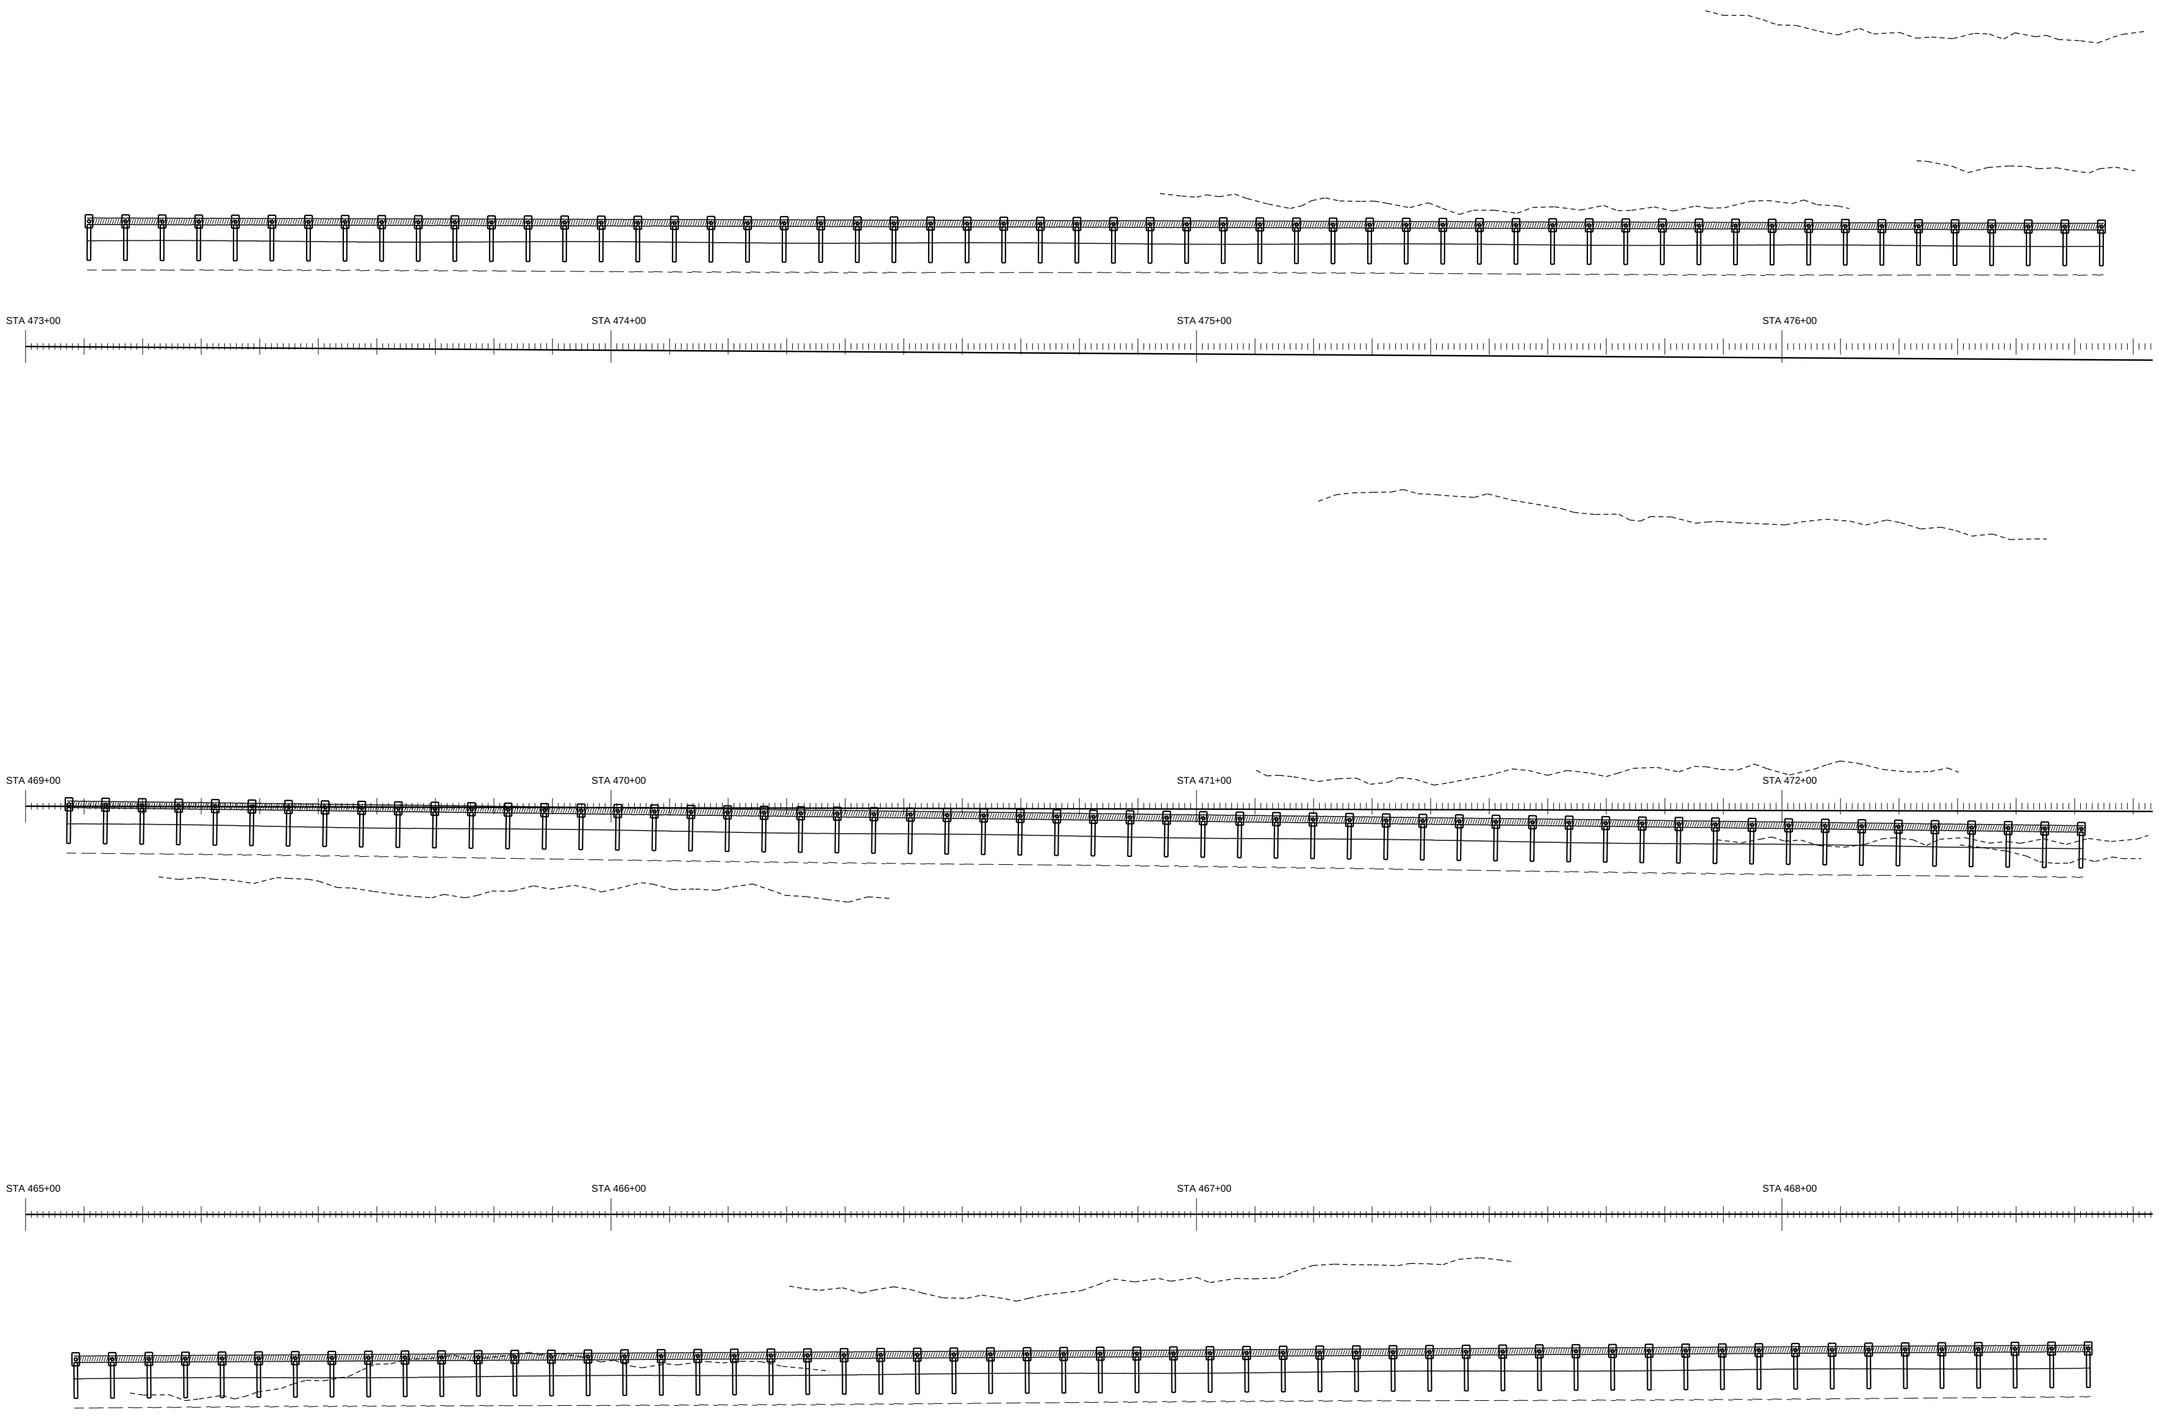


PAY ITEM 536-1-1 GUARDRAIL ROADWAY (TL-3)

PAY ITEM 536-85-24 END TREATMENT

GUARANTEED FENCE CORP

FIN. PROJ. ID 441234-1-52-01

SHEET 24 OF 120

SHEET NO. 124

ROADWAY PLAN SCALE: 1" = 20'

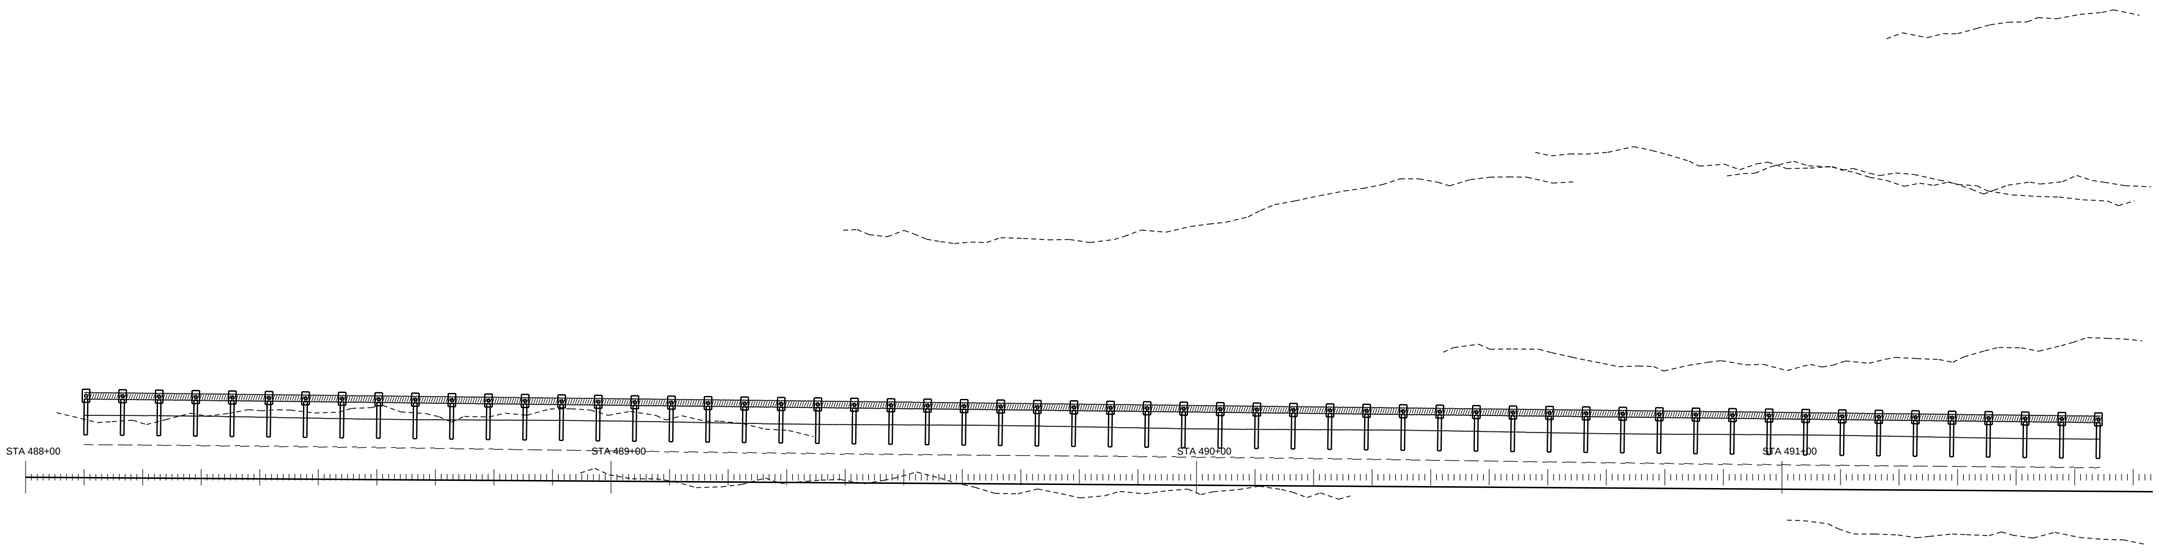

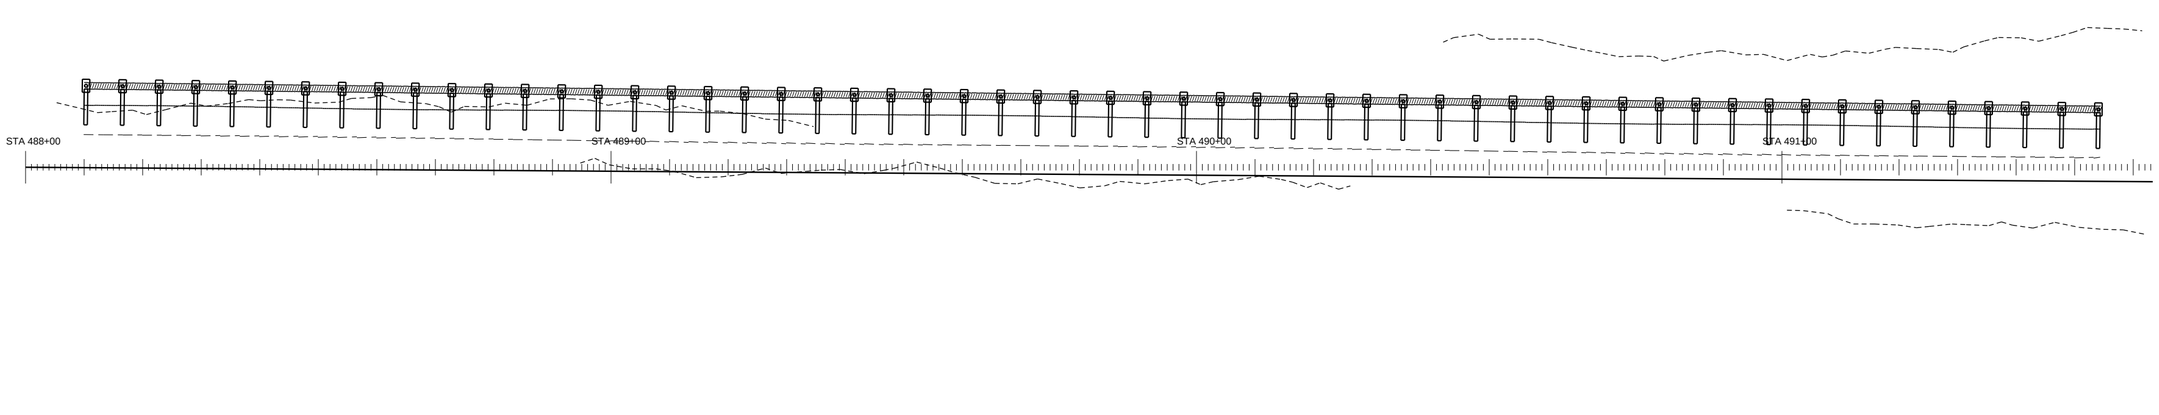








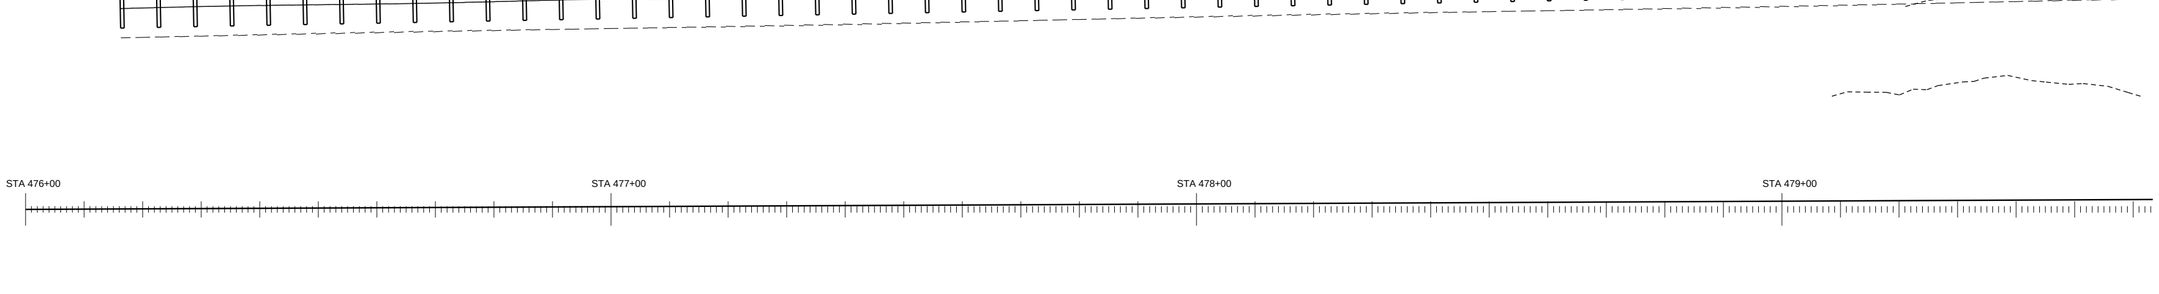





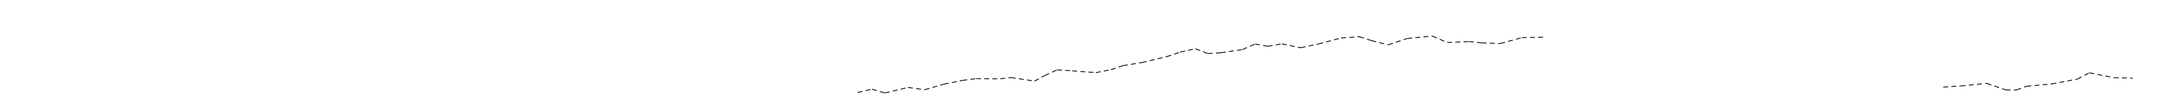


PAY ITEM 536-1-1 GUARDRAIL ROADWAY (TL-3)

PAY ITEM 536-85-24 END TREATMENT

GUARANTEED FENCE CORP

FIN. PROJ. ID 441234-1-52-01

SHEET 25 OF 120

SHEET NO. 125

ROADWAY PLAN SCALE: 1" = 20'




PAY ITEM 536-1-1 GUARDRAIL ROADWAY (TL-3)

PAY ITEM 536-85-24 END TREATMENT

GUARANTEED FENCE CORP

FIN. PROJ. ID 441234-1-52-01

SHEET 26 OF 120

SHEET NO. 126

ROADWAY PLAN SCALE: 1" = 20'

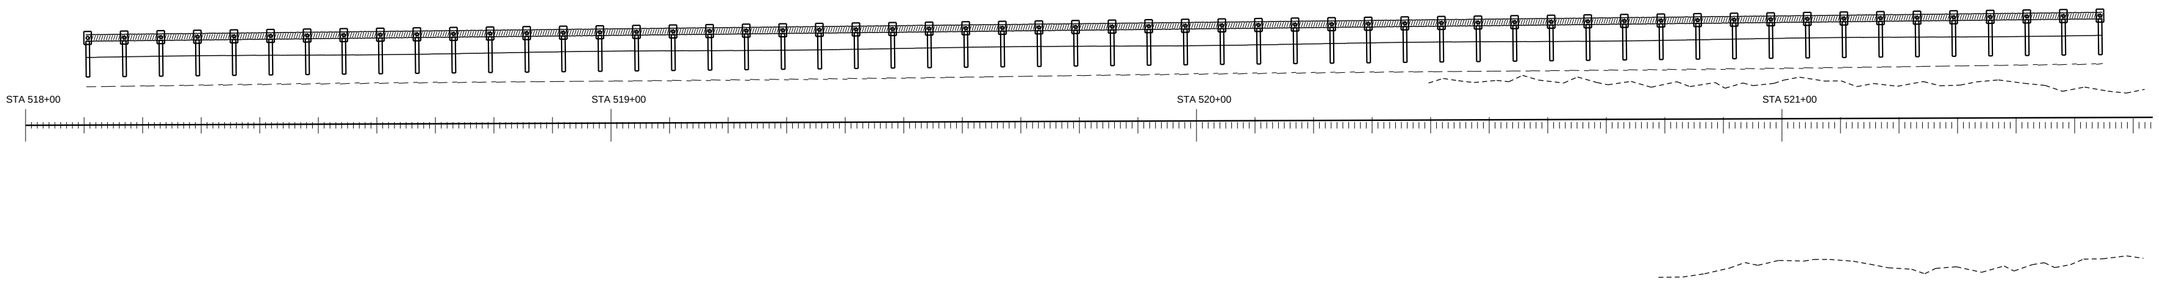


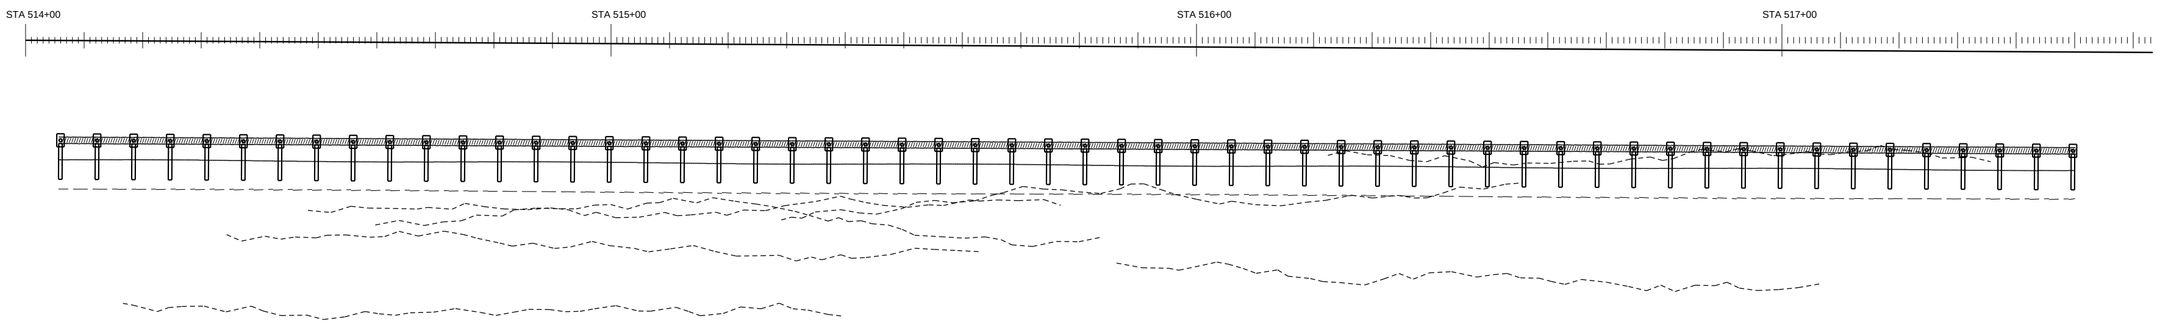


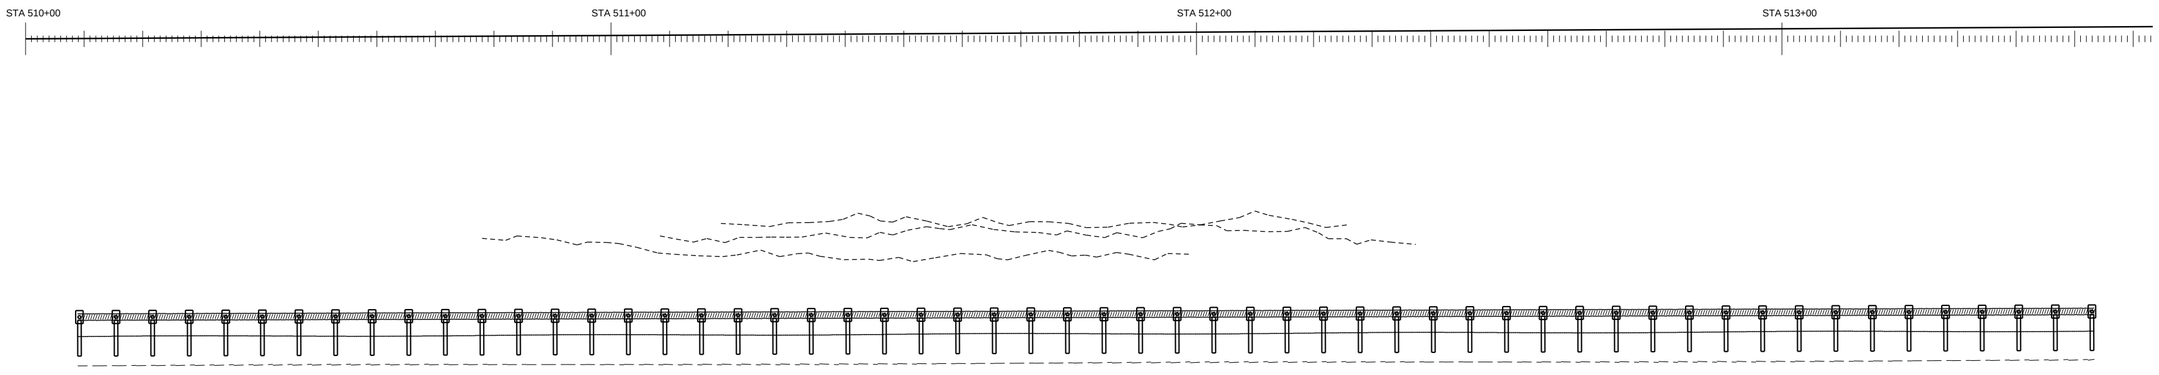

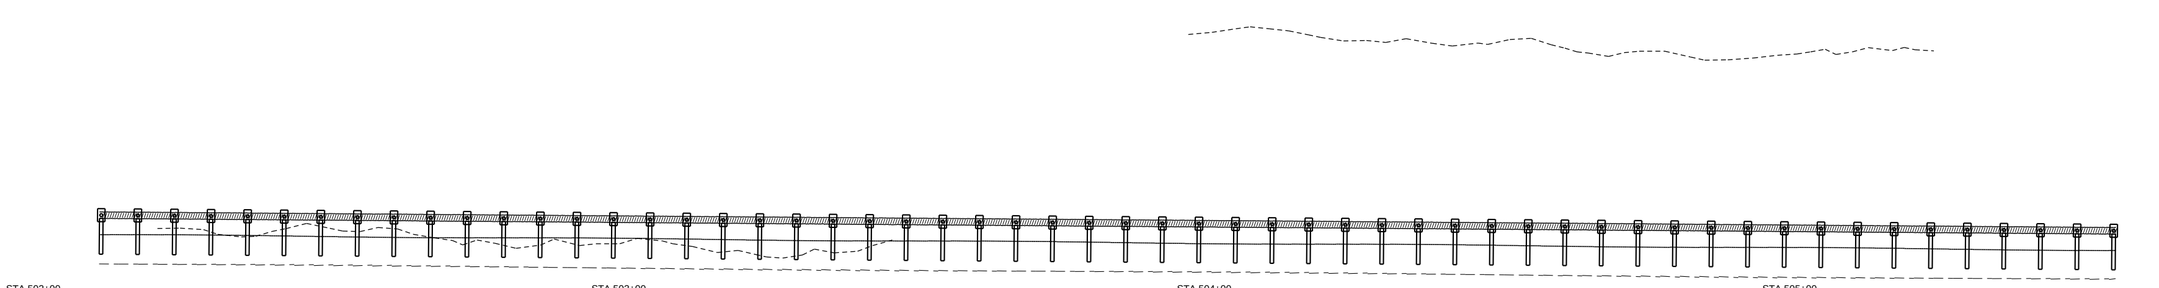


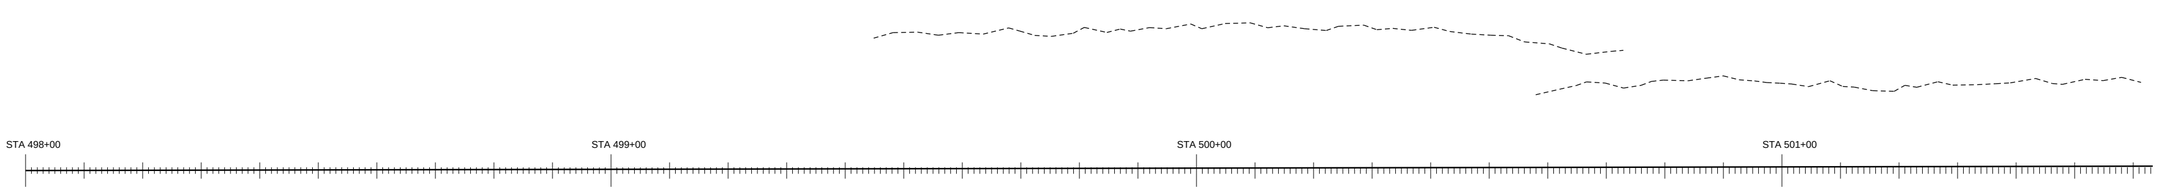


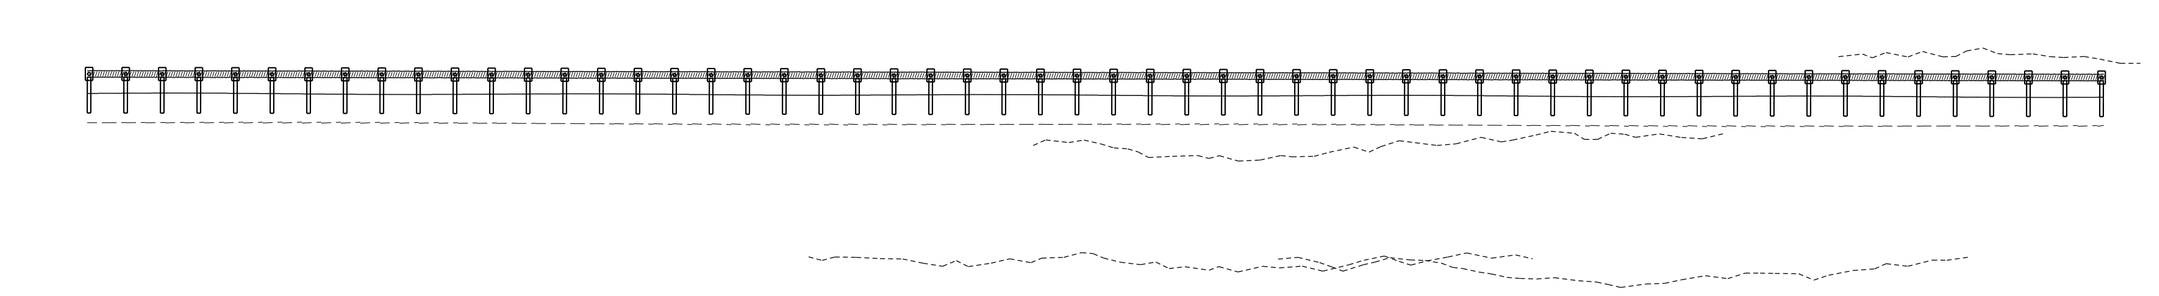


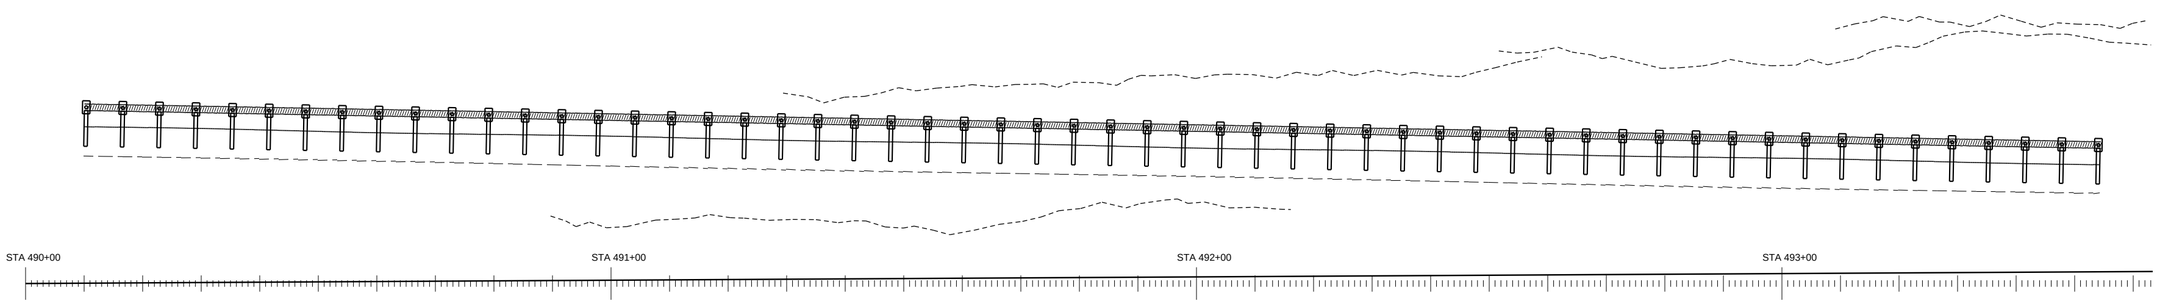


PAY ITEM 536-1-1 GUARDRAIL ROADWAY (TL-3)

PAY ITEM 536-85-24 END TREATMENT

GUARANTEED FENCE CORP

FIN. PROJ. ID 441234-1-52-01

SHEET 27 OF 120

SHEET NO. 127

ROADWAY PLAN SCALE: 1" = 20'

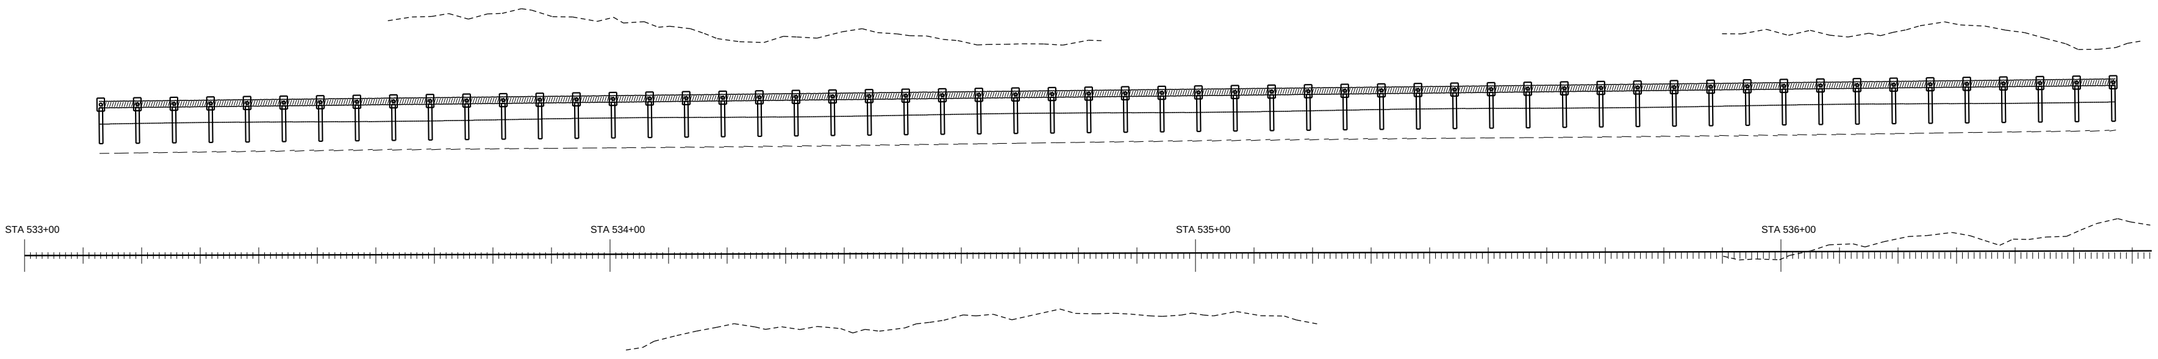


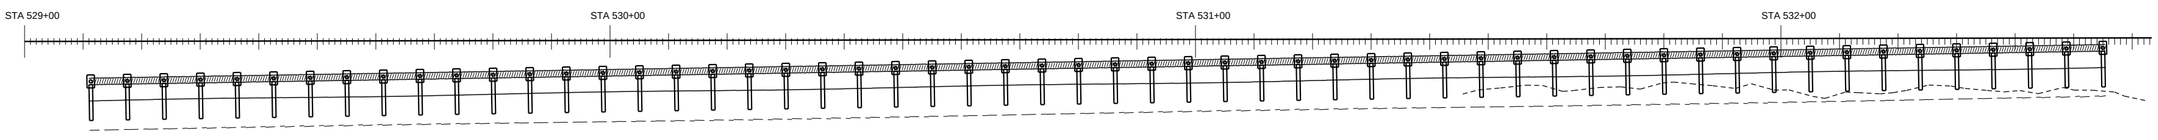


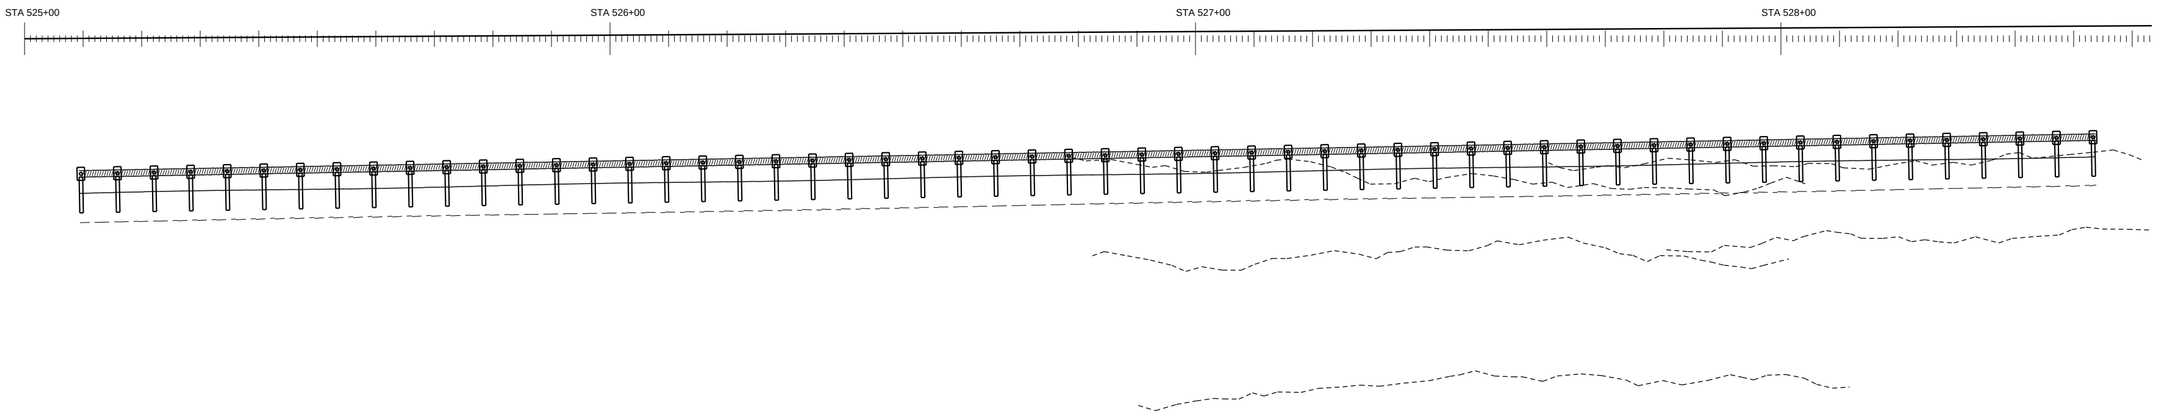





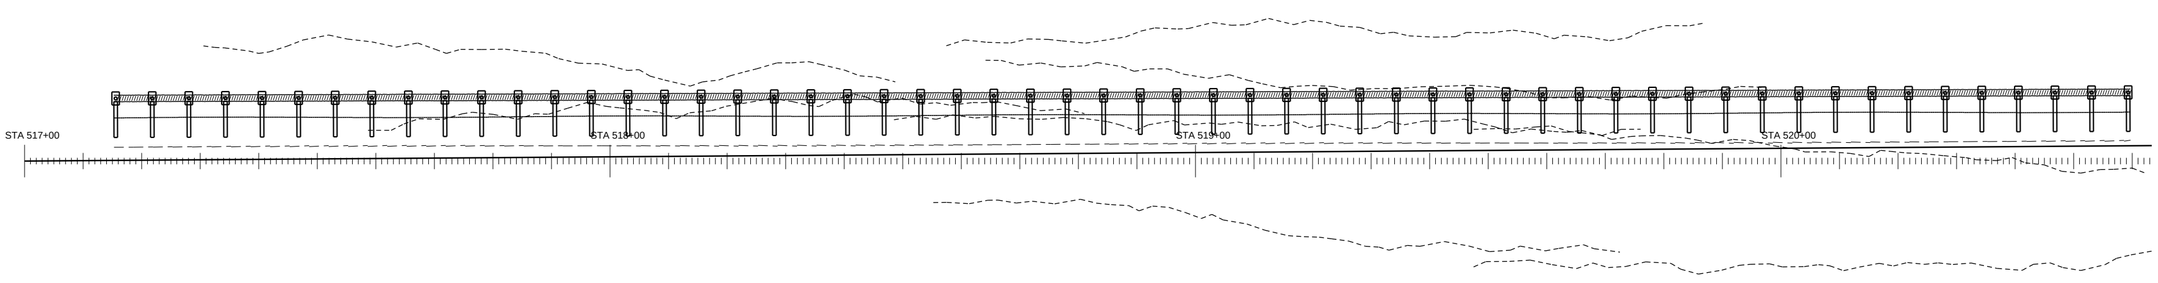


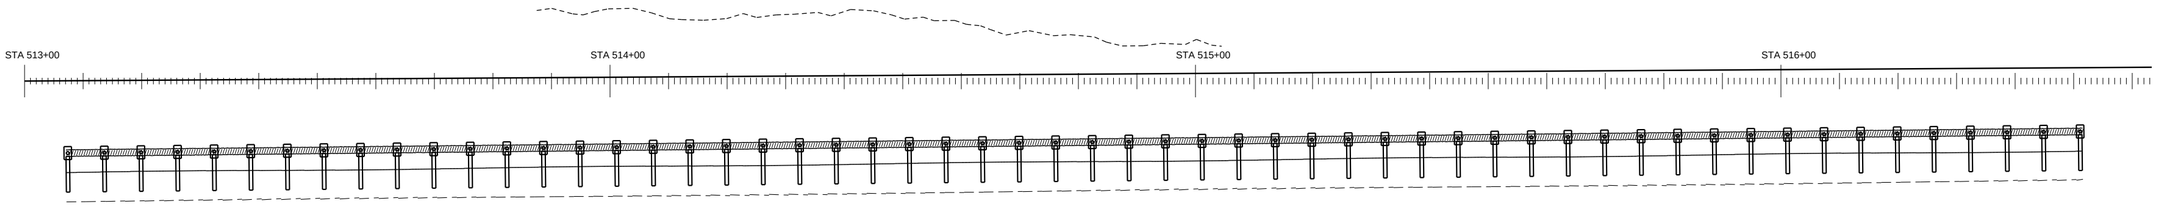


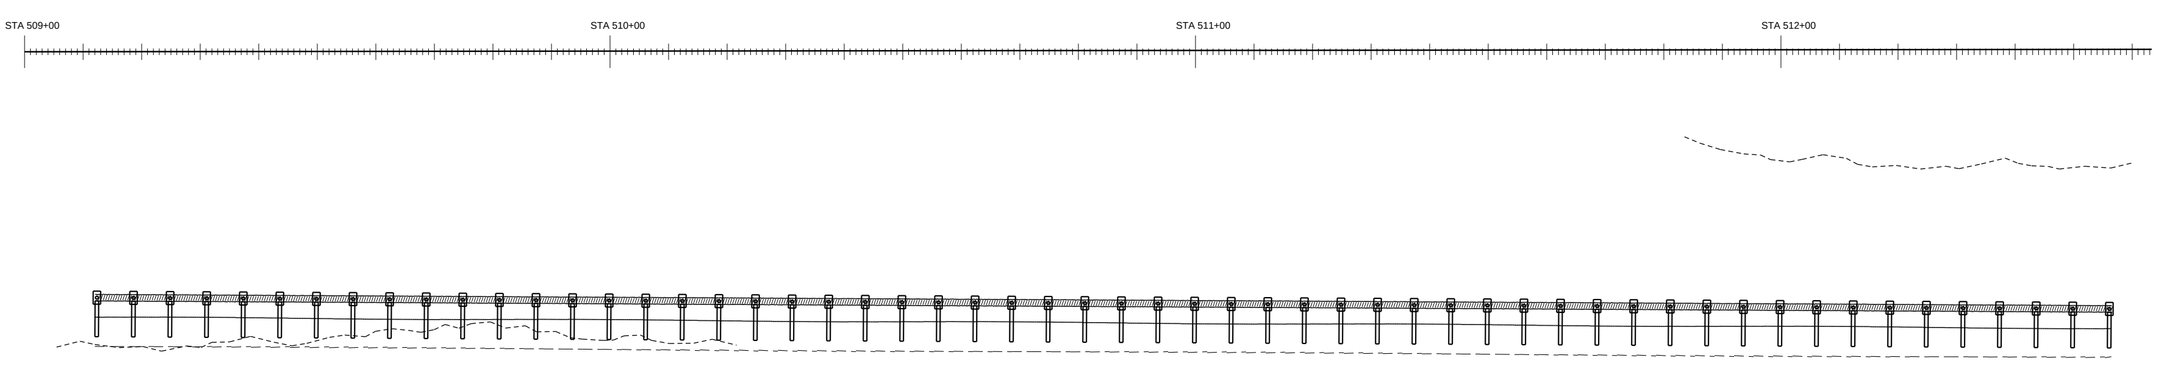

PAY ITEM 536-1-1 GUARDRAIL ROADWAY (TL-3)

PAY ITEM 536-85-24 END TREATMENT

GUARANTEED FENCE CORP

FIN. PROJ. ID 441234-1-52-01

SHEET 28 OF 120

SHEET NO. 128

ROADWAY PLAN SCALE: 1" = 20'

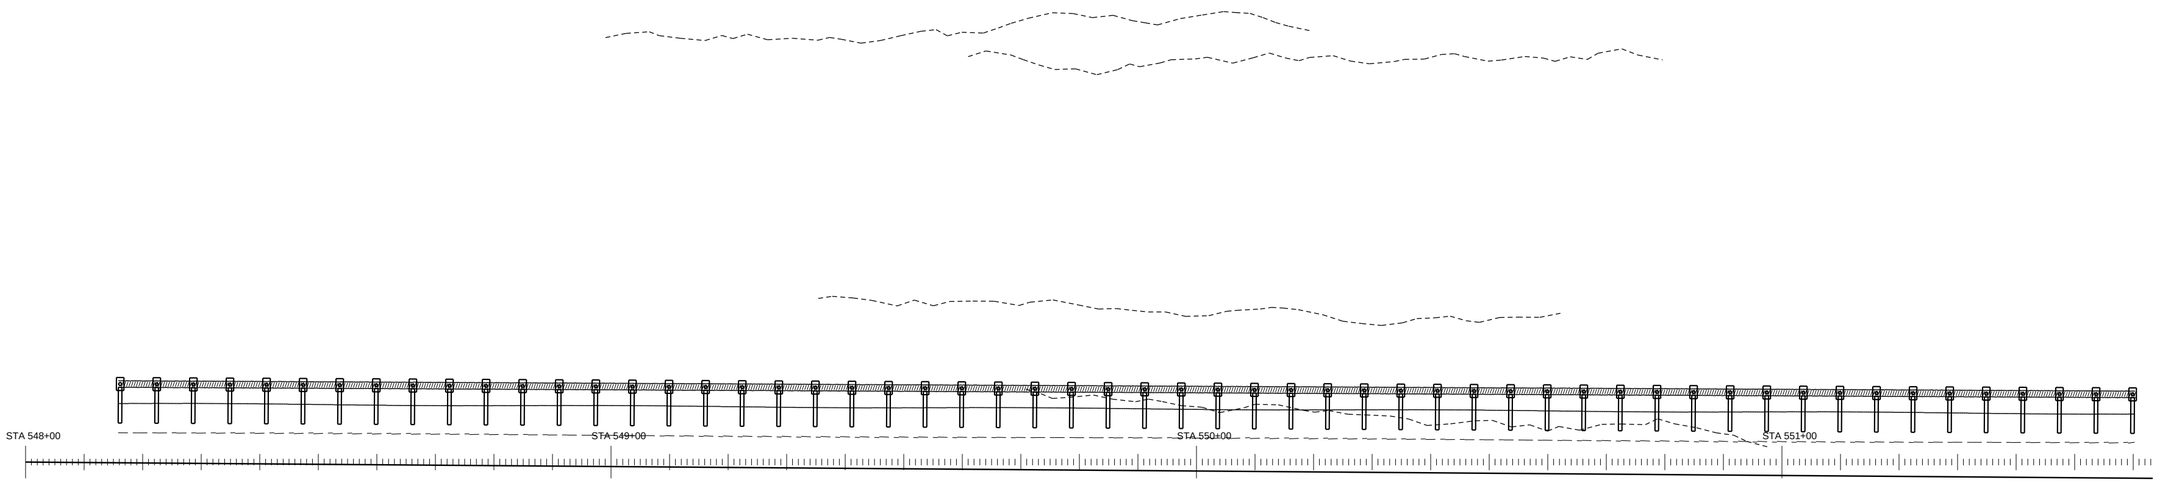


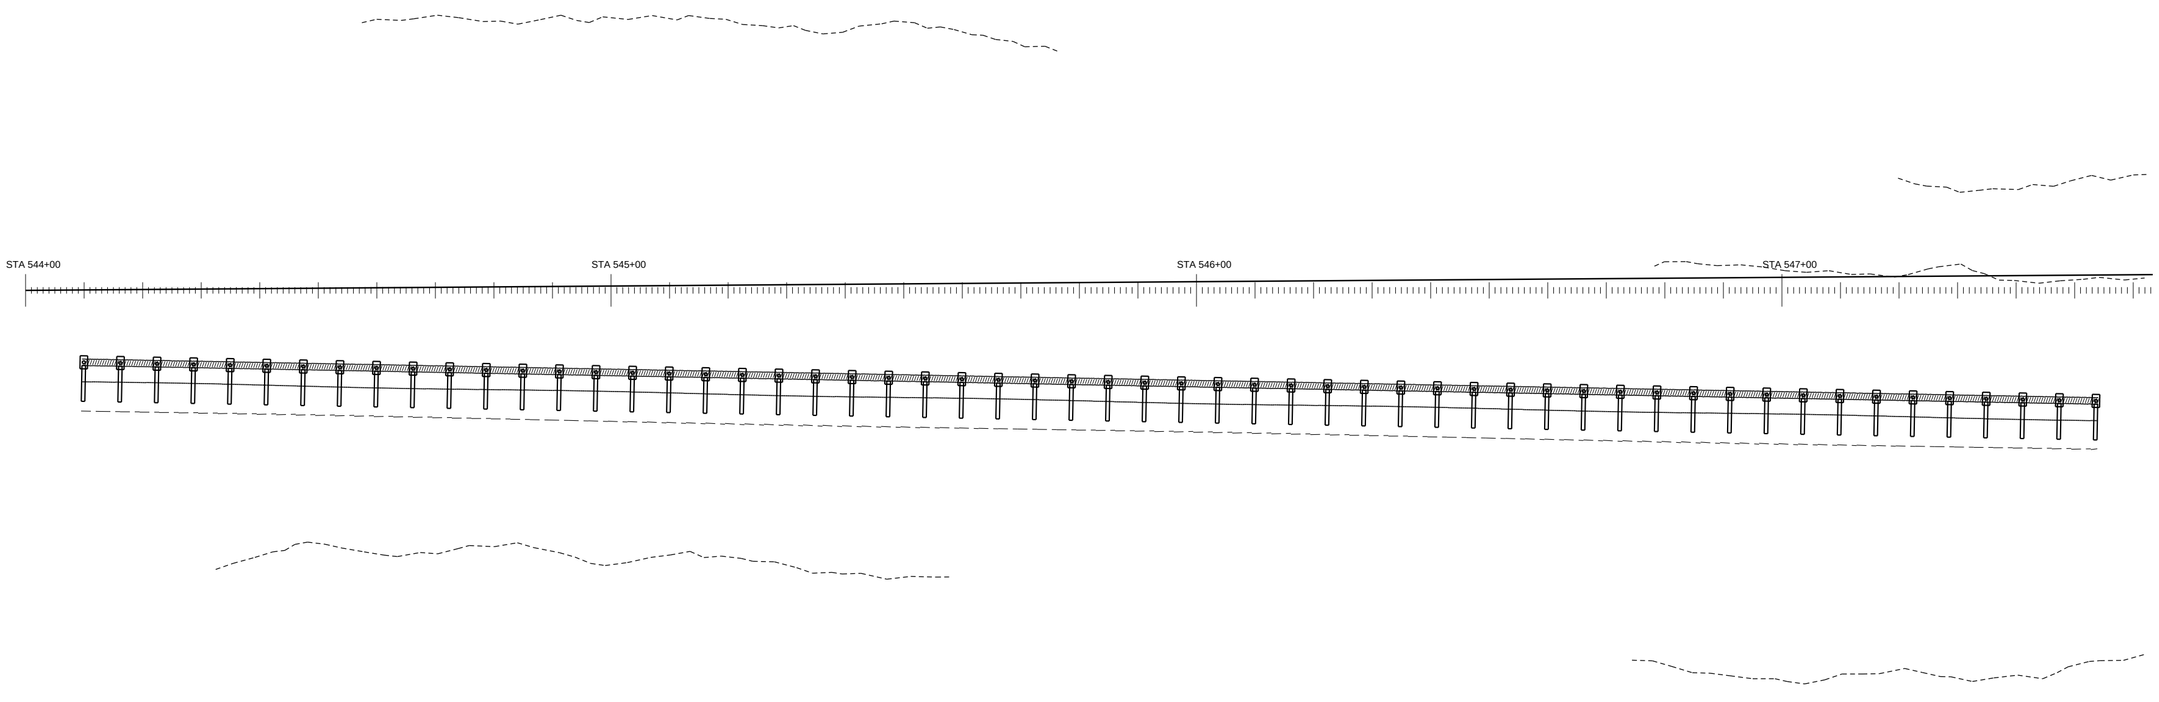


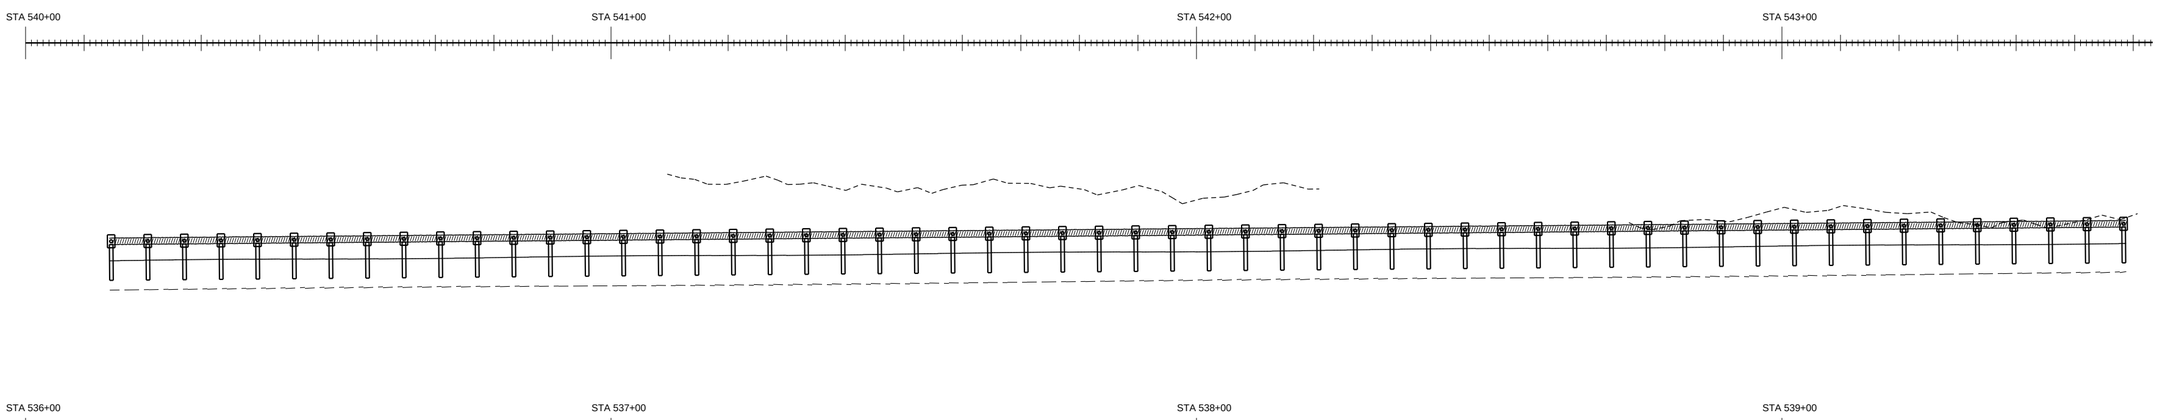


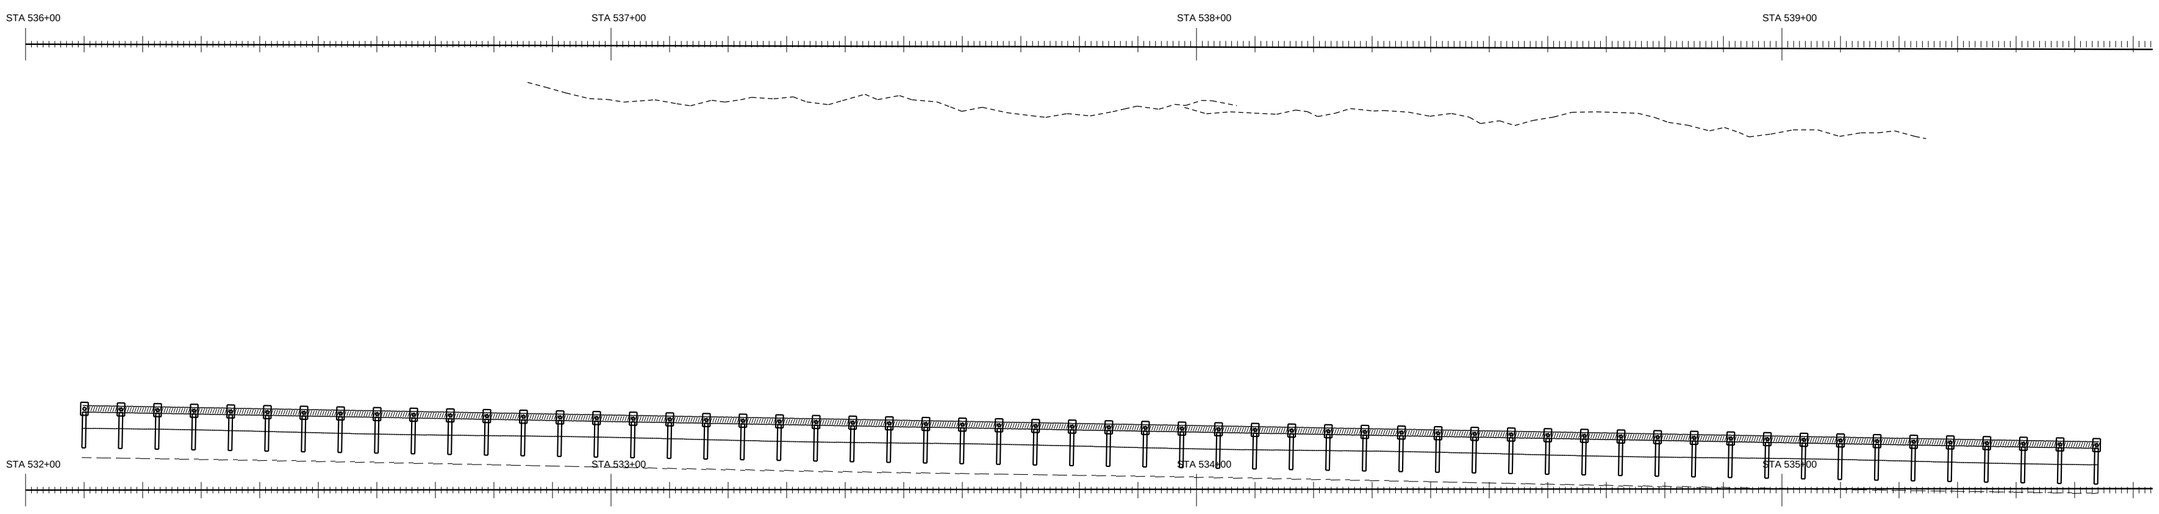





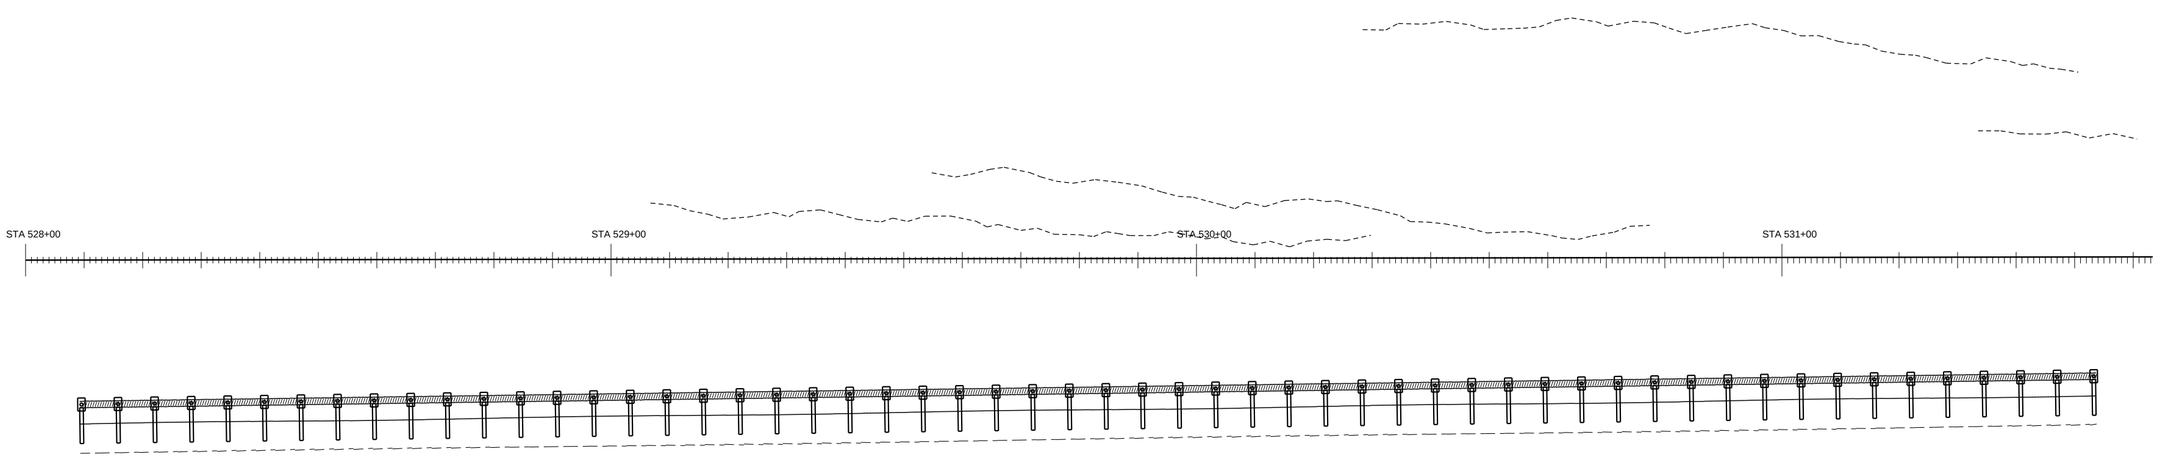


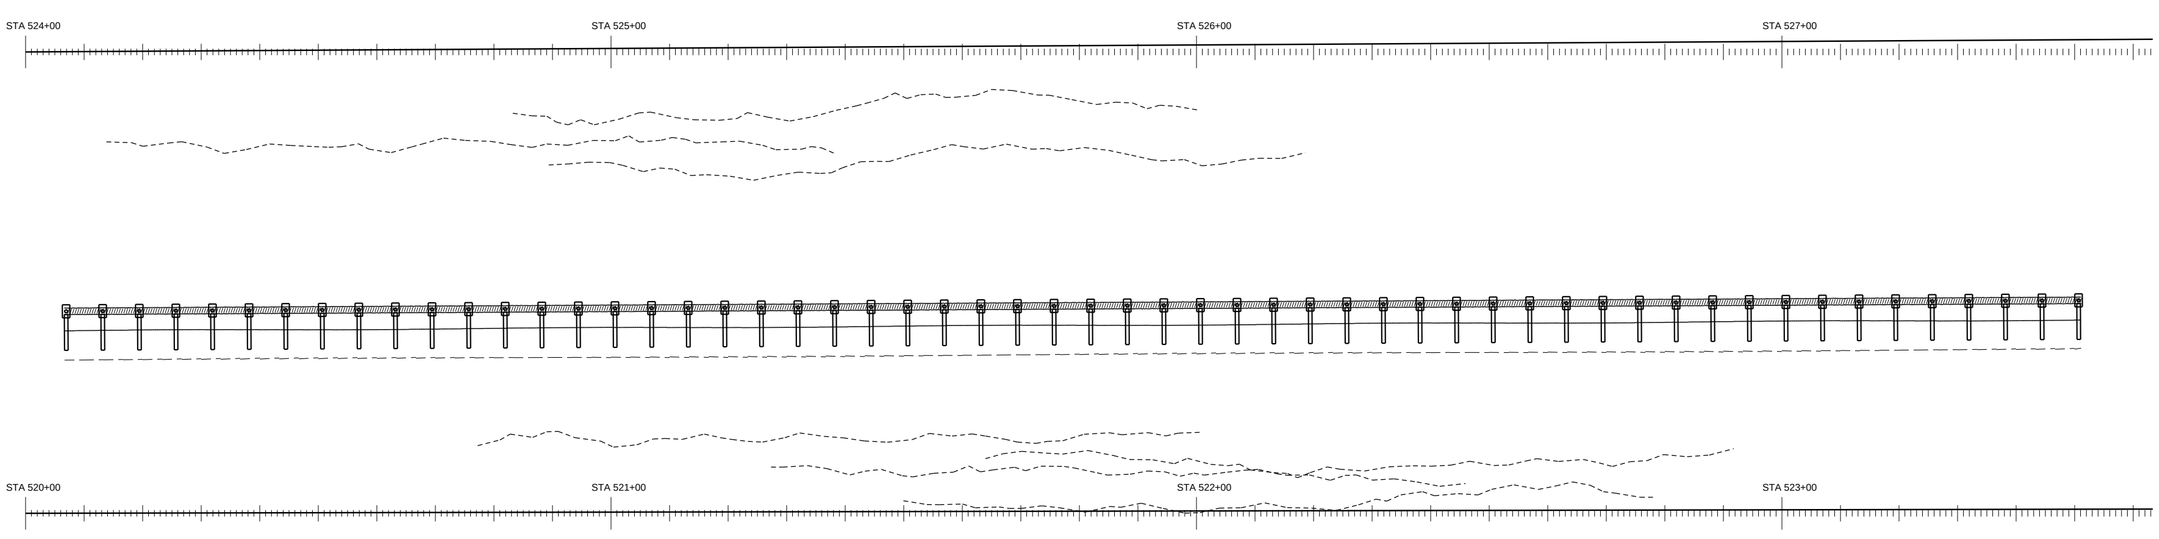


PAY ITEM 536-1-1 GUARDRAIL ROADWAY (TL-3)

PAY ITEM 536-85-24 END TREATMENT

GUARANTEED FENCE CORP

FIN. PROJ. ID 441234-1-52-01

SHEET 29 OF 120

SHEET NO. 129

ROADWAY PLAN SCALE: 1" = 20'




PAY ITEM 536-1-1 GUARDRAIL ROADWAY (TL-3)

PAY ITEM 536-85-24 END TREATMENT

GUARANTEED FENCE CORP

FIN. PROJ. ID 441234-1-52-01

SHEET 30 OF 120

SHEET NO. 130

ROADWAY PLAN SCALE: 1" = 20'

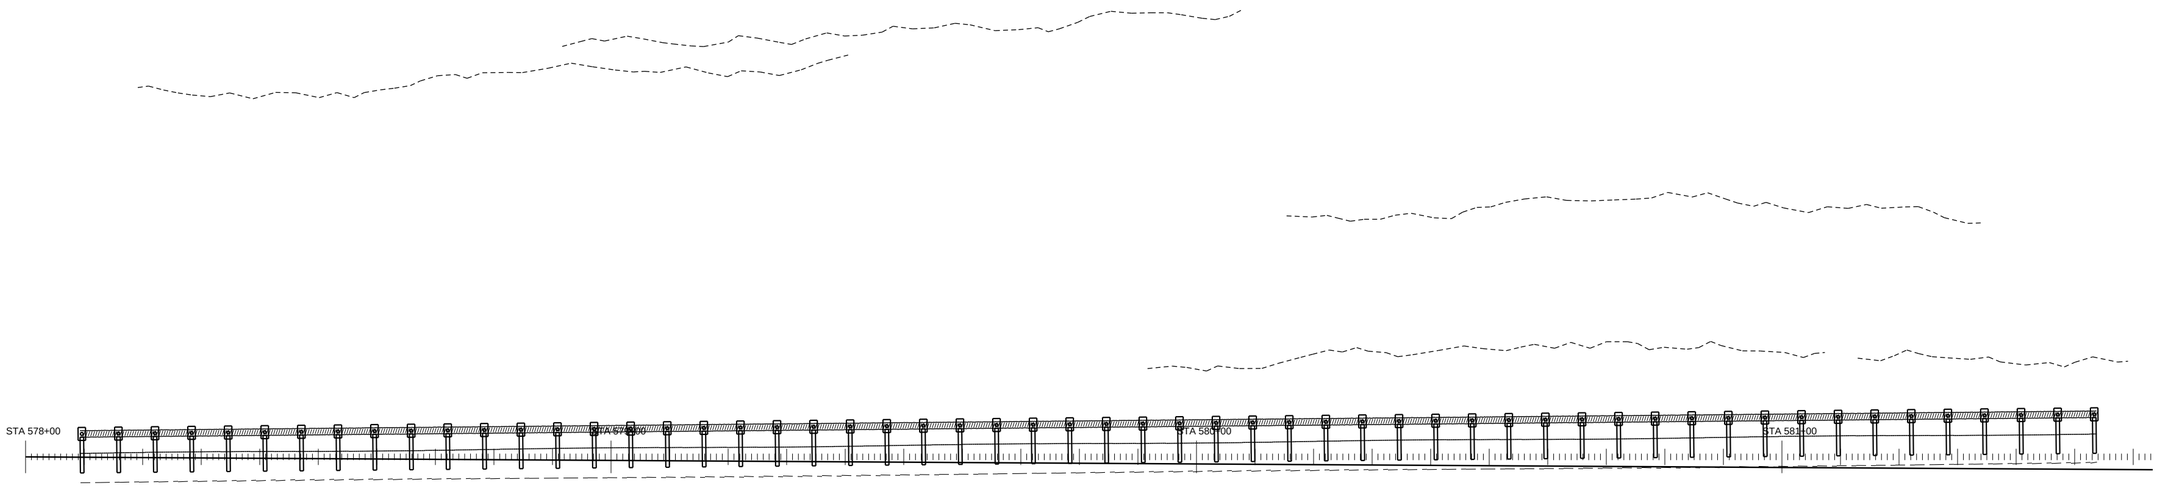


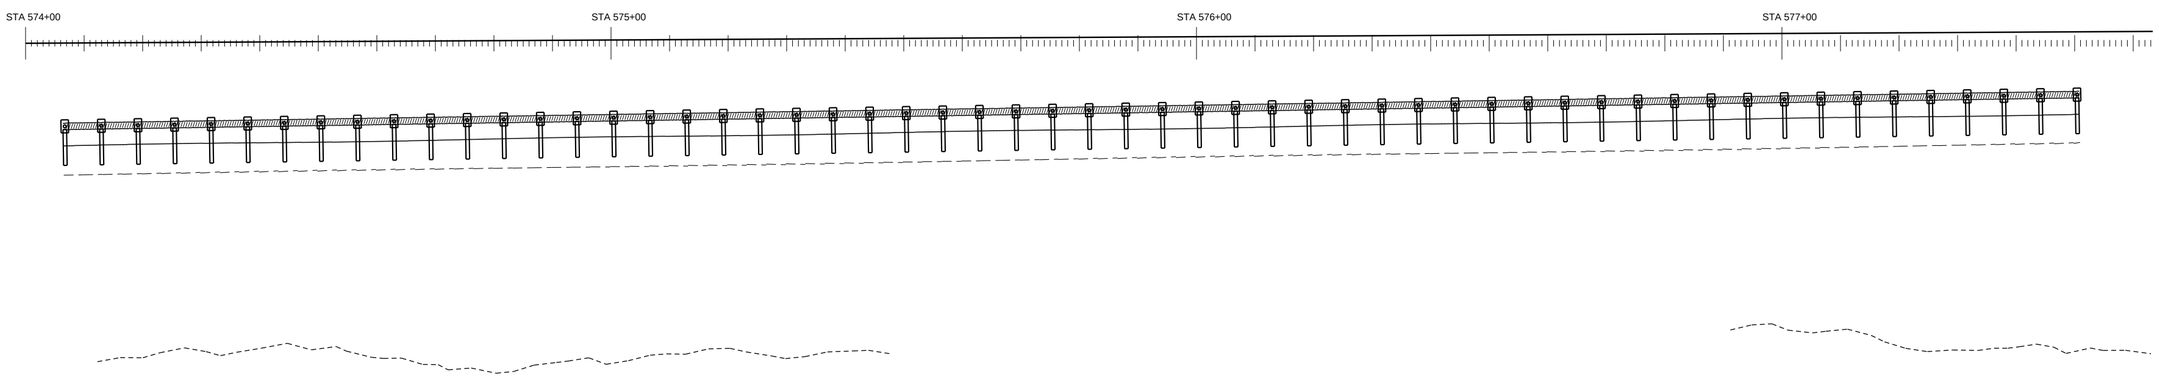


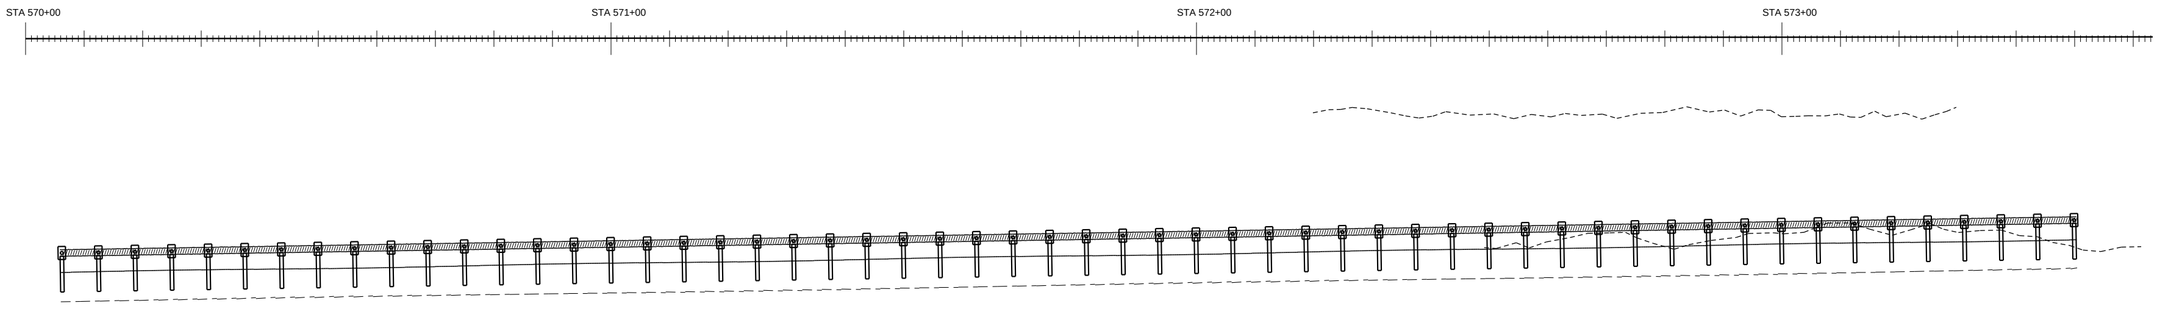


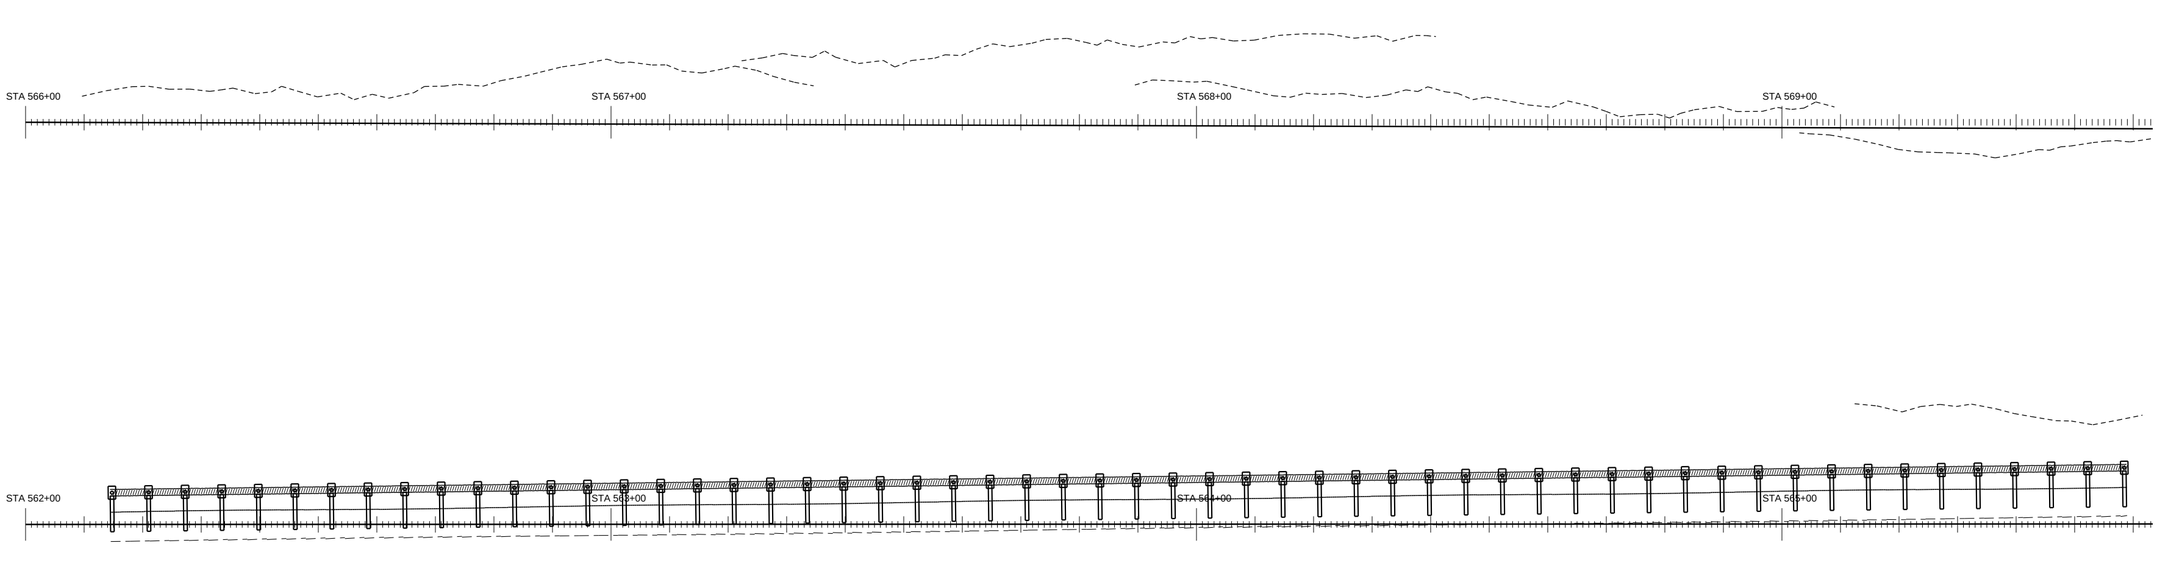


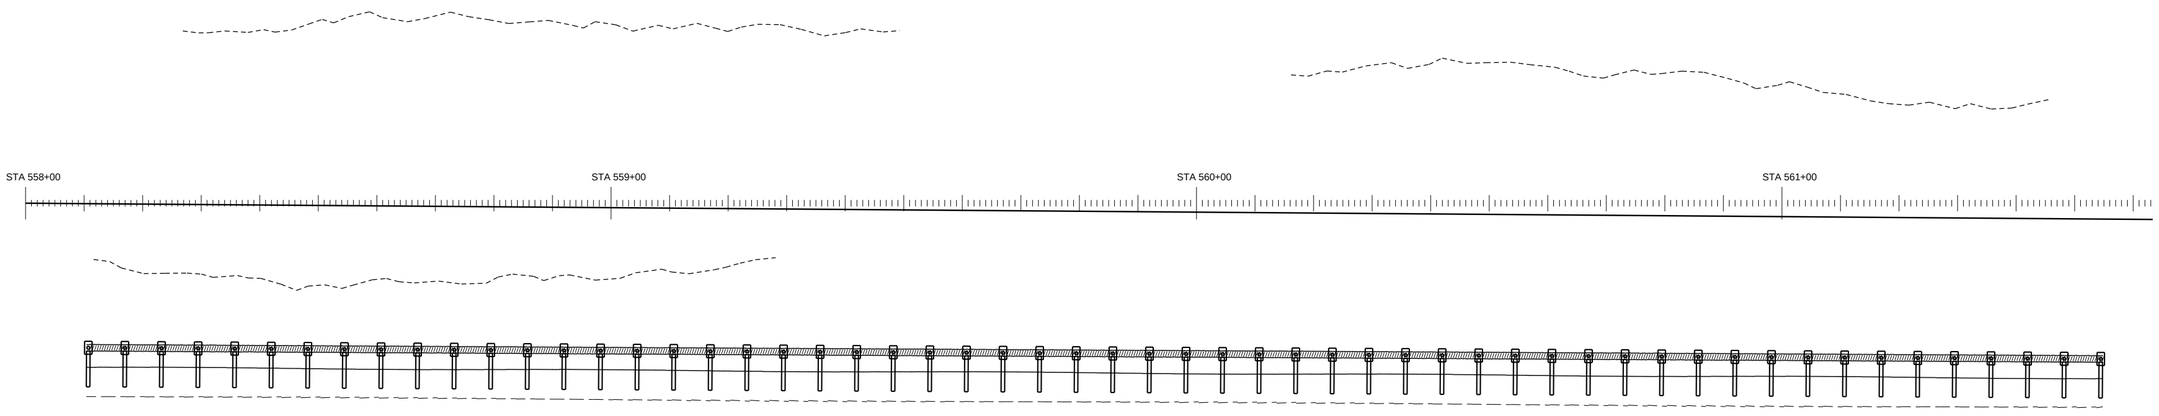


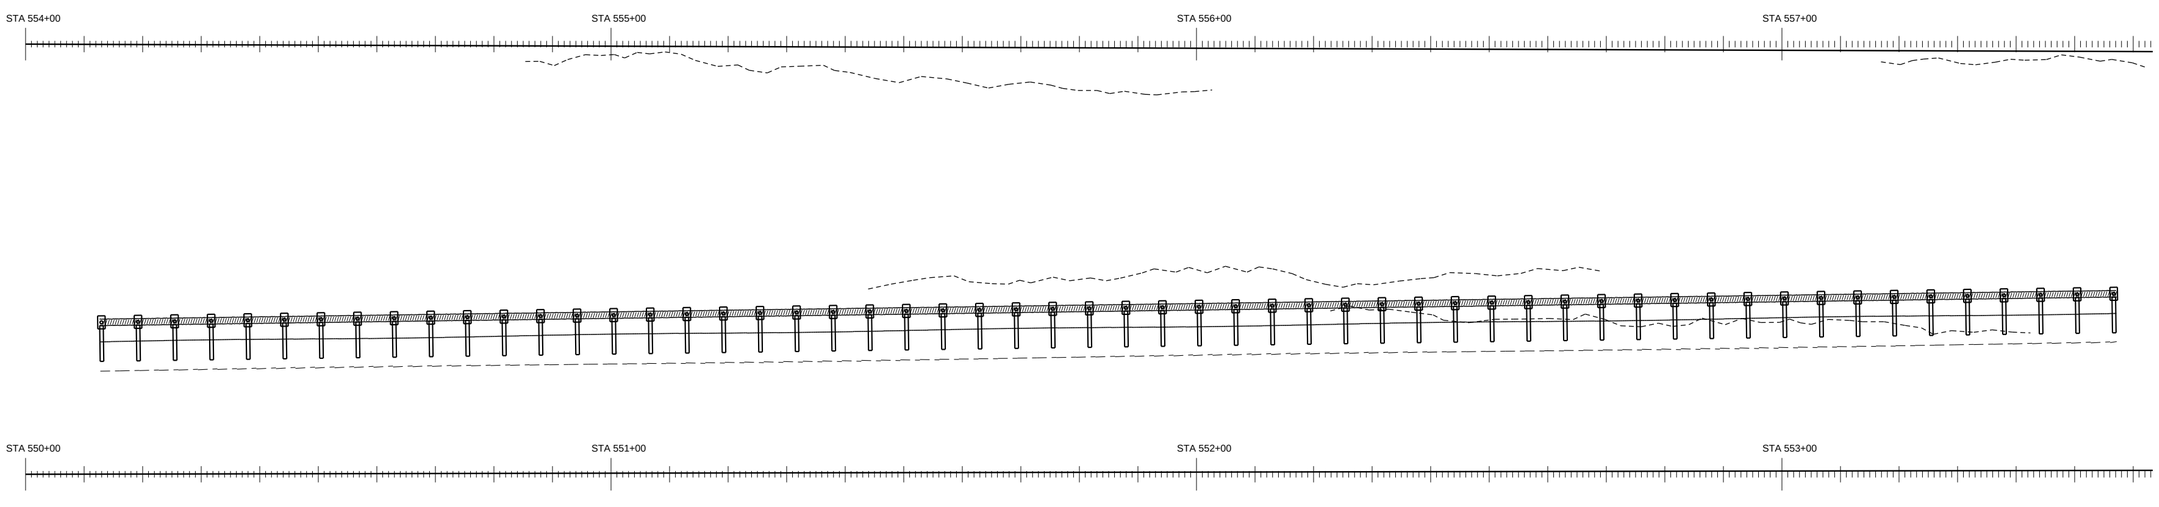


PAY ITEM 536-1-1 GUARDRAIL ROADWAY (TL-3)

PAY ITEM 536-85-24 END TREATMENT

GUARANTEED FENCE CORP

FIN. PROJ. ID 441234-1-52-01

SHEET 31 OF 120

SHEET NO. 131

ROADWAY PLAN SCALE: 1" = 20'




PAY ITEM 536-1-1 GUARDRAIL ROADWAY (TL-3)

PAY ITEM 536-85-24 END TREATMENT

GUARANTEED FENCE CORP

FIN. PROJ. ID 441234-1-52-01

SHEET 32 OF 120

SHEET NO. 132

ROADWAY PLAN SCALE: 1" = 20'

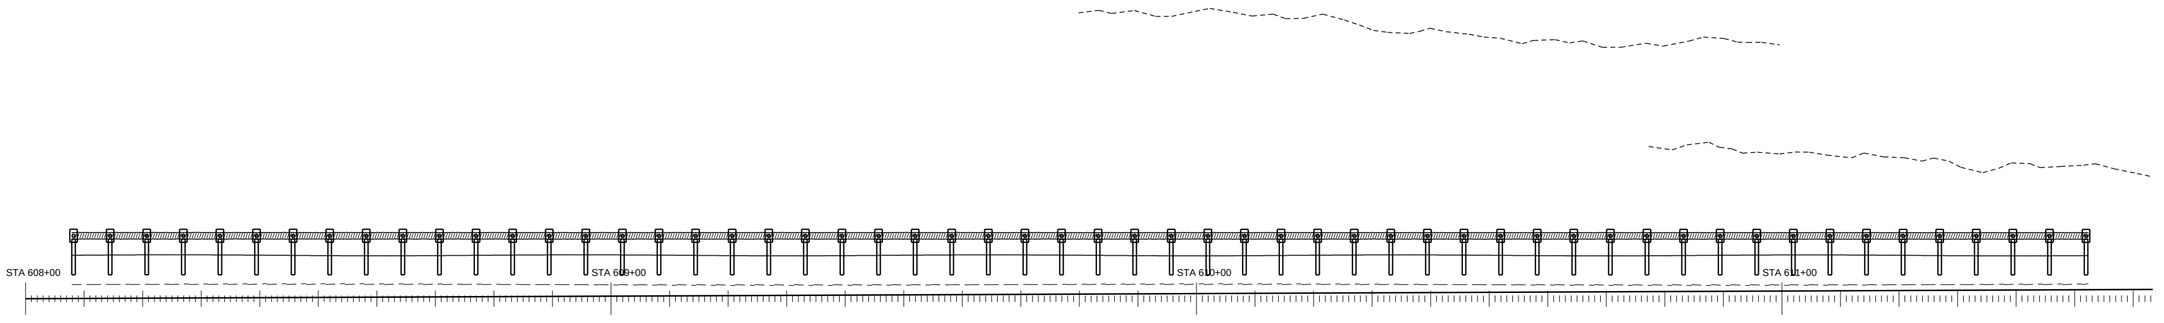


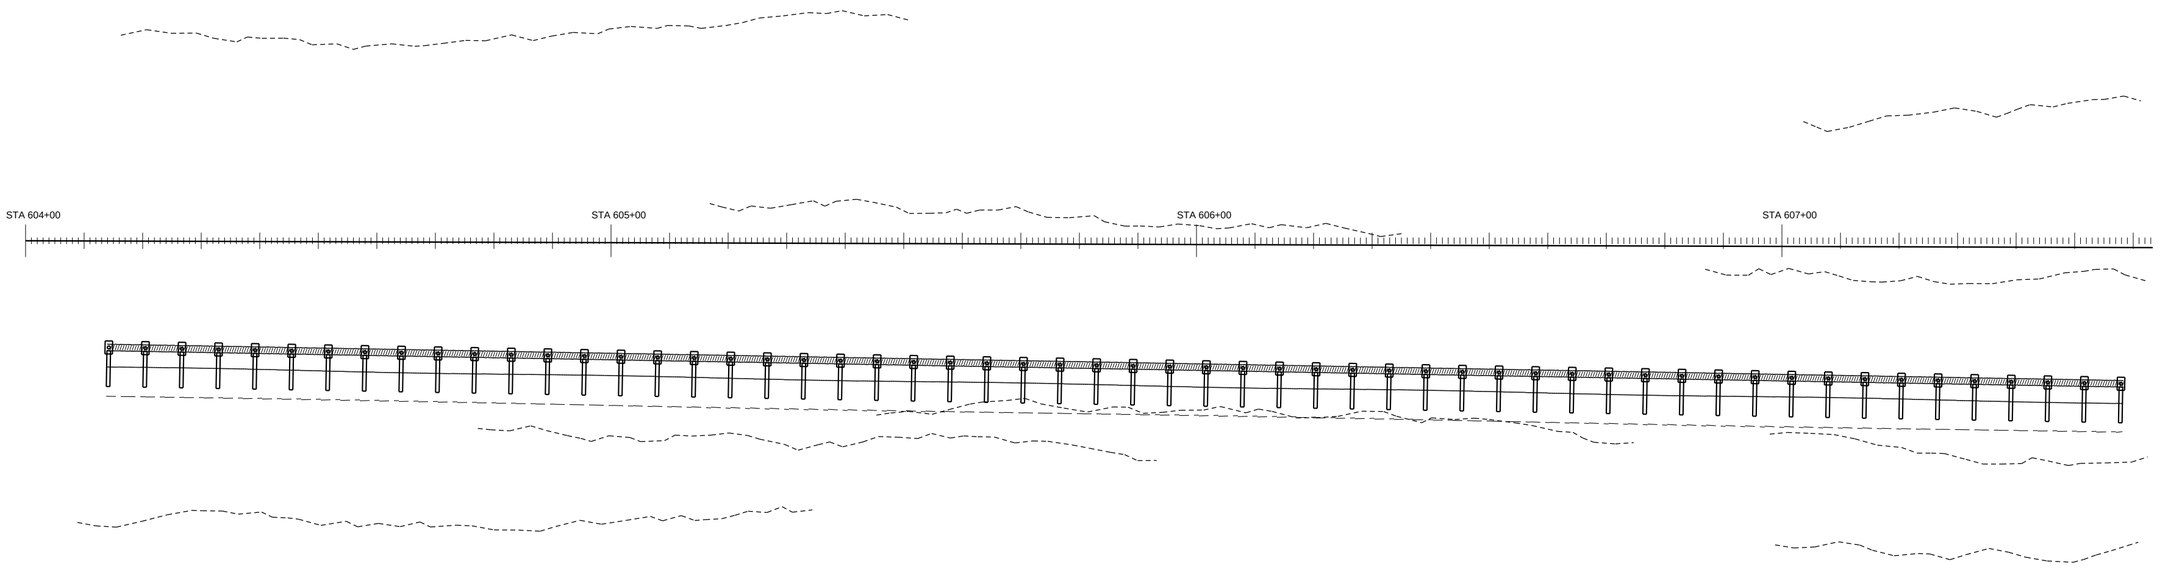


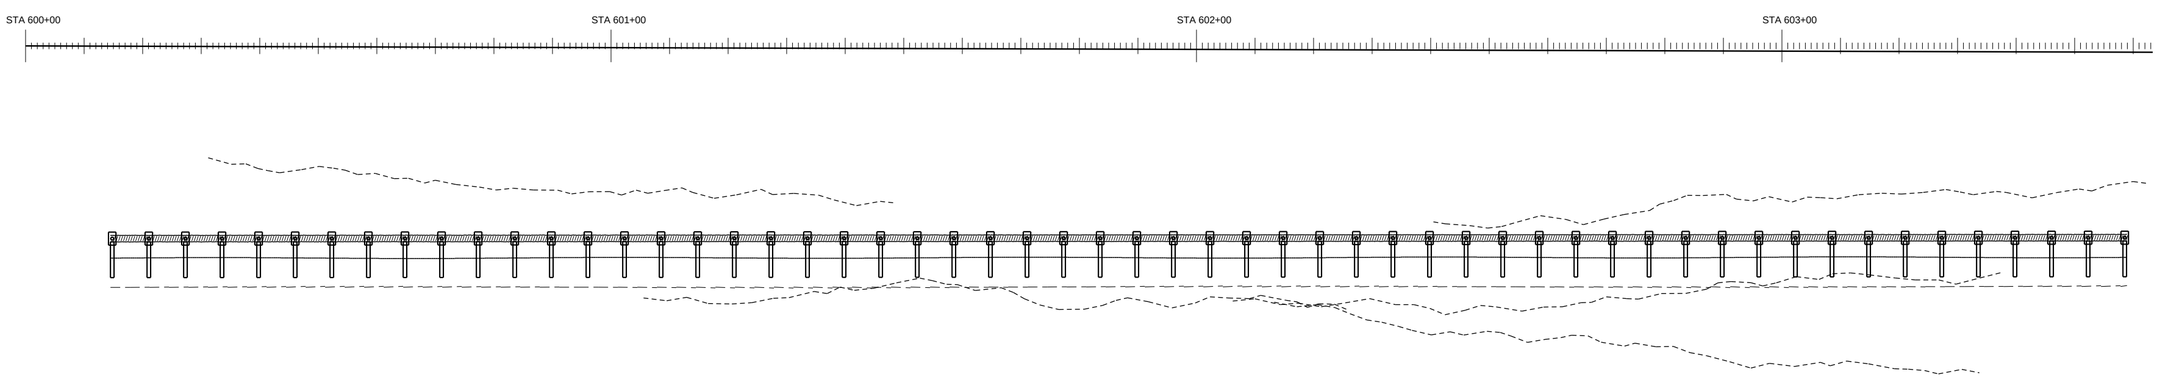


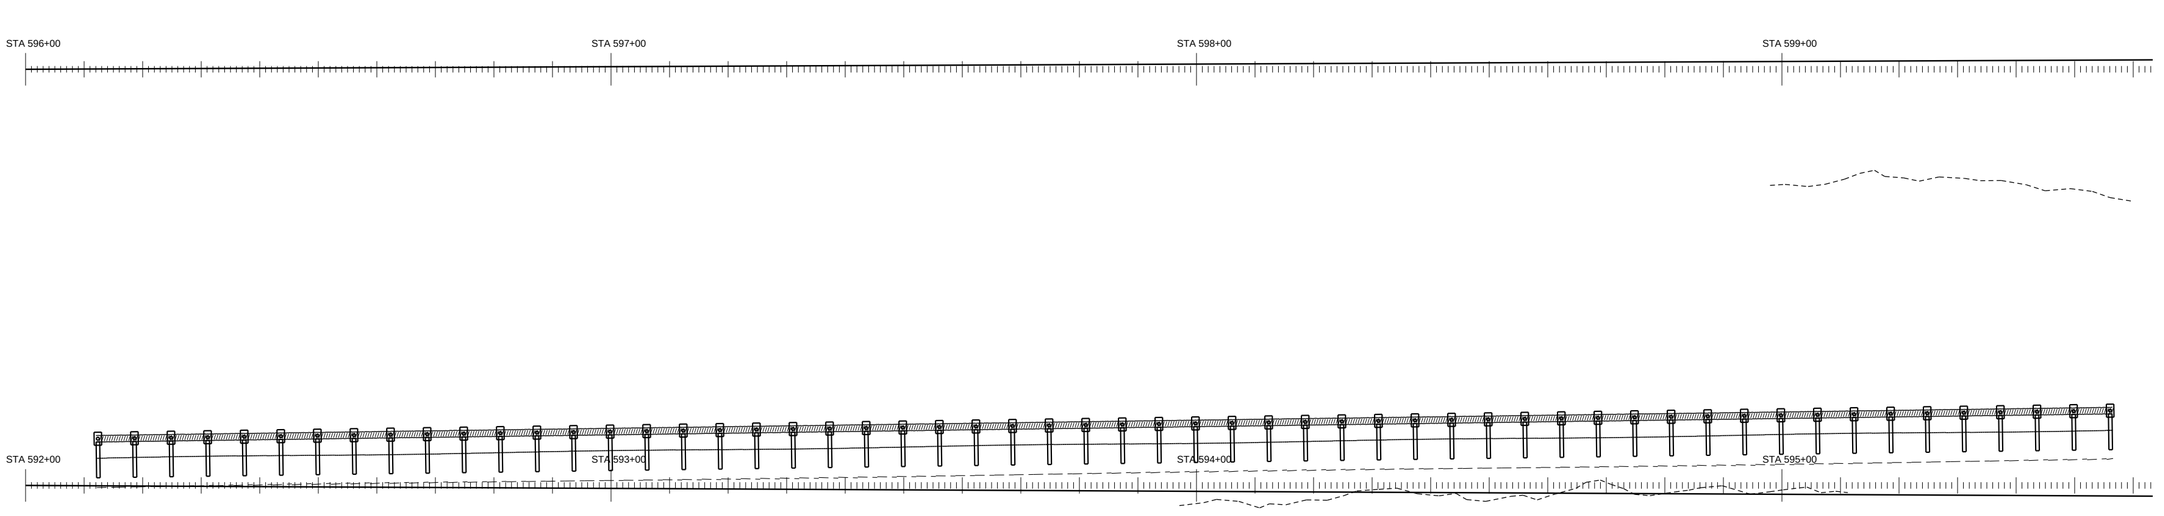


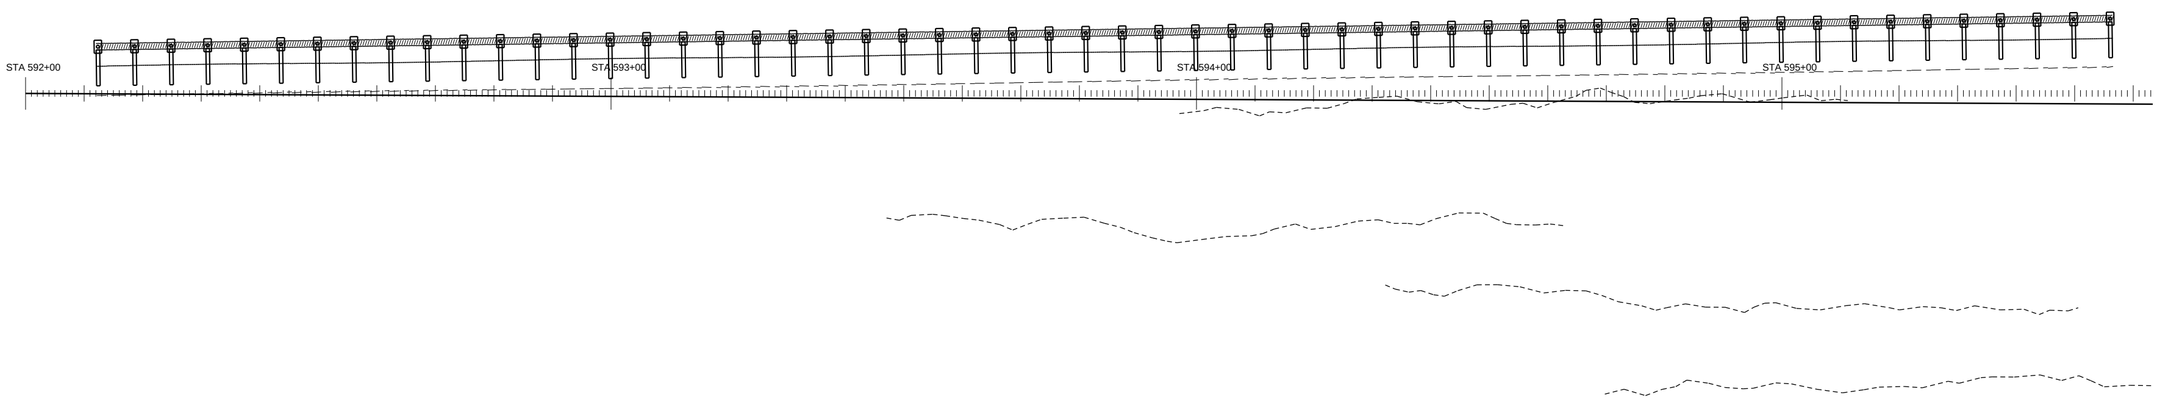


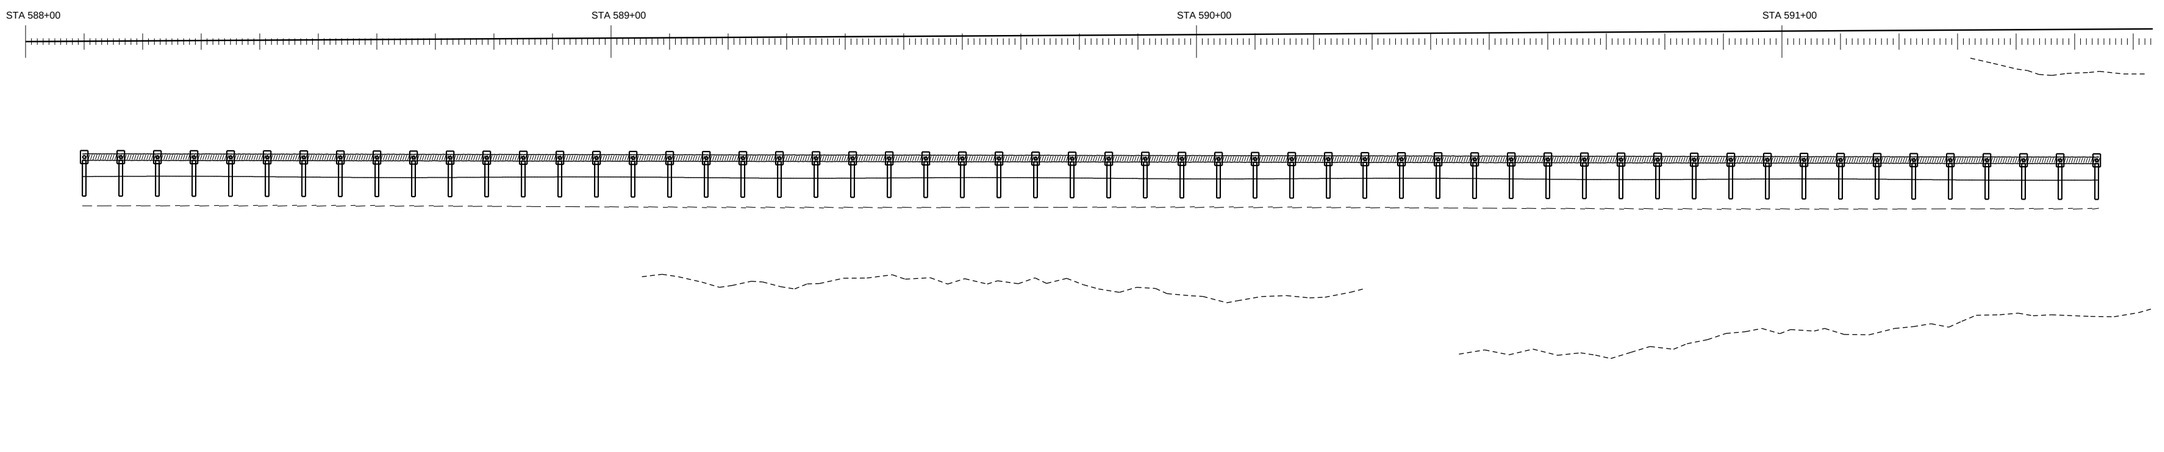


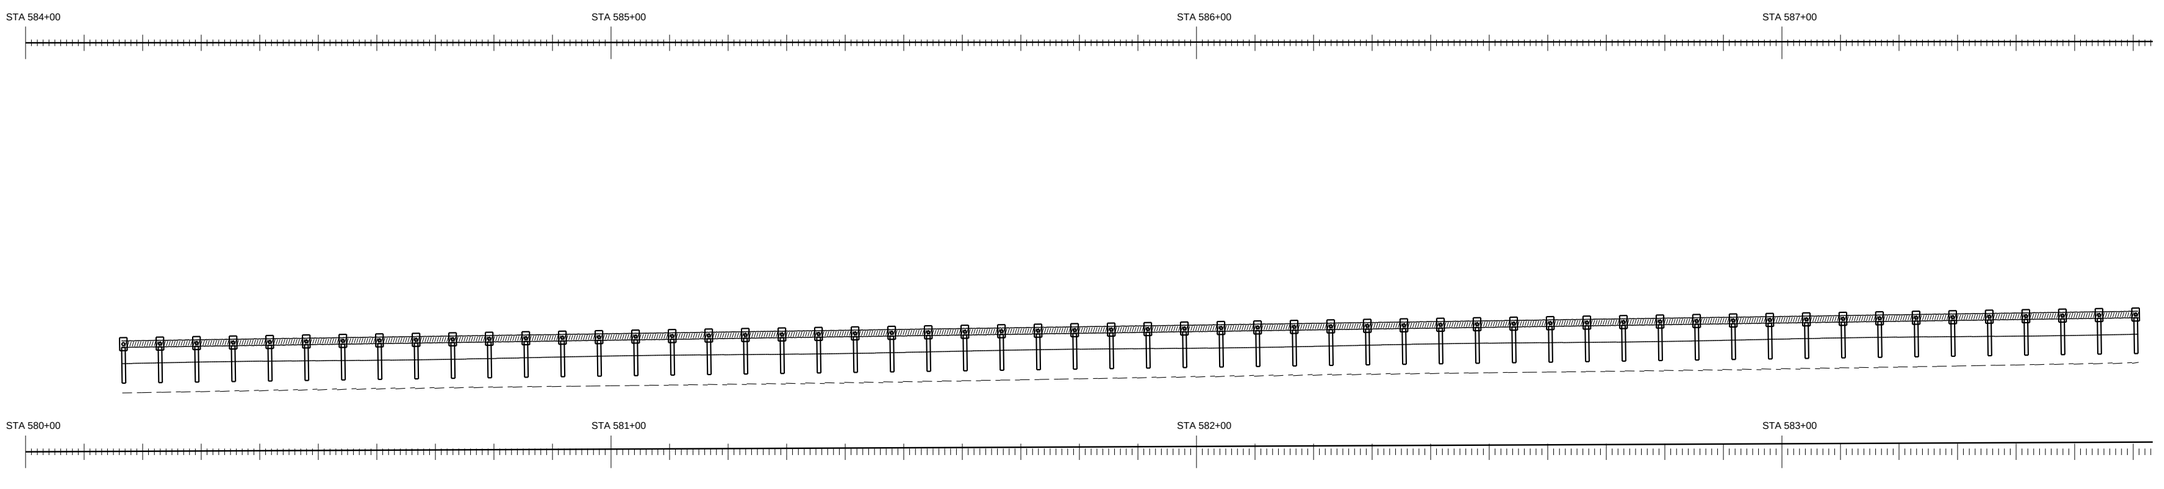





PAY ITEM 536-1-1 GUARDRAIL ROADWAY (TL-3)

PAY ITEM 536-85-24 END TREATMENT

GUARANTEED FENCE CORP

FIN. PROJ. ID 441234-1-52-01

SHEET 33 OF 120

SHEET NO. 133

ROADWAY PLAN SCALE: 1" = 20'

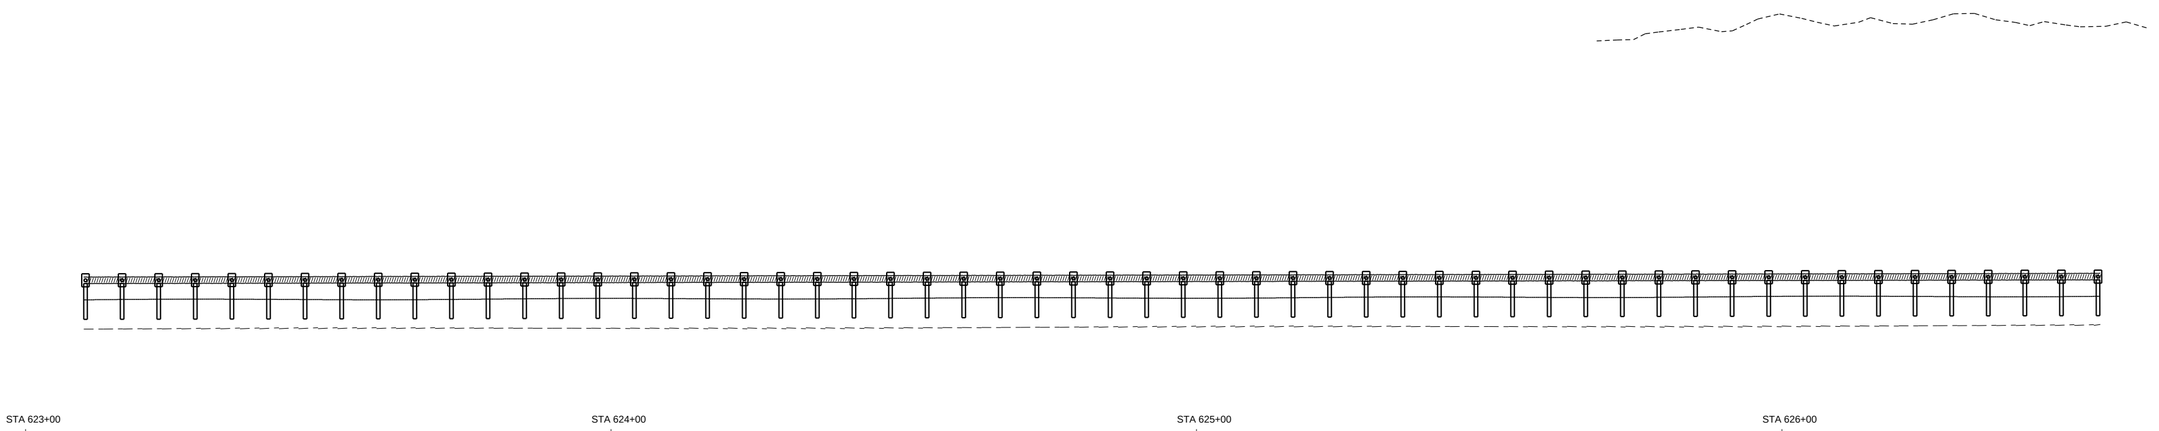


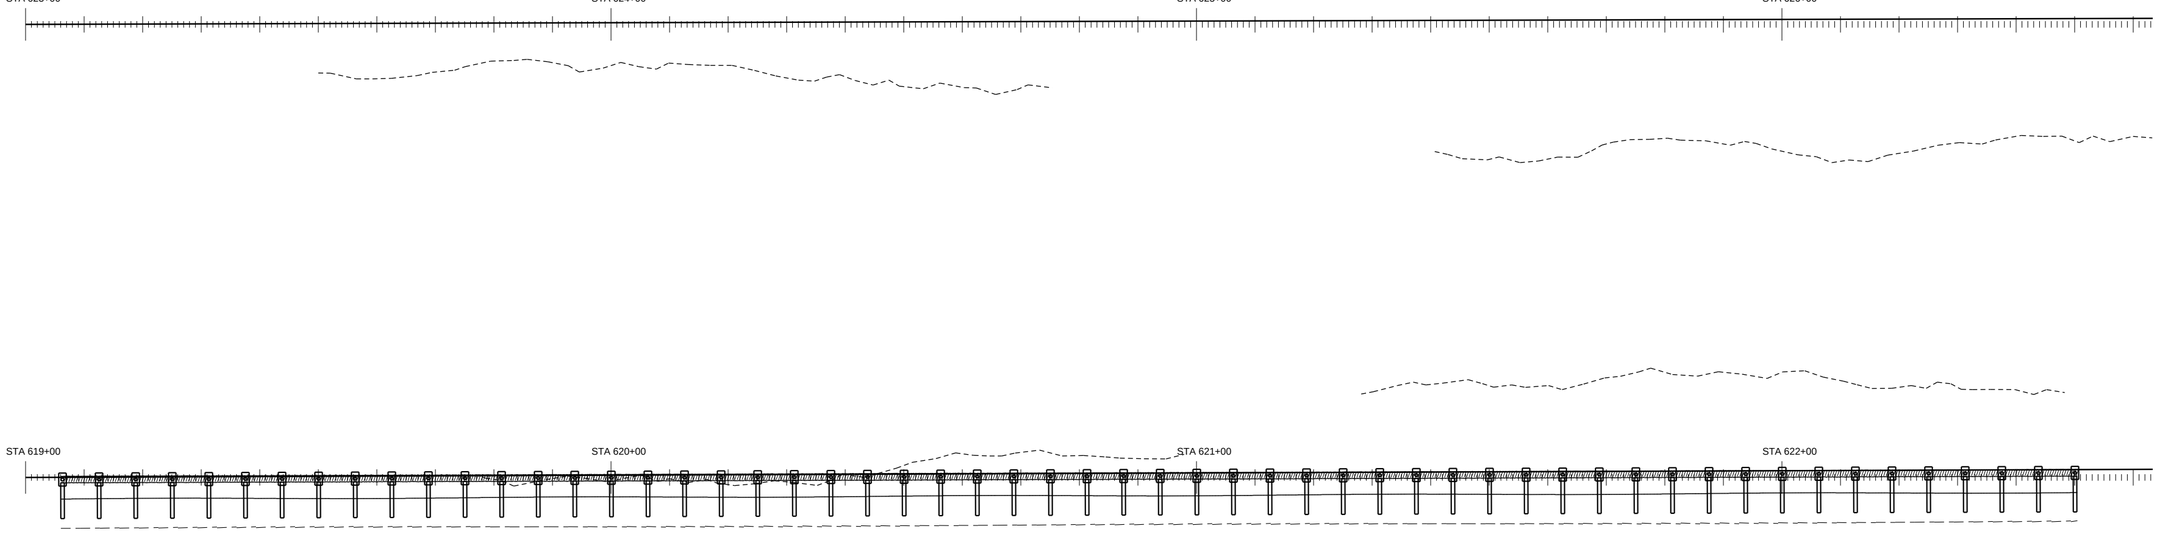


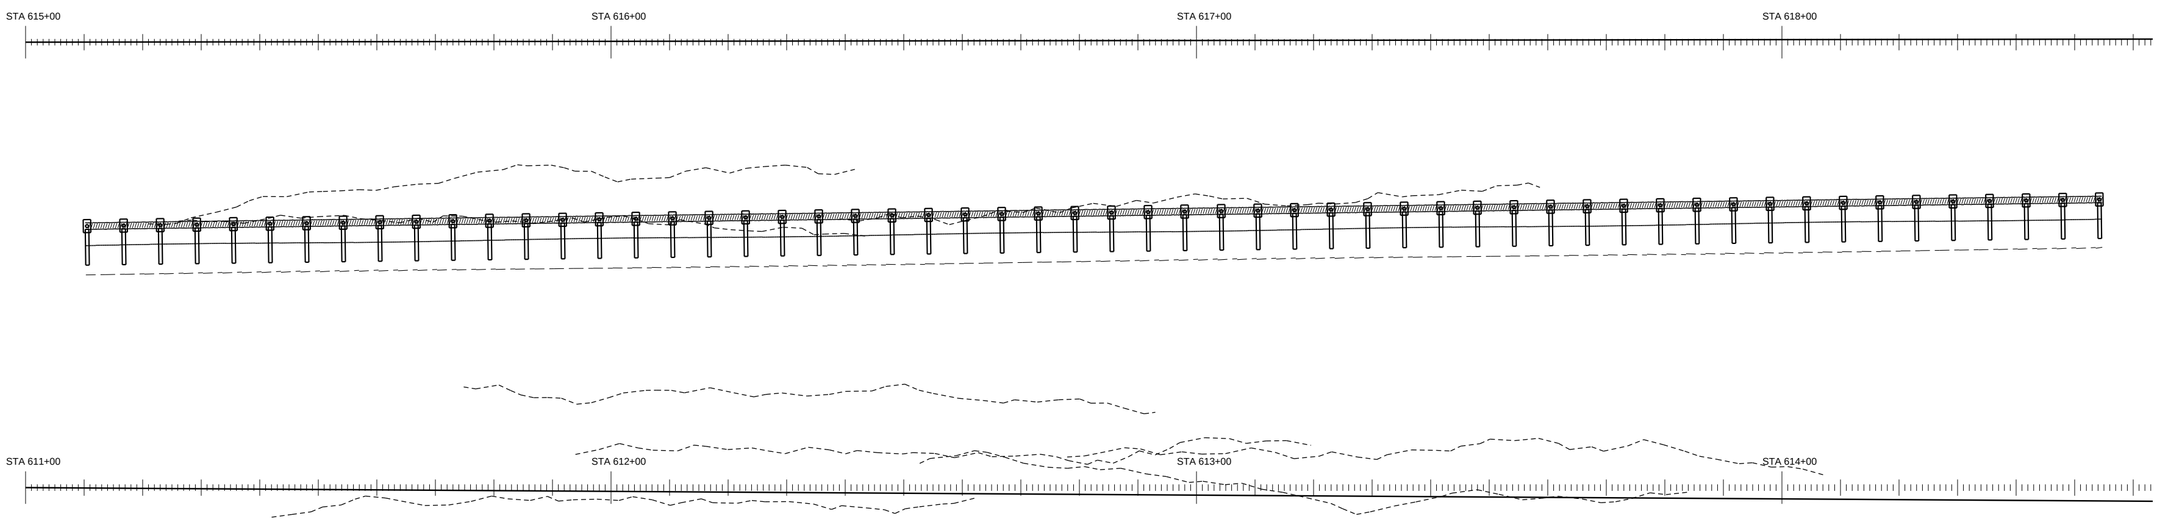


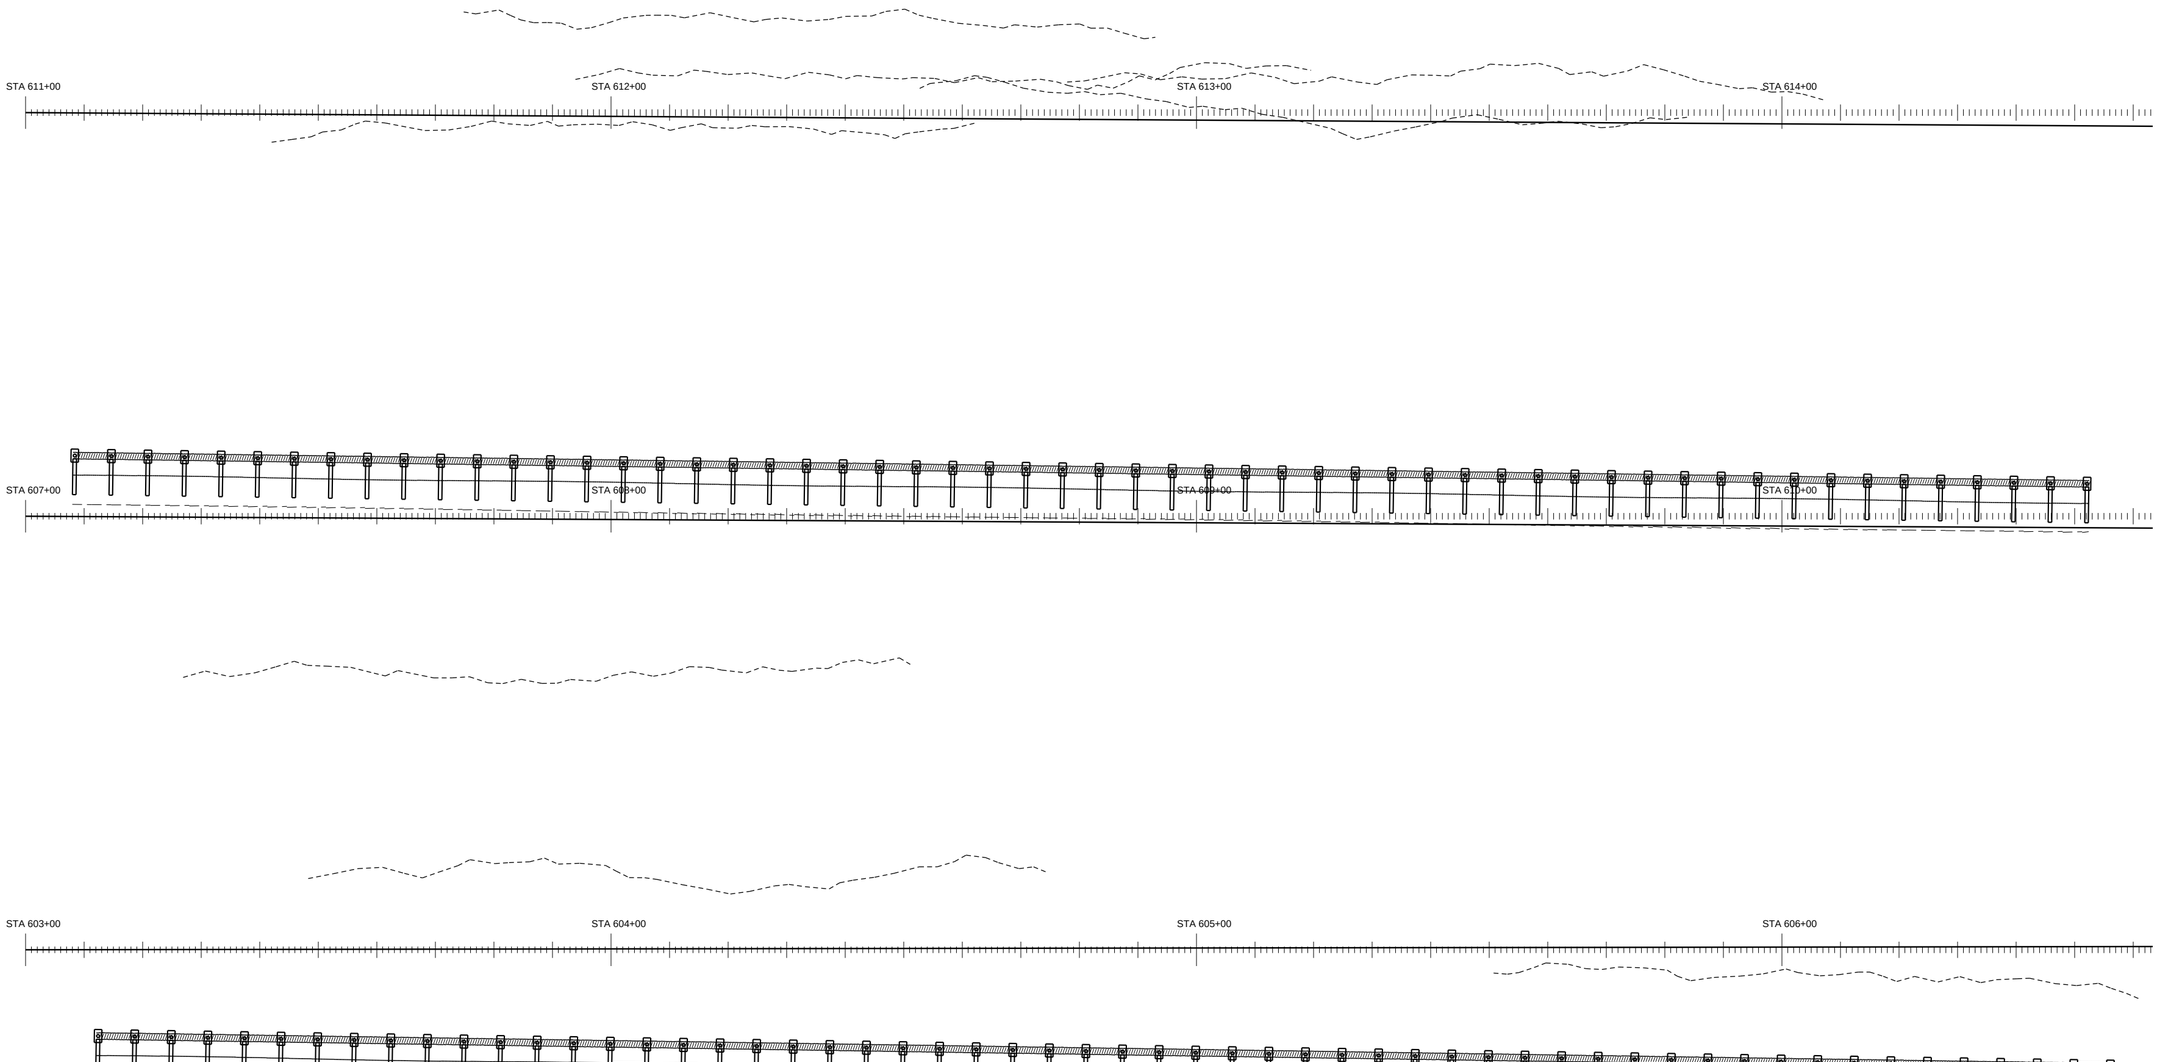














PAY ITEM 536-1-1 GUARDRAIL ROADWAY (TL-3)

PAY ITEM 536-85-24 END TREATMENT

GUARANTEED FENCE CORP

FIN. PROJ. ID 441234-1-52-01

SHEET 34 OF 120

SHEET NO. 134

ROADWAY PLAN SCALE: 1" = 20'

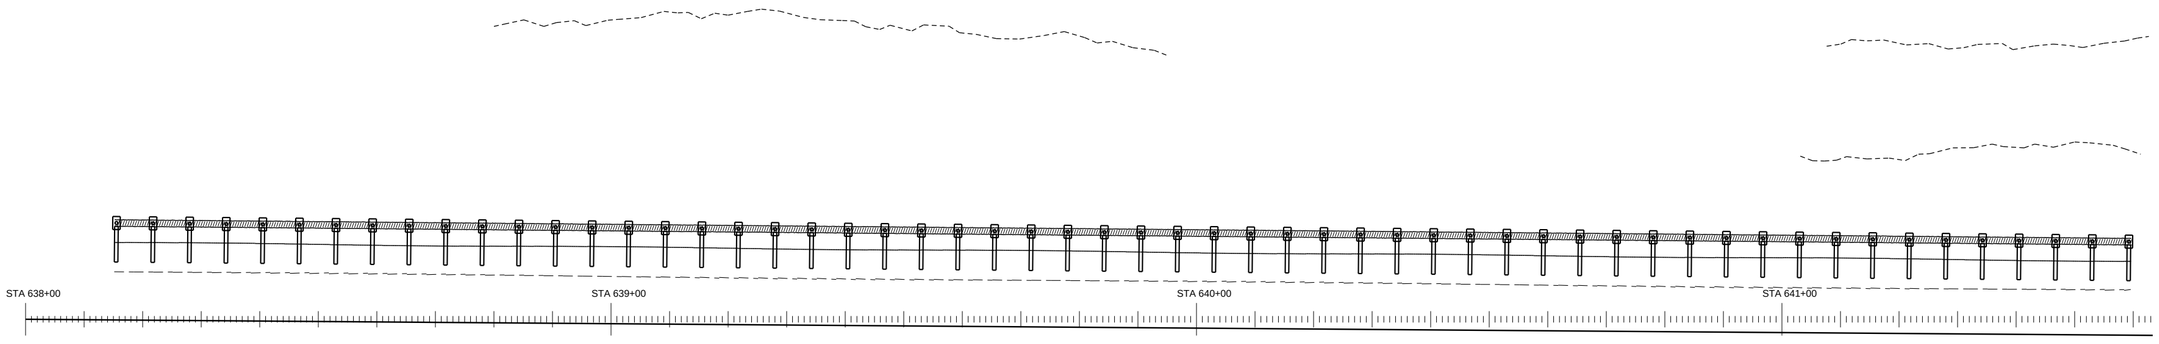


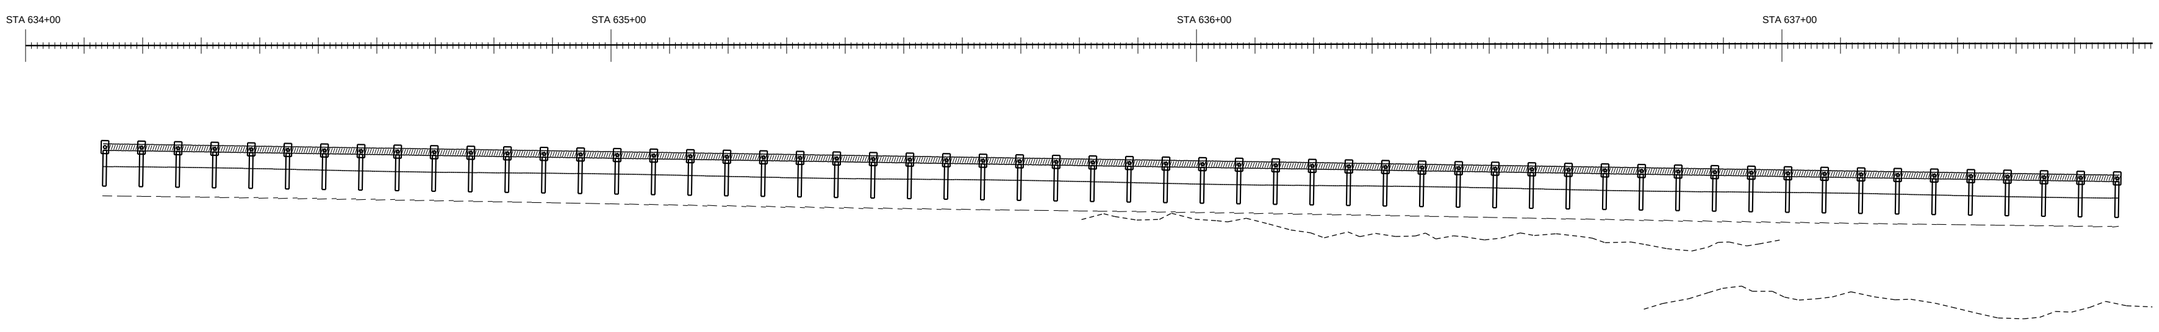


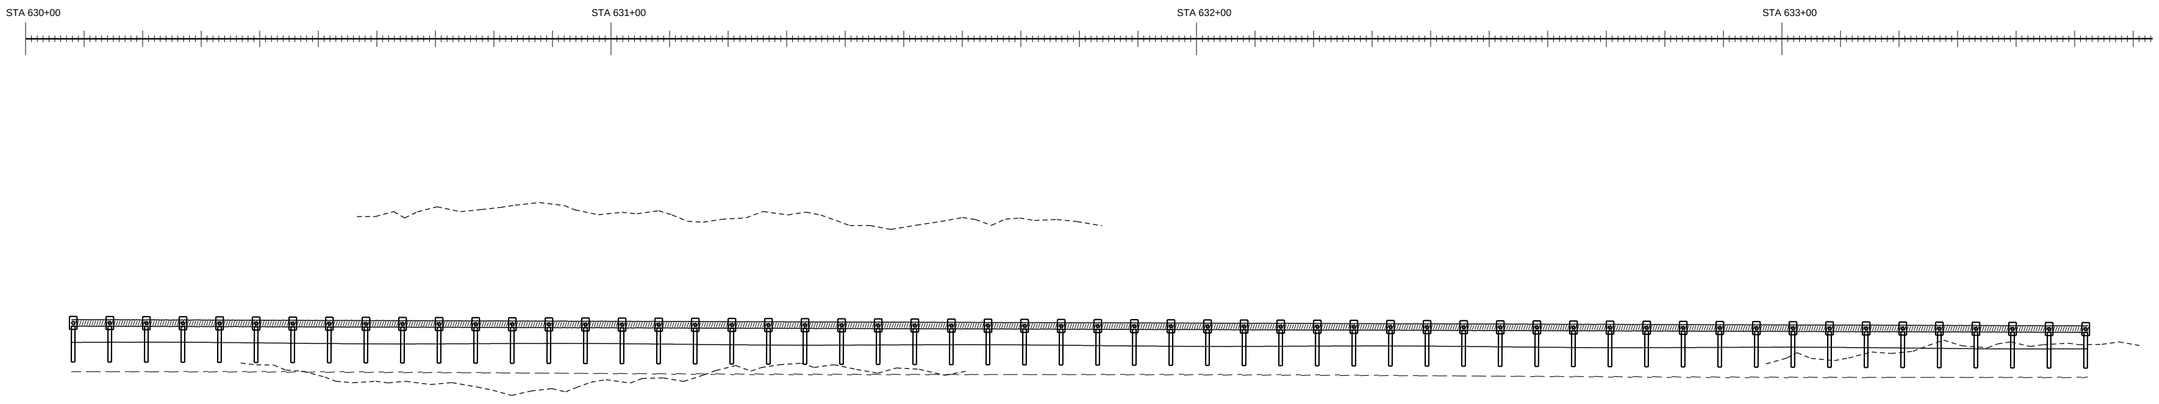


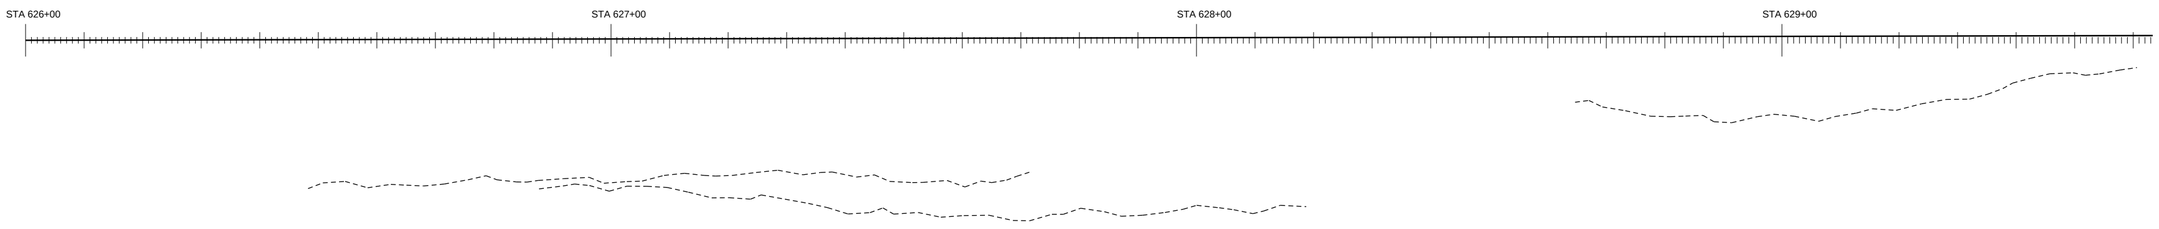


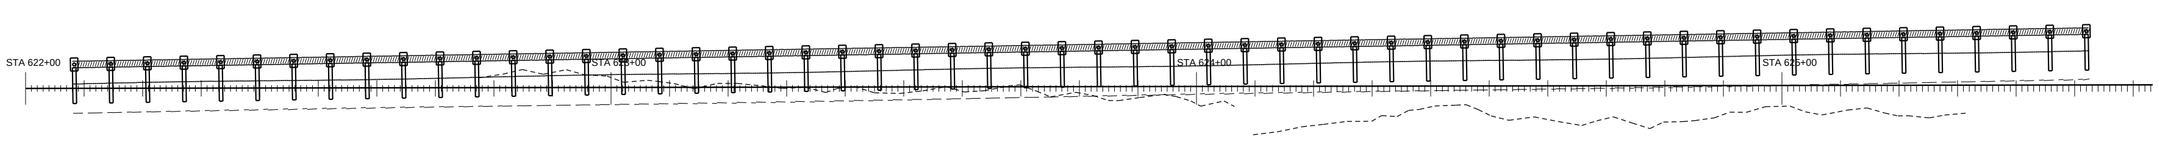


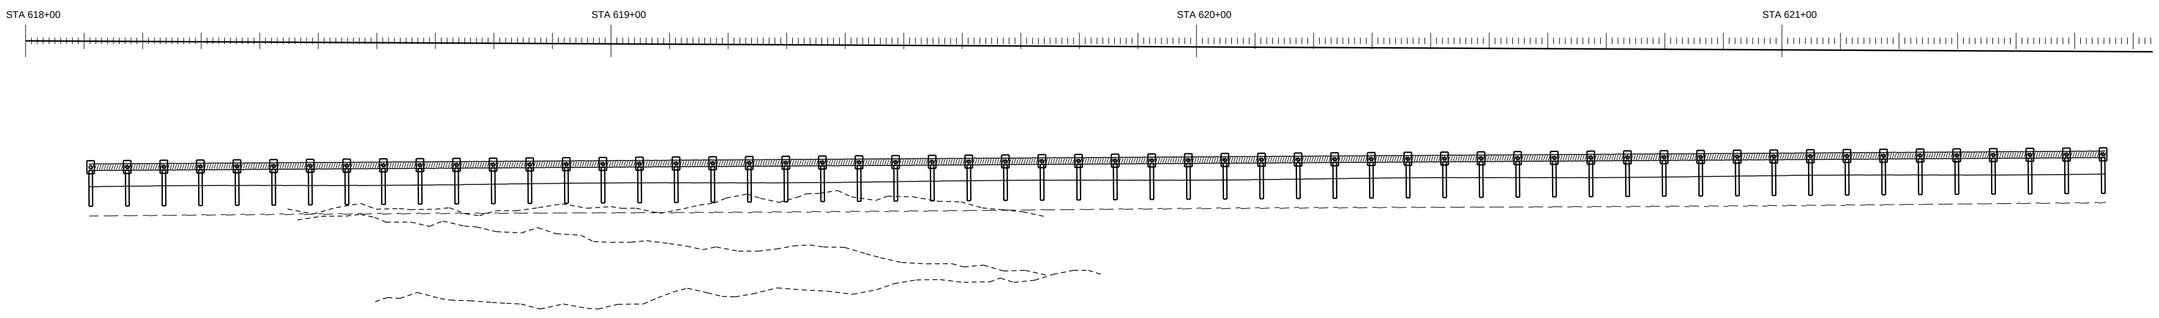


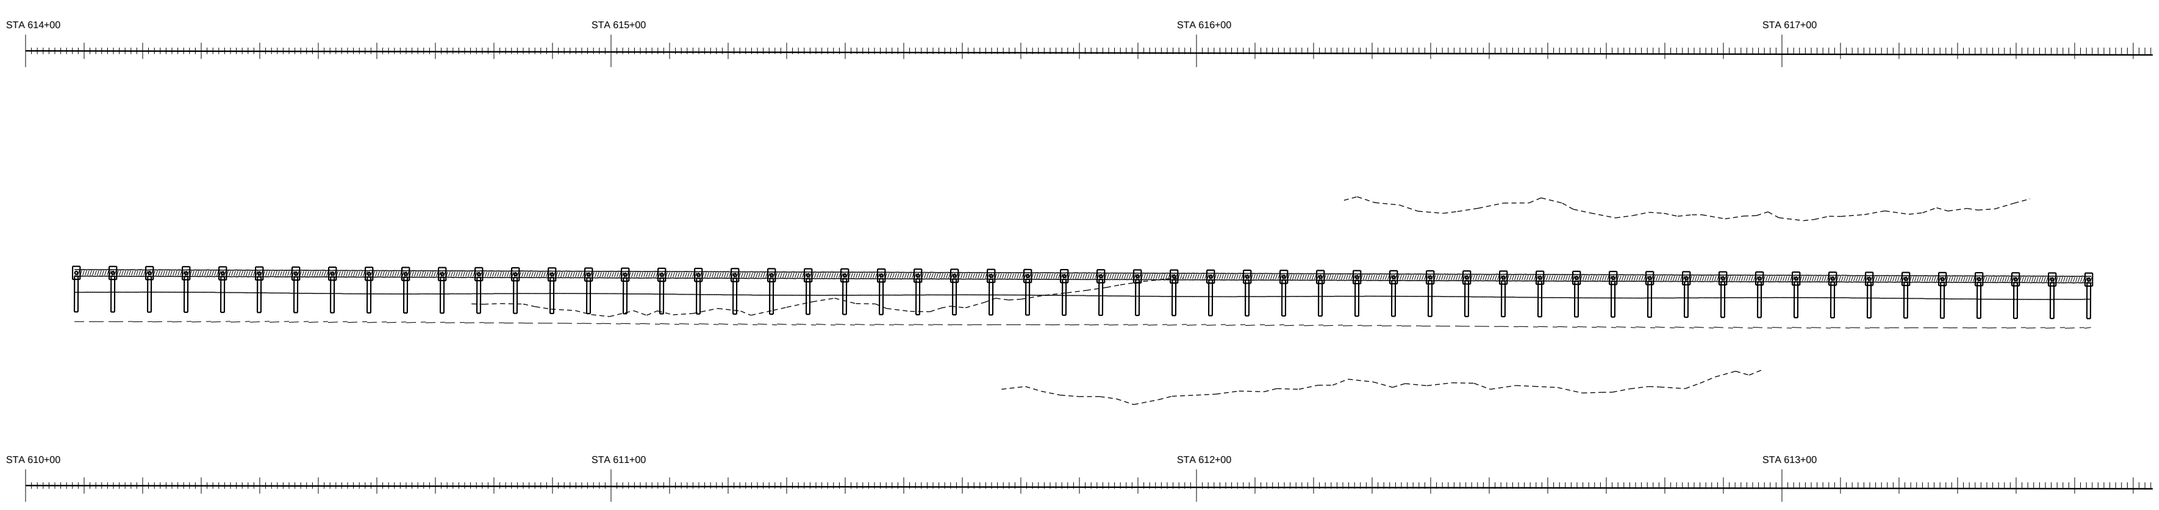


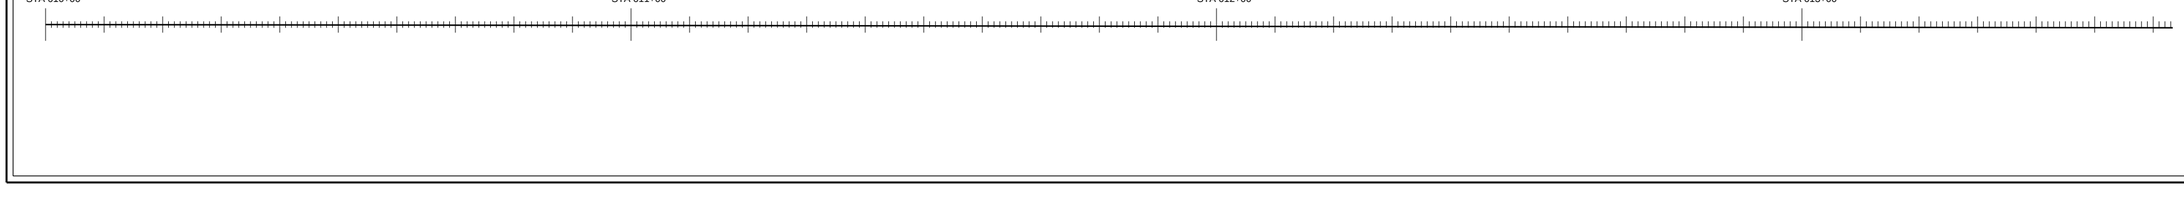


PAY ITEM 536-1-1 GUARDRAIL ROADWAY (TL-3)

PAY ITEM 536-85-24 END TREATMENT

GUARANTEED FENCE CORP

FIN. PROJ. ID 441234-1-52-01

SHEET 35 OF 120

SHEET NO. 135

ROADWAY PLAN SCALE: 1" = 20'

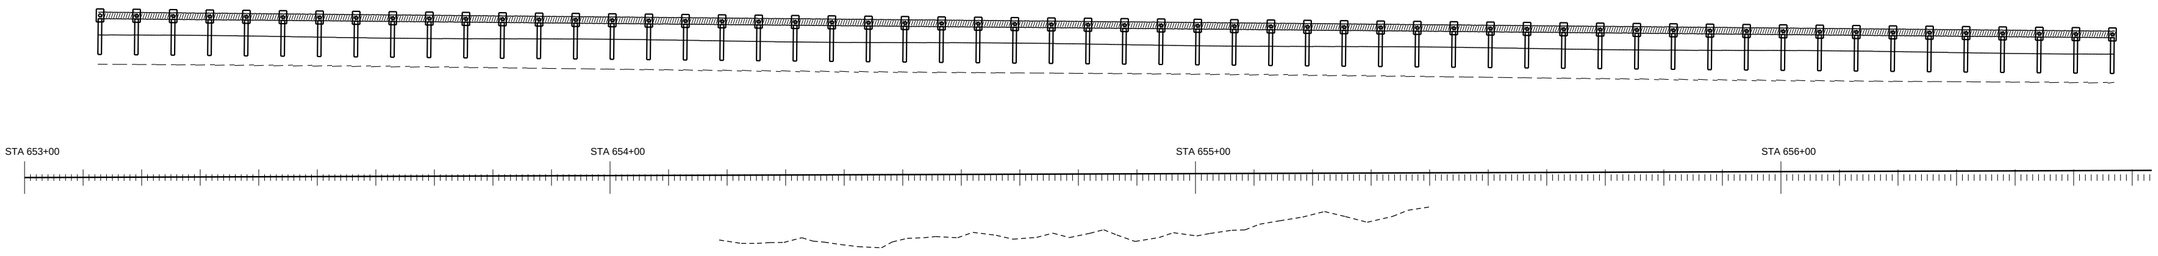


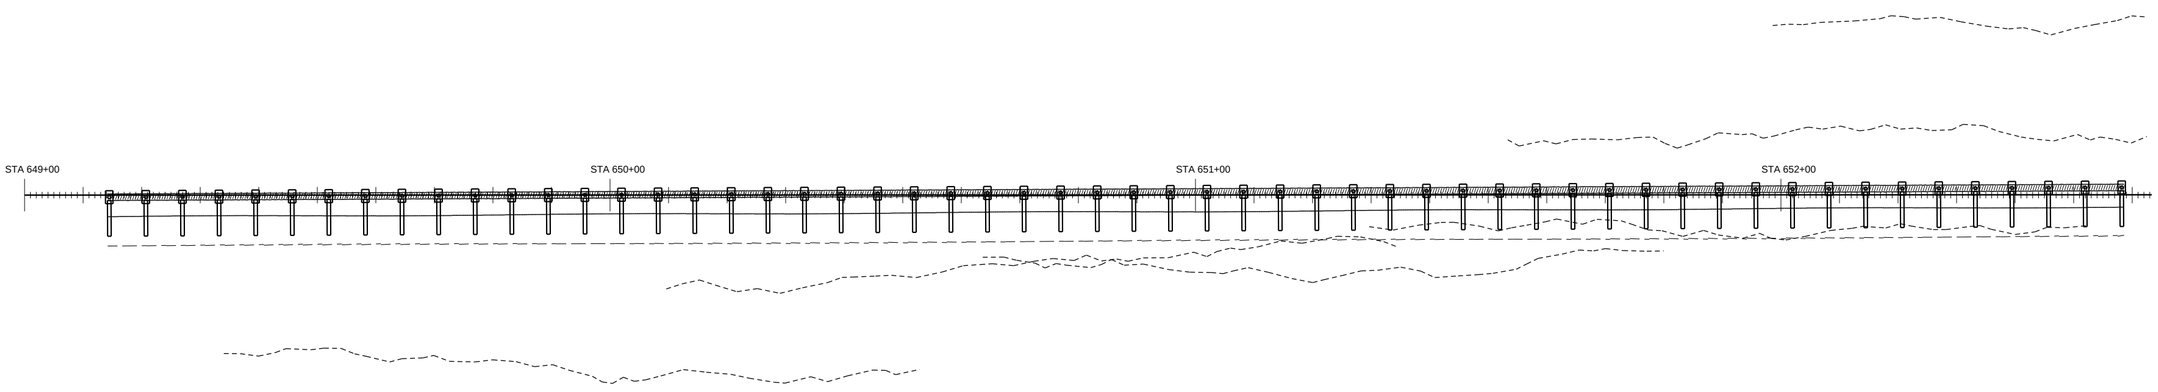


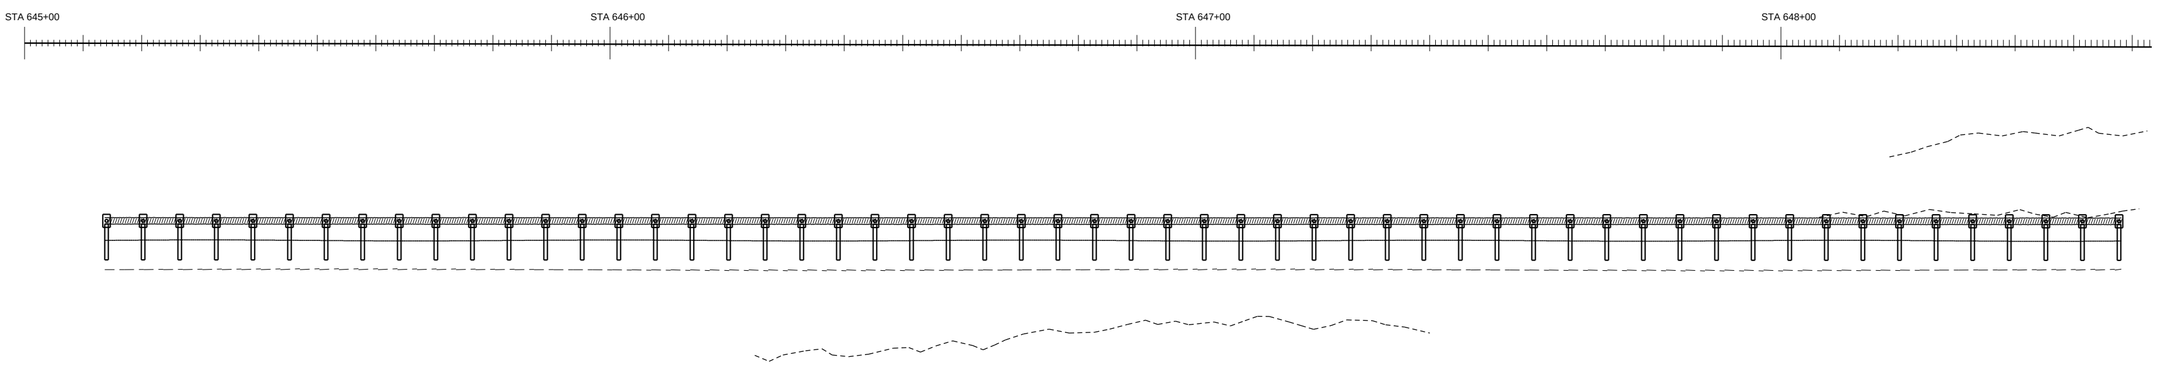


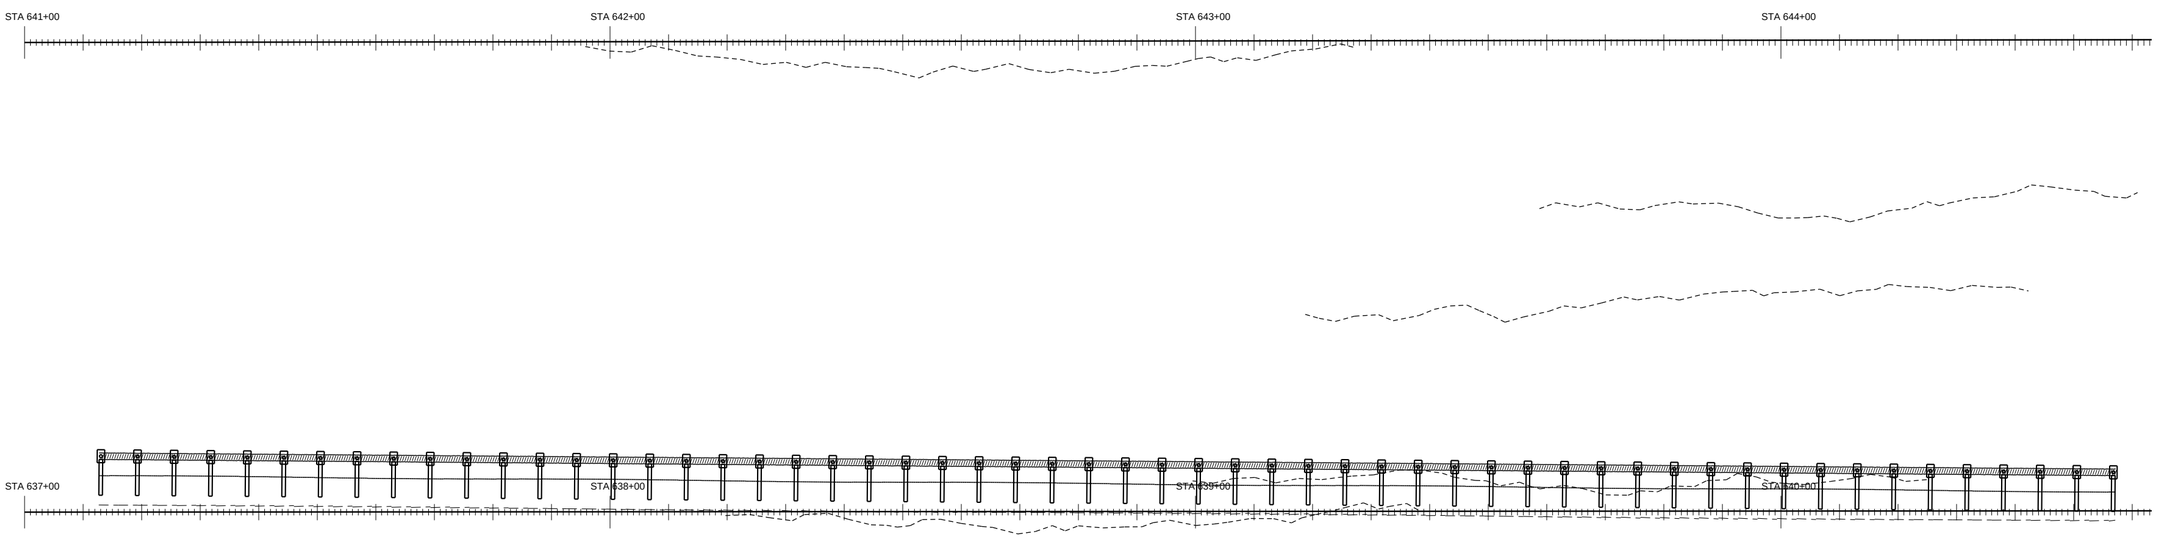


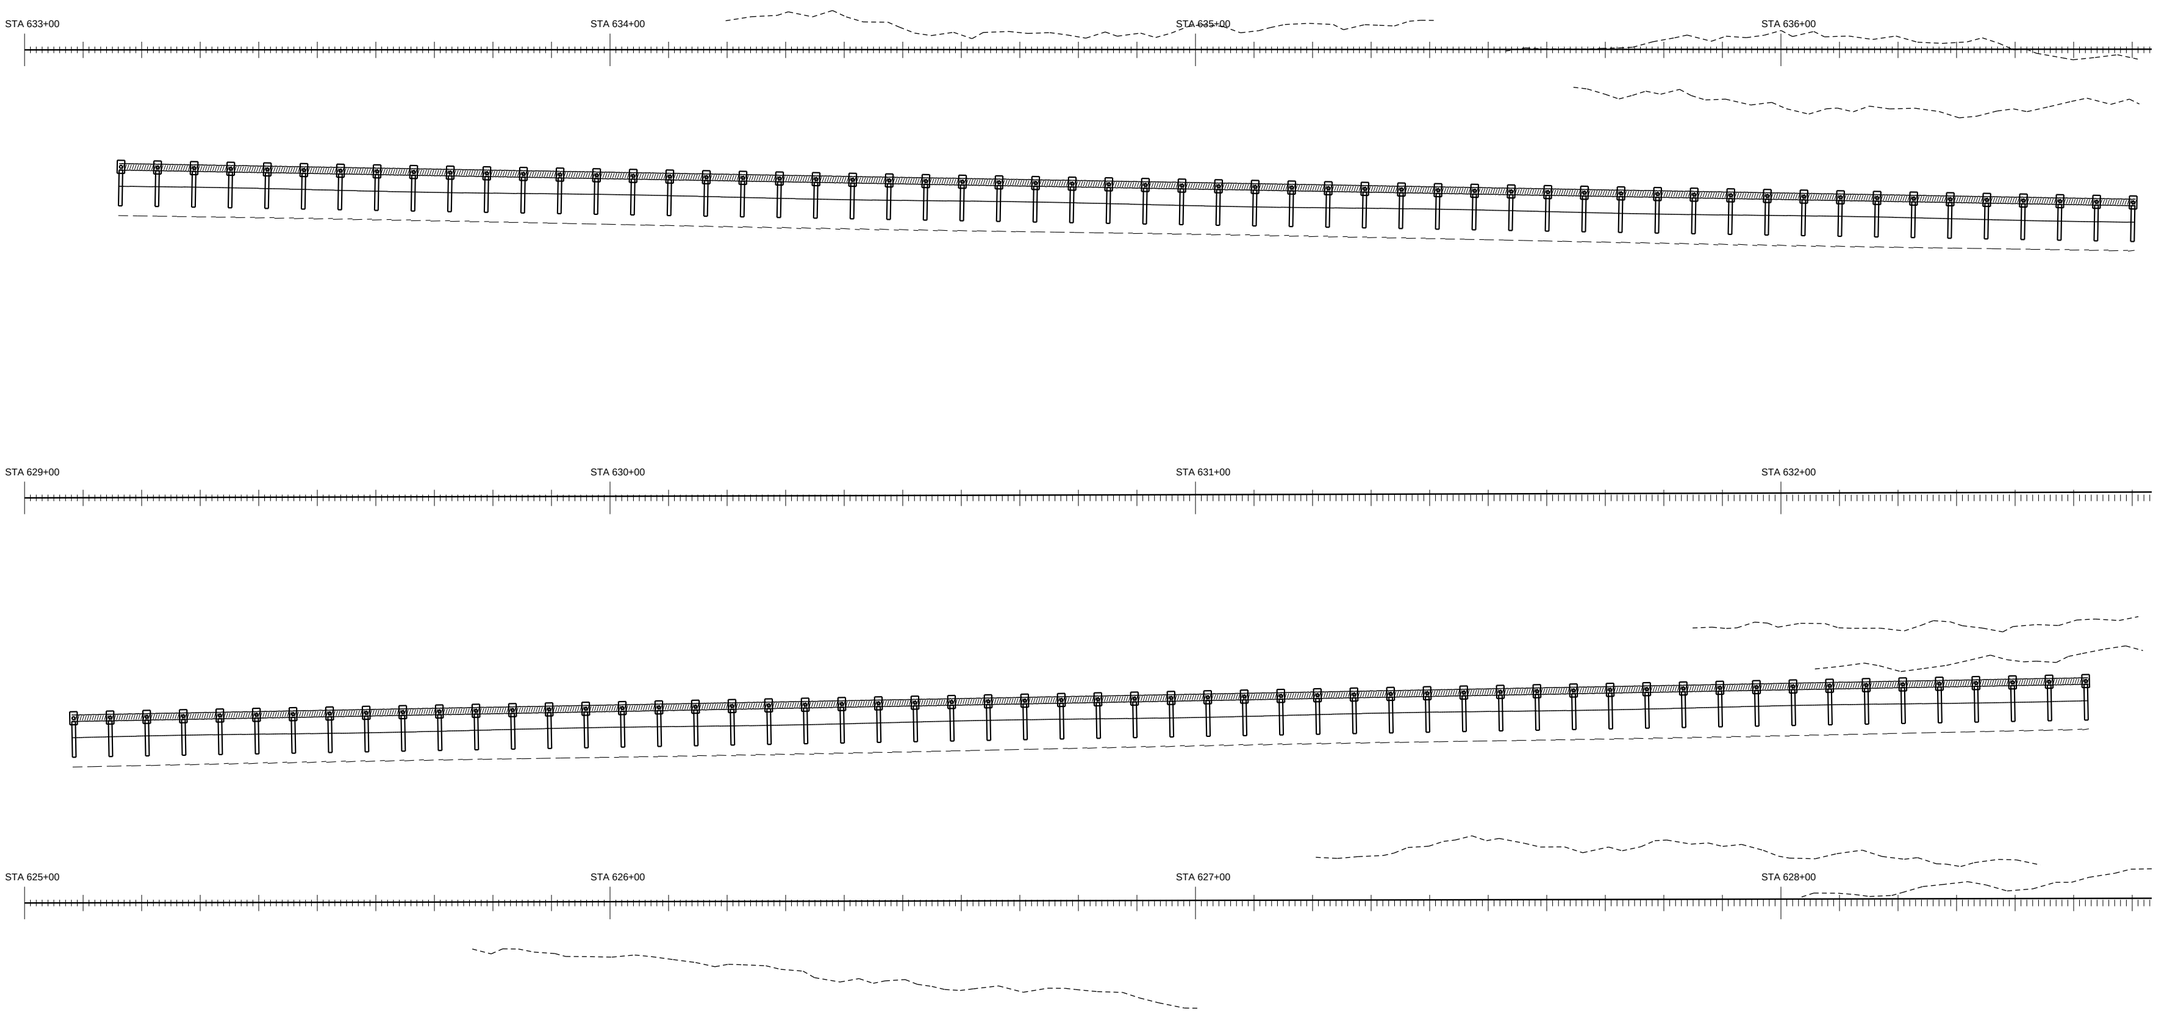





PAY ITEM 536-1-1 GUARDRAIL ROADWAY (TL-3)

PAY ITEM 536-85-24 END TREATMENT

GUARANTEED FENCE CORP

FIN. PROJ. ID 441234-1-52-01

SHEET 36 OF 120

SHEET NO. 136

ROADWAY PLAN SCALE: 1" = 20'

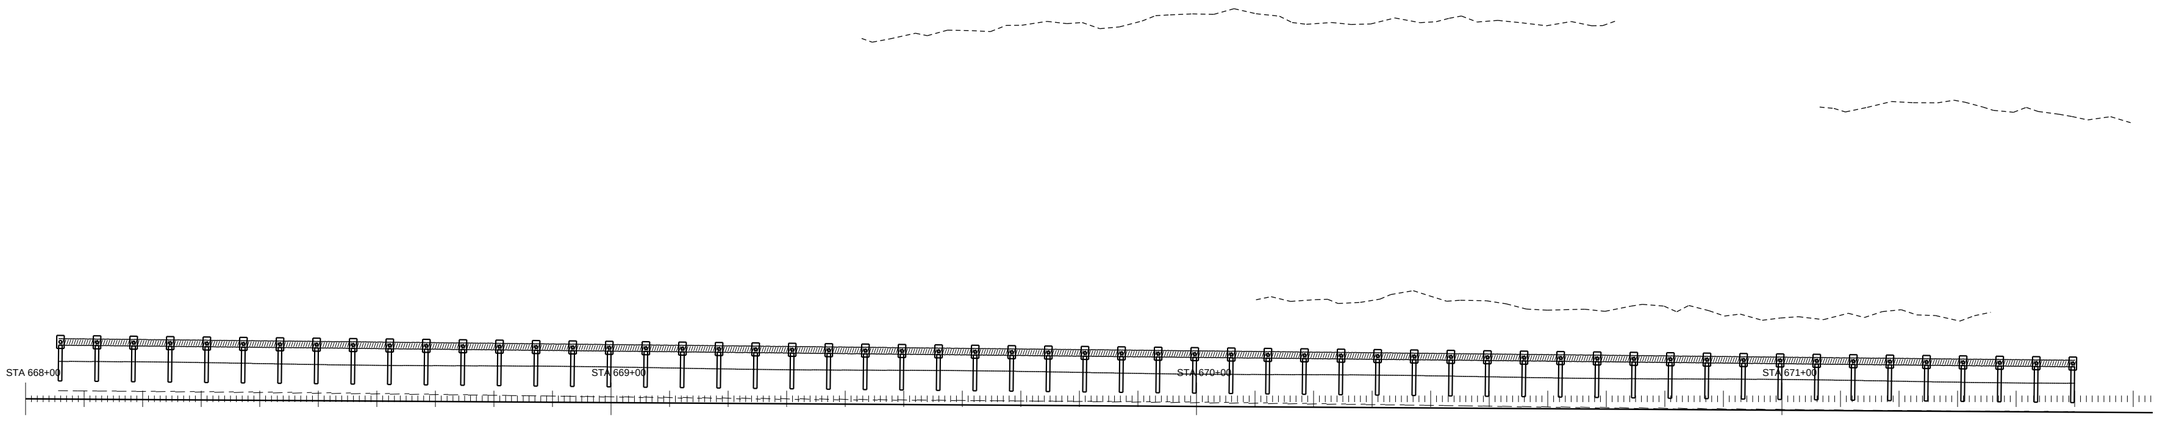


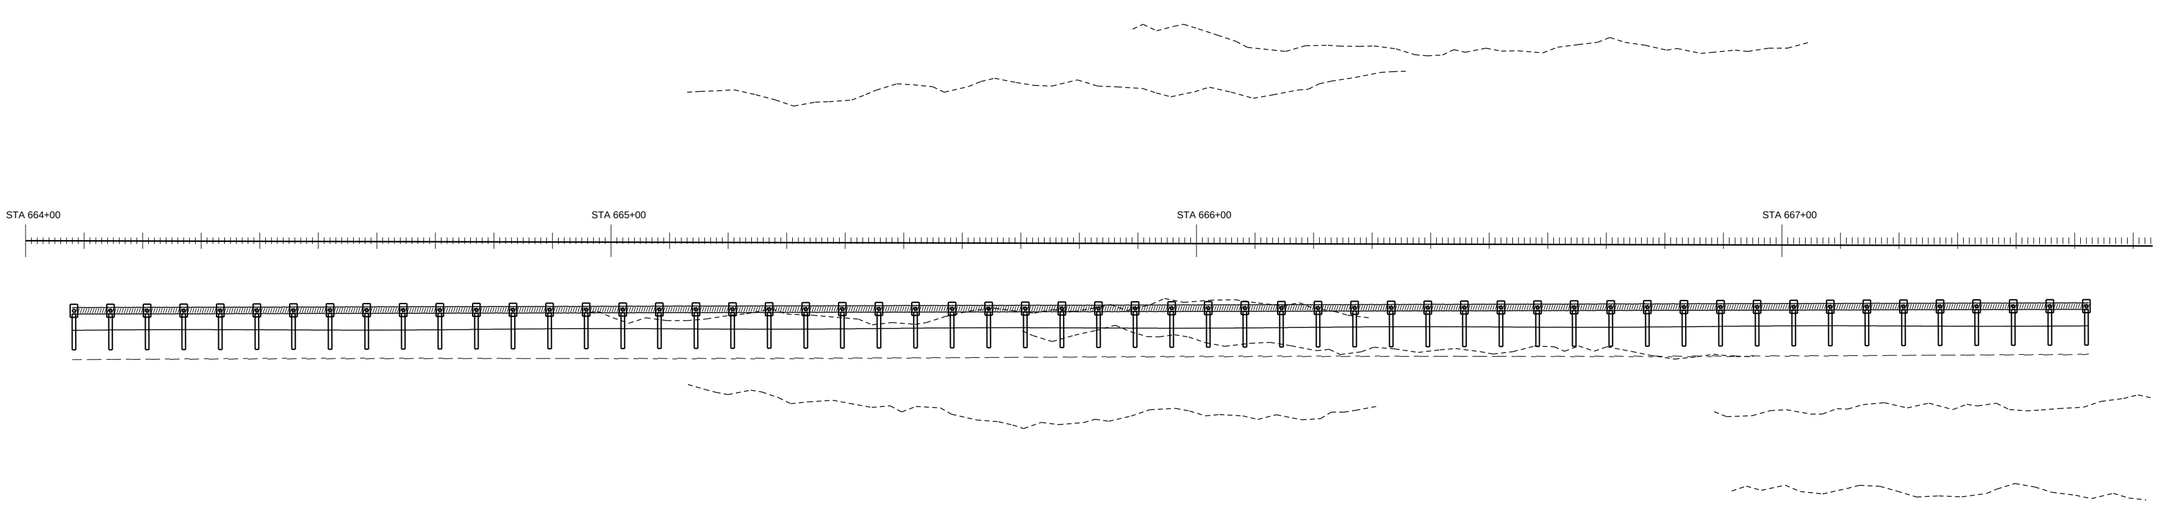


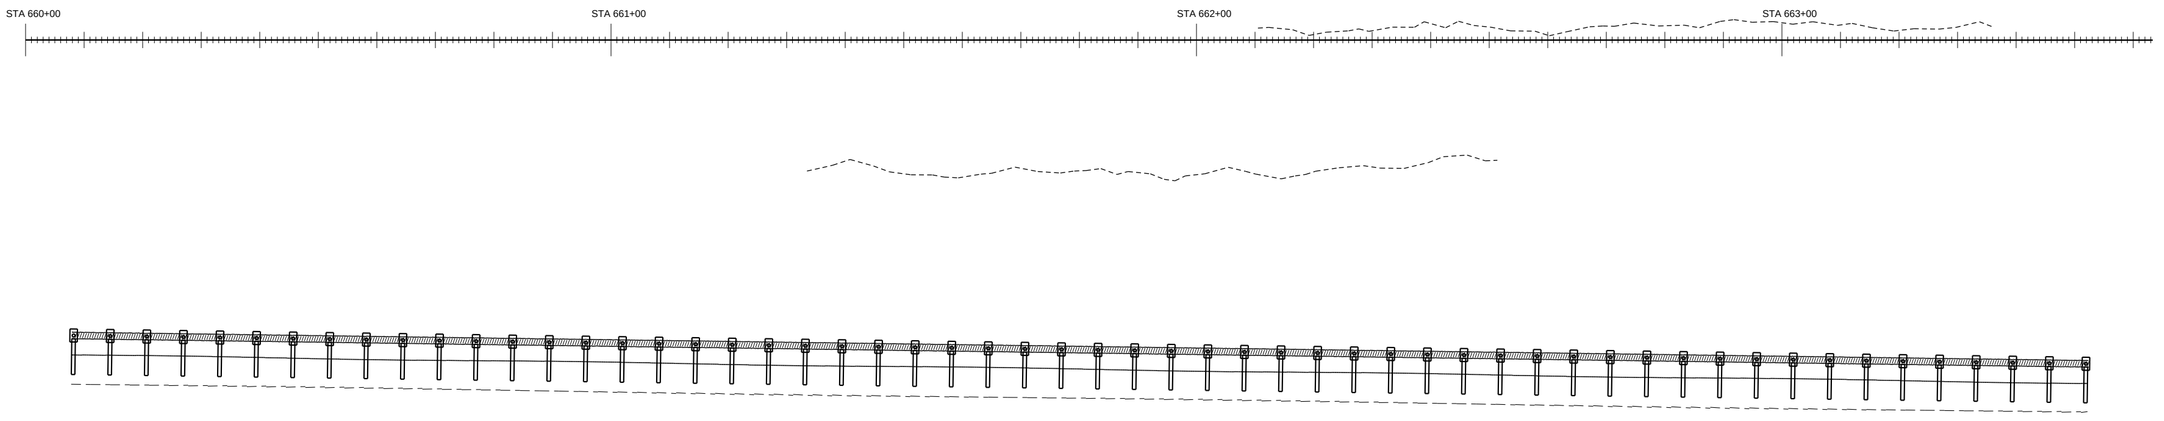


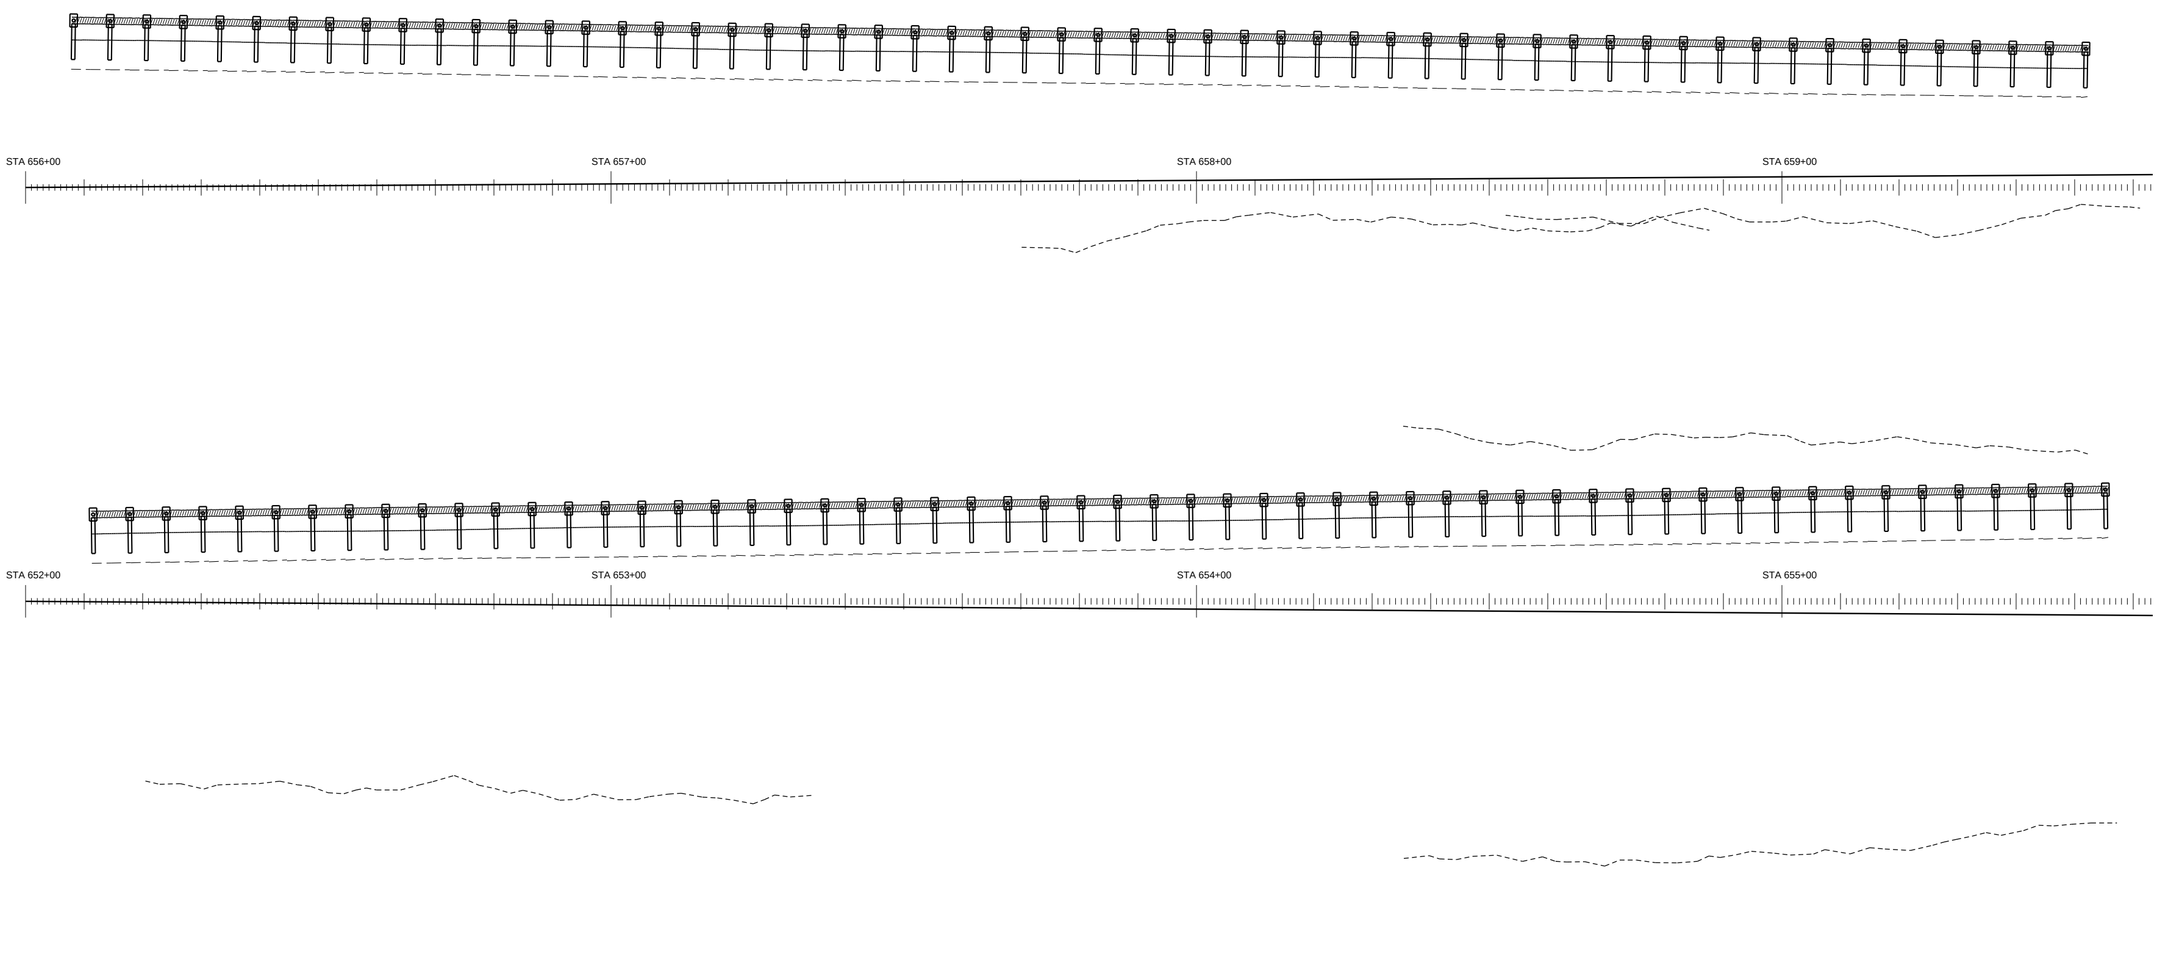





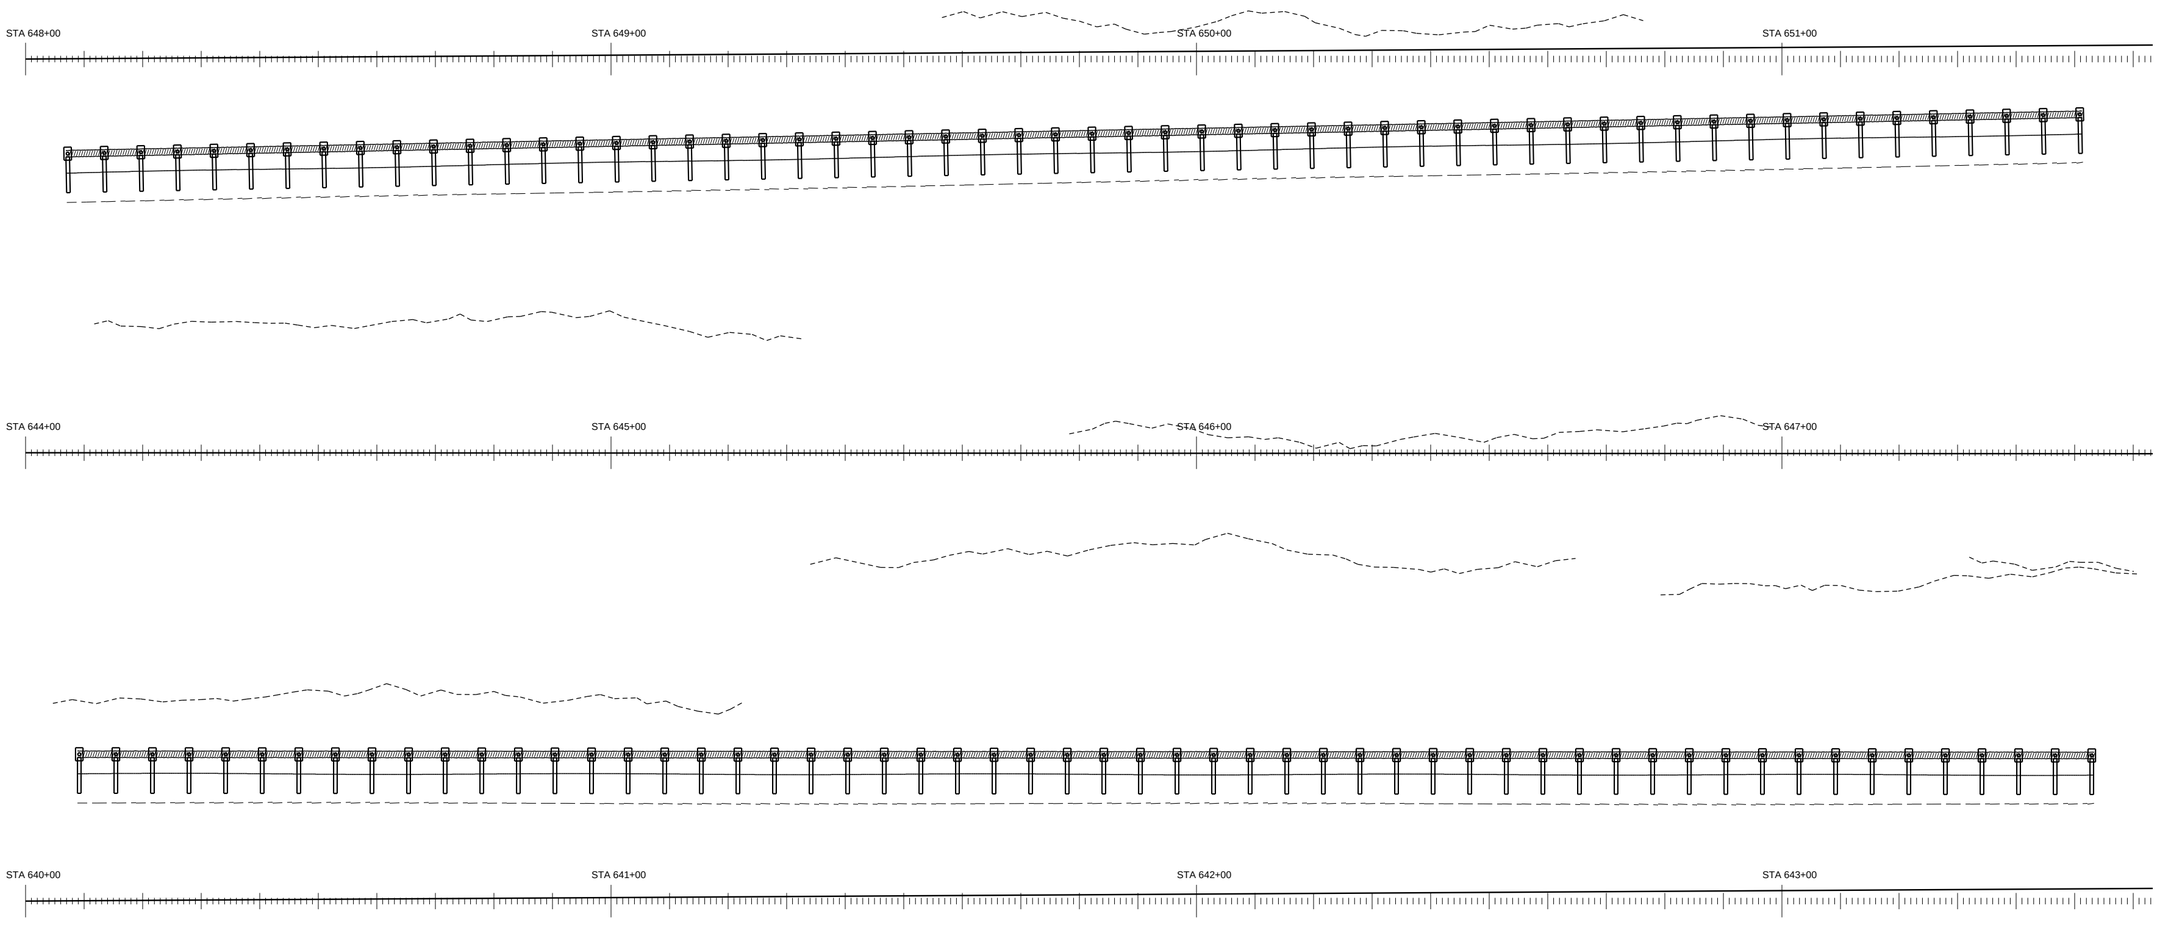








PAY ITEM 536-1-1 GUARDRAIL ROADWAY (TL-3)

PAY ITEM 536-85-24 END TREATMENT

GUARANTEED FENCE CORP

FIN. PROJ. ID 441234-1-52-01

SHEET 37 OF 120

SHEET NO. 137

ROADWAY PLAN SCALE: 1" = 20'

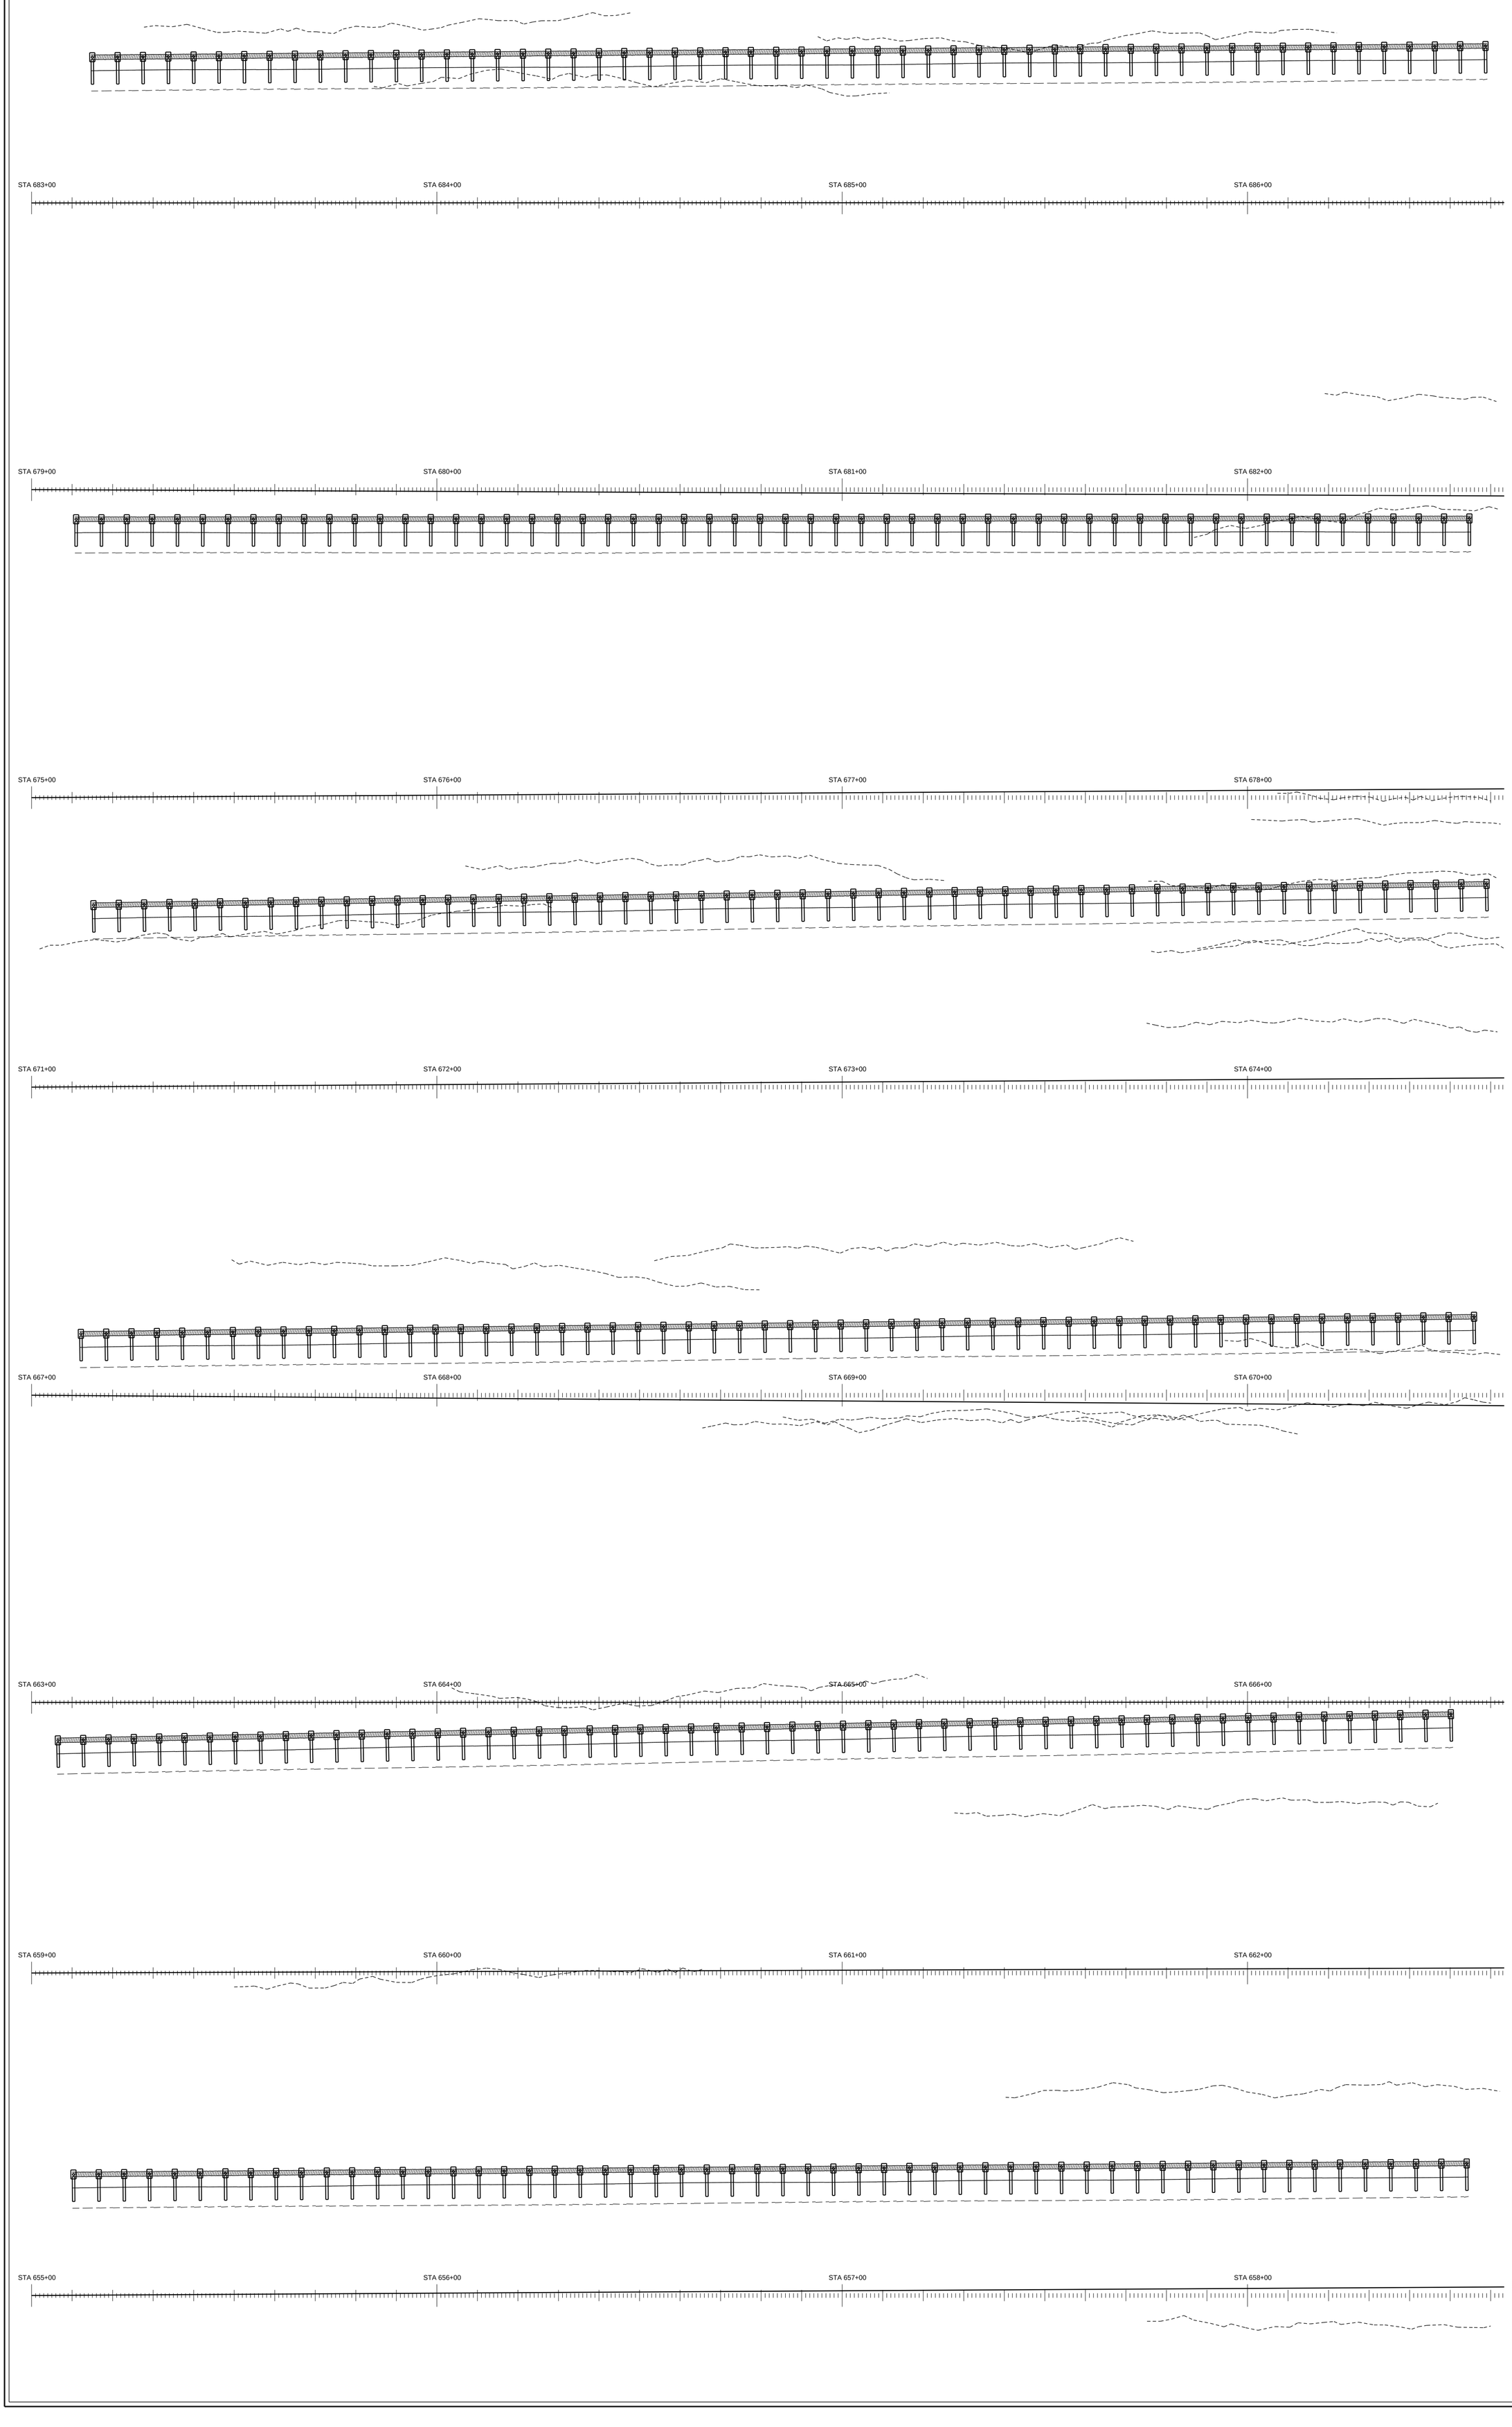


PAY ITEM 536-1-1 GUARDRAIL ROADWAY (TL-3)

PAY ITEM 536-85-24 END TREATMENT

GUARANTEED FENCE CORP

FIN. PROJ. ID 441234-1-52-01

SHEET 38 OF 120

SHEET NO. 138

ROADWAY PLAN SCALE: 1" = 20'




PAY ITEM 536-1-1 GUARDRAIL ROADWAY (TL-3)

PAY ITEM 536-85-24 END TREATMENT

GUARANTEED FENCE CORP

FIN. PROJ. ID 441234-1-52-01

SHEET 39 OF 120

SHEET NO. 139

ROADWAY PLAN SCALE: 1" = 20'




PAY ITEM 536-1-1 GUARDRAIL ROADWAY (TL-3)

PAY ITEM 536-85-24 END TREATMENT

GUARANTEED FENCE CORP

FIN. PROJ. ID 441234-1-52-01

SHEET 40 OF 120

SHEET NO. 140

ROADWAY PLAN SCALE: 1" = 20'

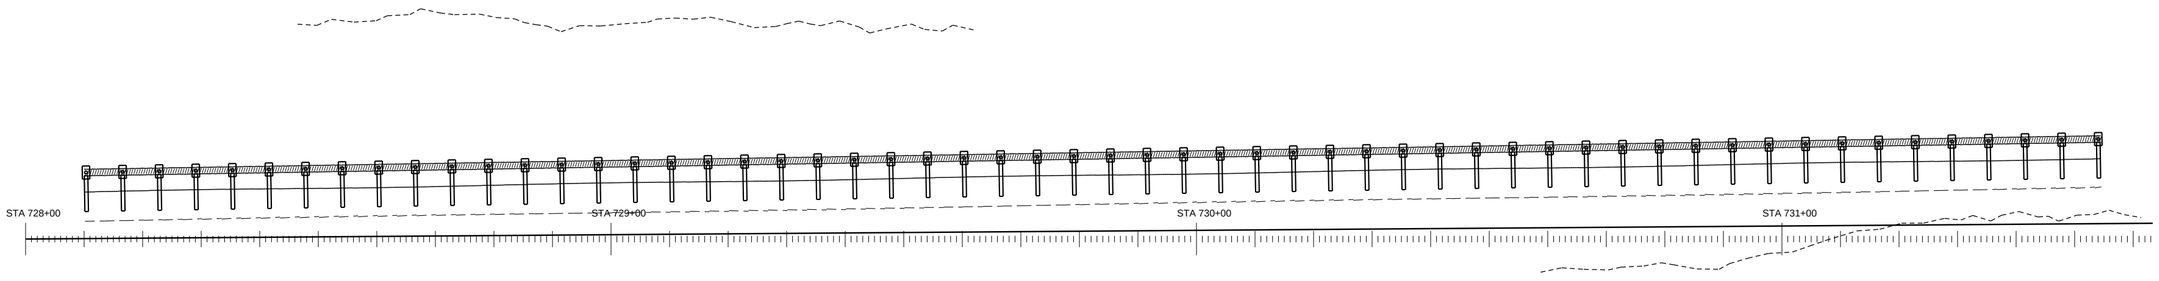


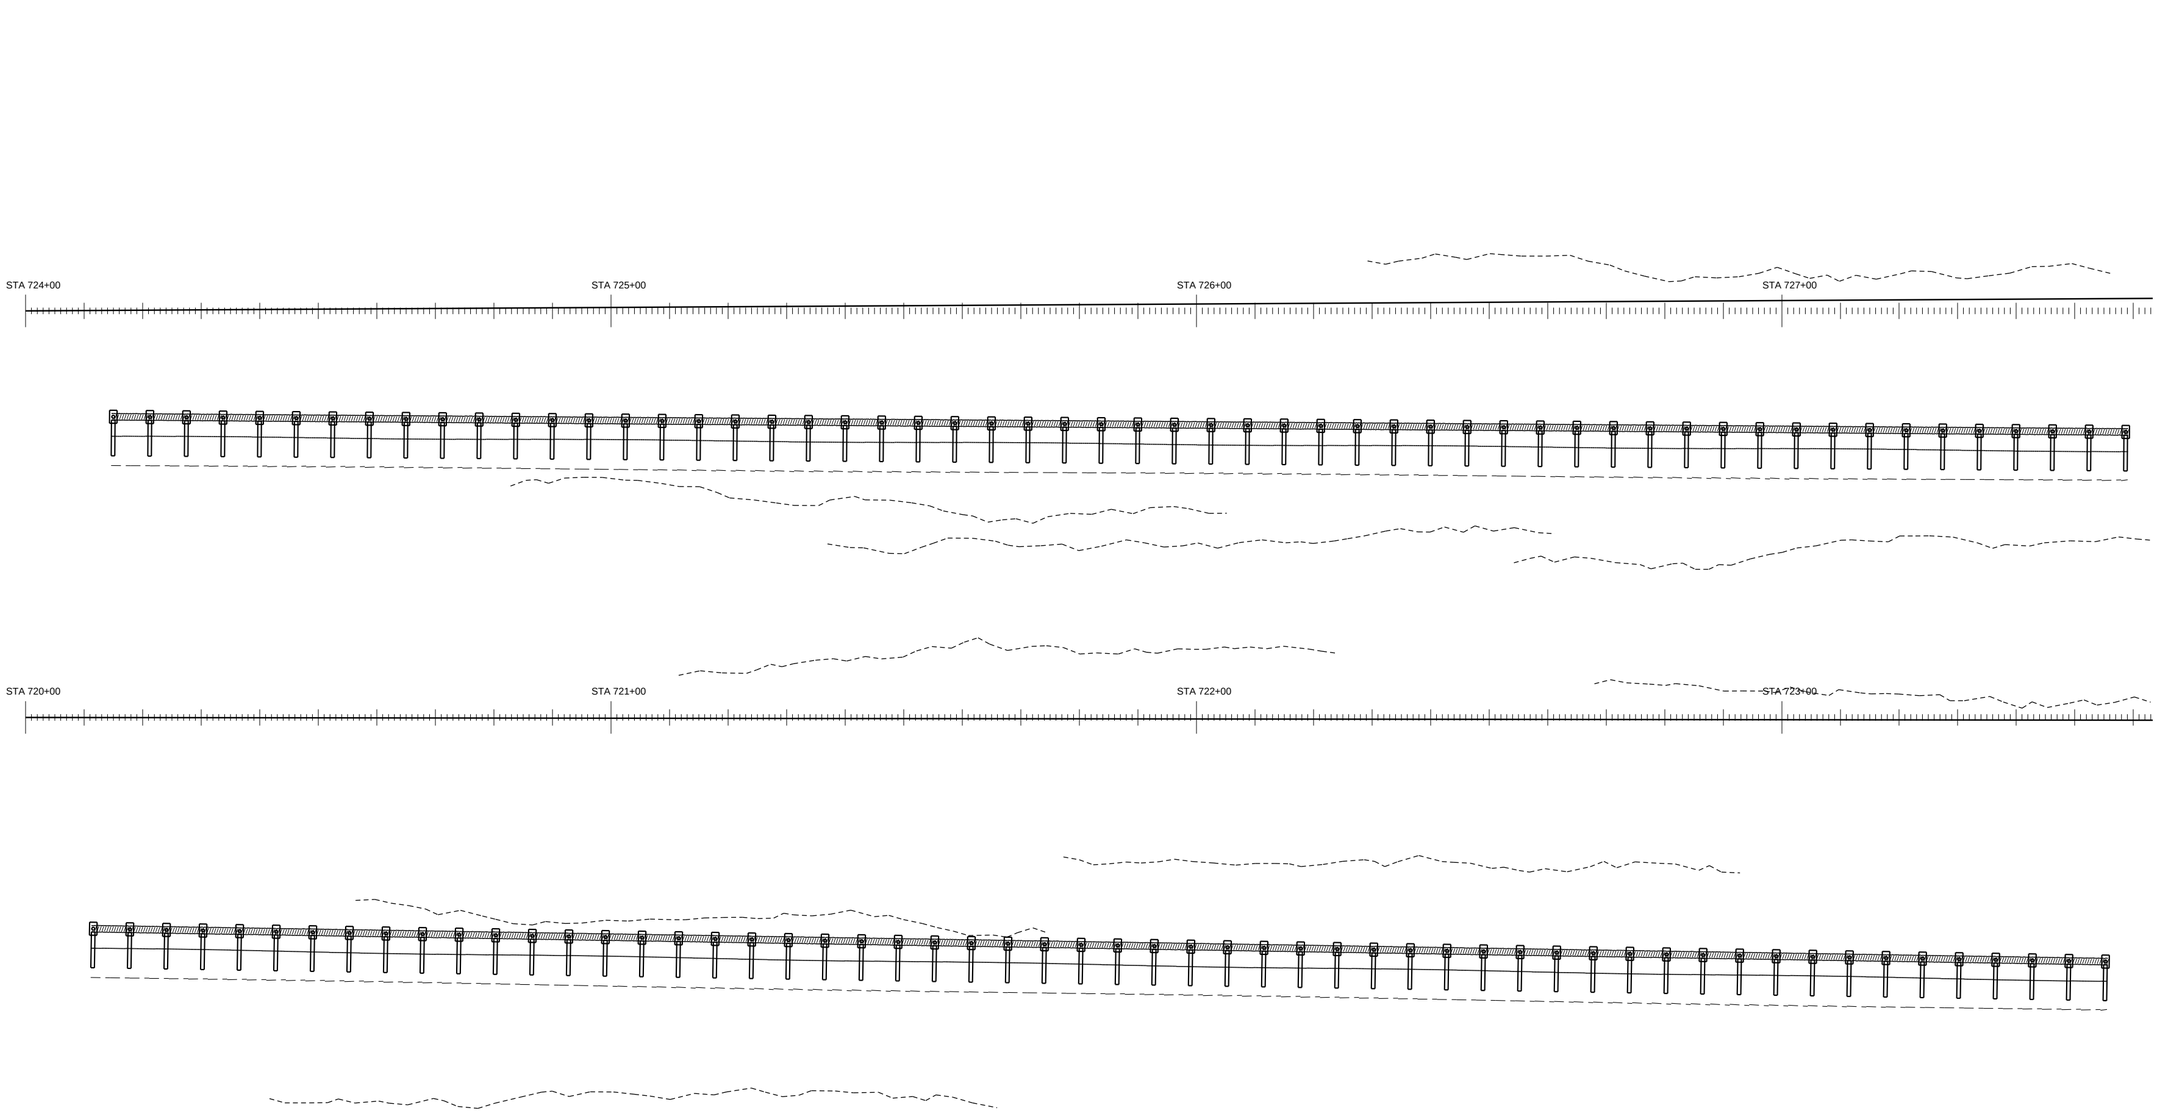








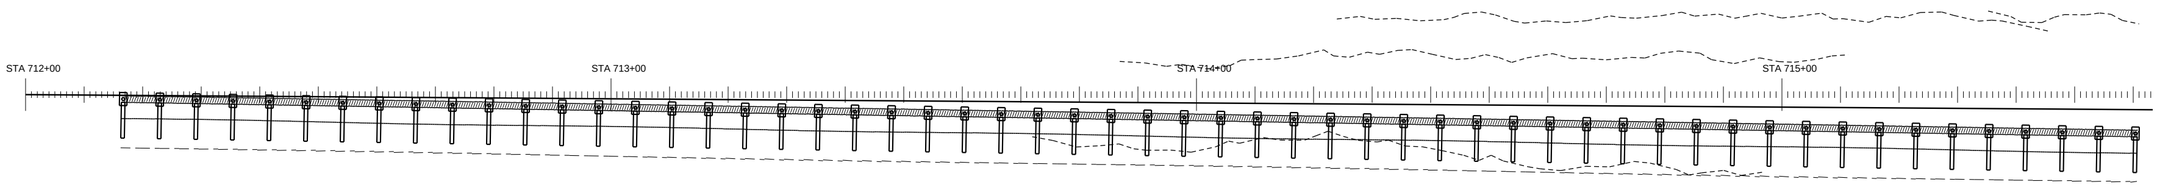


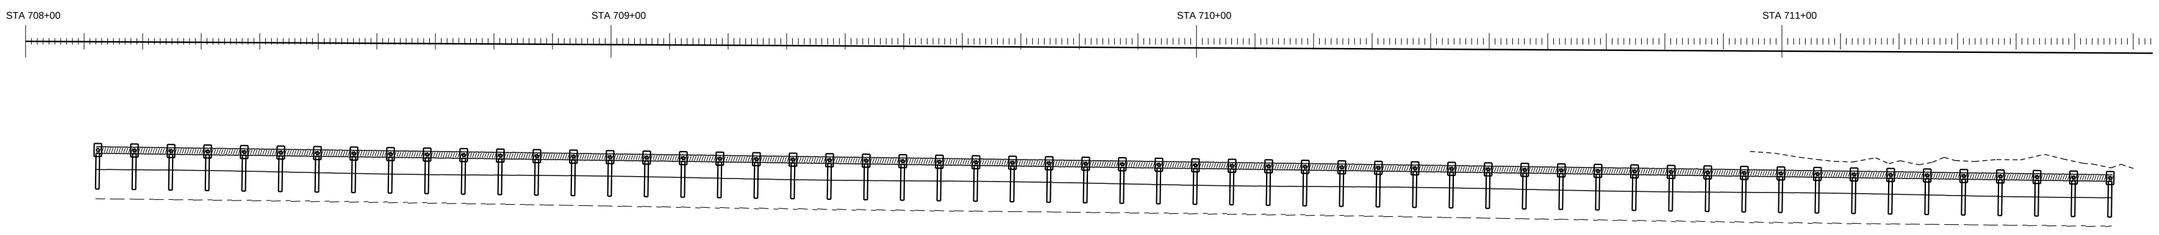


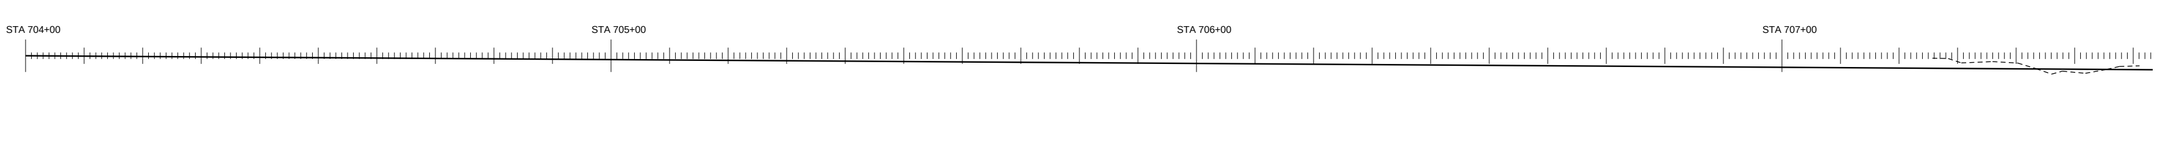


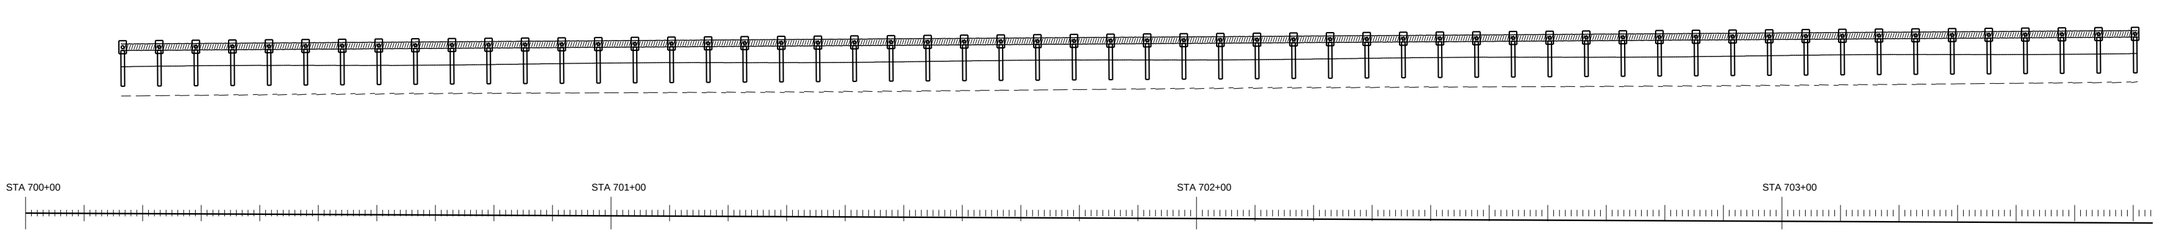


PAY ITEM 536-1-1 GUARDRAIL ROADWAY (TL-3)

PAY ITEM 536-85-24 END TREATMENT

GUARANTEED FENCE CORP

FIN. PROJ. ID 441234-1-52-01

SHEET 41 OF 120

SHEET NO. 141

ROADWAY PLAN SCALE: 1" = 20'

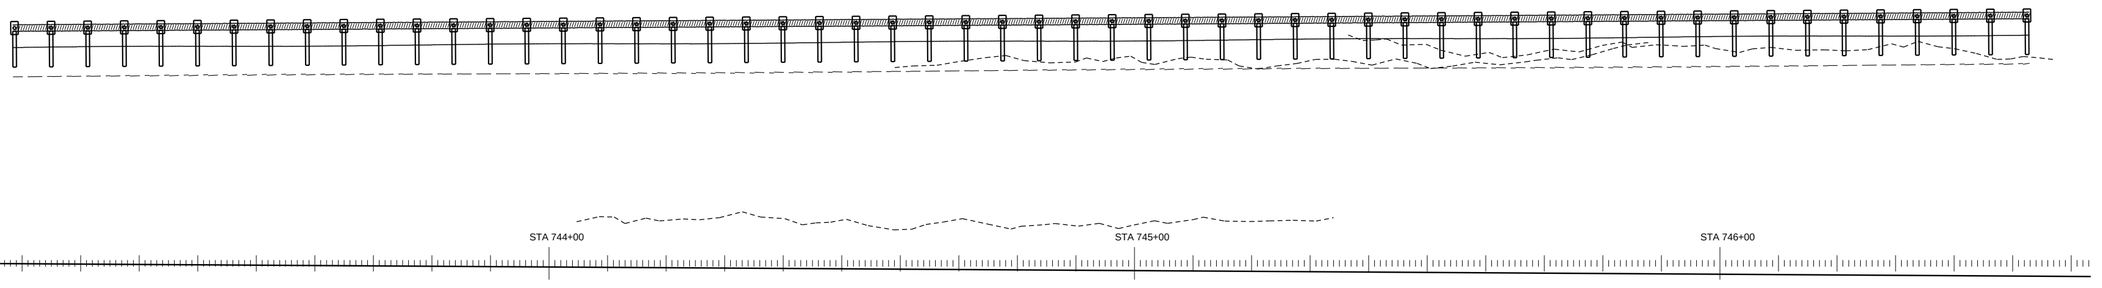


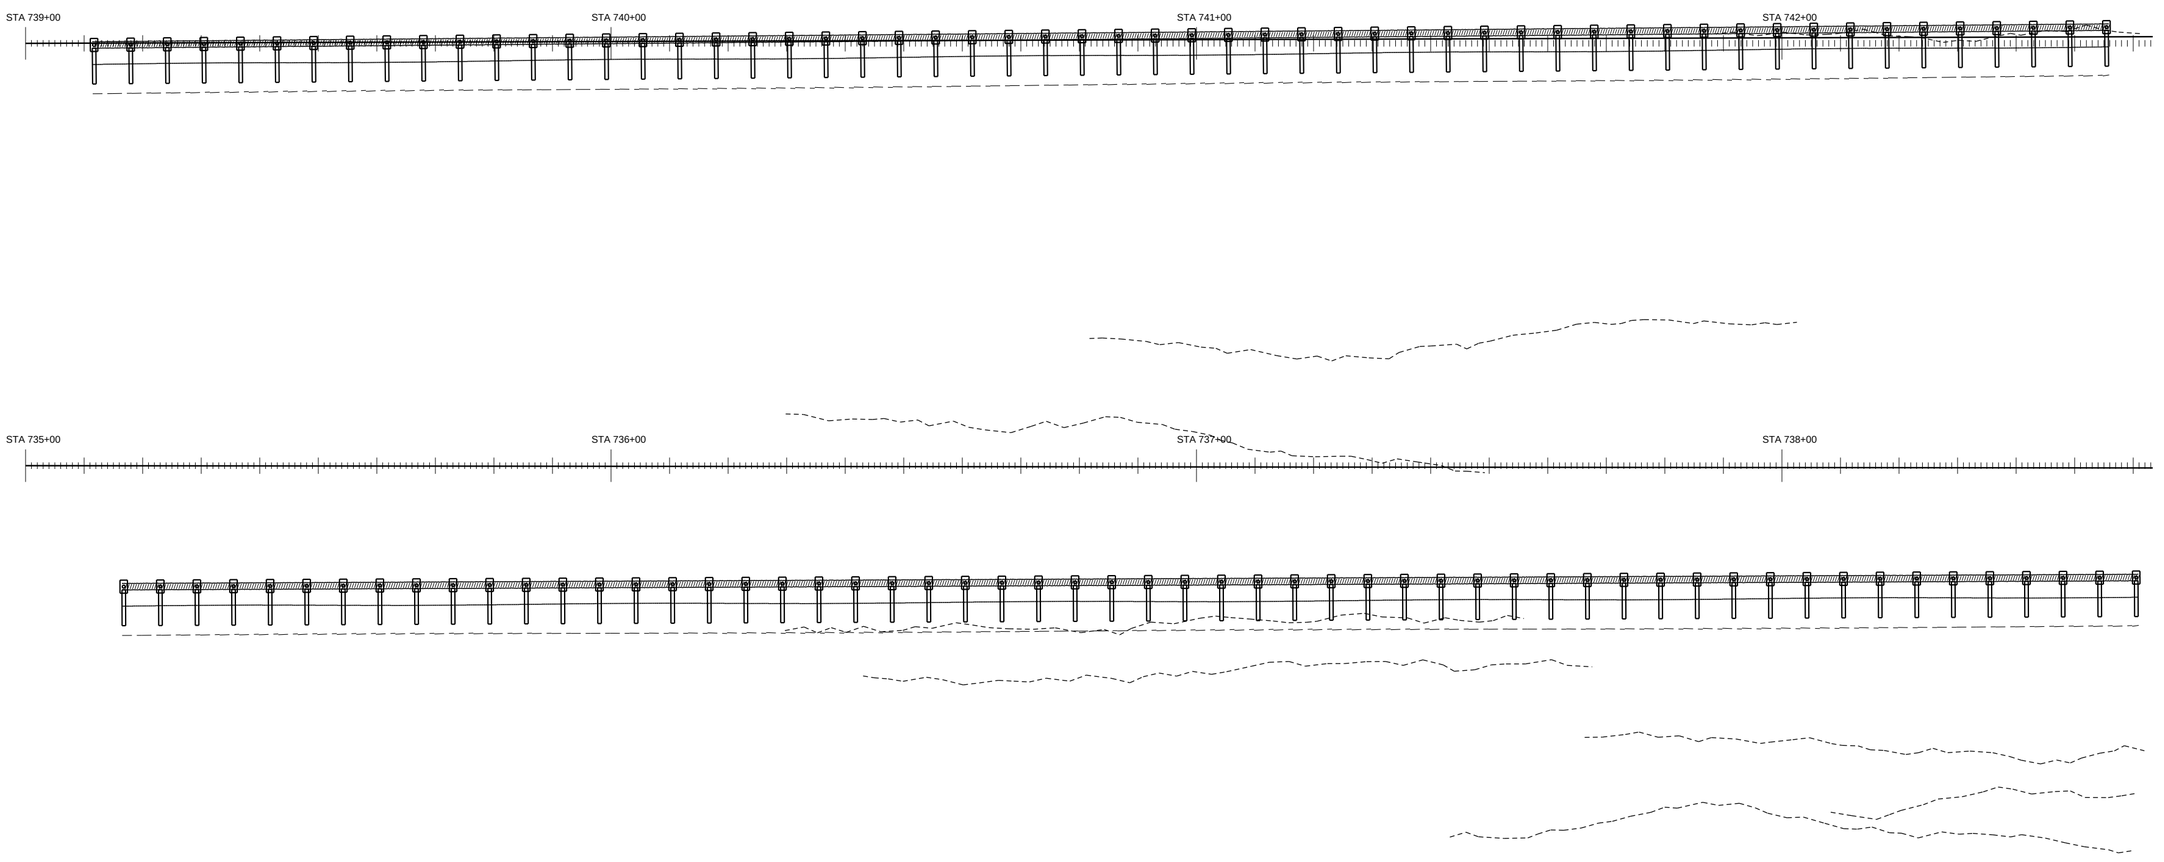


PAY ITEM 536-1-1 GUARDRAIL ROADWAY (TL-3)

PAY ITEM 536-85-24 END TREATMENT

GUARANTEED FENCE CORP

FIN. PROJ. ID 441234-1-52-01

SHEET 42 OF 120

SHEET NO. 142

ROADWAY PLAN SCALE: 1" = 20'

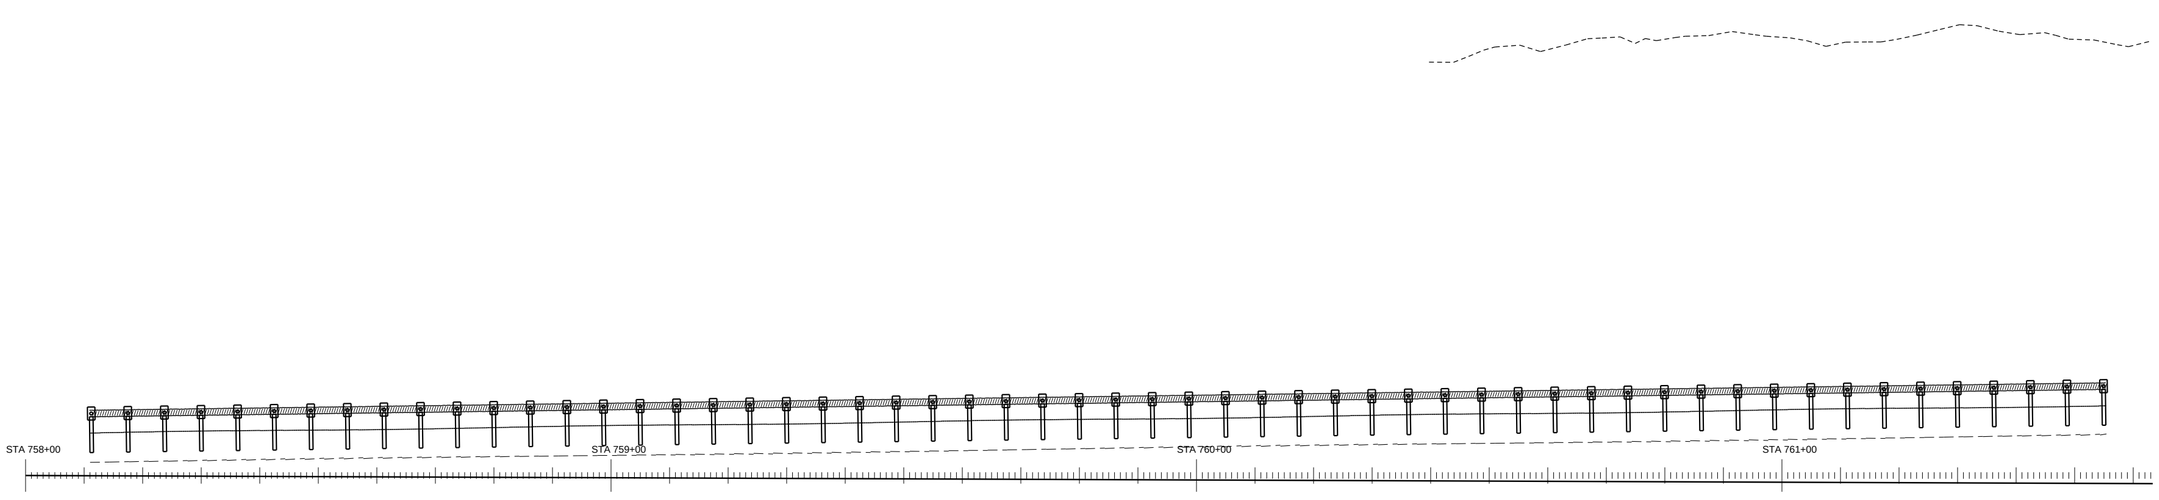


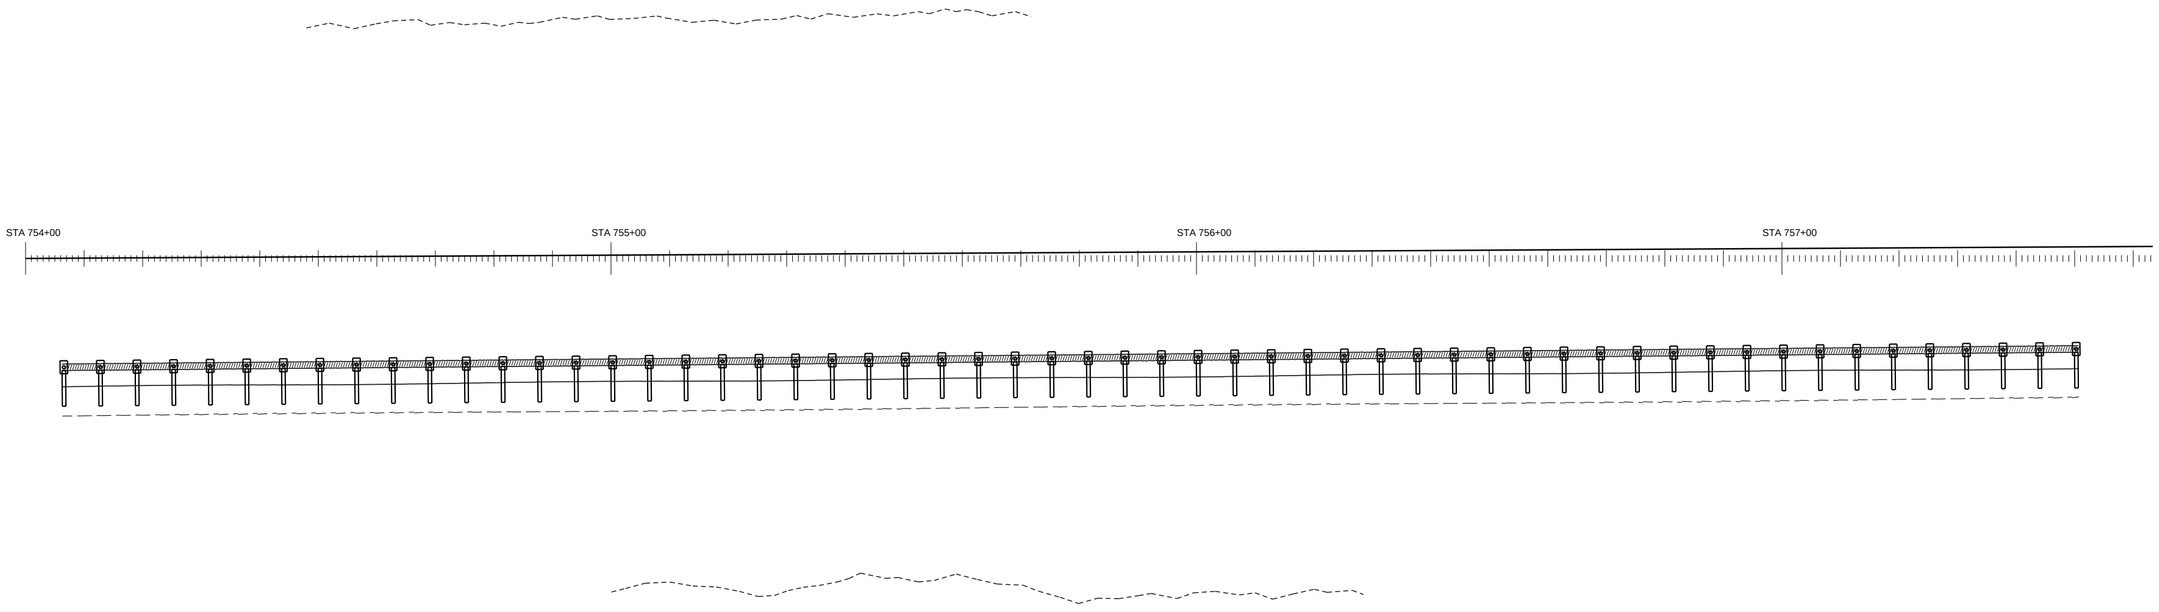


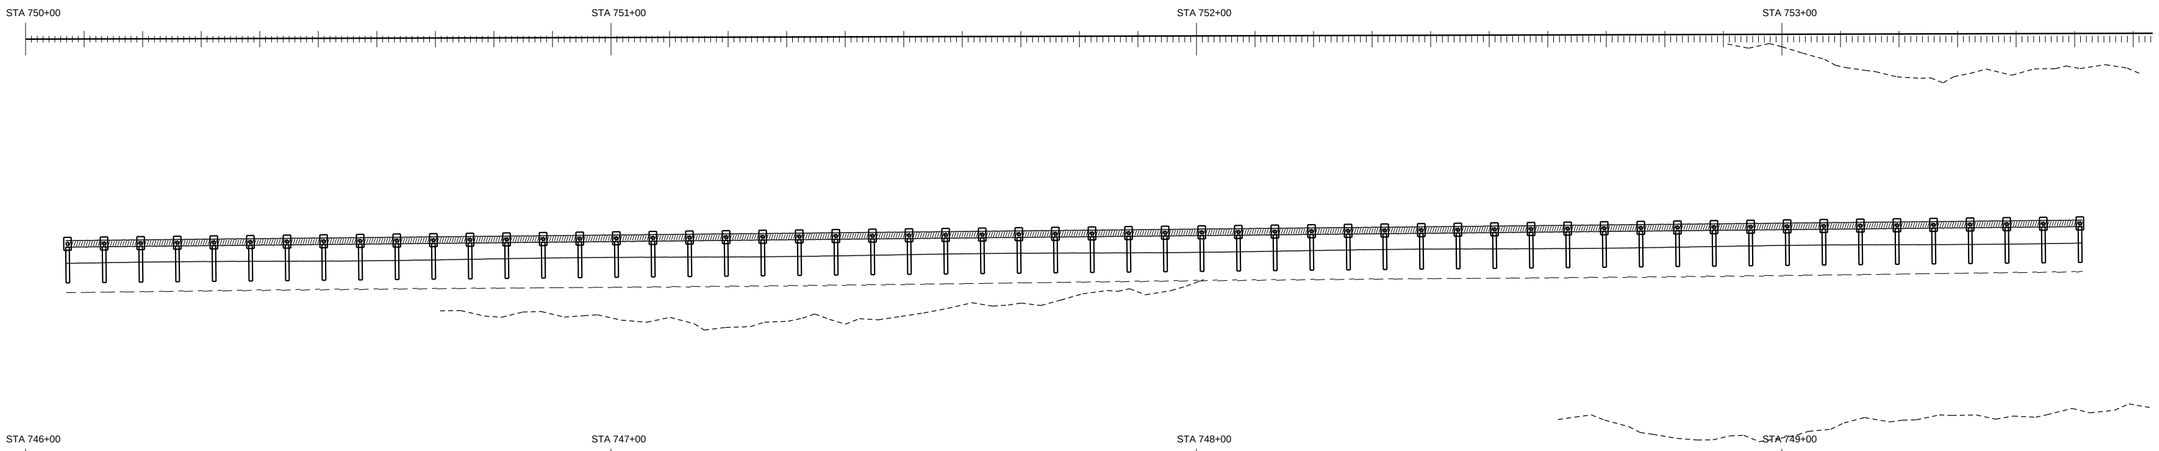


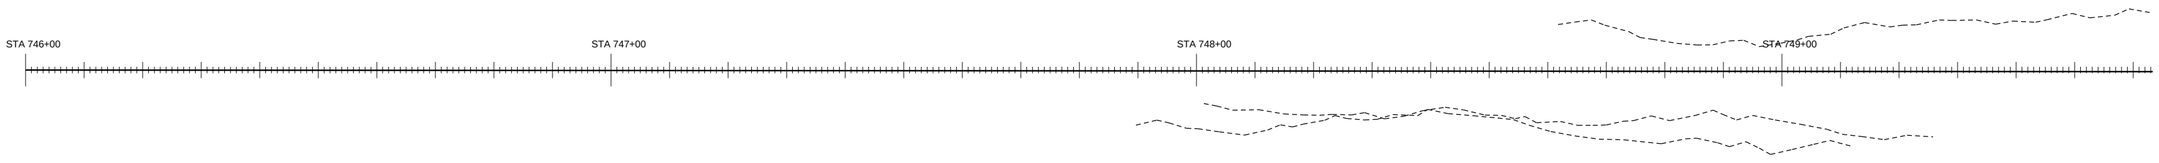


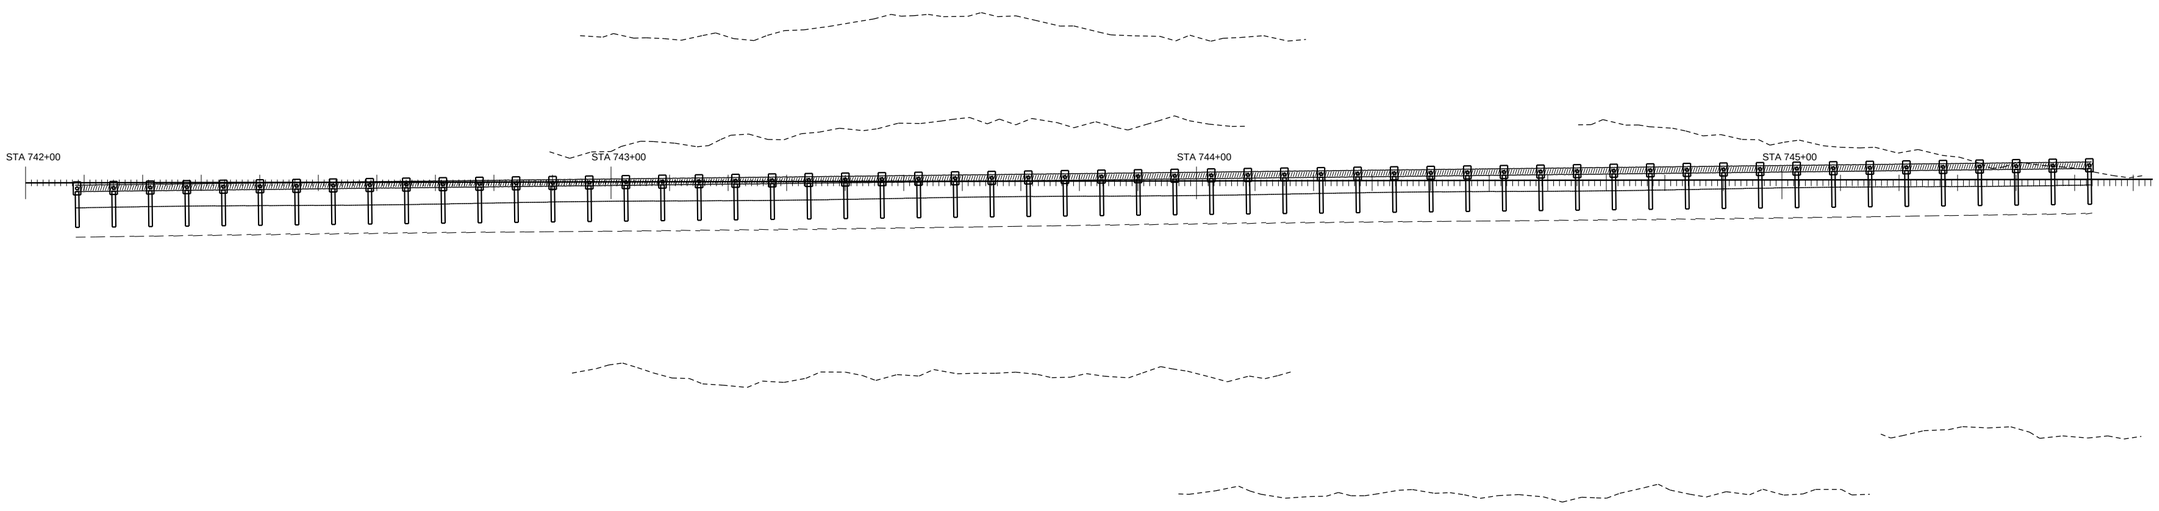


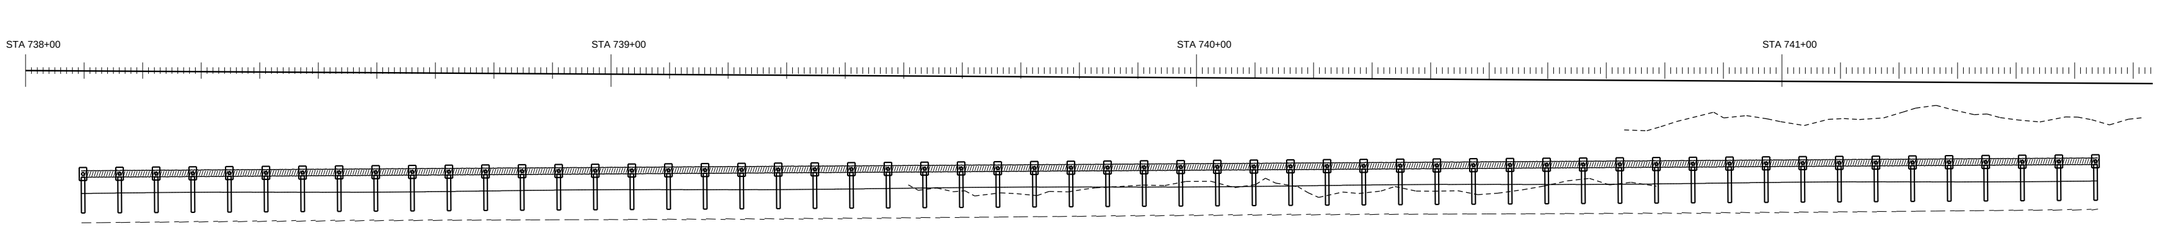


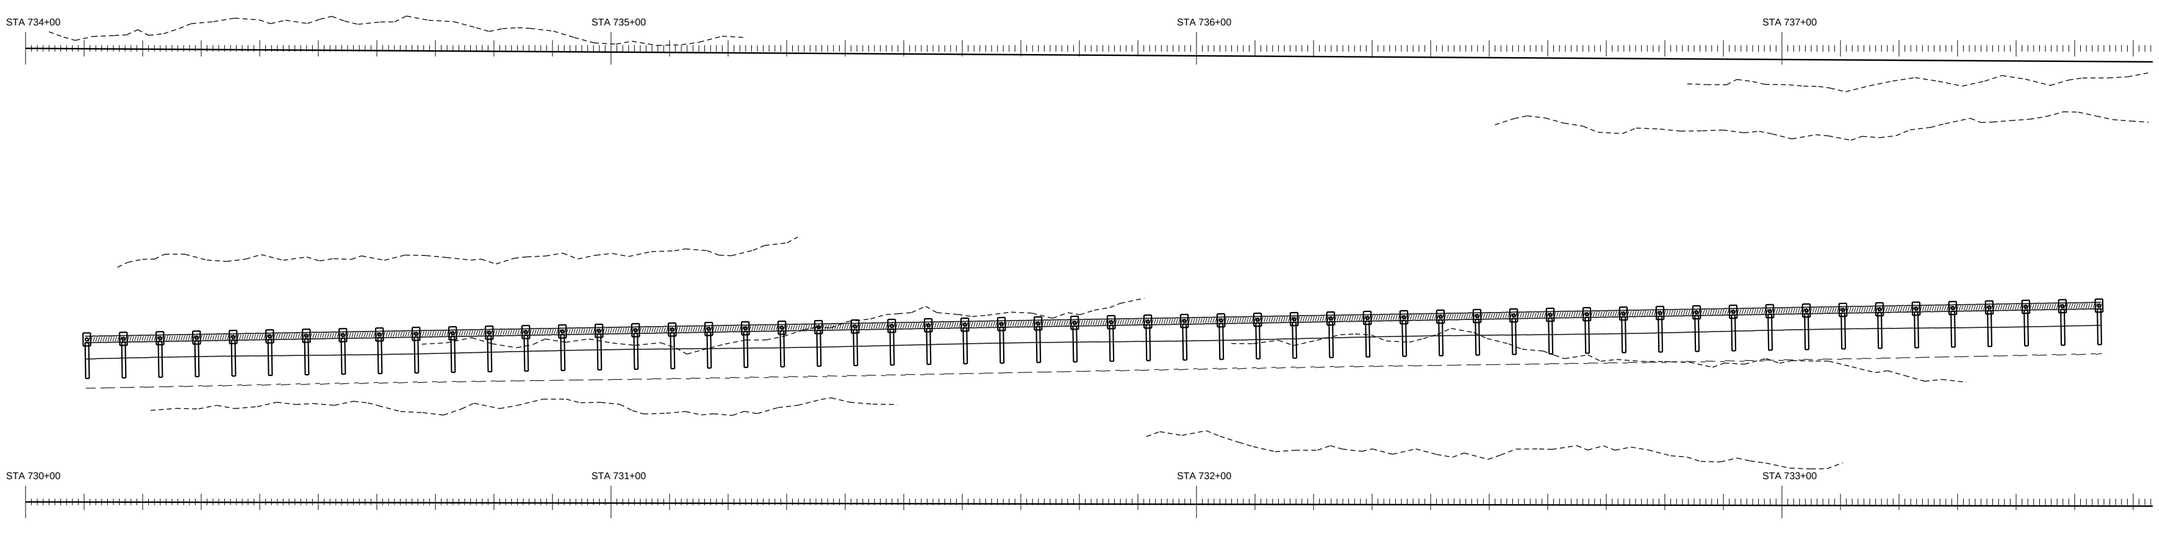





PAY ITEM 536-1-1 GUARDRAIL ROADWAY (TL-3)

PAY ITEM 536-85-24 END TREATMENT

GUARANTEED FENCE CORP

FIN. PROJ. ID 441234-1-52-01

SHEET 43 OF 120

SHEET NO. 143

ROADWAY PLAN SCALE: 1" = 20'

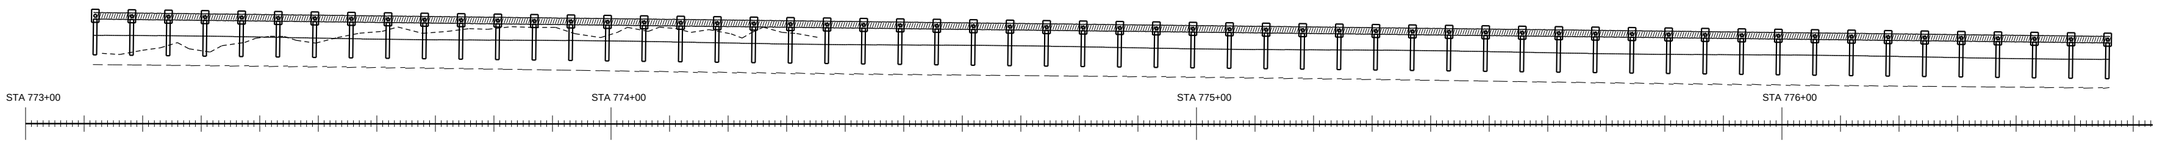


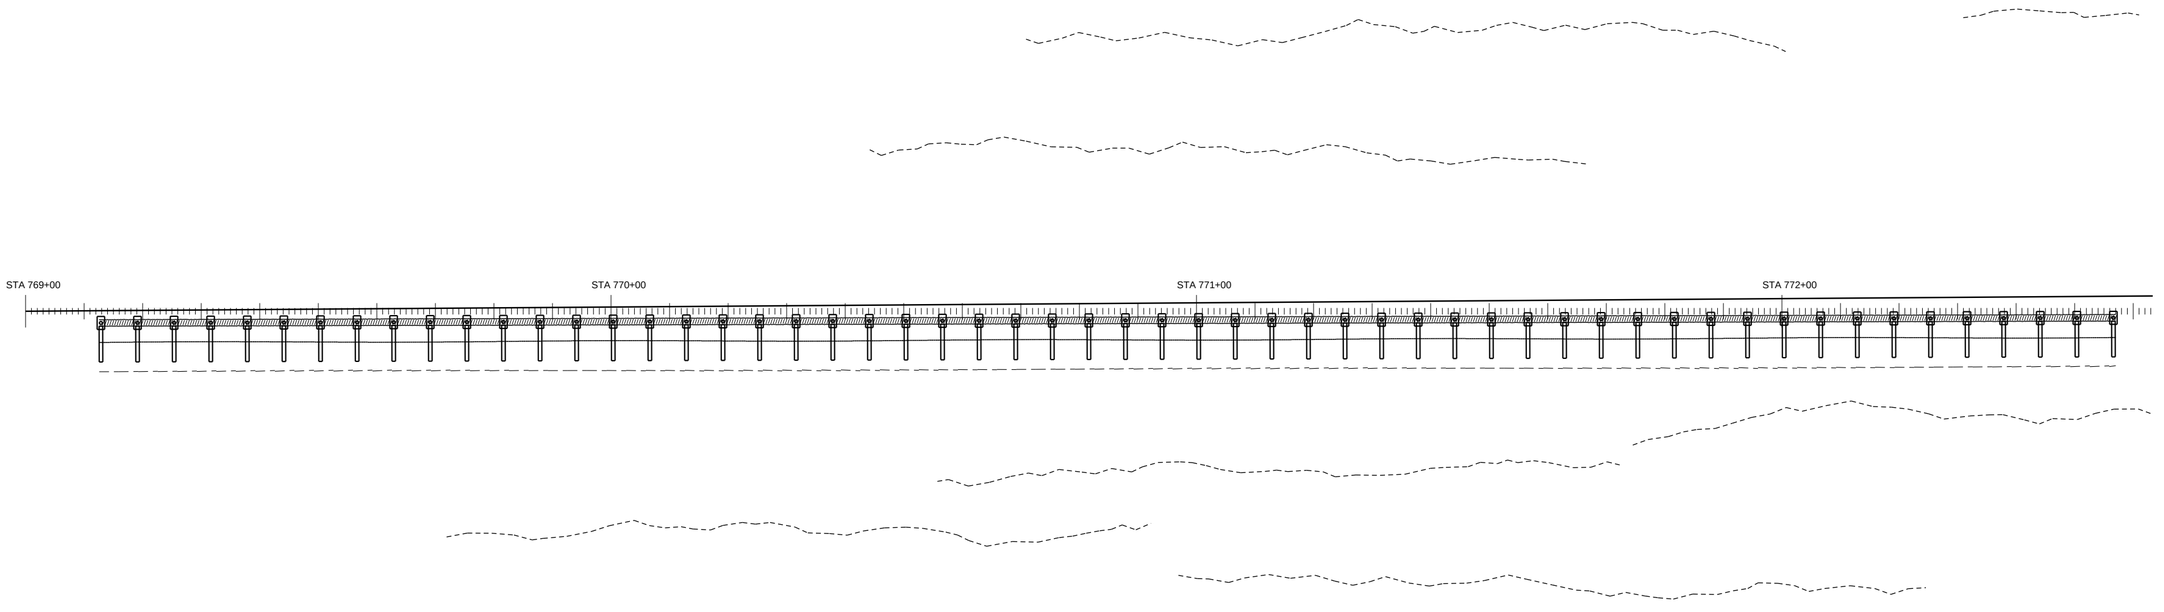


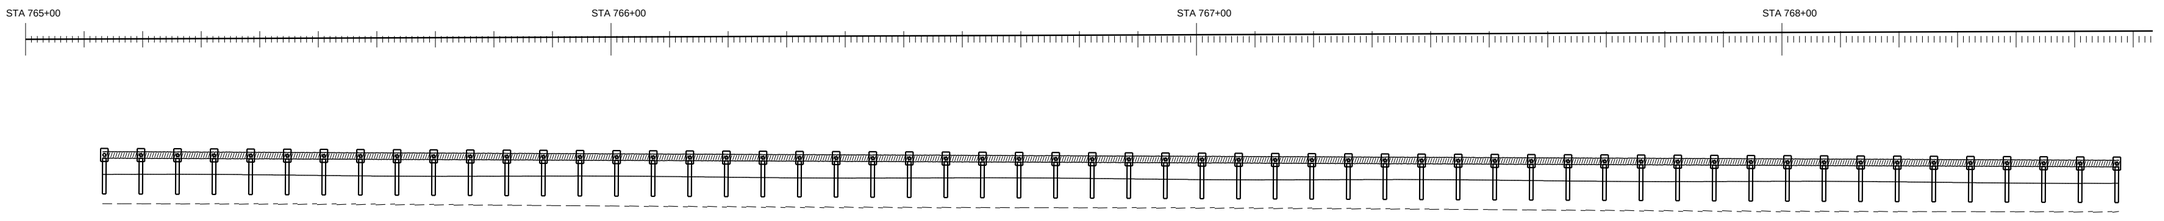


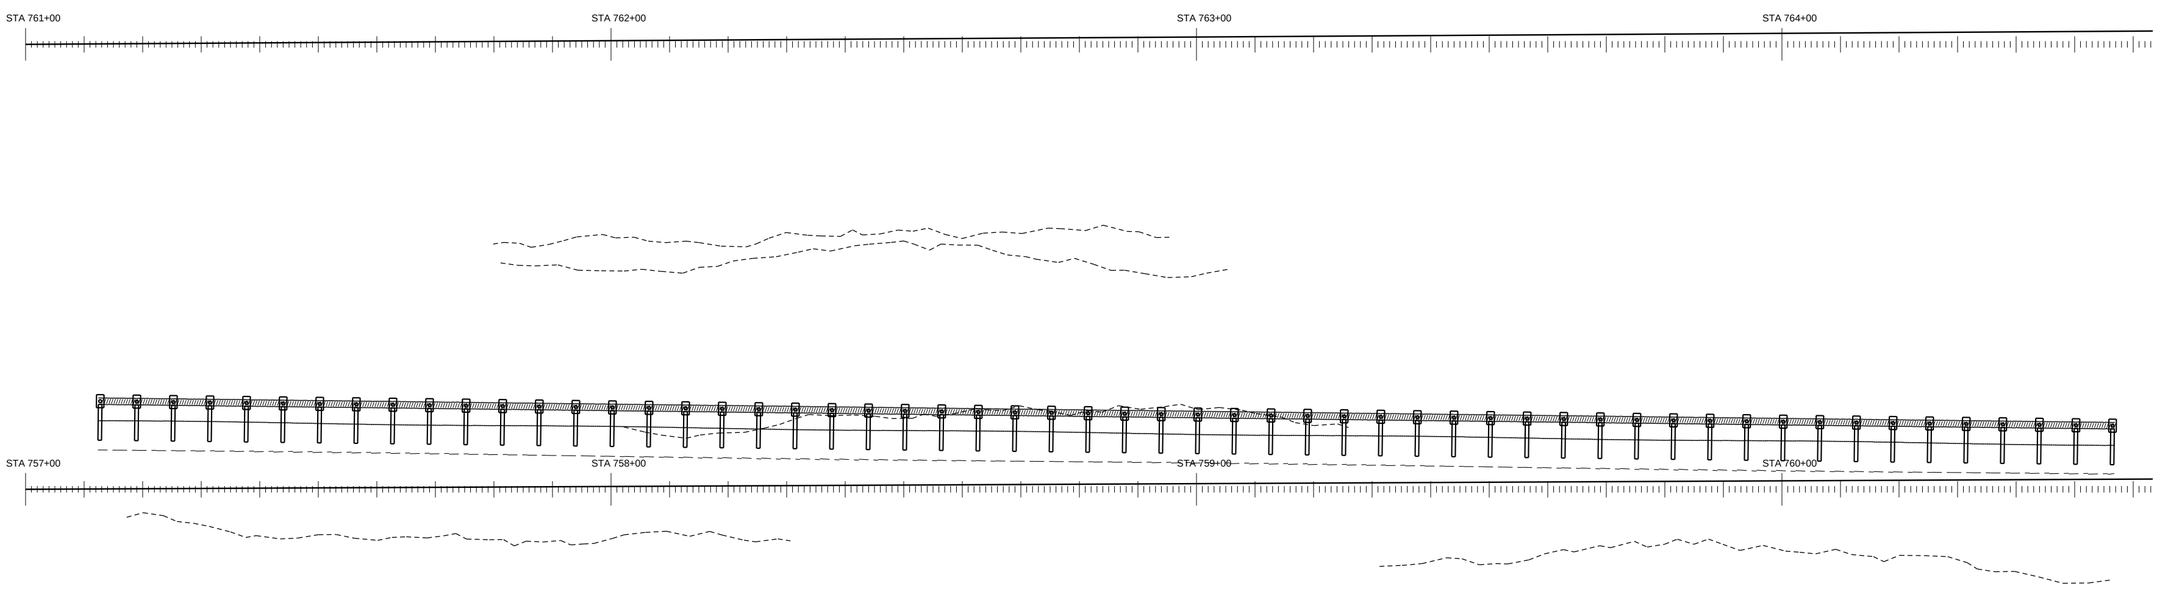


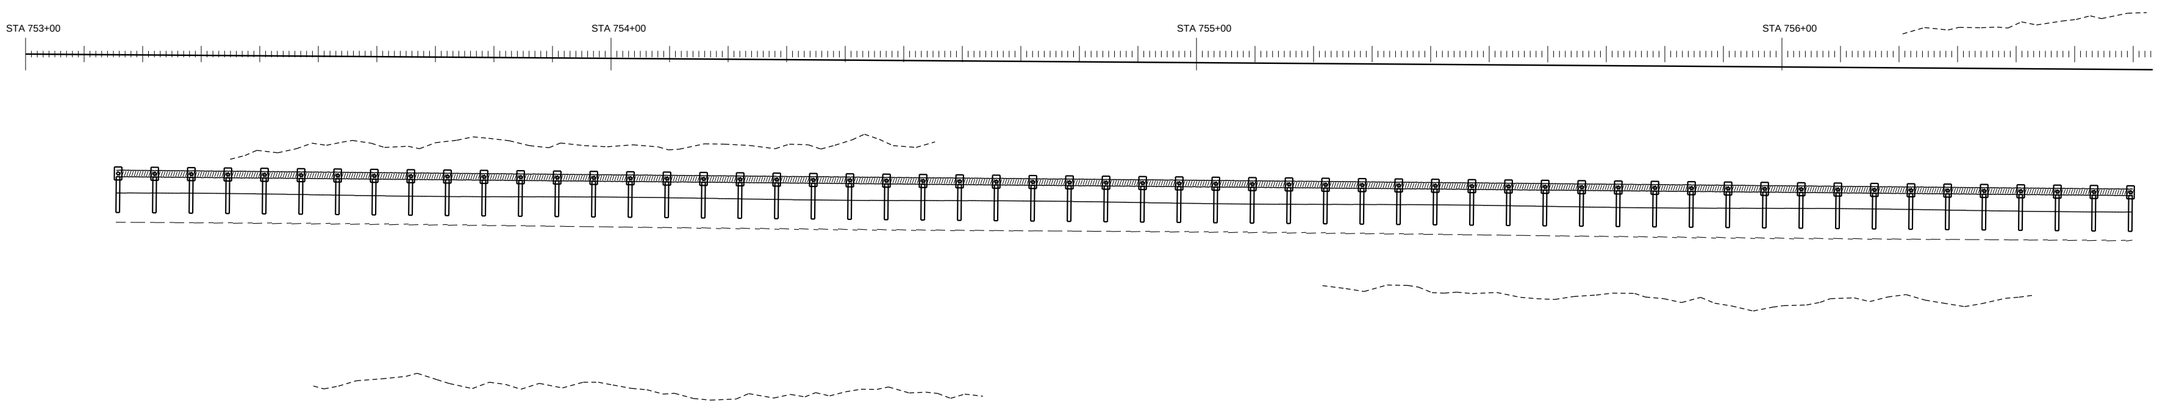


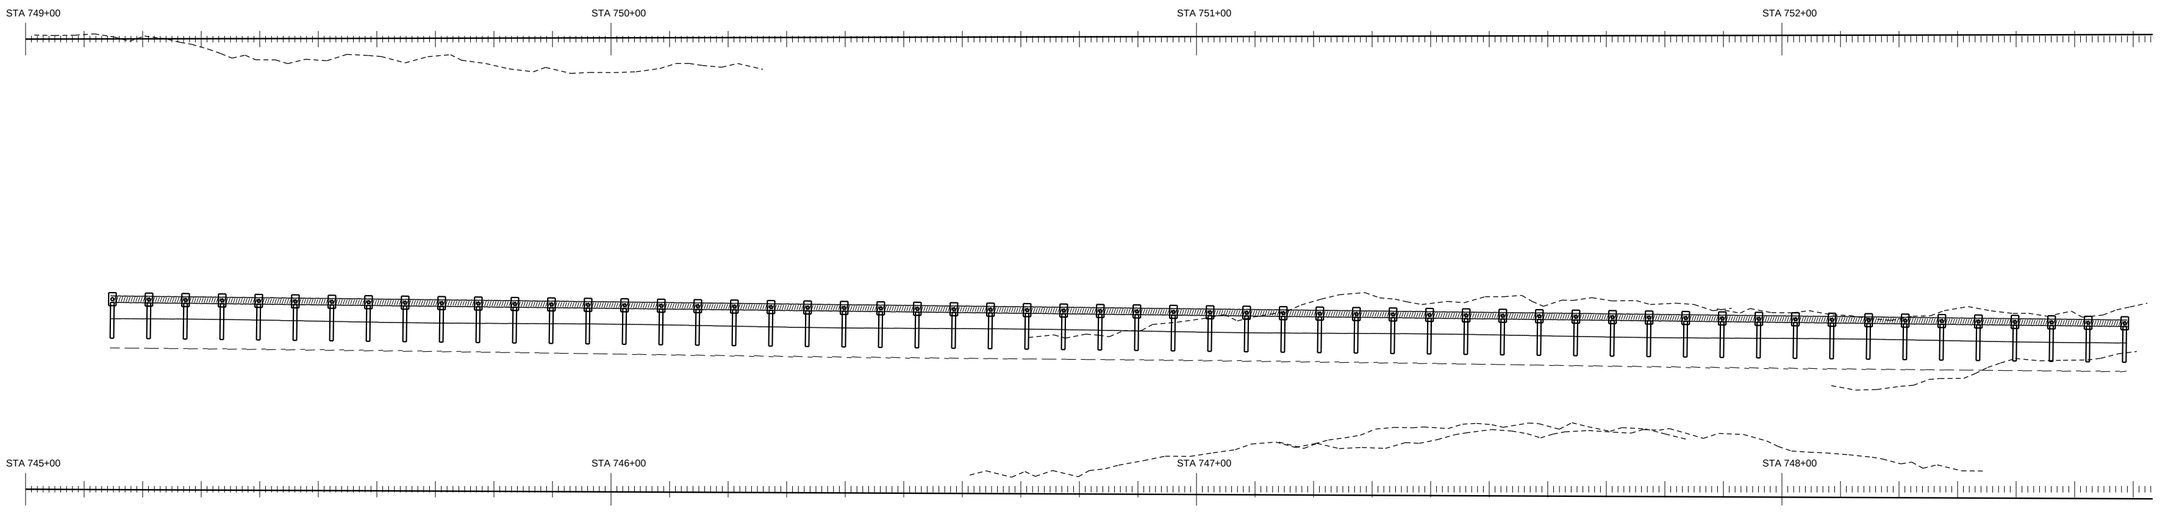


PAY ITEM 536-1-1 GUARDRAIL ROADWAY (T-3)

PAY ITEM 536-85-24 END TREATMENT

GUARANTEED FENCE CORP

FIN. PROJ. ID 441234-1-52-01

SHEET 44 OF 120

SHEET NO. 144

ROADWAY PLAN SCALE: 1" = 20'




PAY ITEM 536-1-1 GUARDRAIL ROADWAY (TL-3)

PAY ITEM 536-85-24 END TREATMENT

GUARANTEED FENCE CORP

FIN. PROJ. ID 441234-1-52-01

SHEET 45 OF 120

SHEET NO. 145

ROADWAY PLAN SCALE: 1" = 20'

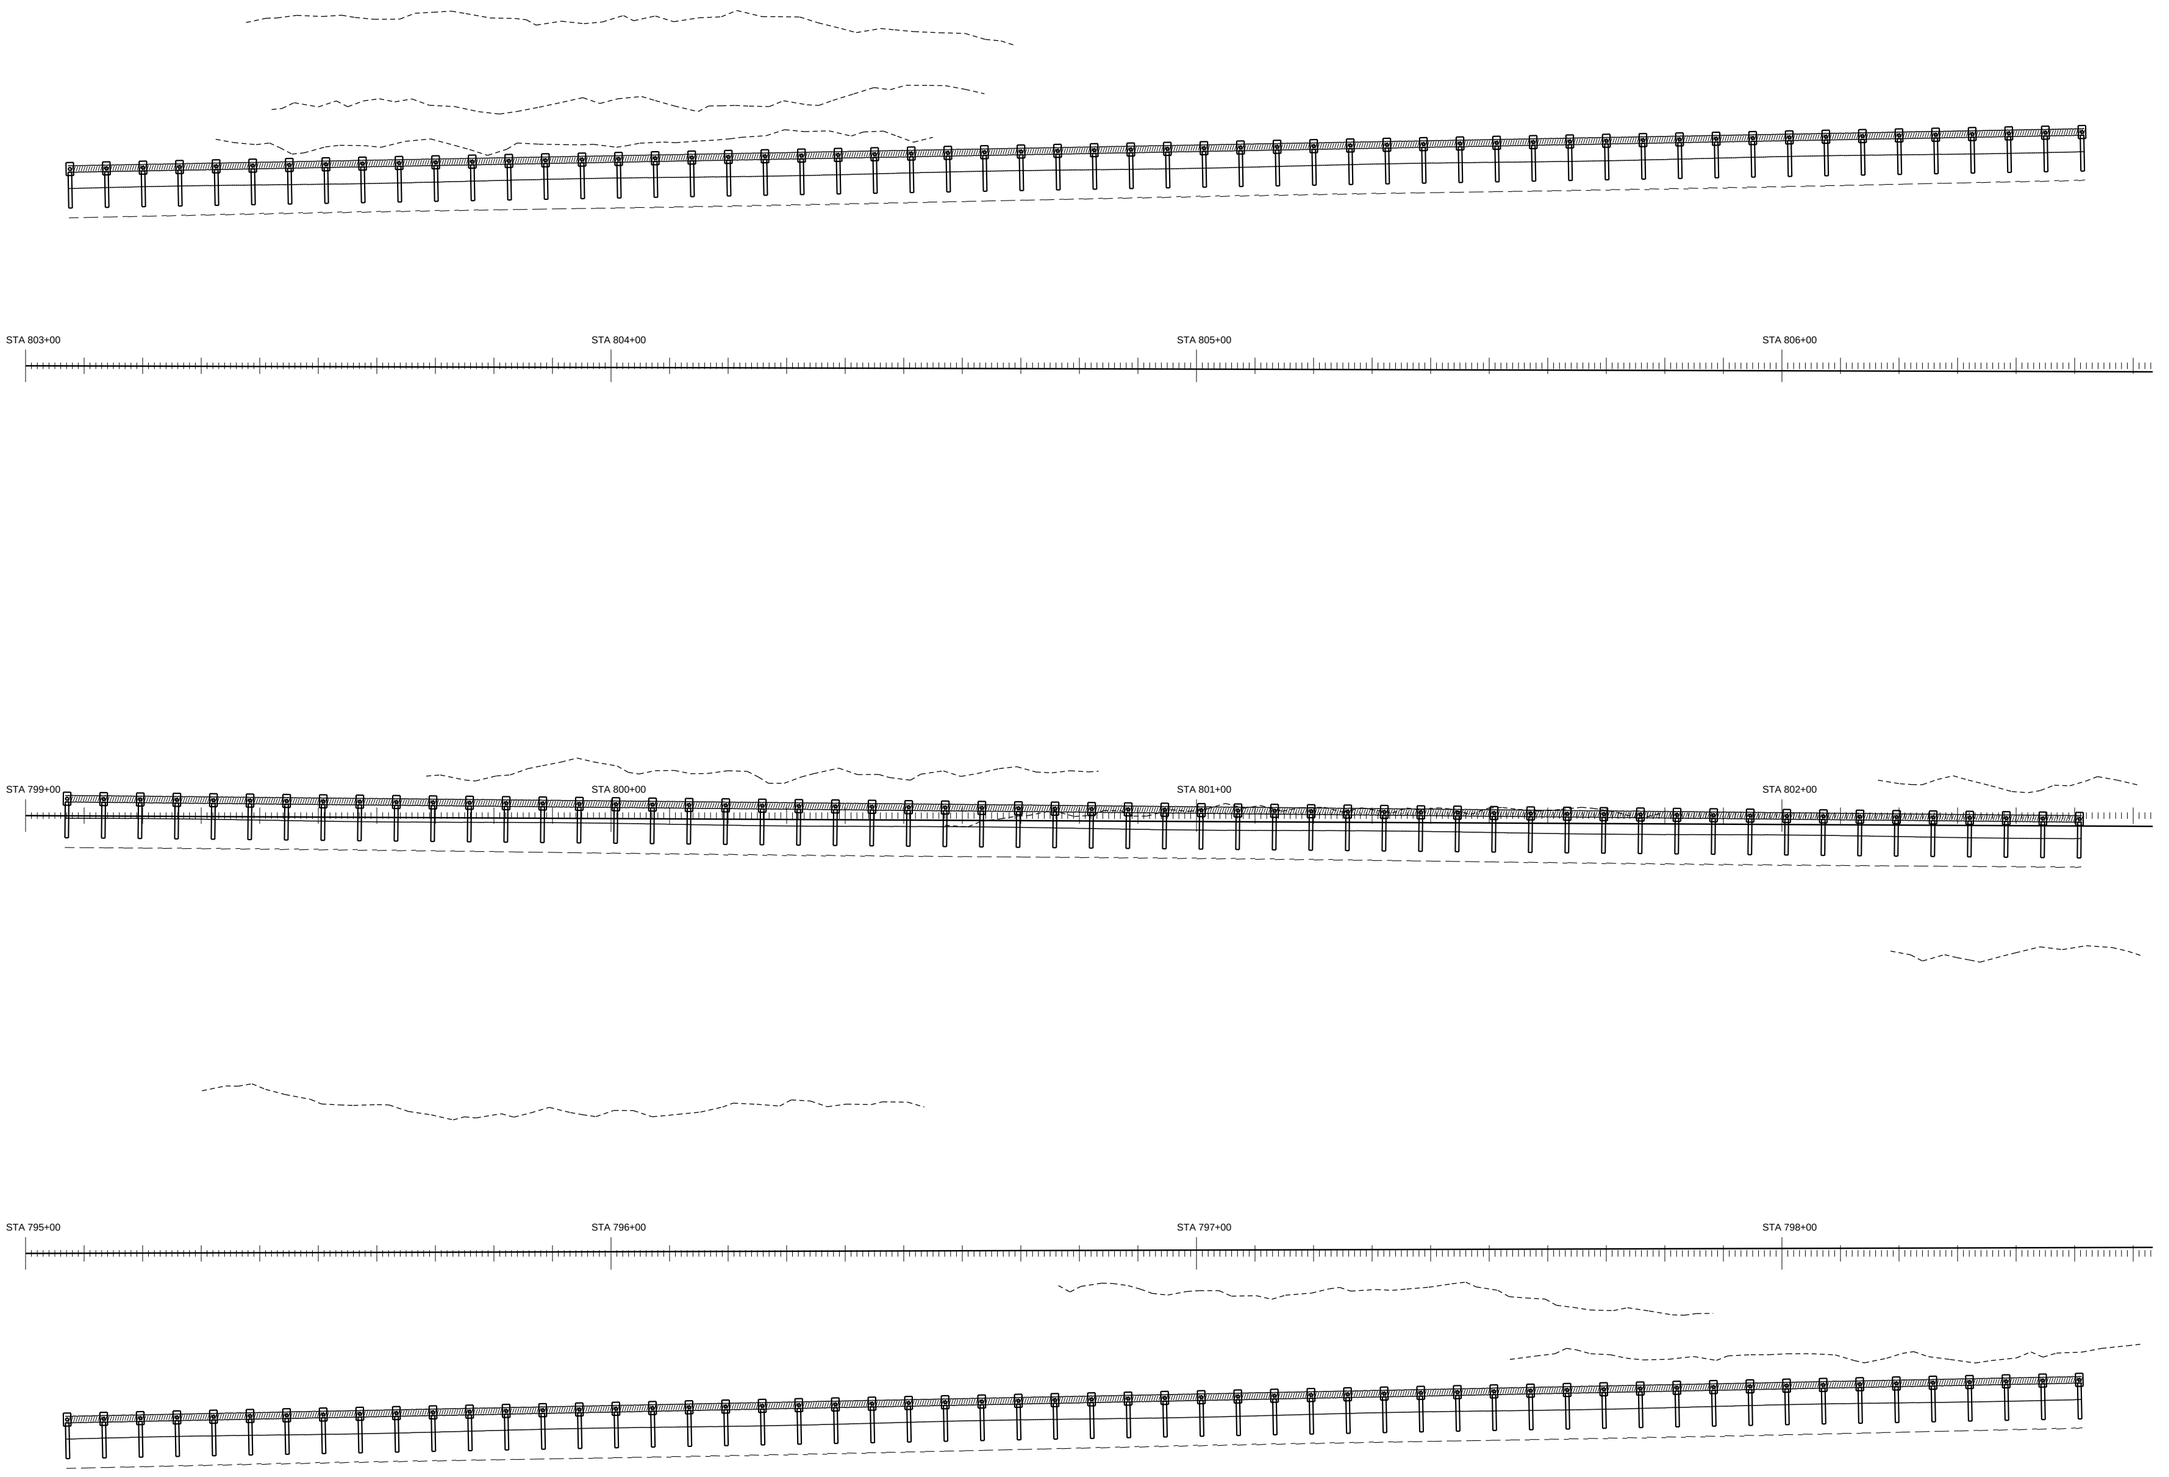


PAY ITEM 536-1-1 GUARDRAIL ROADWAY (TL-3)

PAY ITEM 536-85-24 END TREATMENT

GUARANTEED FENCE CORP

FIN. PROJ. ID 441234-1-52-01

SHEET 46 OF 120

SHEET NO. 146

ROADWAY PLAN SCALE: 1" = 20'

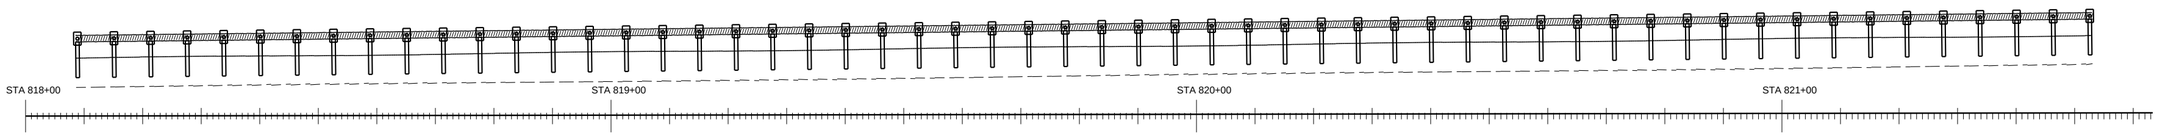


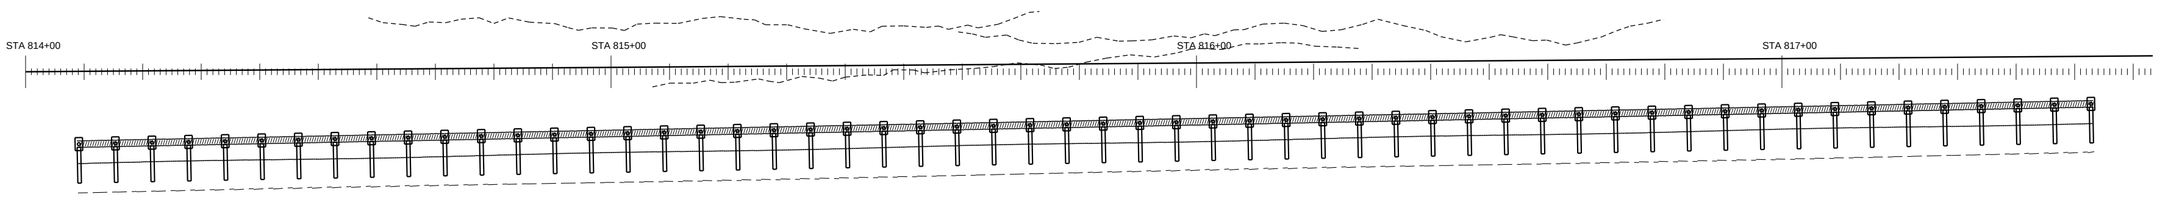


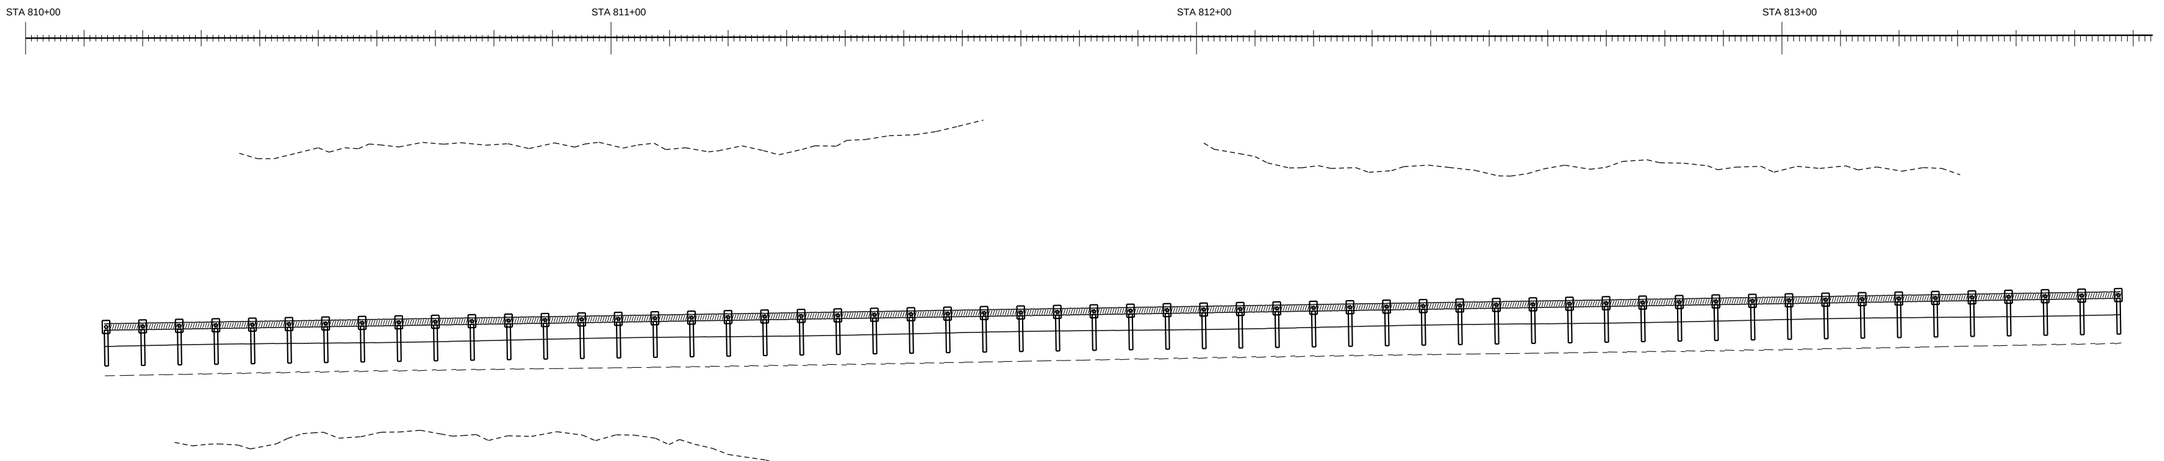


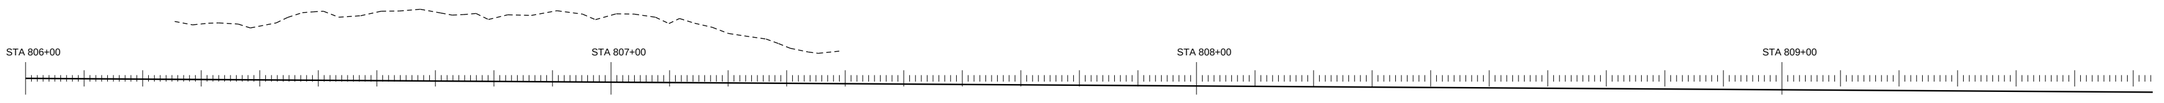


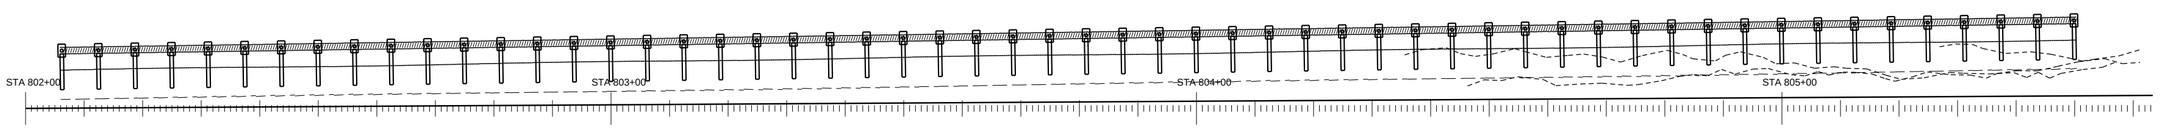


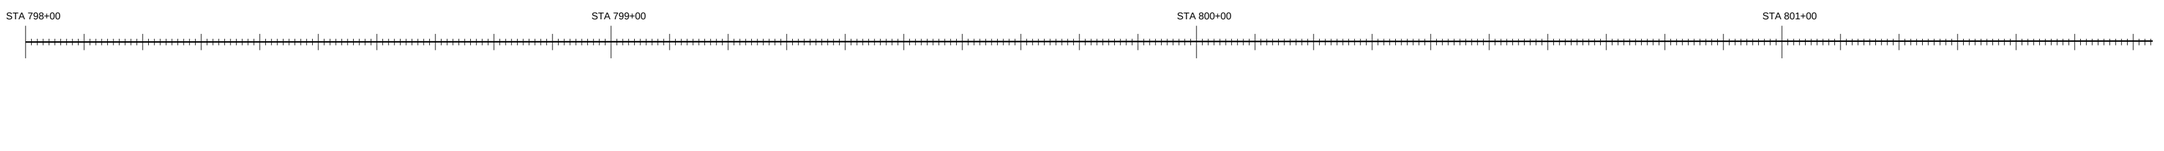


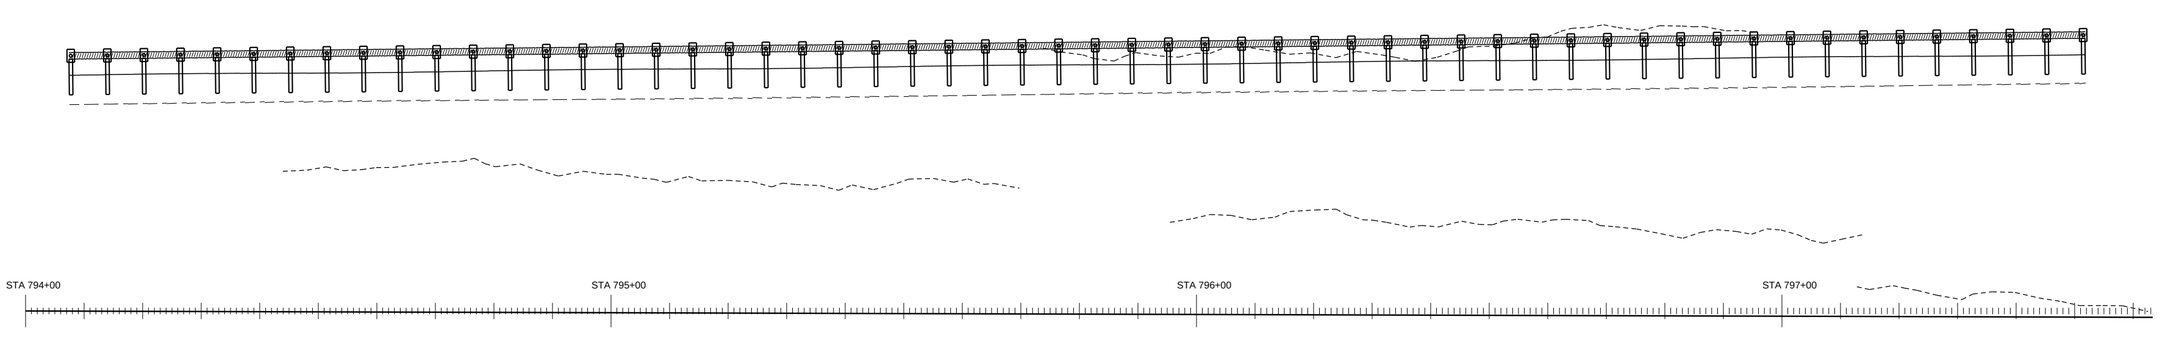


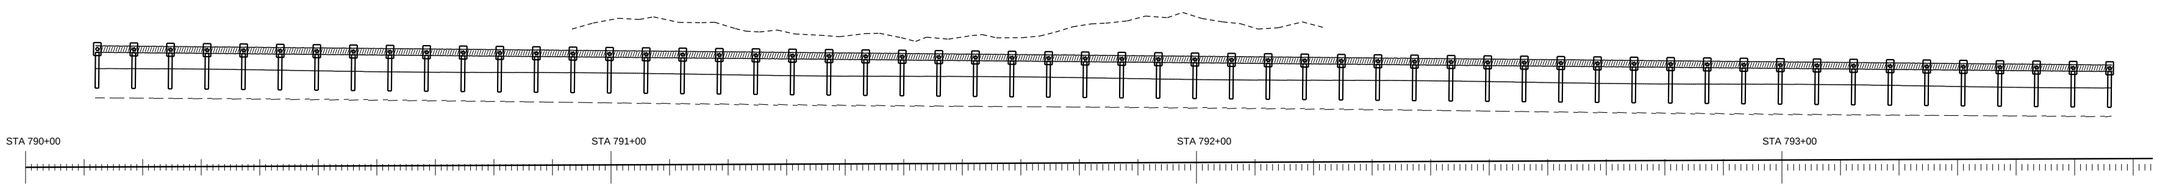


PAY ITEM 536-1-1 GUARDRAIL ROADWAY (TL-3)

PAY ITEM 536-85-24 END TREATMENT

GUARANTEED FENCE CORP

FIN. PROJ. ID 441234-1-52-01

SHEET 47 OF 120

SHEET NO. 147

ROADWAY PLAN SCALE: 1" = 20'

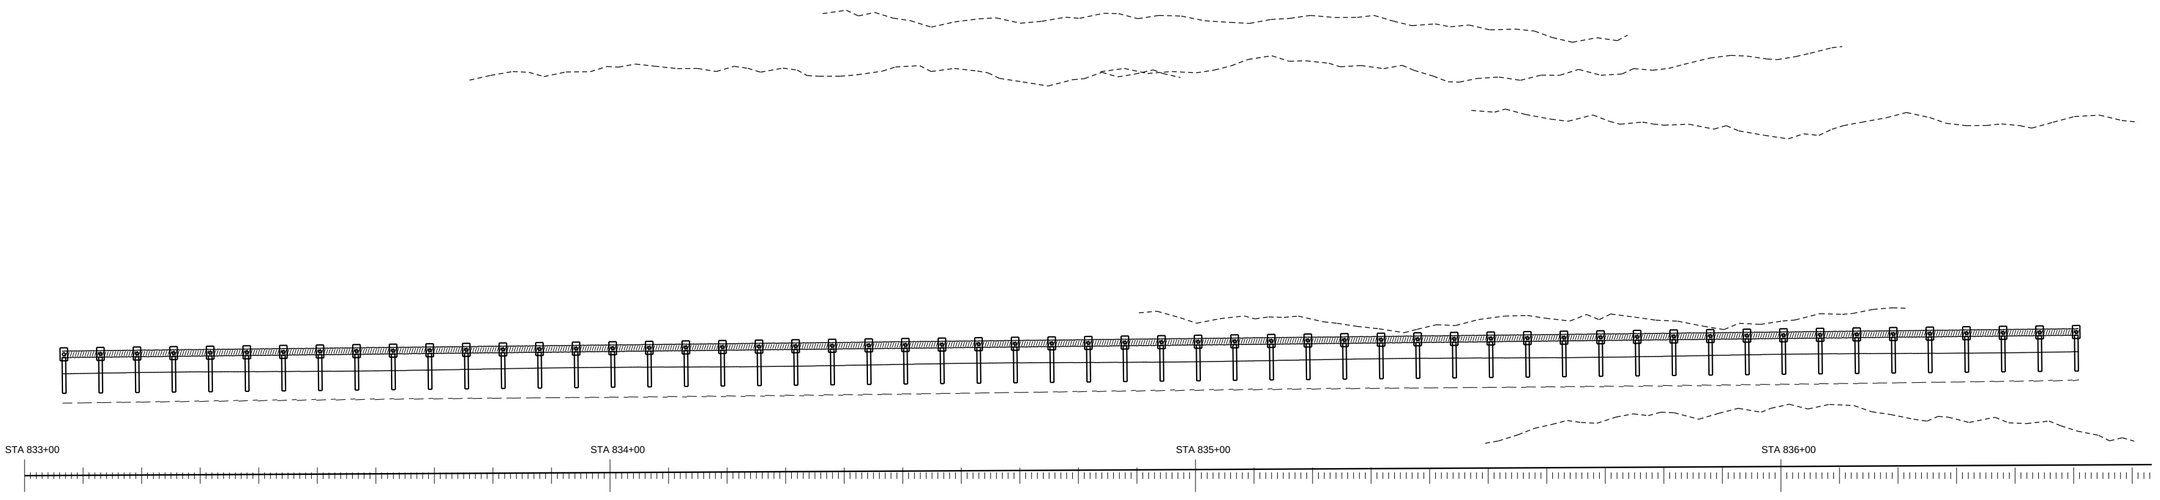


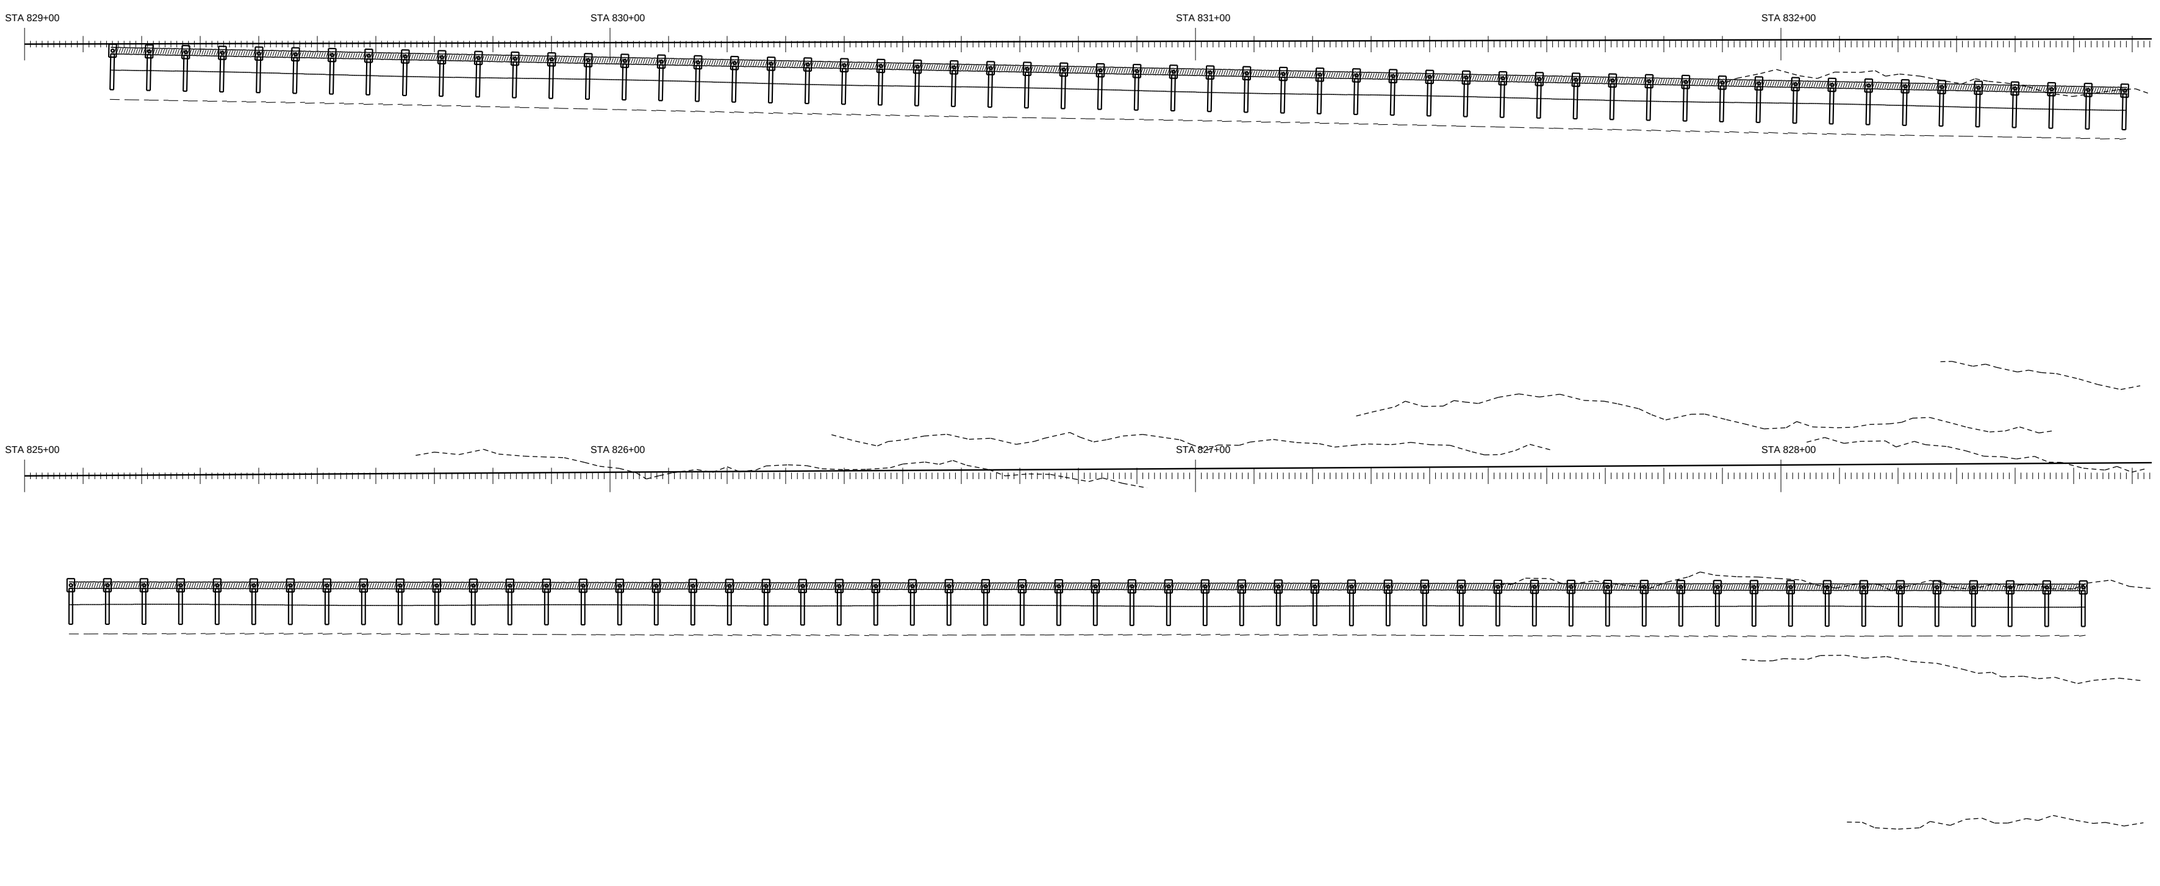


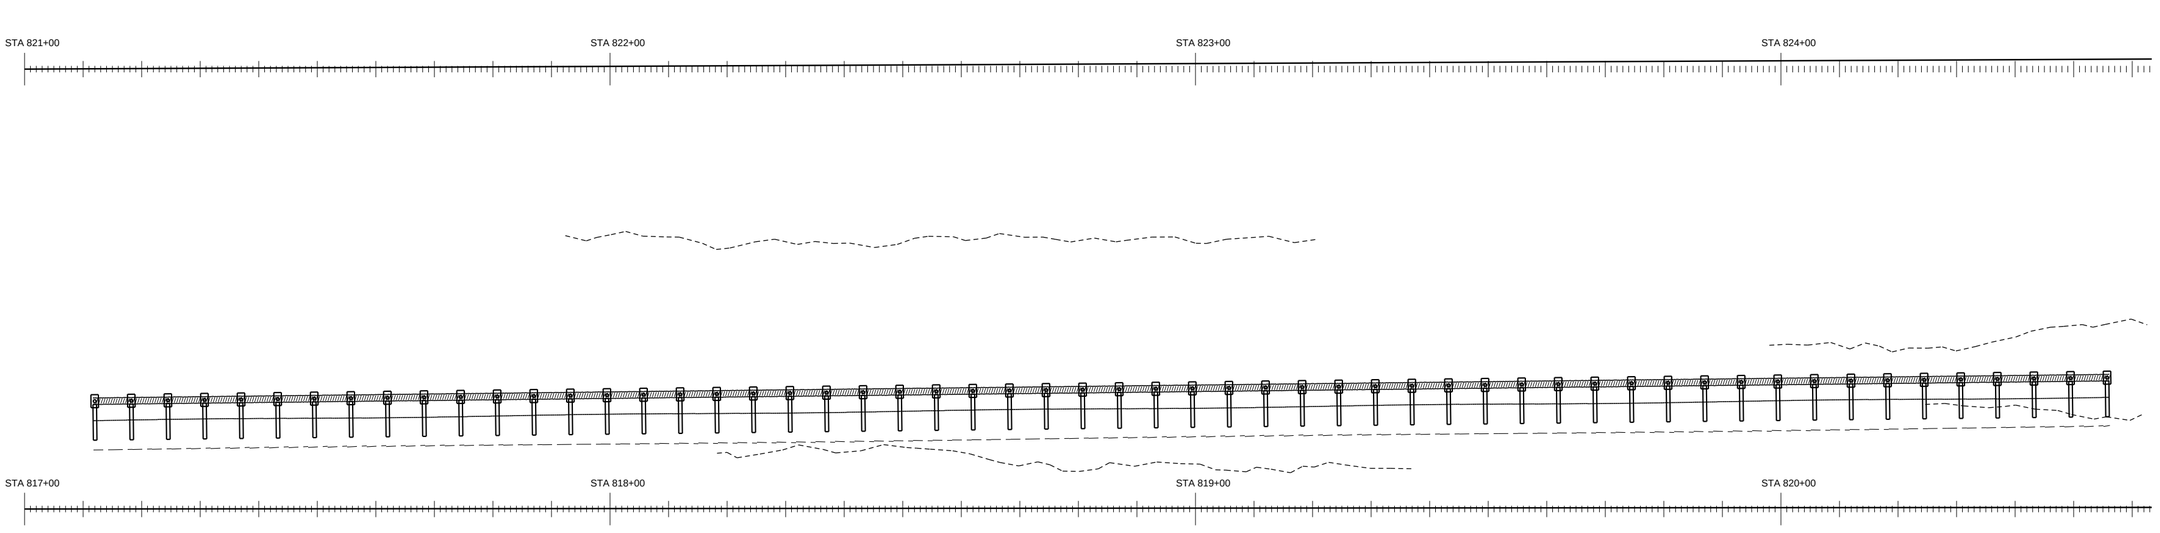


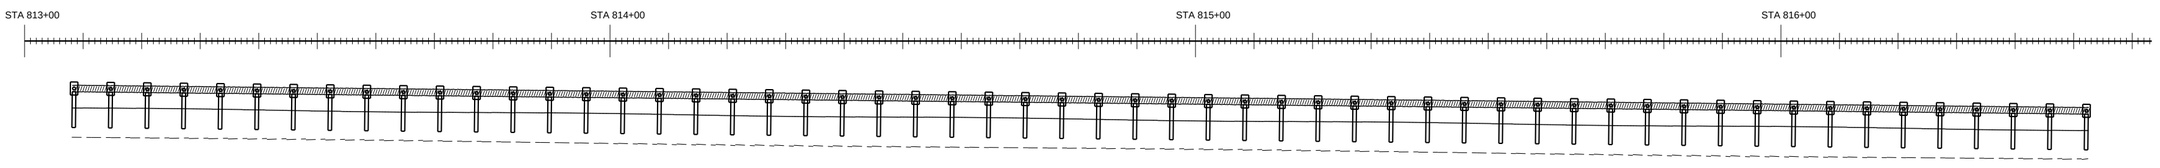


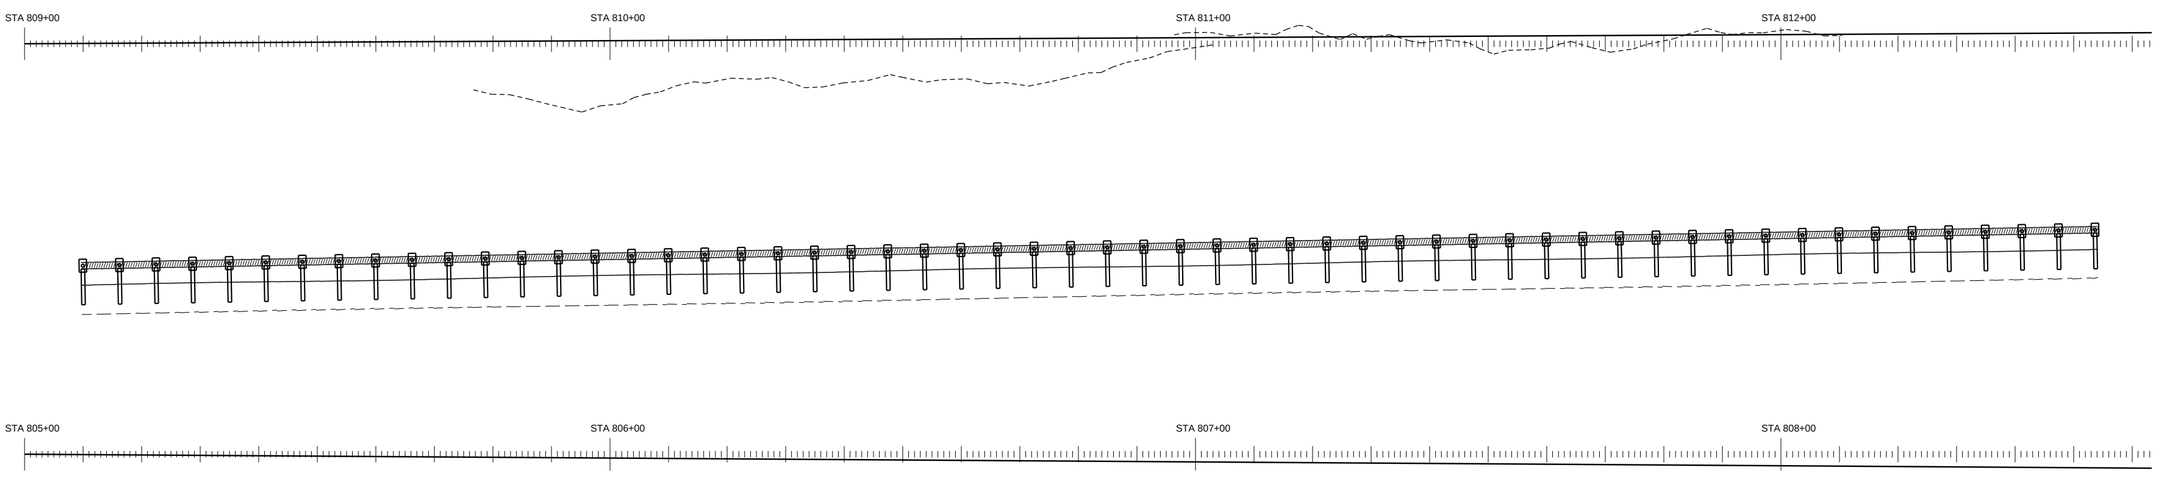


PAY ITEM 536-1-1 GUARDRAIL ROADWAY (TL-3)

PAY ITEM 536-85-24 END TREATMENT

GUARANTEED FENCE CORP

FIN. PROJ. ID 441234-1-52-01

SHEET 48 OF 120

SHEET NO. 148

ROADWAY PLAN SCALE: 1" = 20'

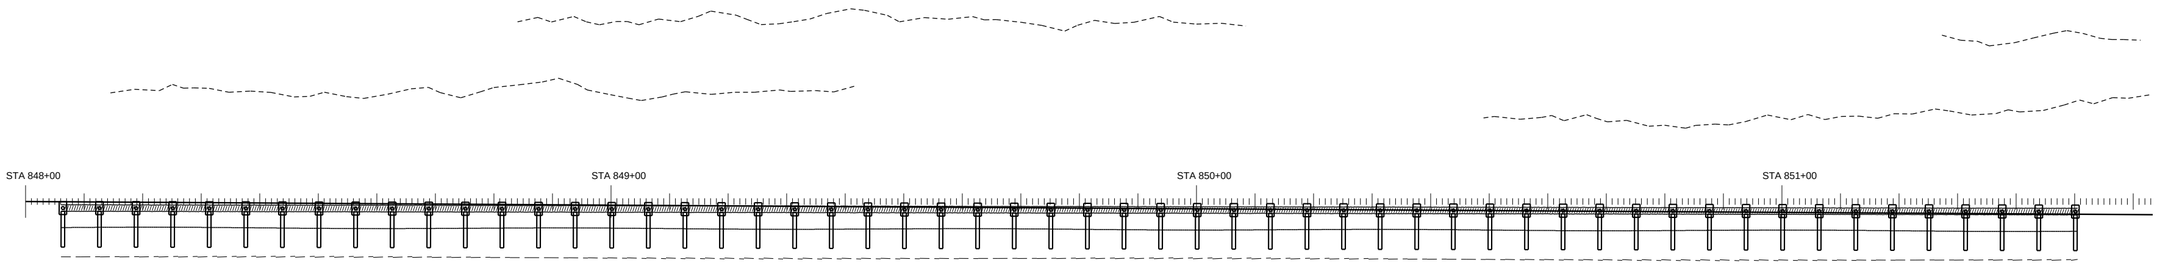


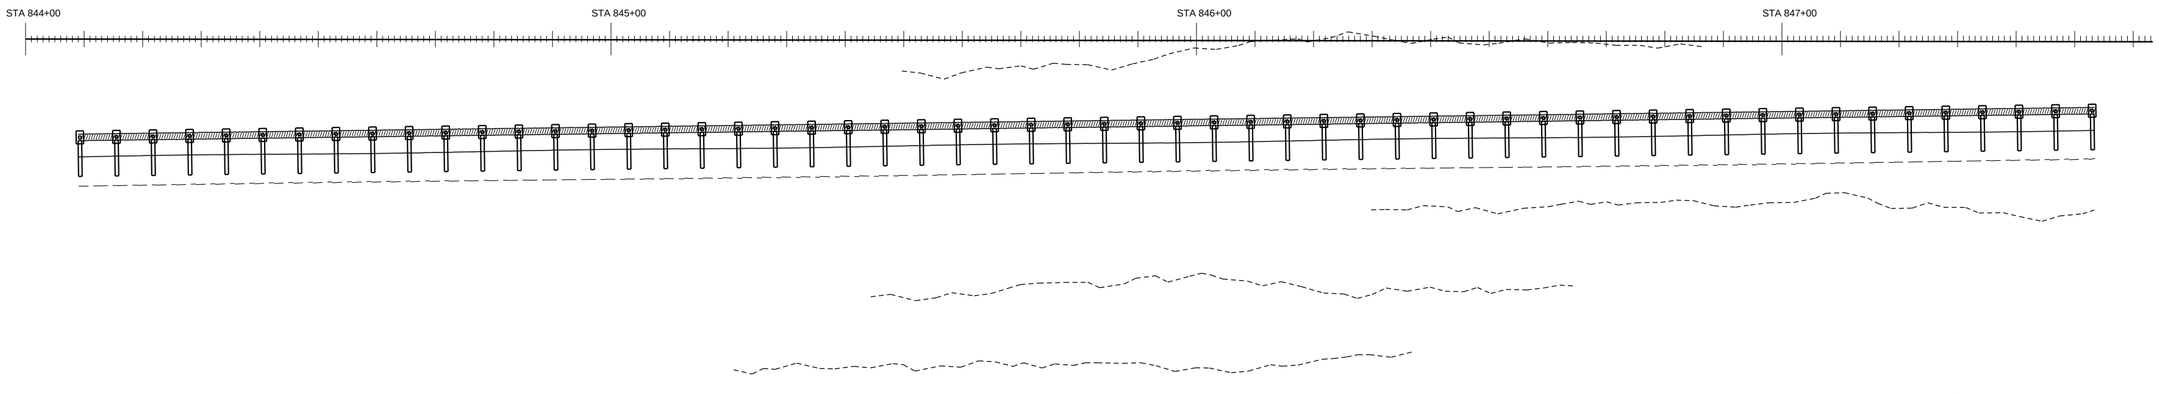


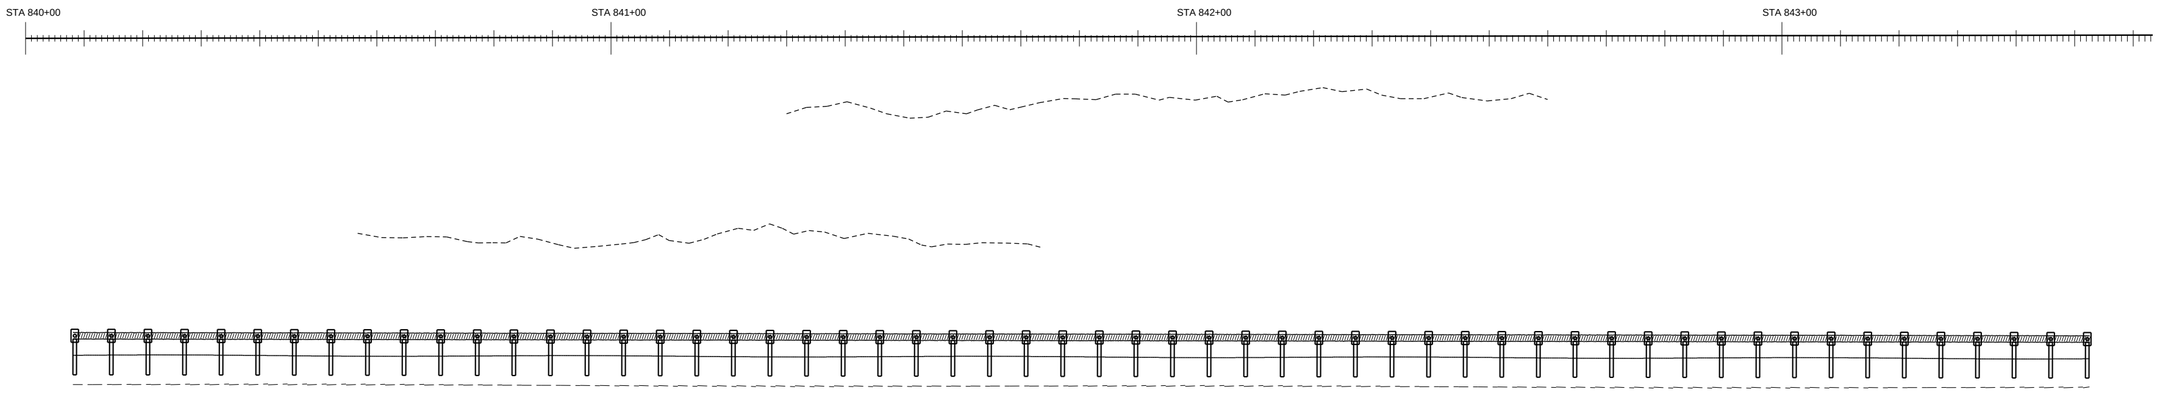


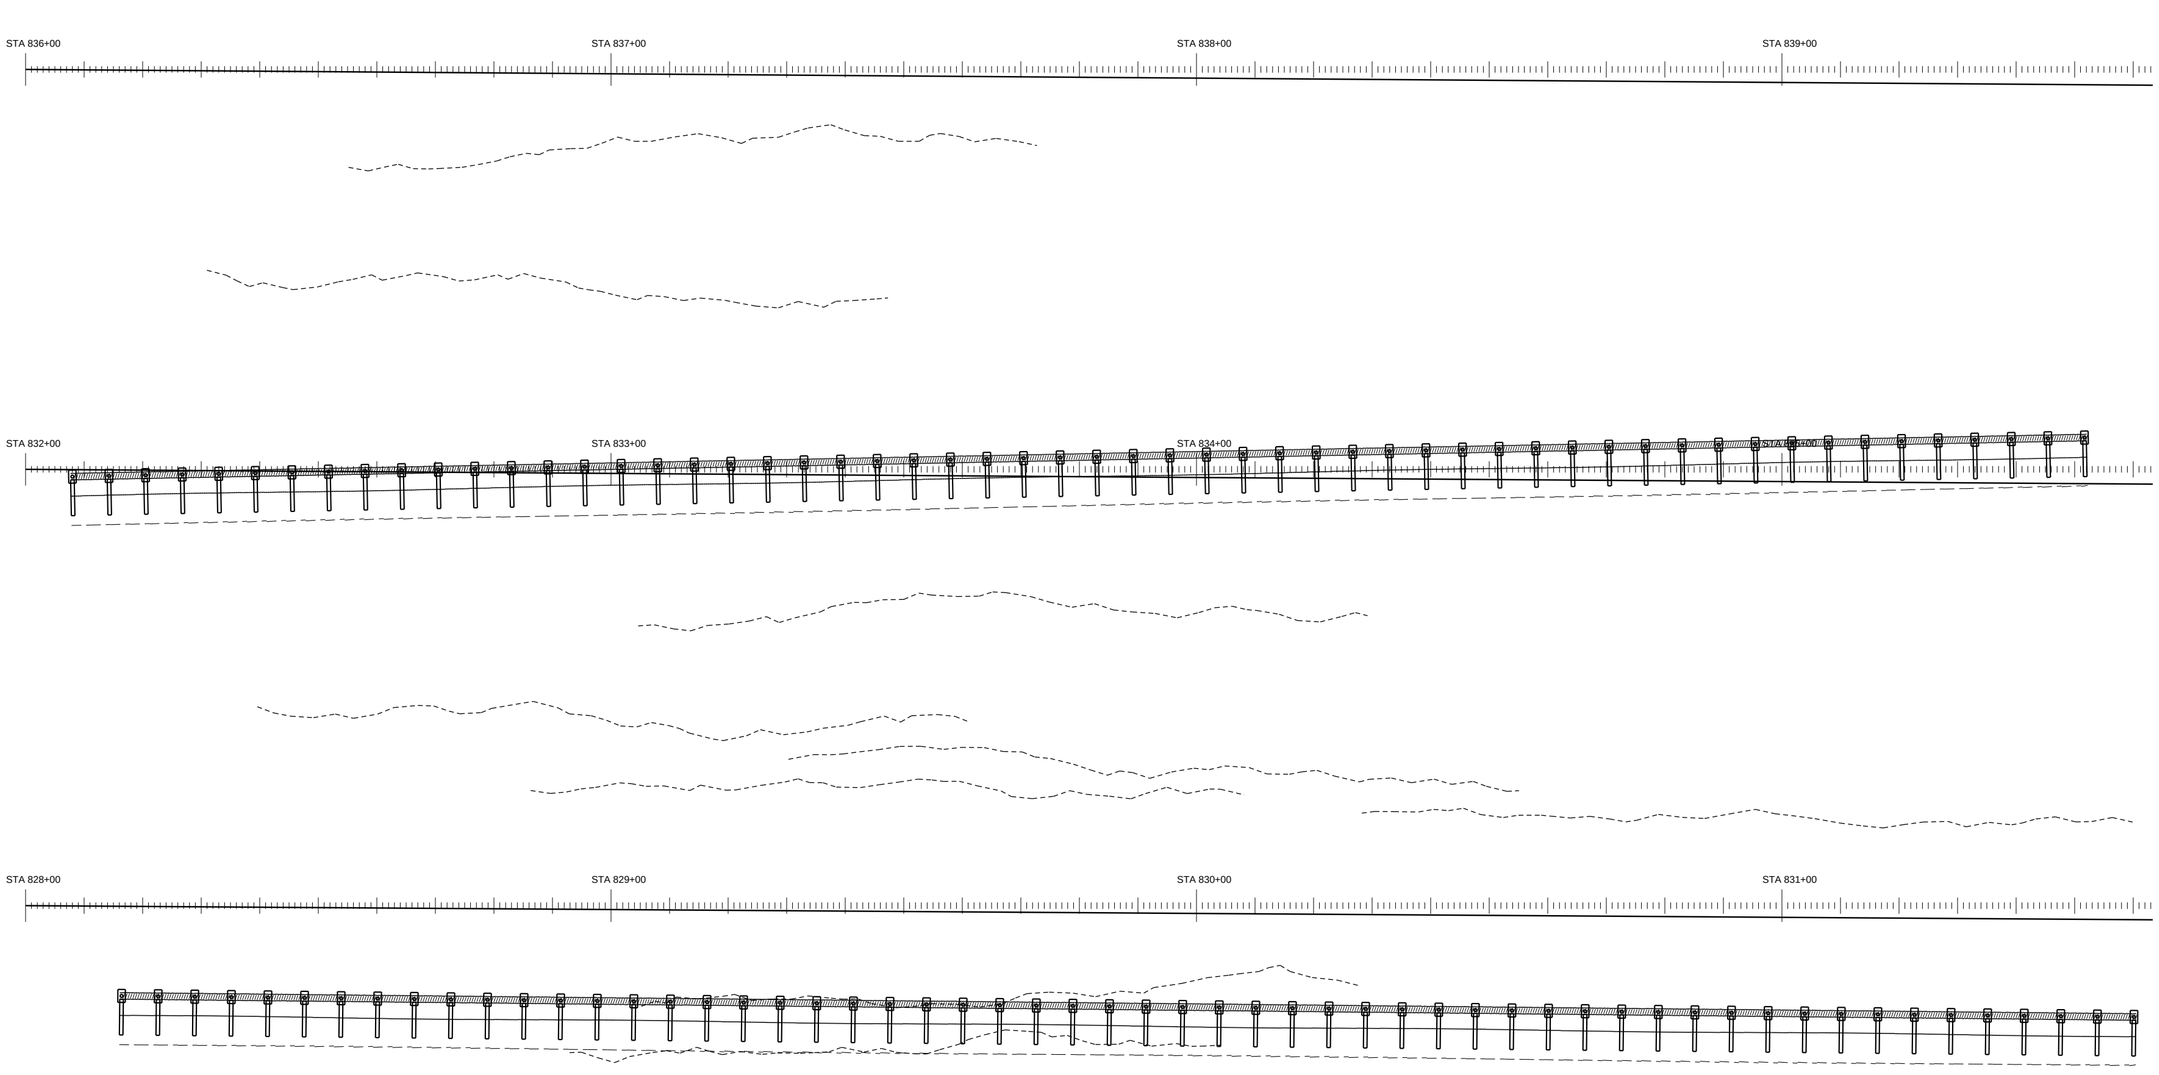








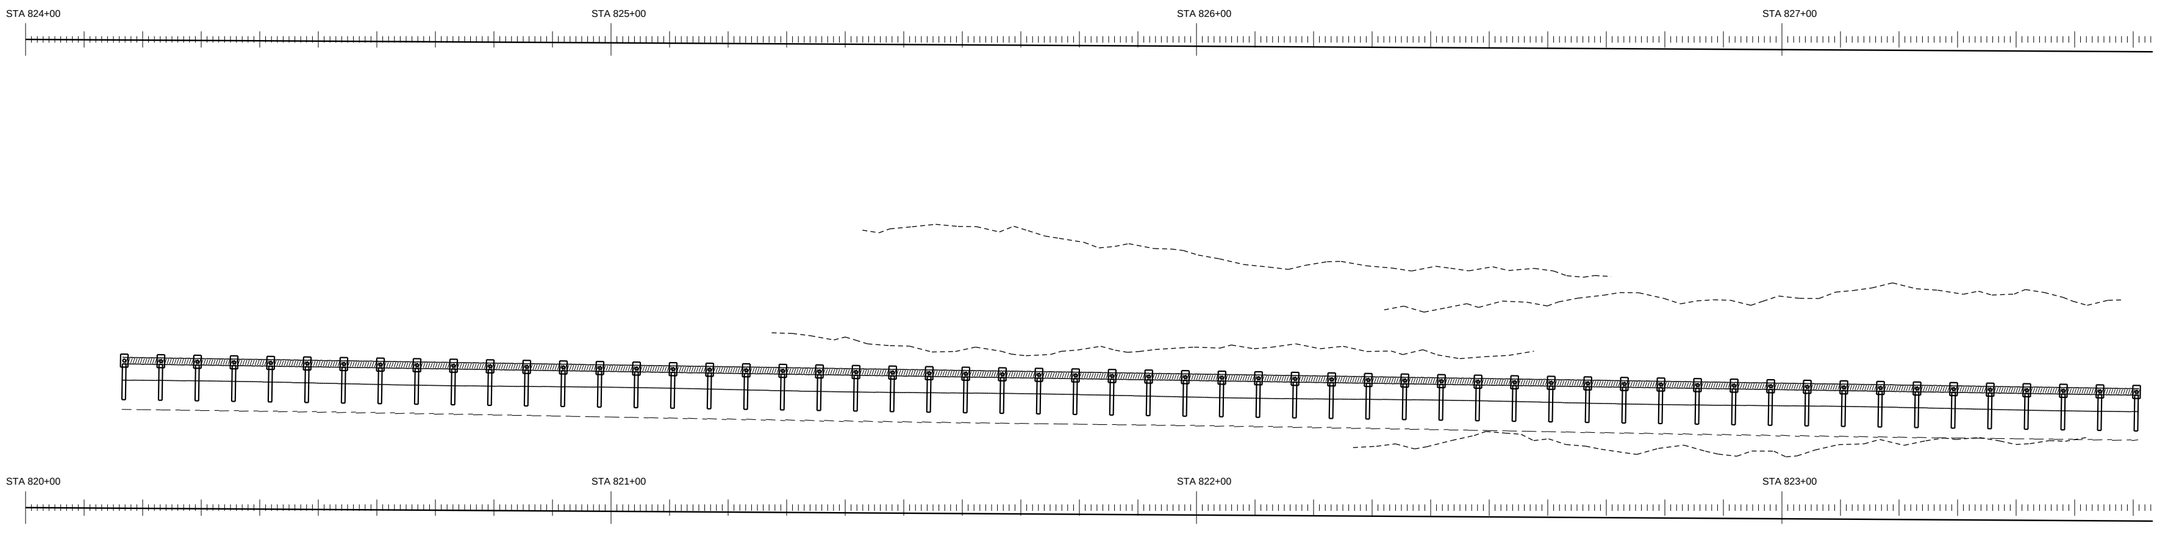


PAY ITEM 536-1-1 GUARDRAIL ROADWAY (TL-3)

PAY ITEM 536-85-24 END TREATMENT

GUARANTEED FENCE CORP

FIN. PROJ. ID 441234-1-52-01

SHEET 49 OF 120

SHEET NO. 149

ROADWAY PLAN SCALE: 1" = 20'




PAY ITEM 536-1-1 GUARDRAIL ROADWAY (TL-3)

PAY ITEM 536-85-24 END TREATMENT

GUARANTEED FENCE CORP

FIN. PROJ. ID 441234-1-52-01

SHEET 50 OF 120

SHEET NO. 150

ROADWAY PLAN SCALE: 1" = 20'

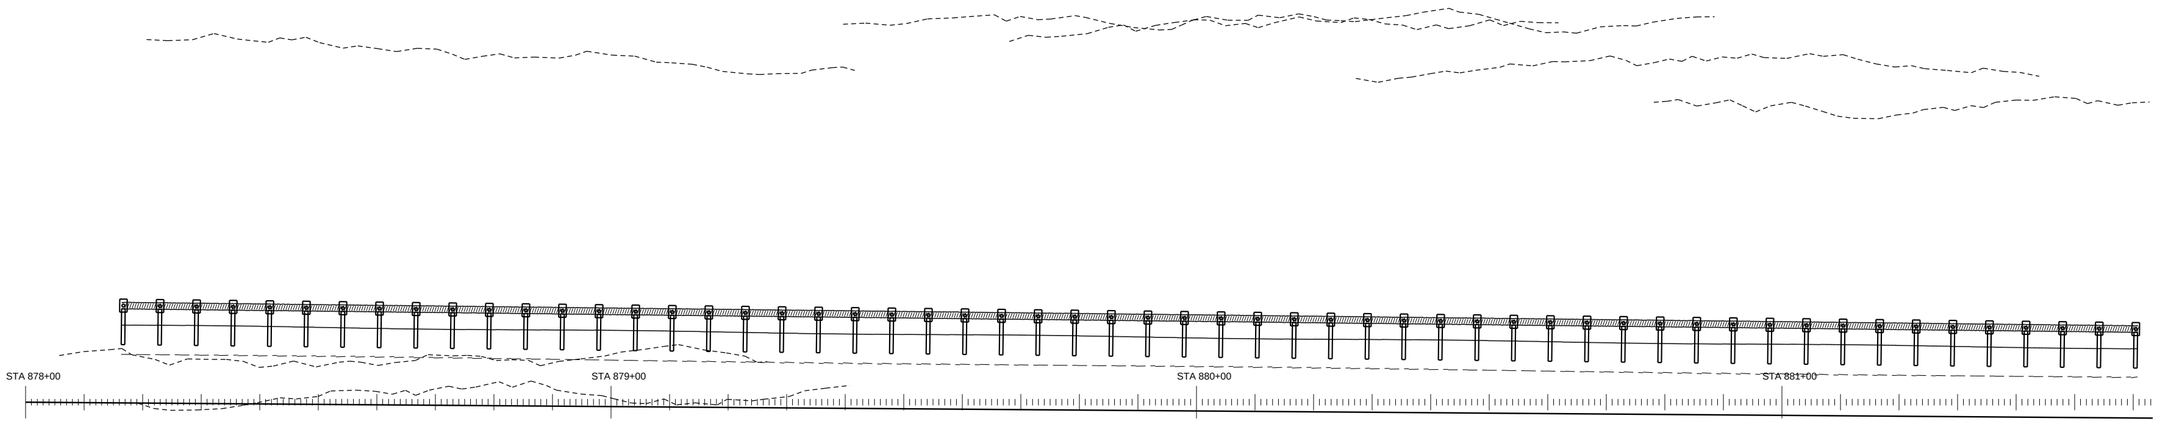





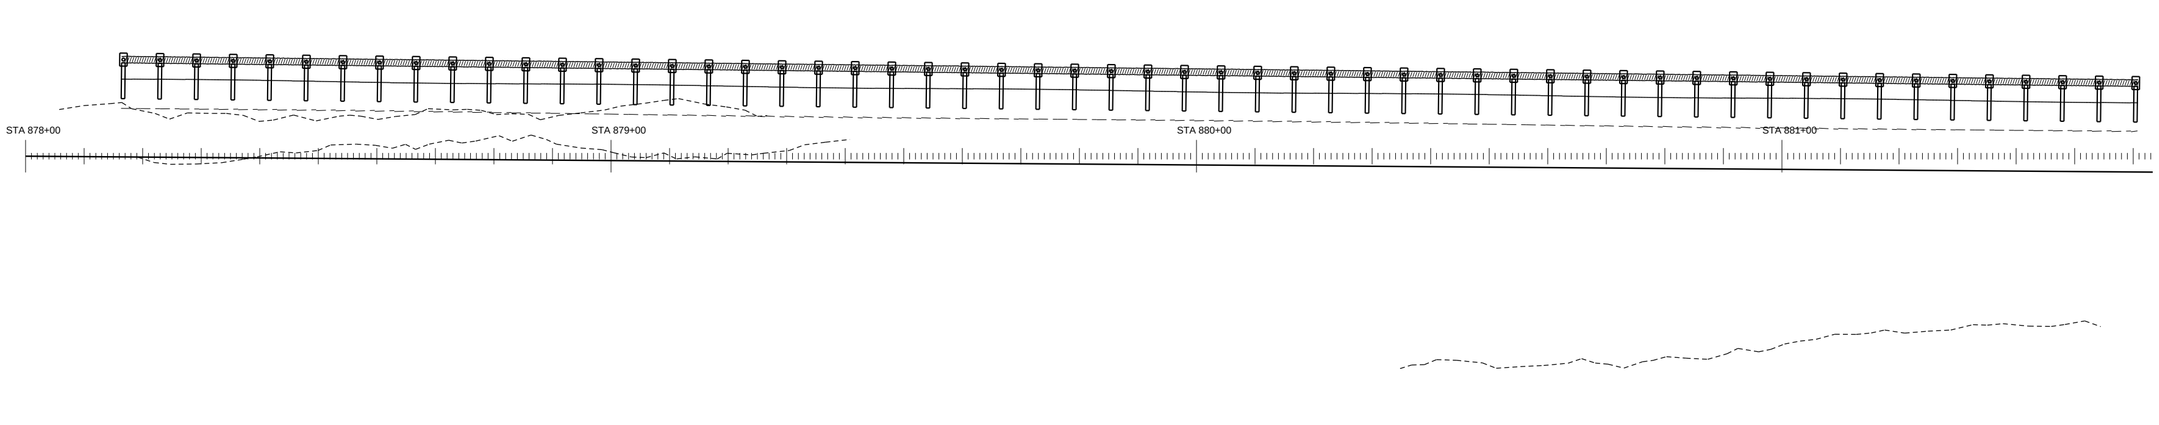

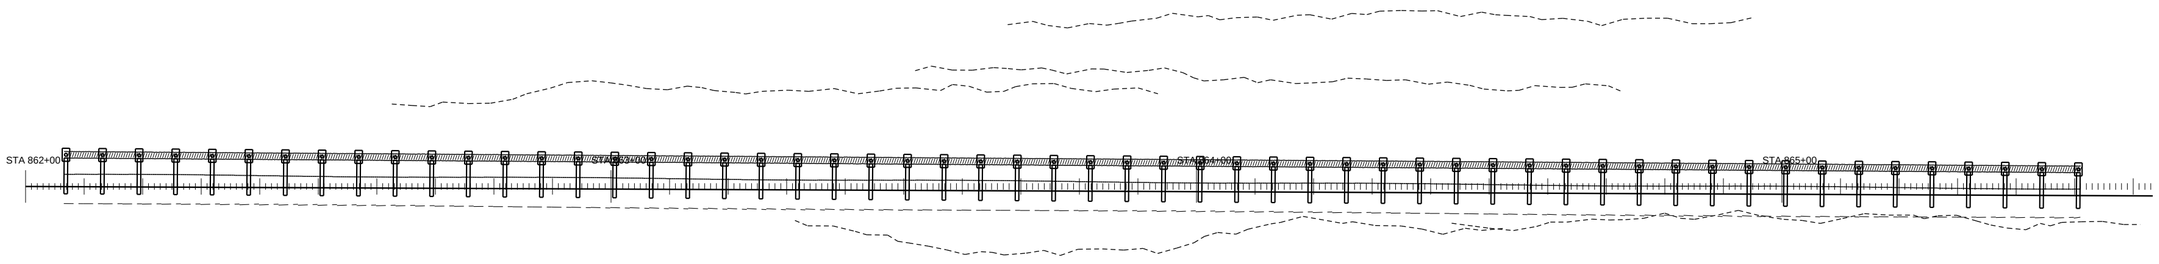


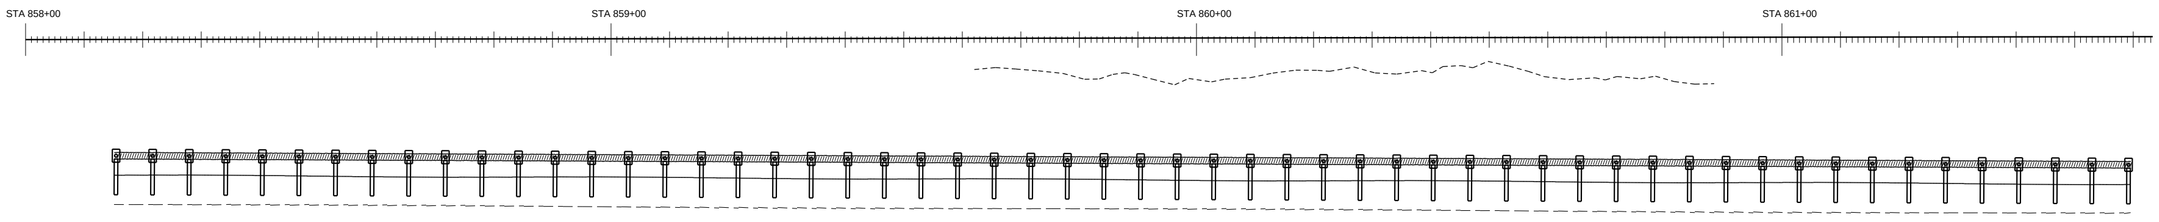


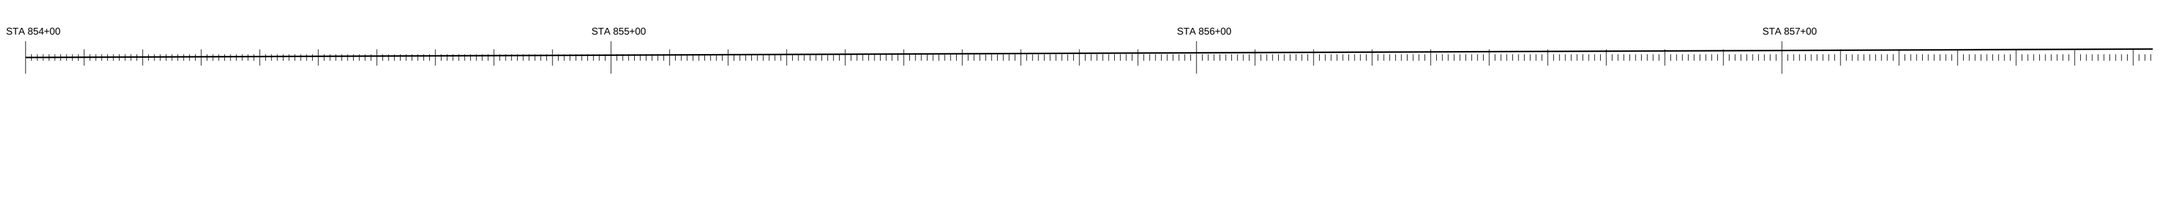

PAY ITEM 536-1-1 GUARDRAIL ROADWAY (TL-3)

PAY ITEM 536-85-24 END TREATMENT

GUARANTEED FENCE CORP

FIN. PROJ. ID 441234-1-52-01

SHEET 51 OF 120

SHEET NO. 151

ROADWAY PLAN SCALE: 1" = 20'

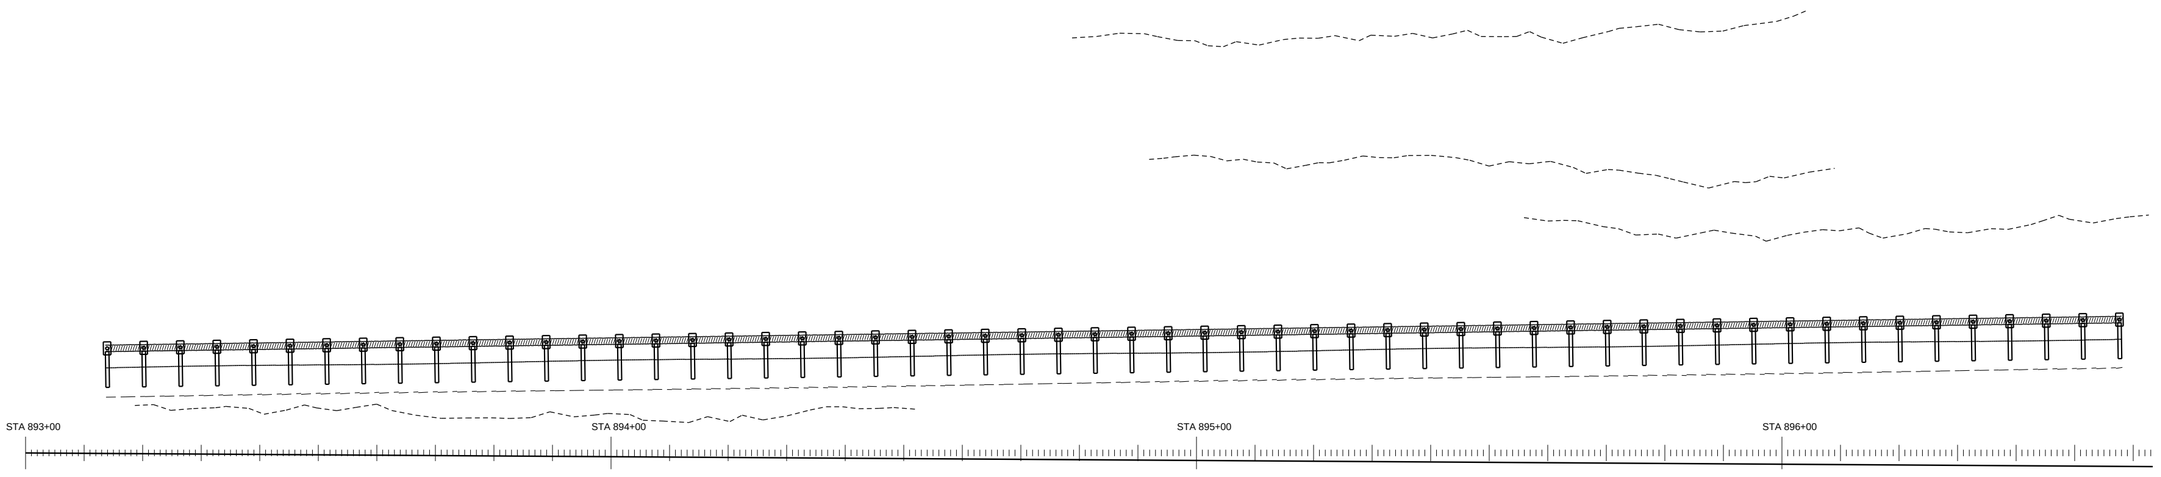


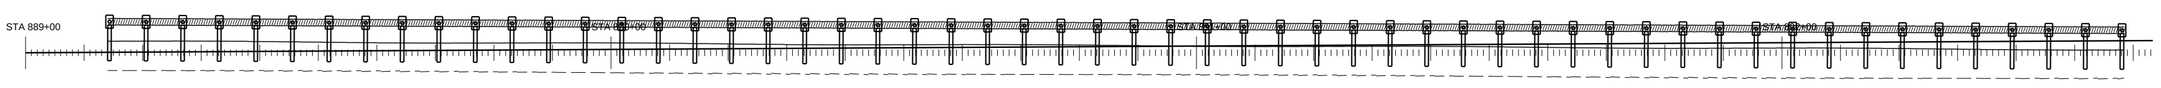


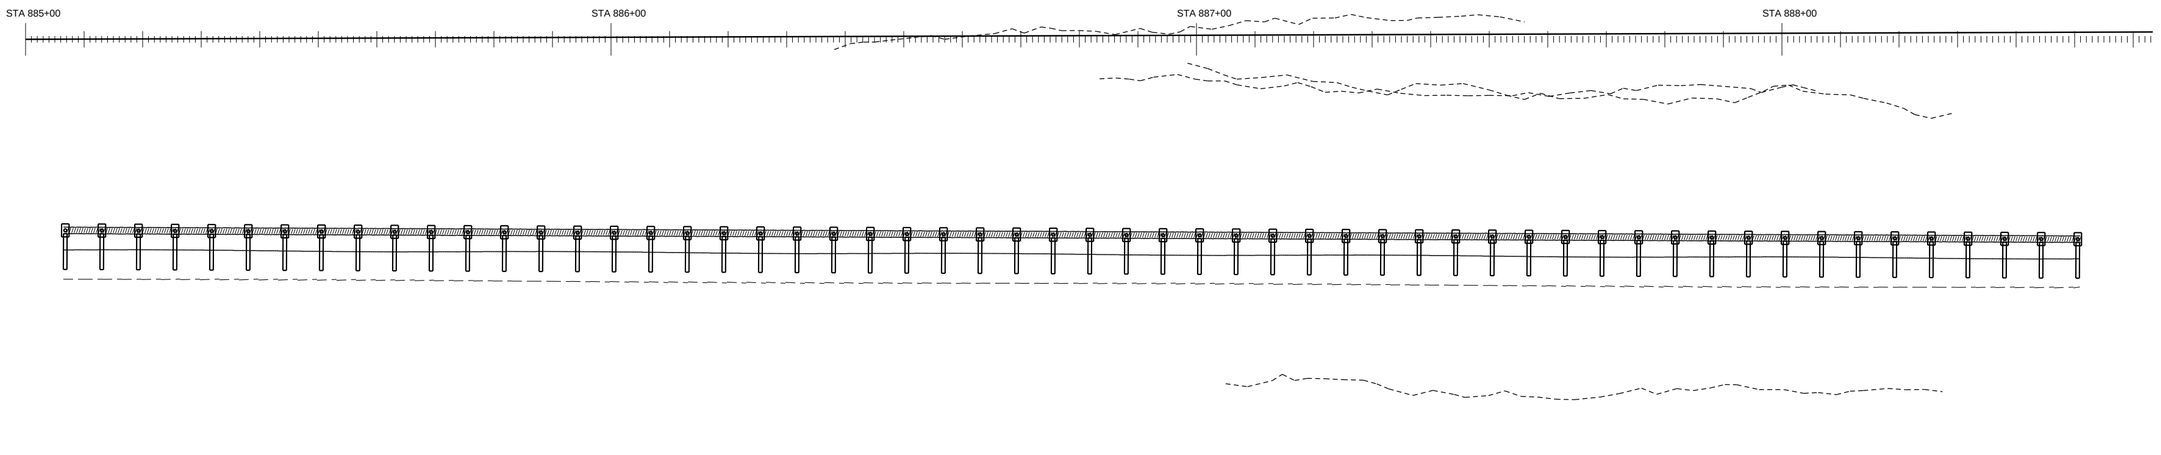


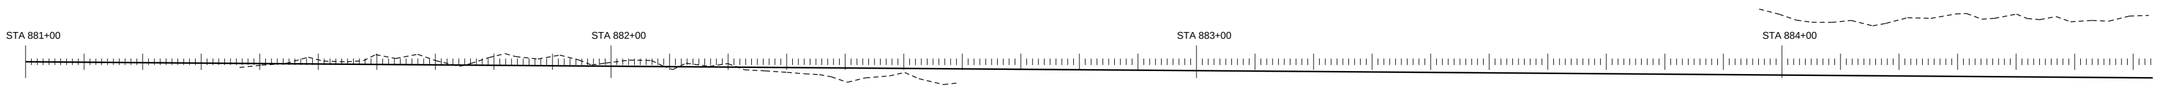


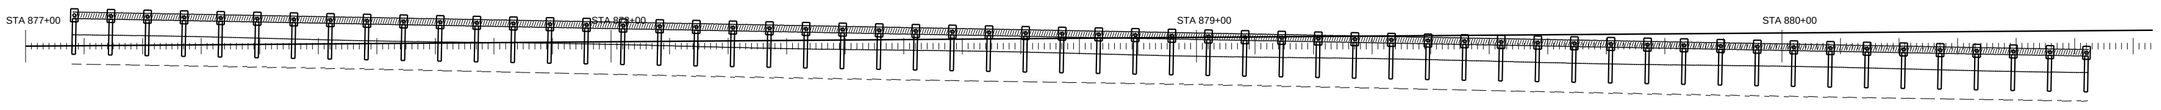


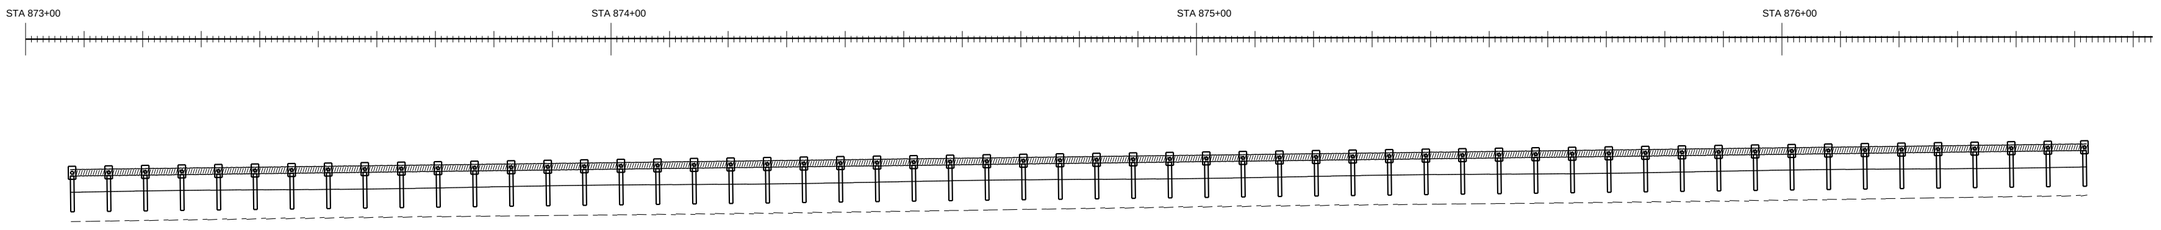


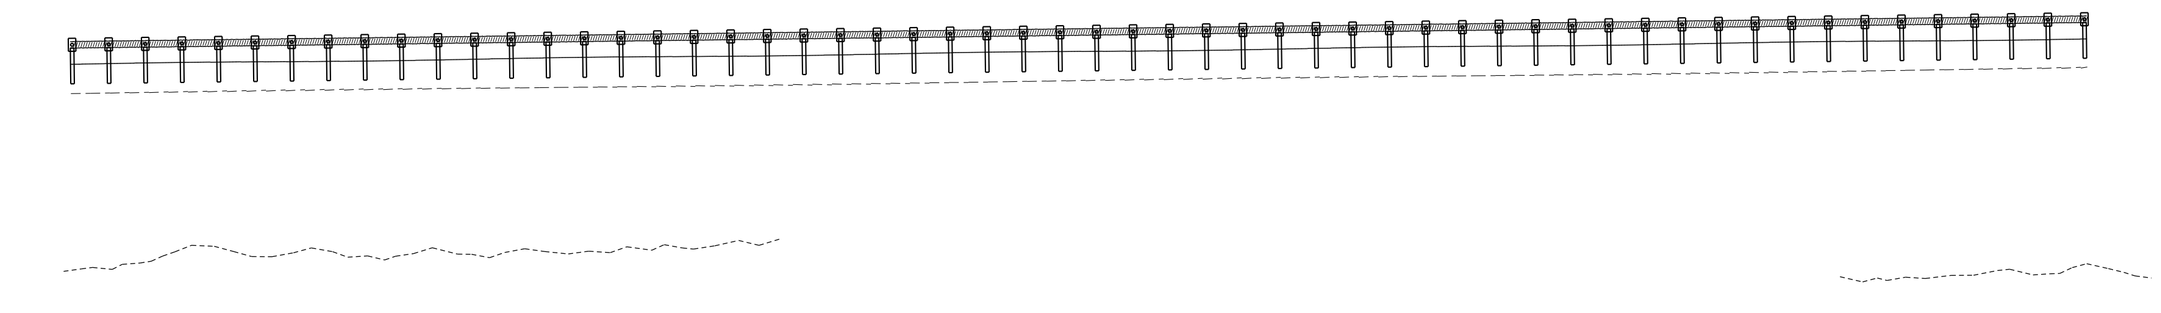


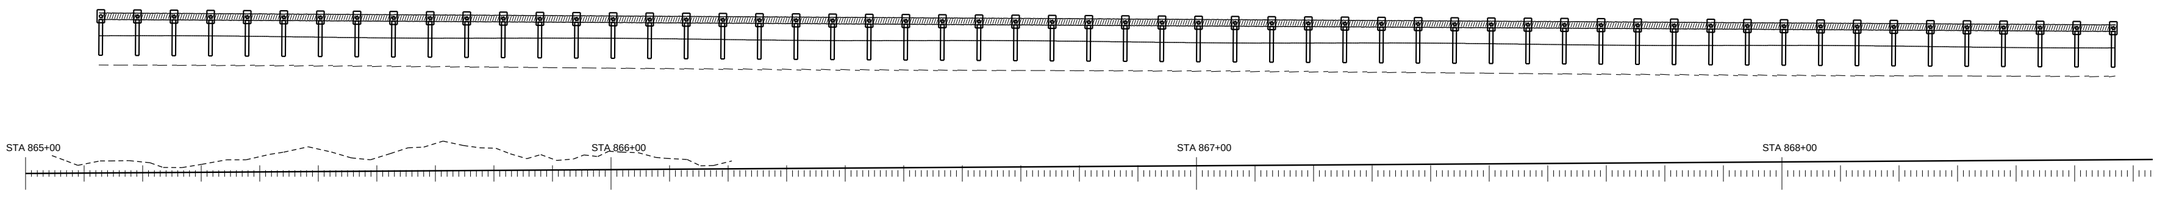


PAY ITEM 536-1-1 GUARDRAIL ROADWAY (TL-3)

PAY ITEM 536-85-24 END TREATMENT

GUARANTEED FENCE CORP

FIN. PROJ. ID 441234-1-52-01

SHEET 52 OF 120

SHEET NO. 152

ROADWAY PLAN SCALE: 1" = 20'

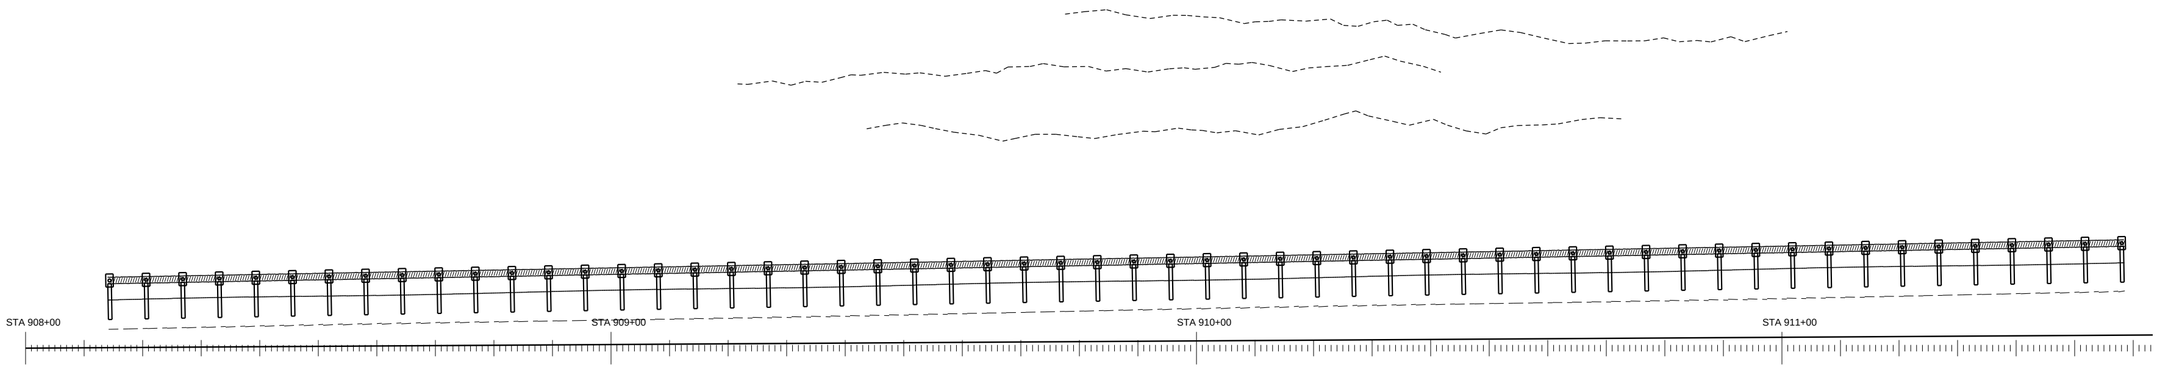

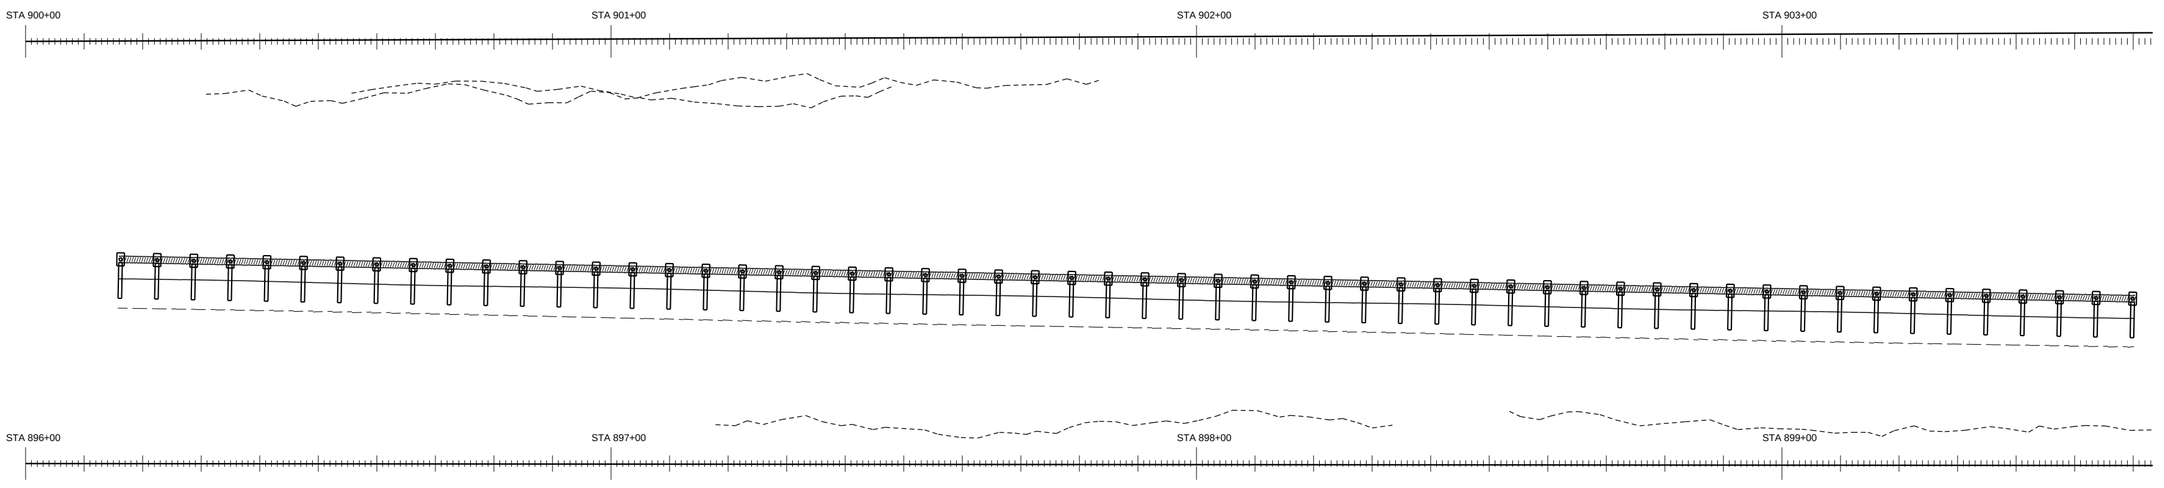





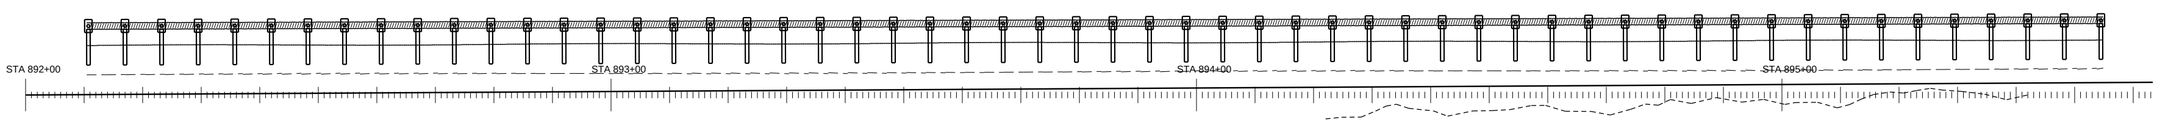


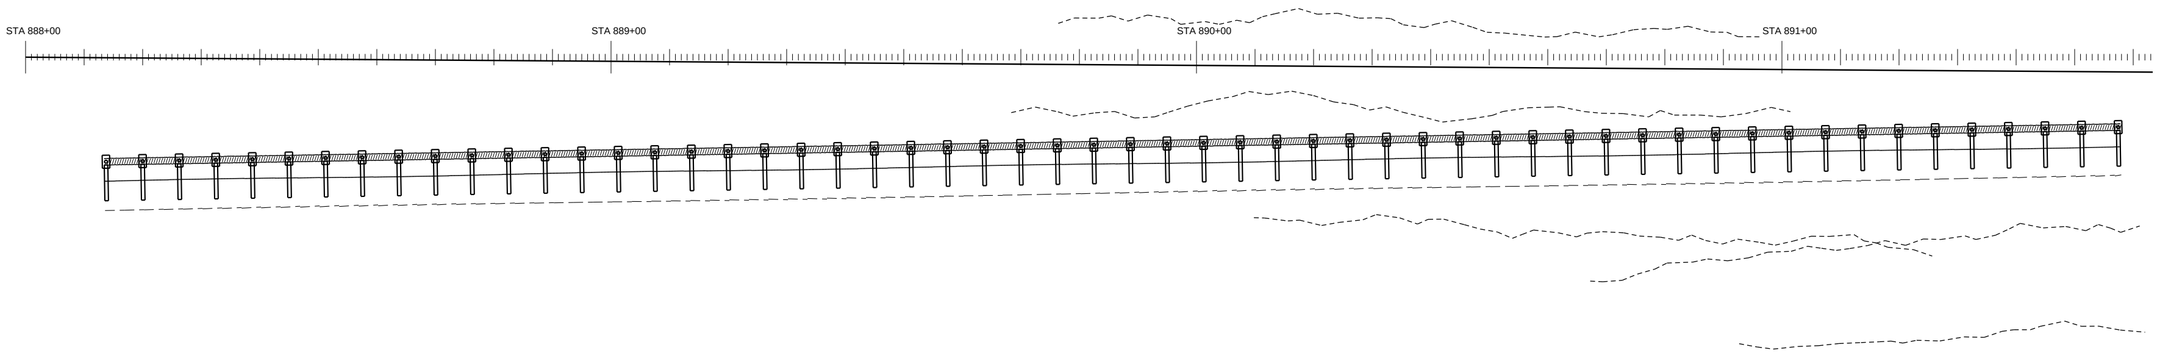


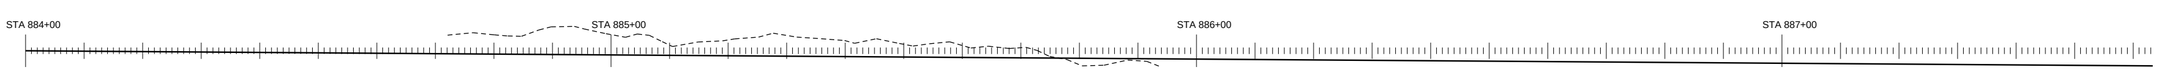


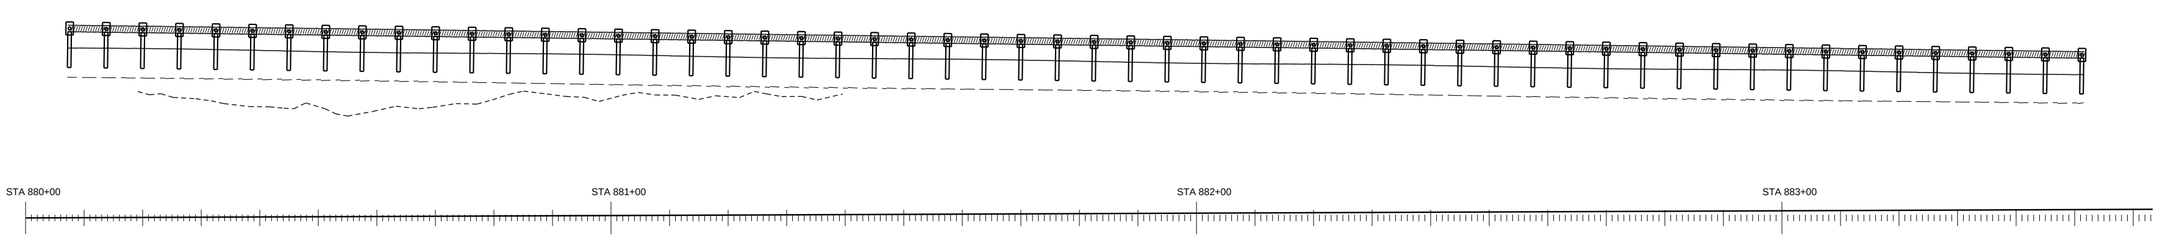


PAY ITEM 536-1-1 GUARDRAIL ROADWAY (TL-3)

PAY ITEM 536-85-24 END TREATMENT

GUARANTEED FENCE CORP

FIN. PROJ. ID 441234-1-52-01

SHEET 53 OF 120

SHEET NO. 153

ROADWAY PLAN SCALE: 1" = 20'

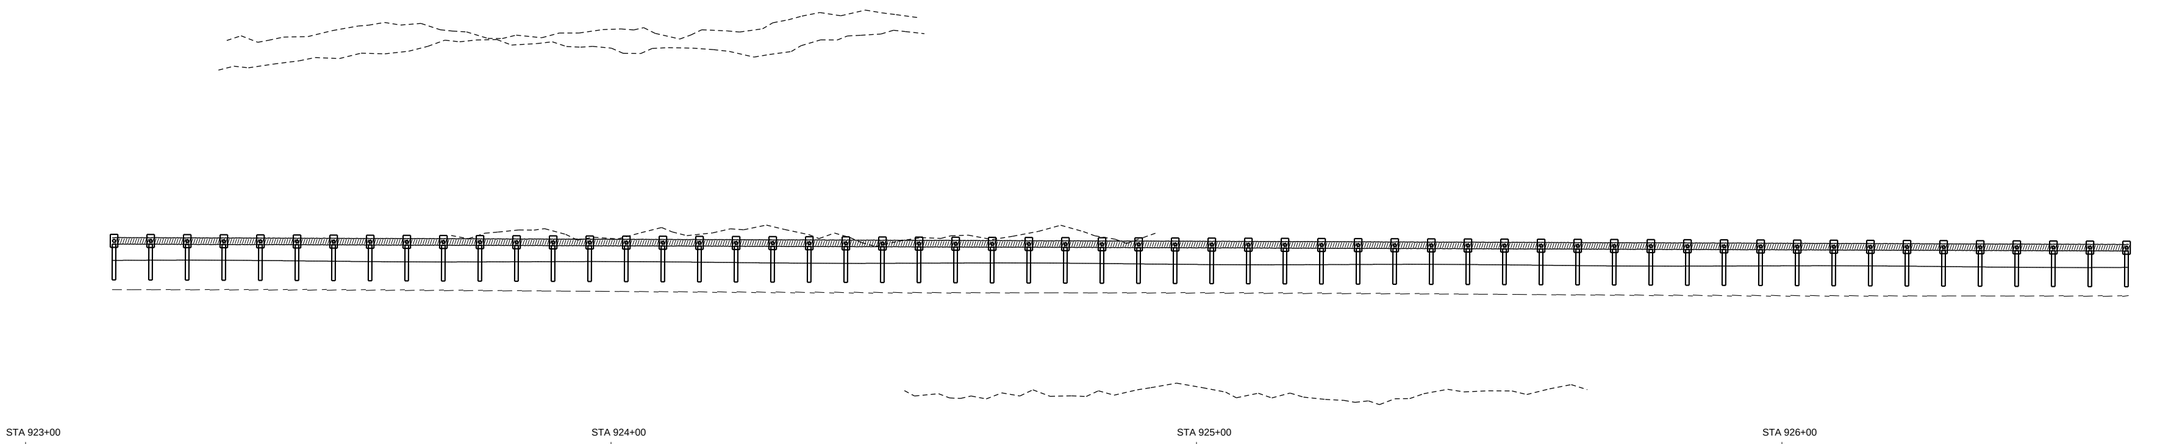


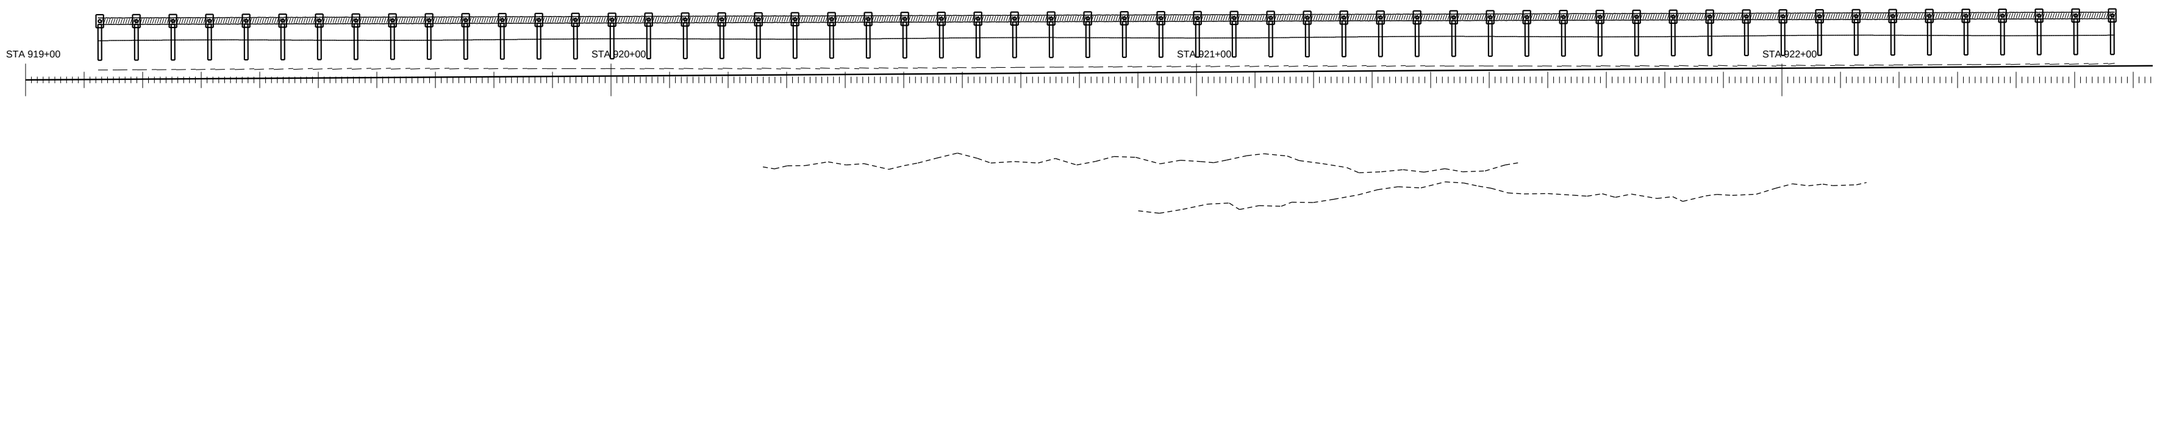


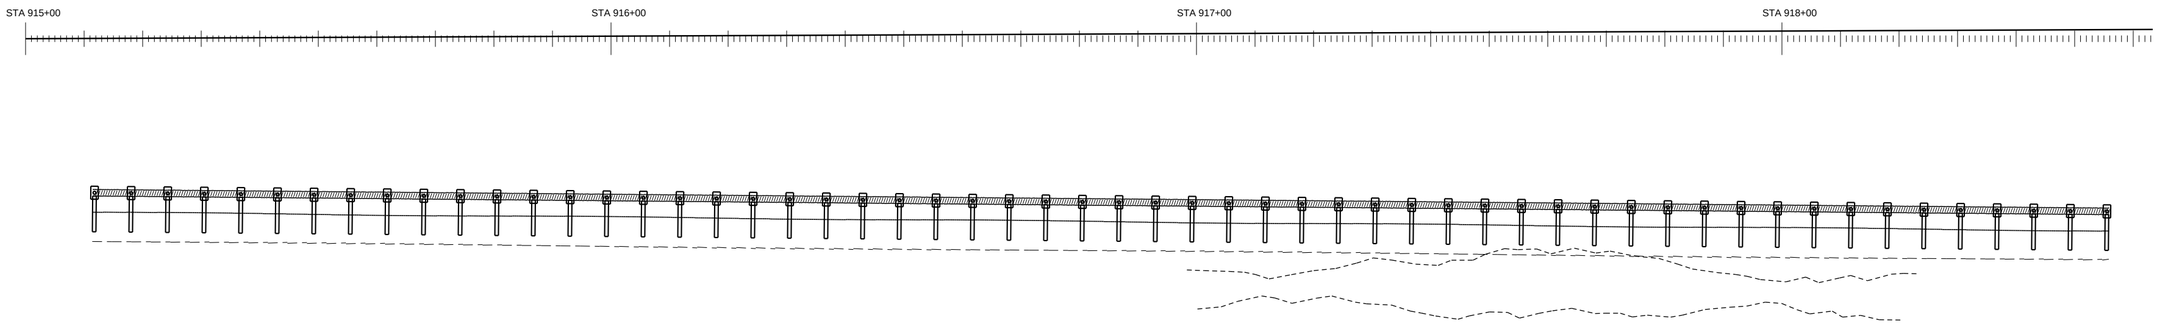


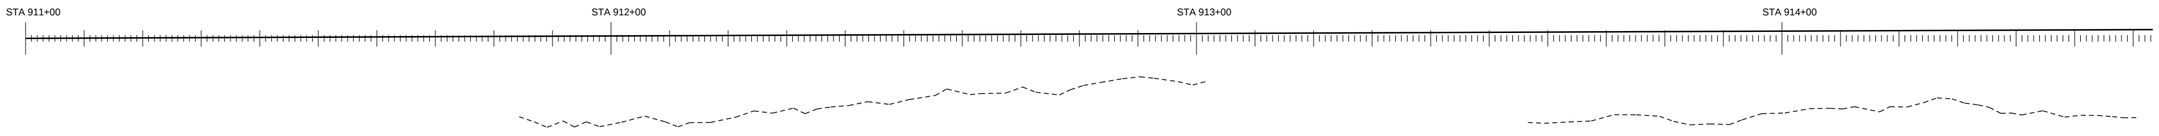


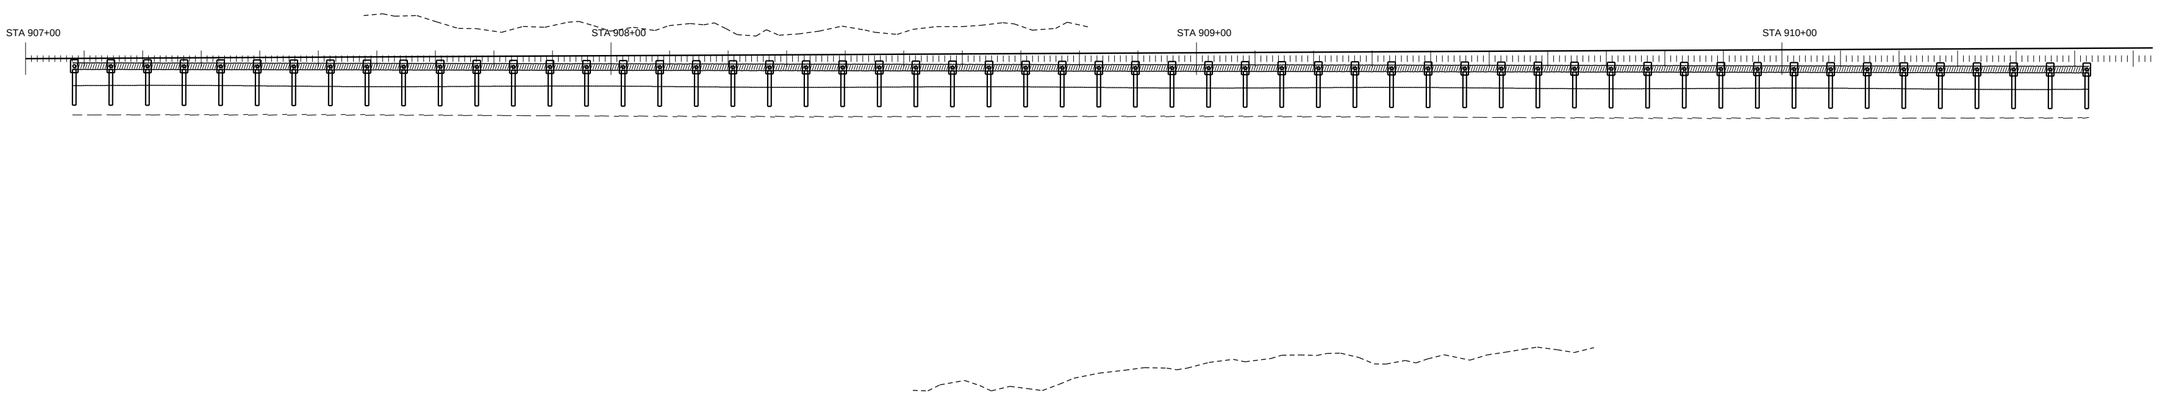


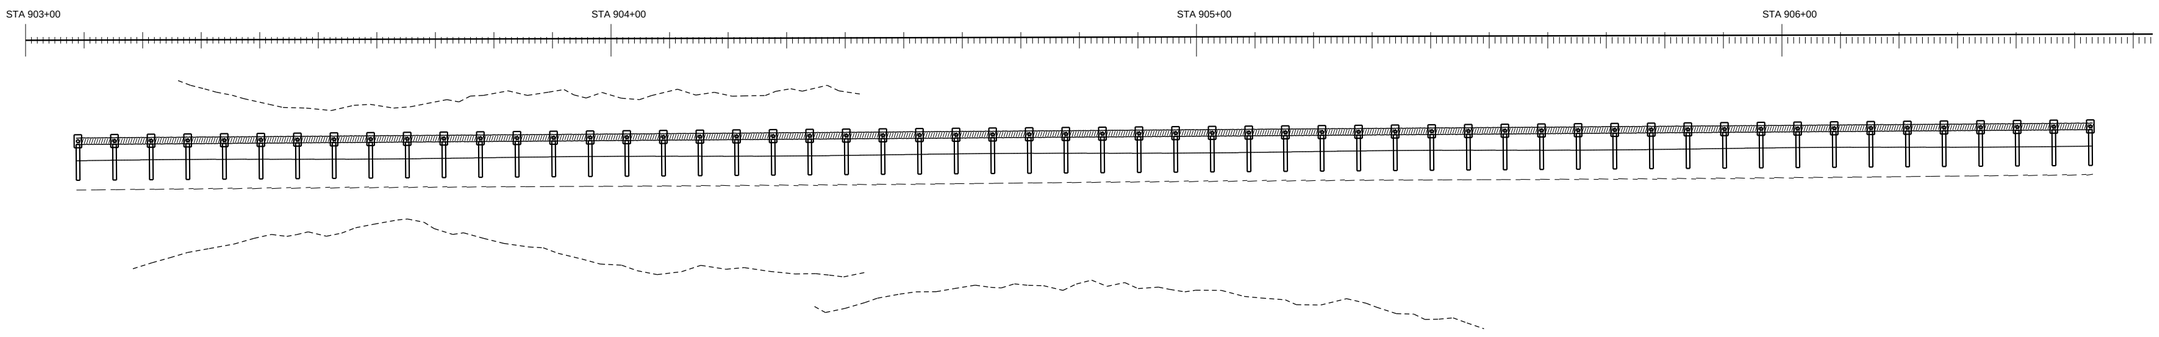


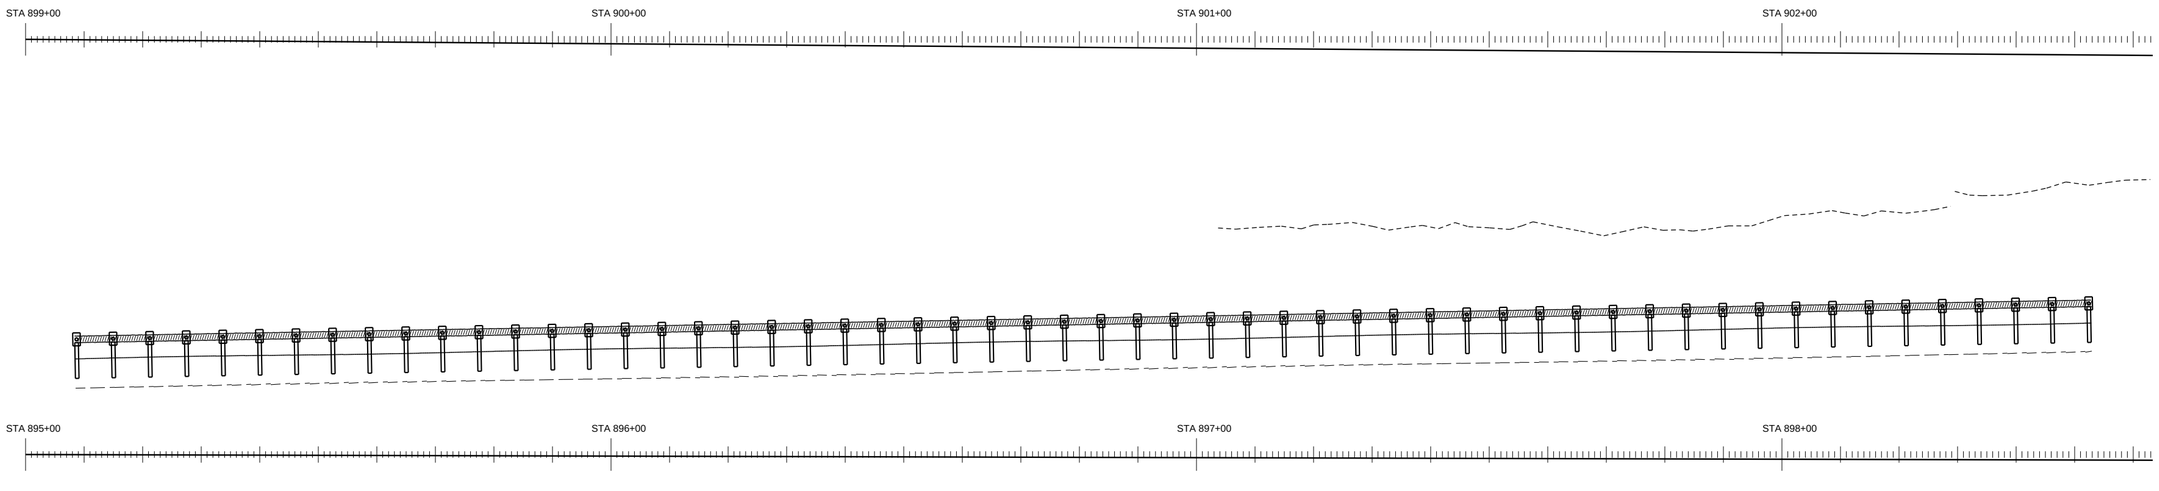


PAY ITEM 536-1-1 GUARDRAIL ROADWAY (TL-3)

PAY ITEM 536-85-24 END TREATMENT

GUARANTEED FENCE CORP

FIN. PROJ. ID 441234-1-52-01

SHEET 54 OF 120

SHEET NO. 154

ROADWAY PLAN SCALE: 1" = 20'




PAY ITEM 536-1-1 GUARDRAIL ROADWAY (TL-3)

PAY ITEM 536-85-24 END TREATMENT

GUARANTEED FENCE CORP

FIN. PROJ. ID 441234-1-52-01

SHEET 55 OF 120

SHEET NO. 155

ROADWAY PLAN SCALE: 1" = 20'

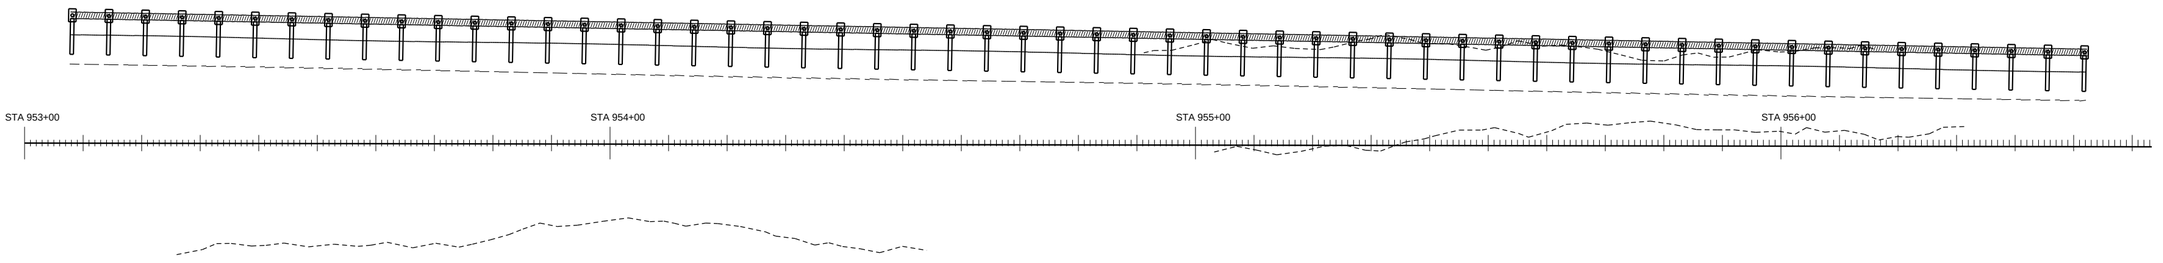


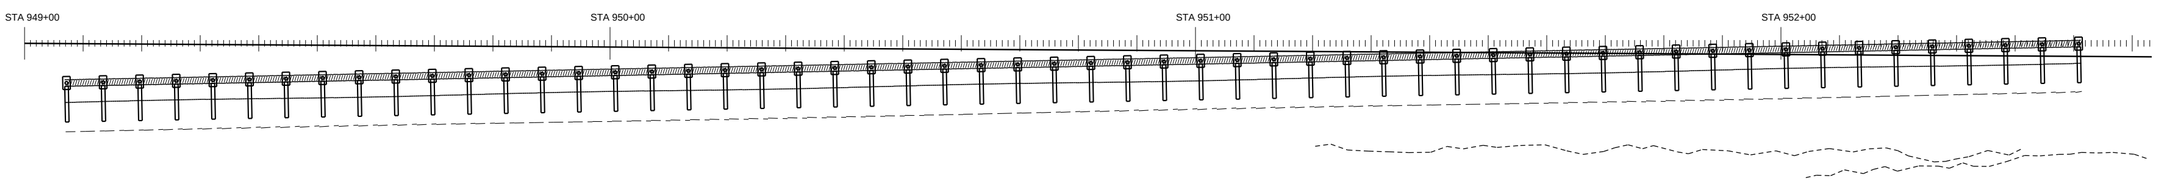


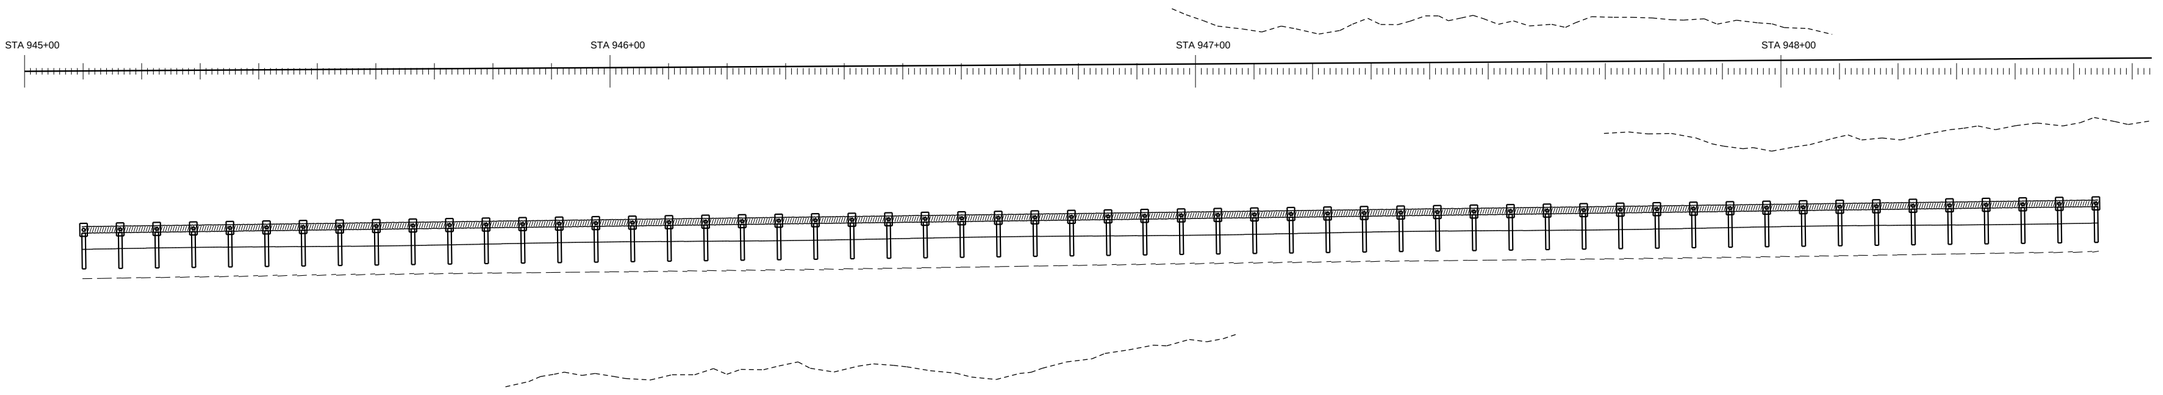


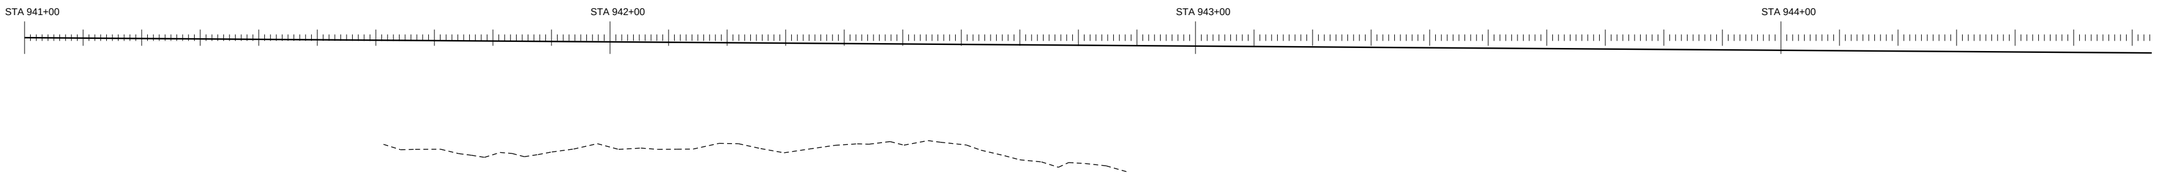


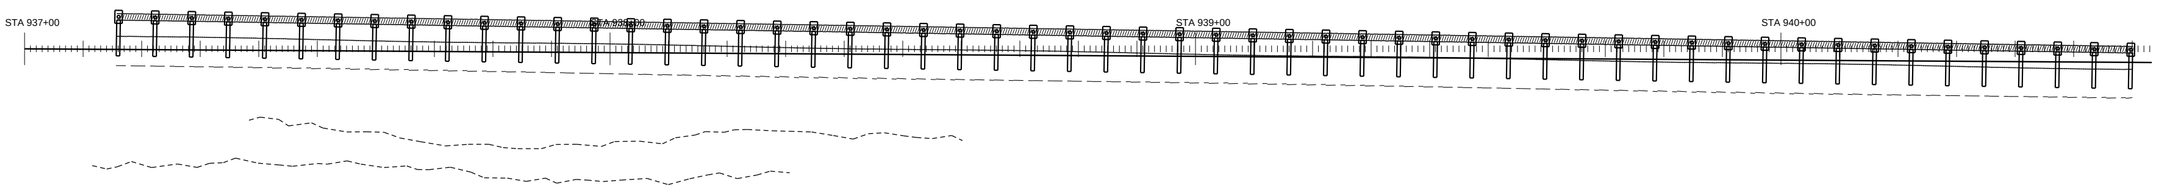


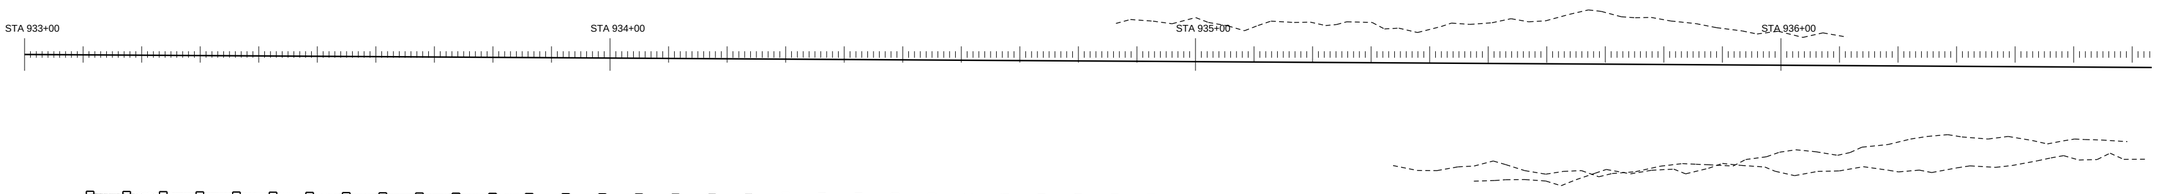


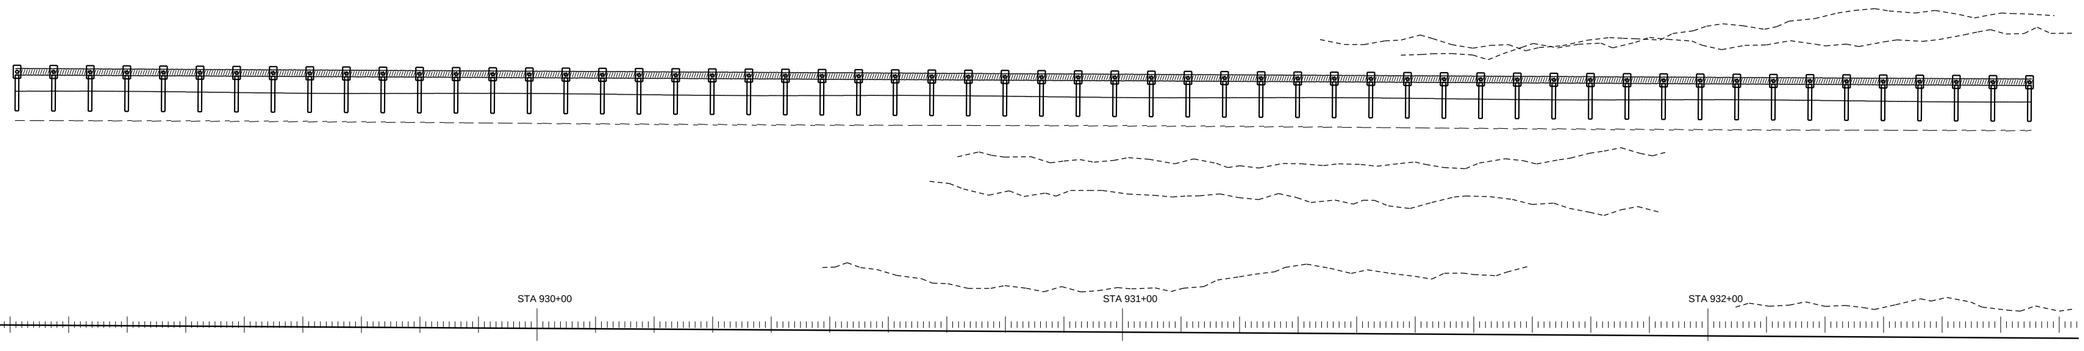


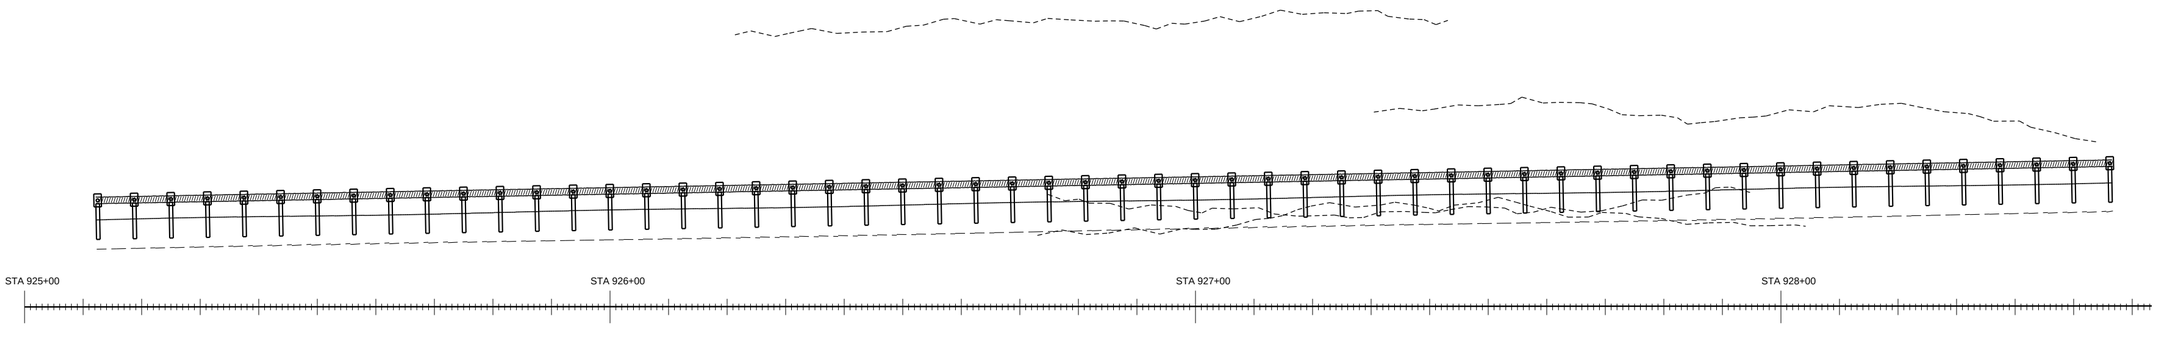


PAY ITEM 536-1-1 GUARDRAIL ROADWAY (TL-3)

PAY ITEM 536-85-24 END TREATMENT

GUARANTEED FENCE CORP

FIN. PROJ. ID 441234-1-52-01

SHEET 56 OF 120

SHEET NO. 156

ROADWAY PLAN SCALE: 1" = 20'

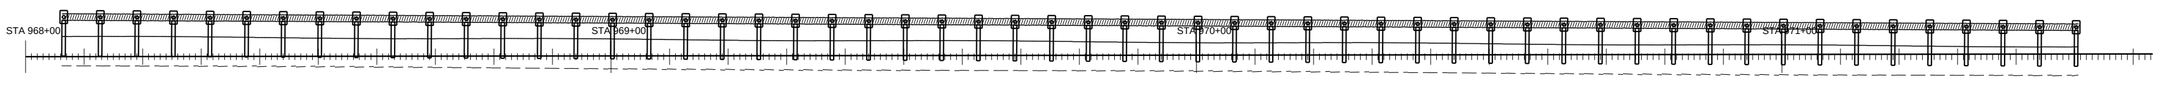


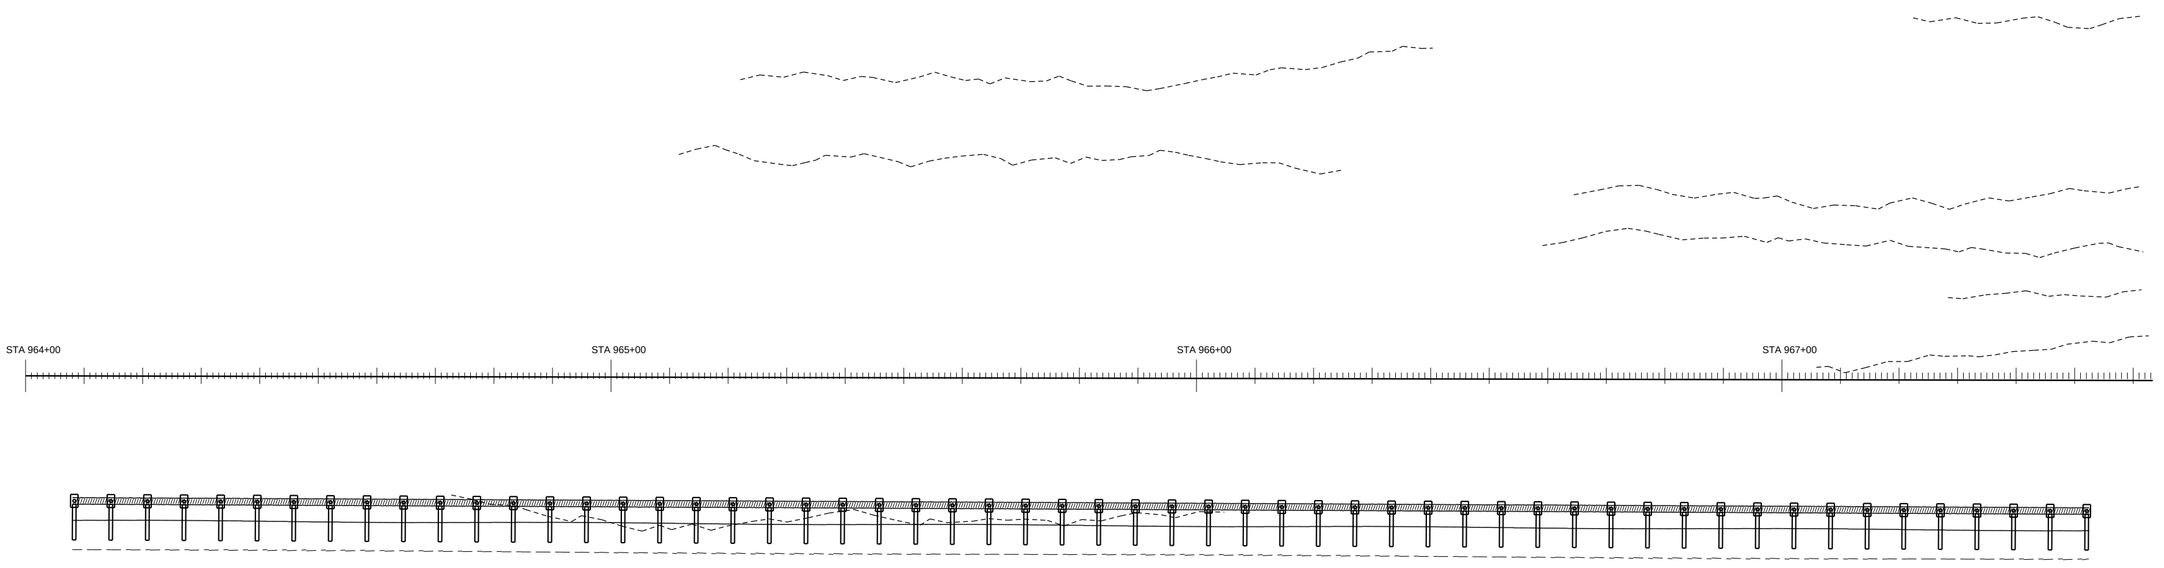


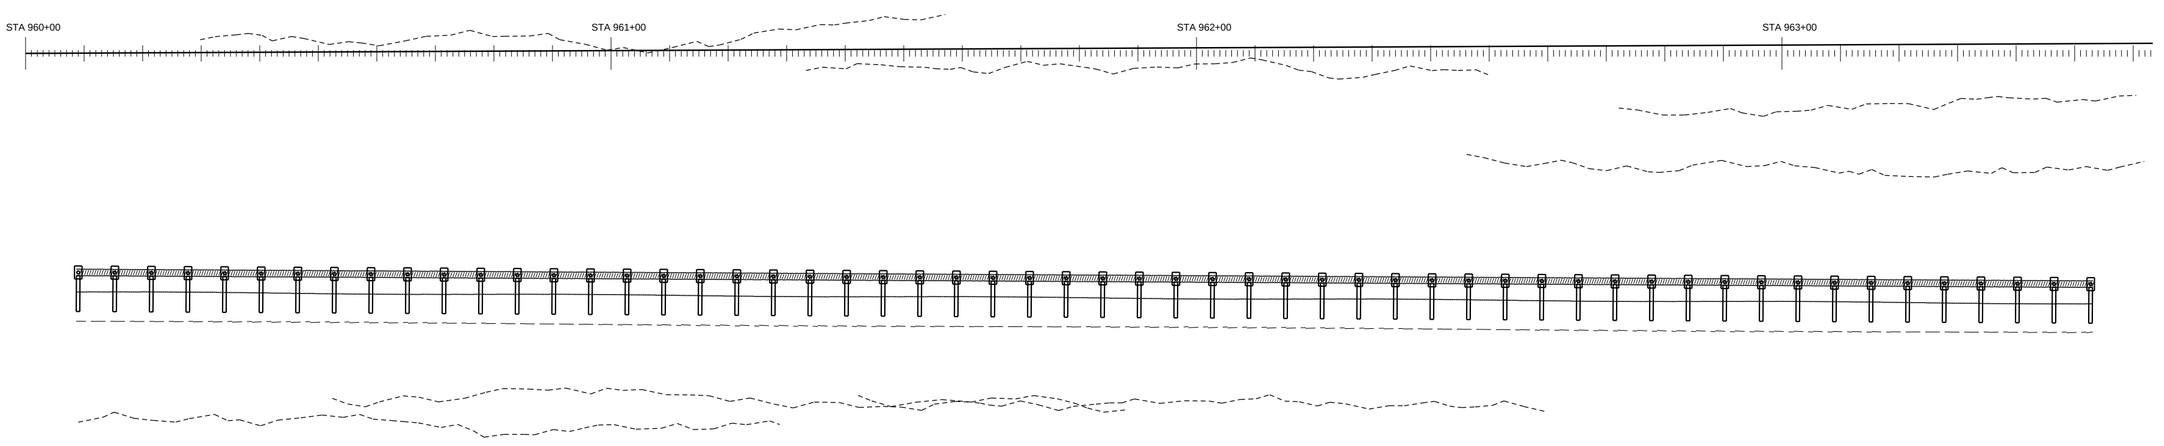


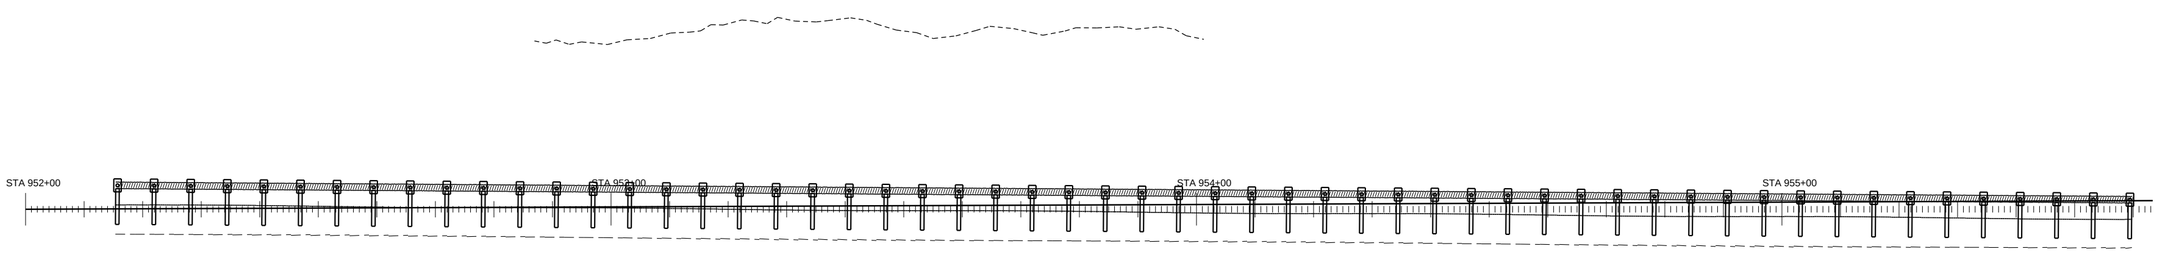


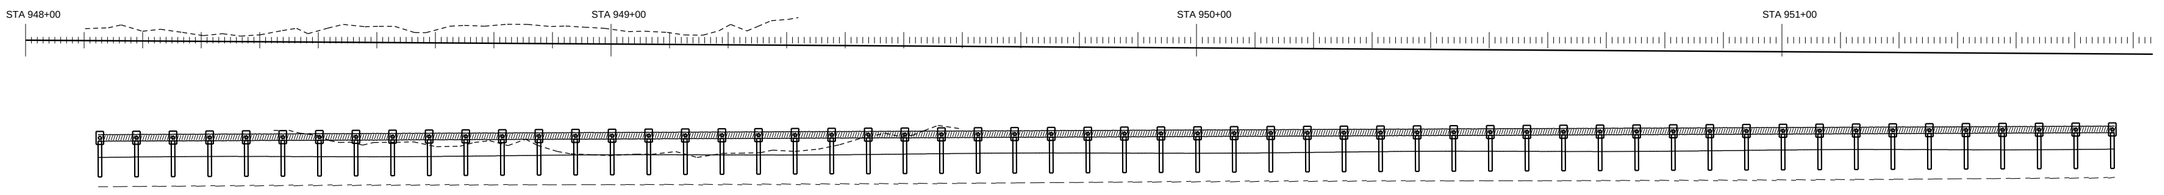


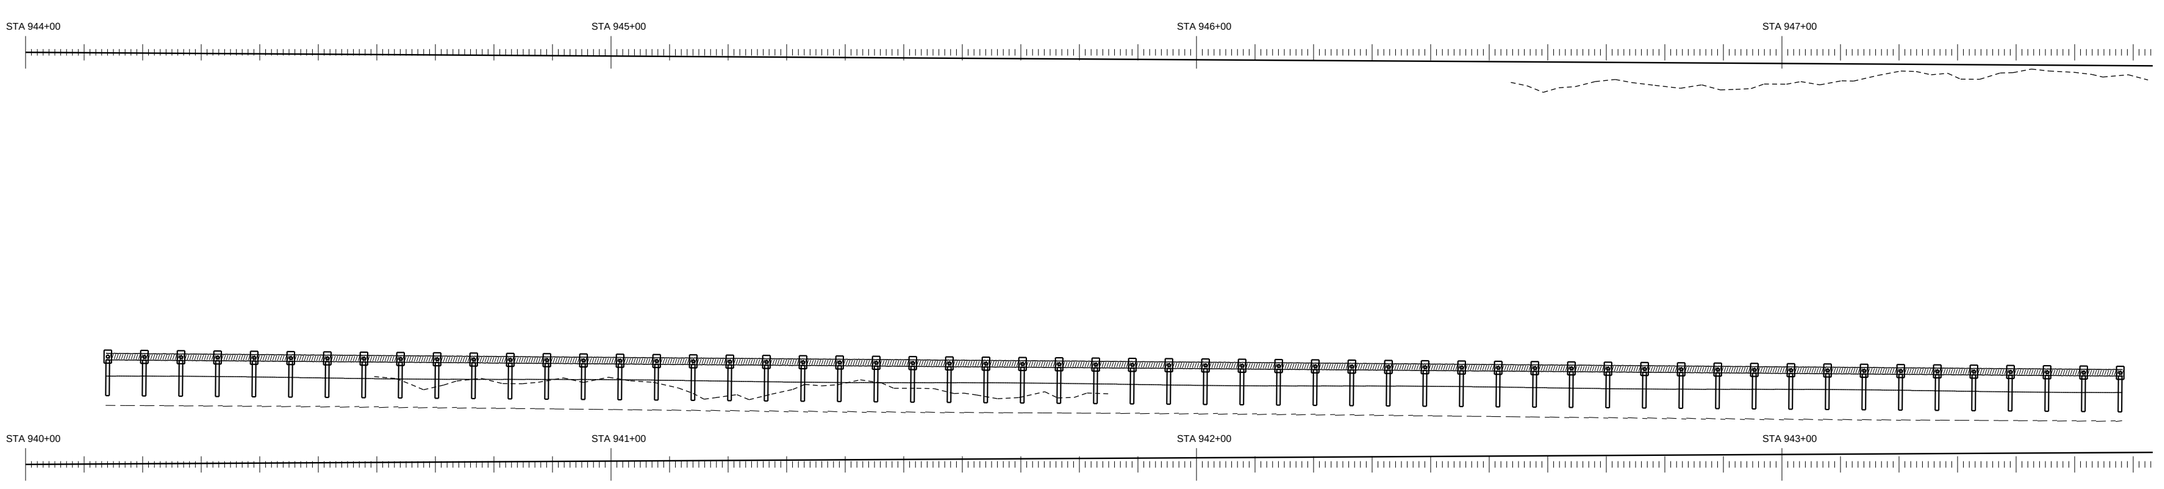


PAY ITEM 536-1-1 GUARDRAIL ROADWAY (TL-3)

PAY ITEM 536-85-24 END TREATMENT

GUARANTEED FENCE CORP

FIN. PROJ. ID 441234-1-52-01

SHEET 57 OF 120

SHEET NO. 157

ROADWAY PLAN SCALE: 1" = 20'




PAY ITEM 536-1-1 GUARDRAIL ROADWAY (TL-3)

PAY ITEM 536-85-24 END TREATMENT

GUARANTEED FENCE CORP

FIN. PROJ. ID 441234-1-52-01

SHEET 58 OF 120

SHEET NO. 158

ROADWAY PLAN SCALE: 1" = 20'

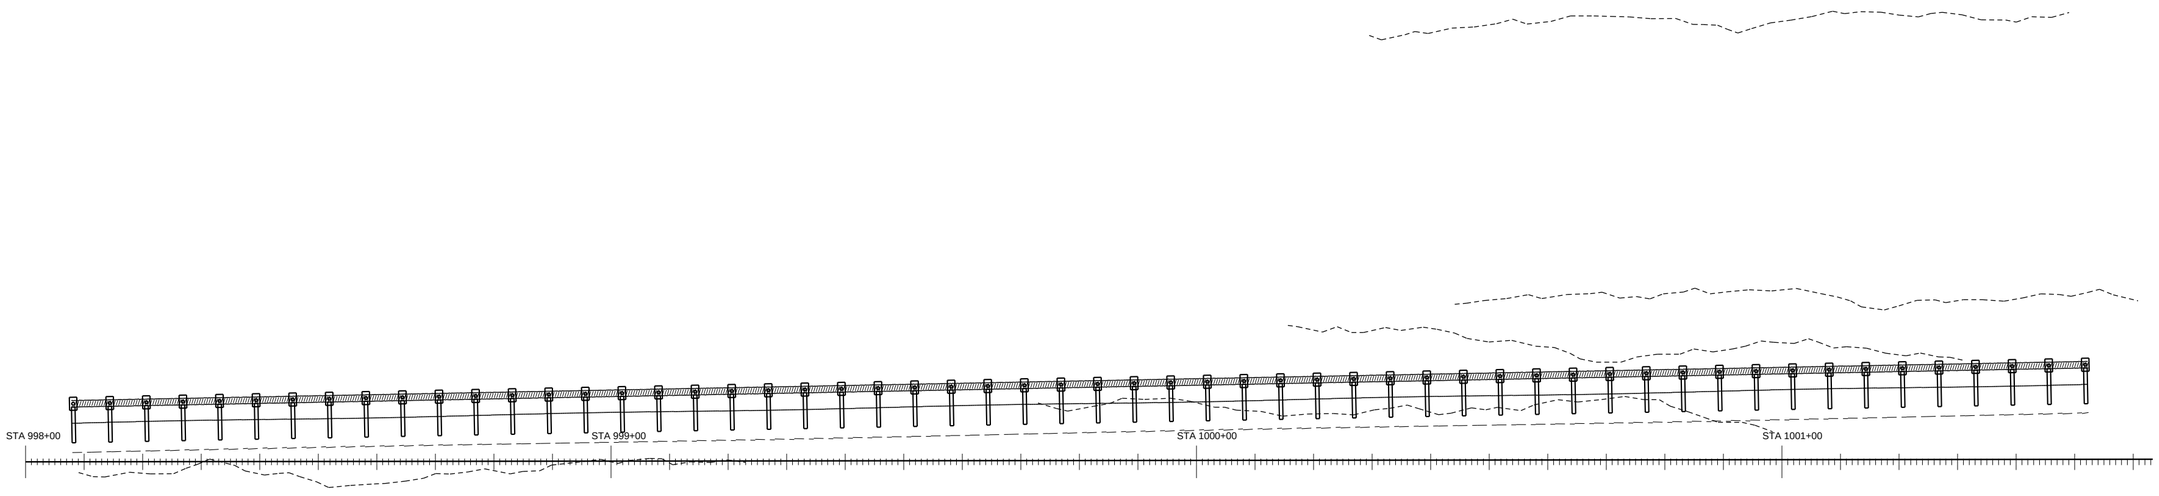


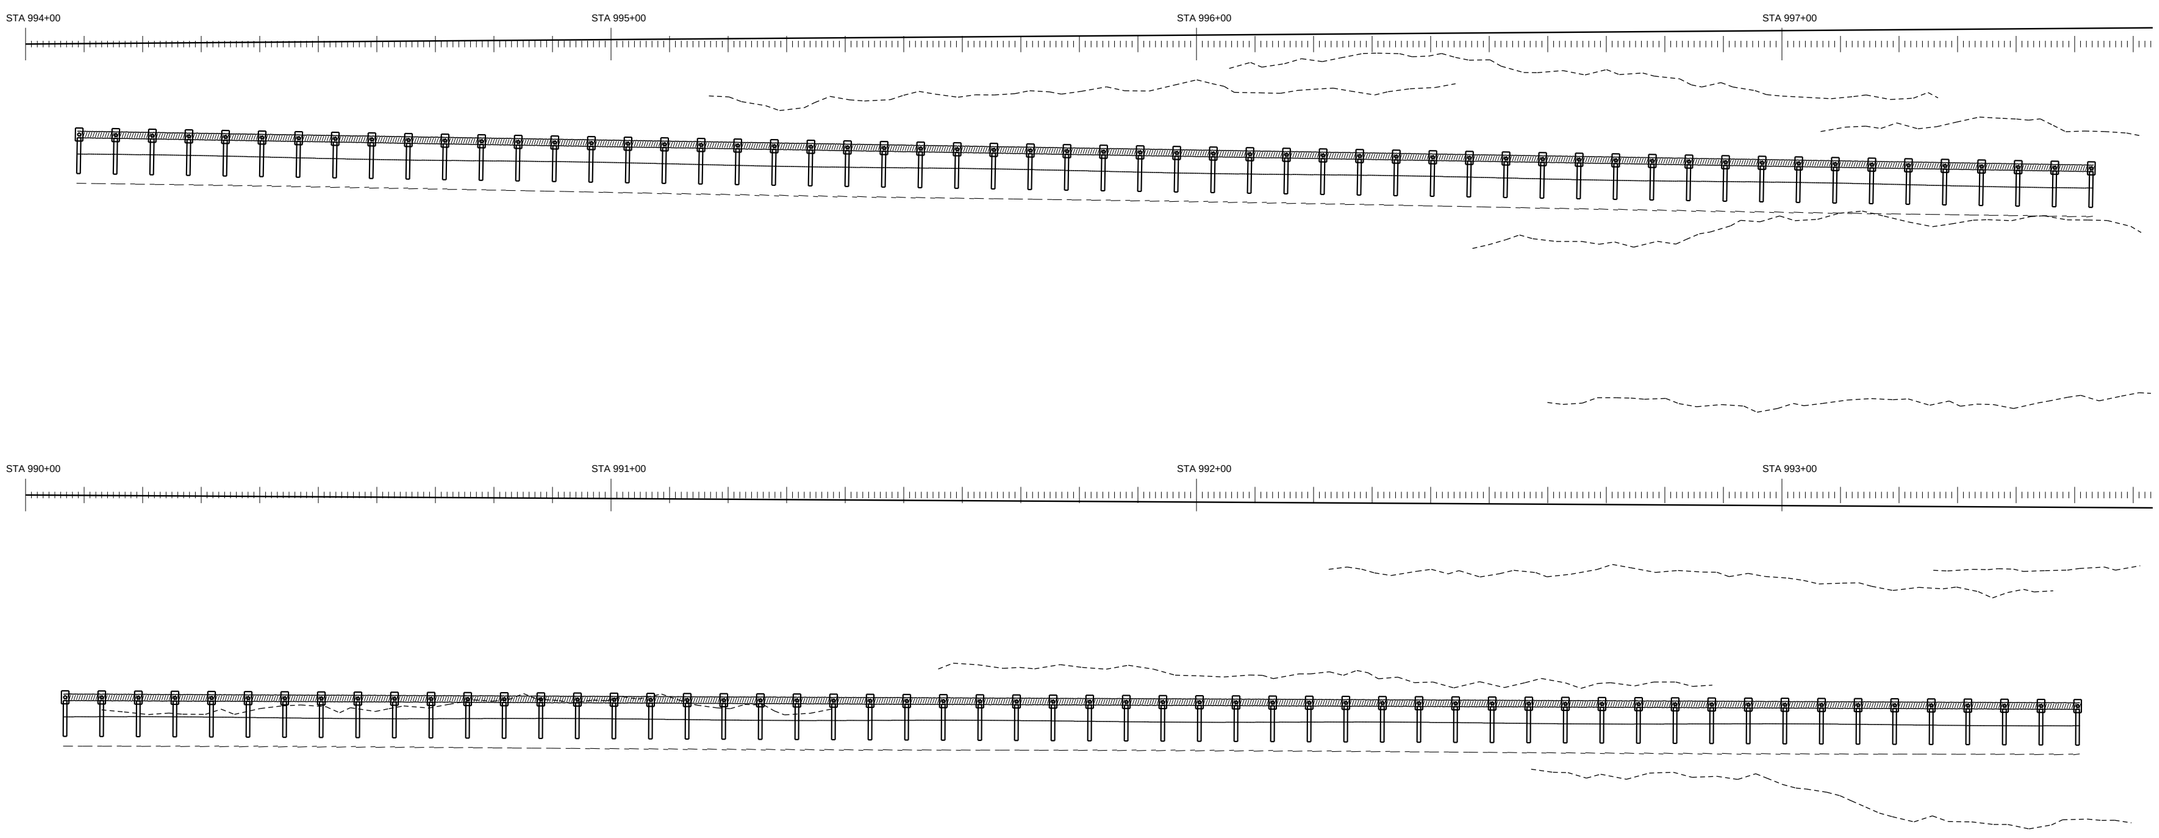


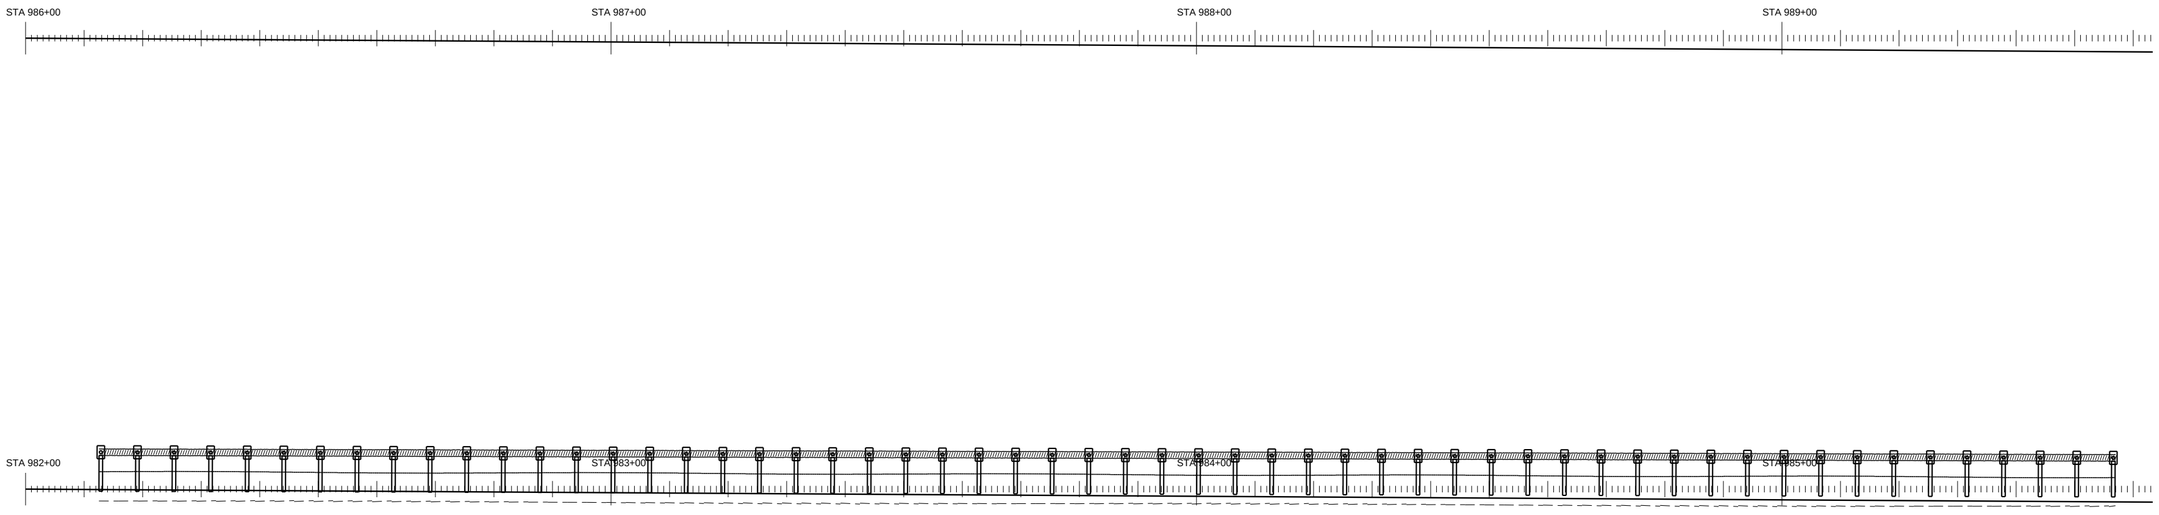


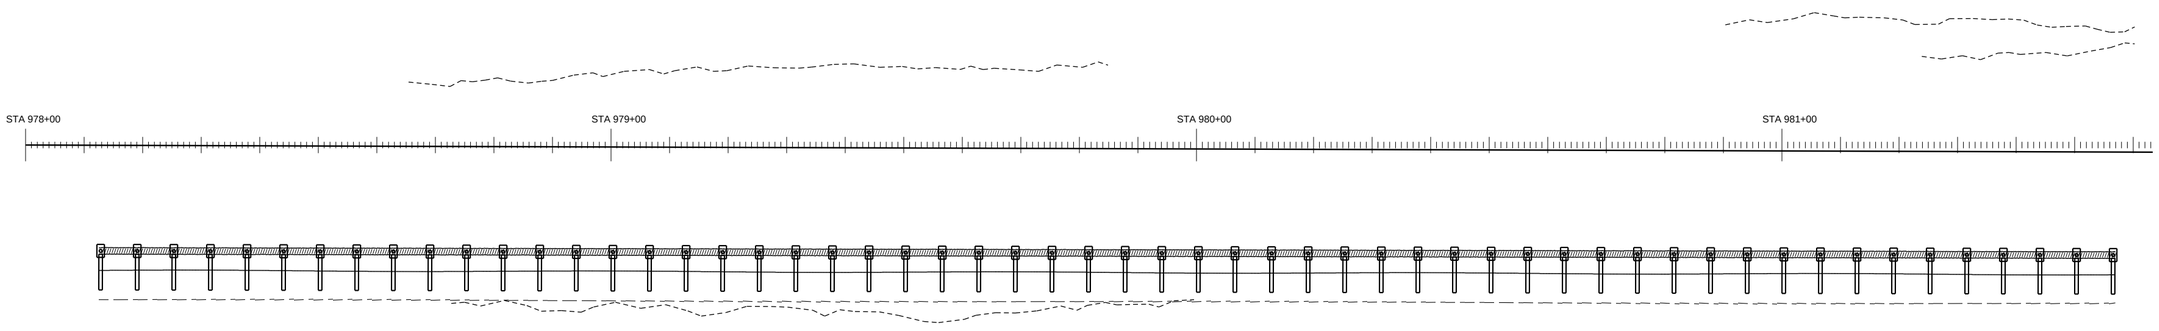


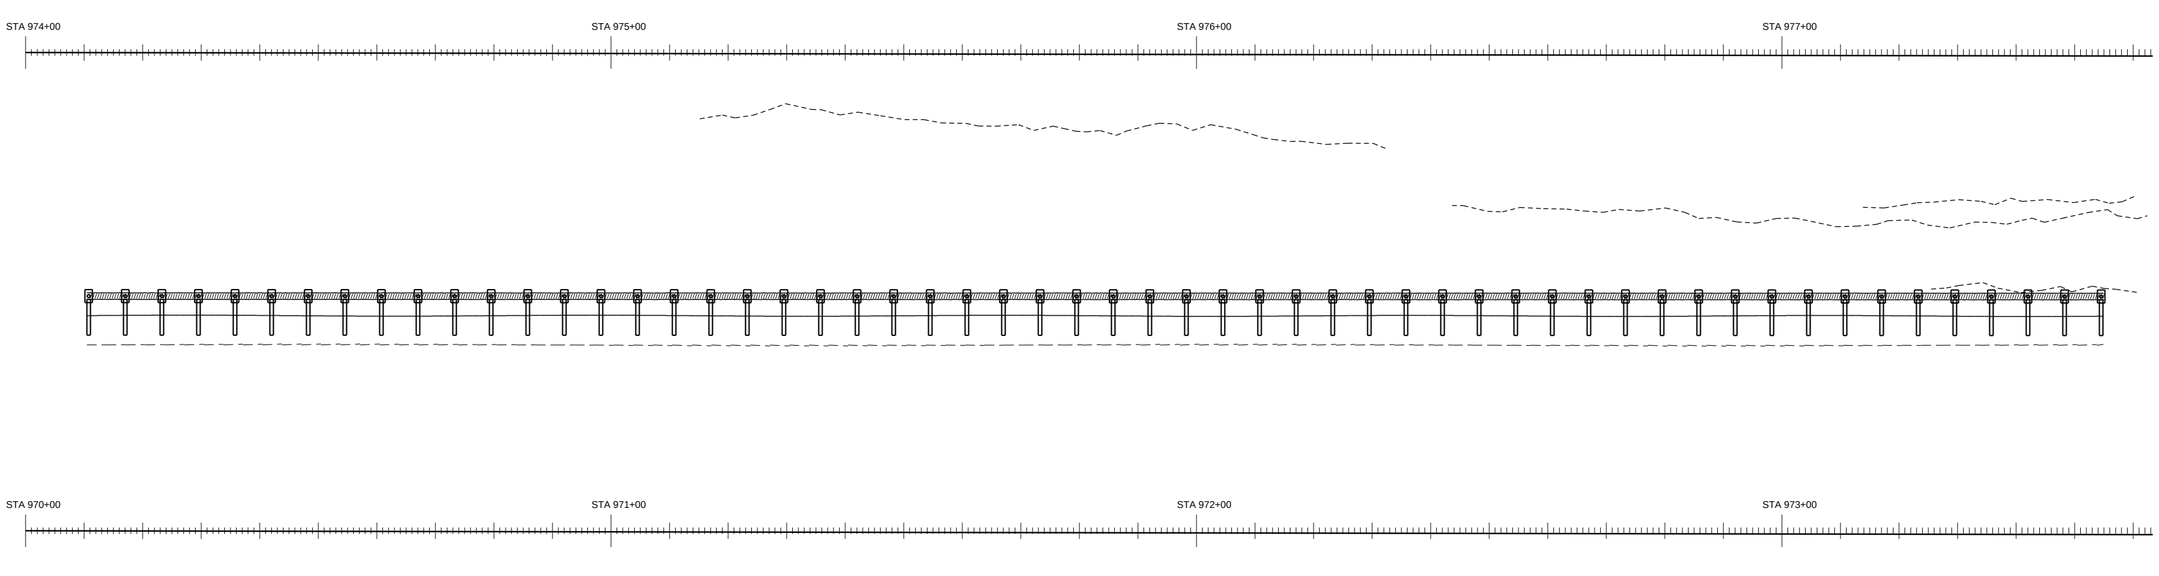


PAY ITEM 536-1-1 GUARDRAIL ROADWAY (TL-3)

PAY ITEM 536-85-24 END TREATMENT

GUARANTEED FENCE CORP

FIN. PROJ. ID 441234-1-52-01

SHEET 59 OF 120

SHEET NO. 159

ROADWAY PLAN SCALE: 1" = 20'

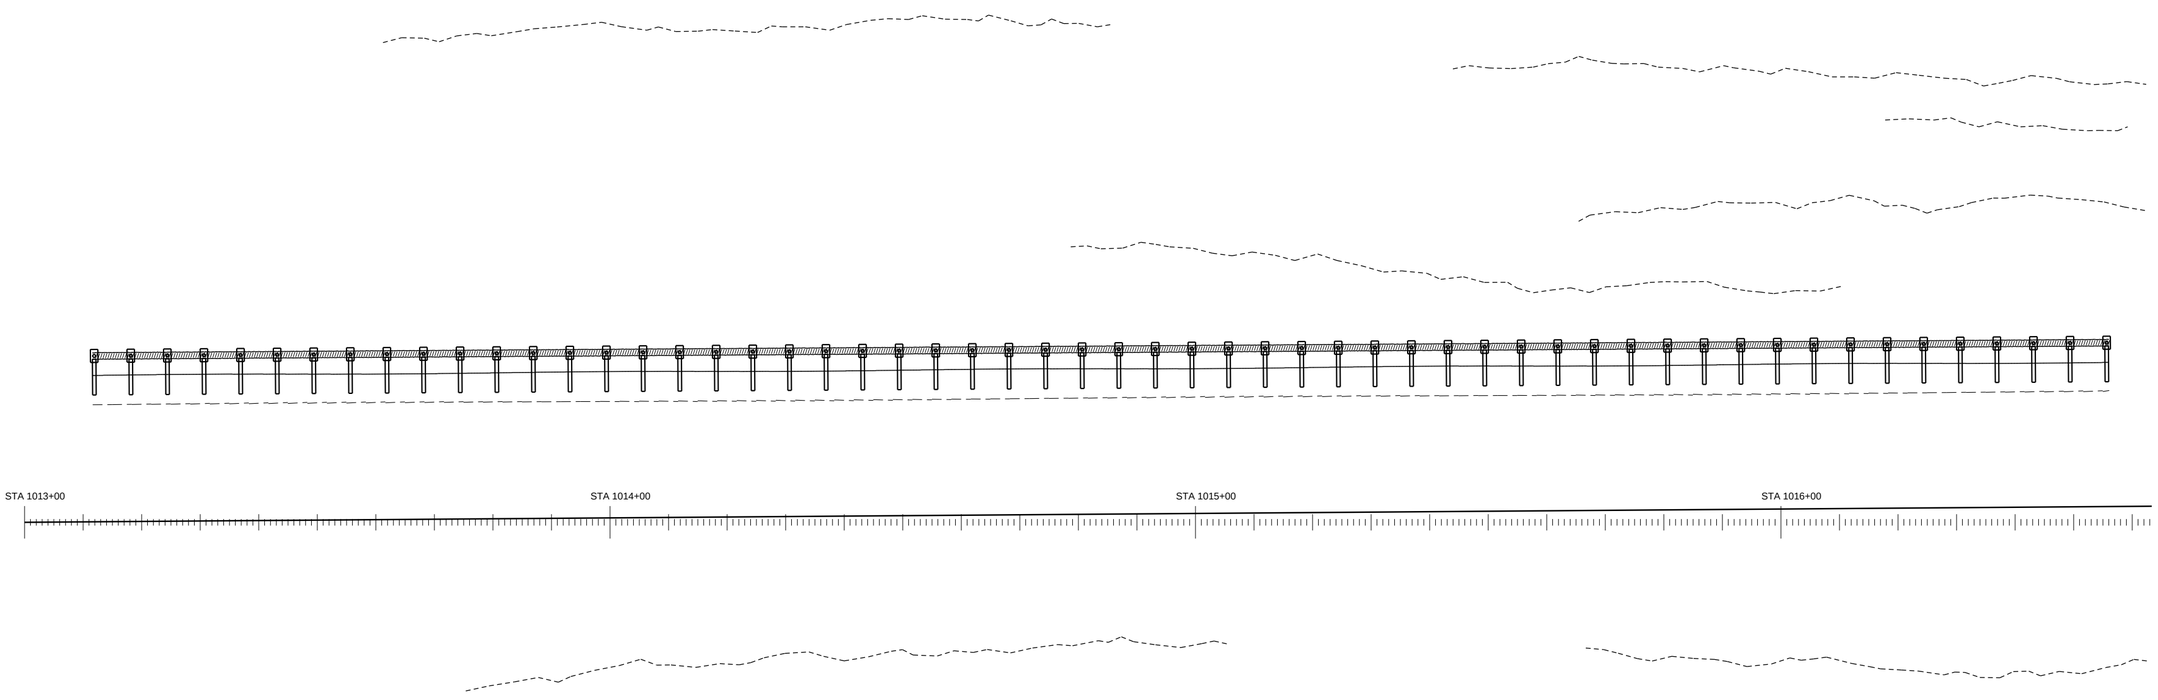


PAY ITEM 536-1-1 GUARDRAIL ROADWAY (TL-3)

PAY ITEM 536-85-24 END TREATMENT

GUARANTEED FENCE CORP

FIN. PROJ. ID 441234-1-52-01

SHEET 60 OF 120

SHEET NO. 160

ROADWAY PLAN SCALE: 1" = 20'

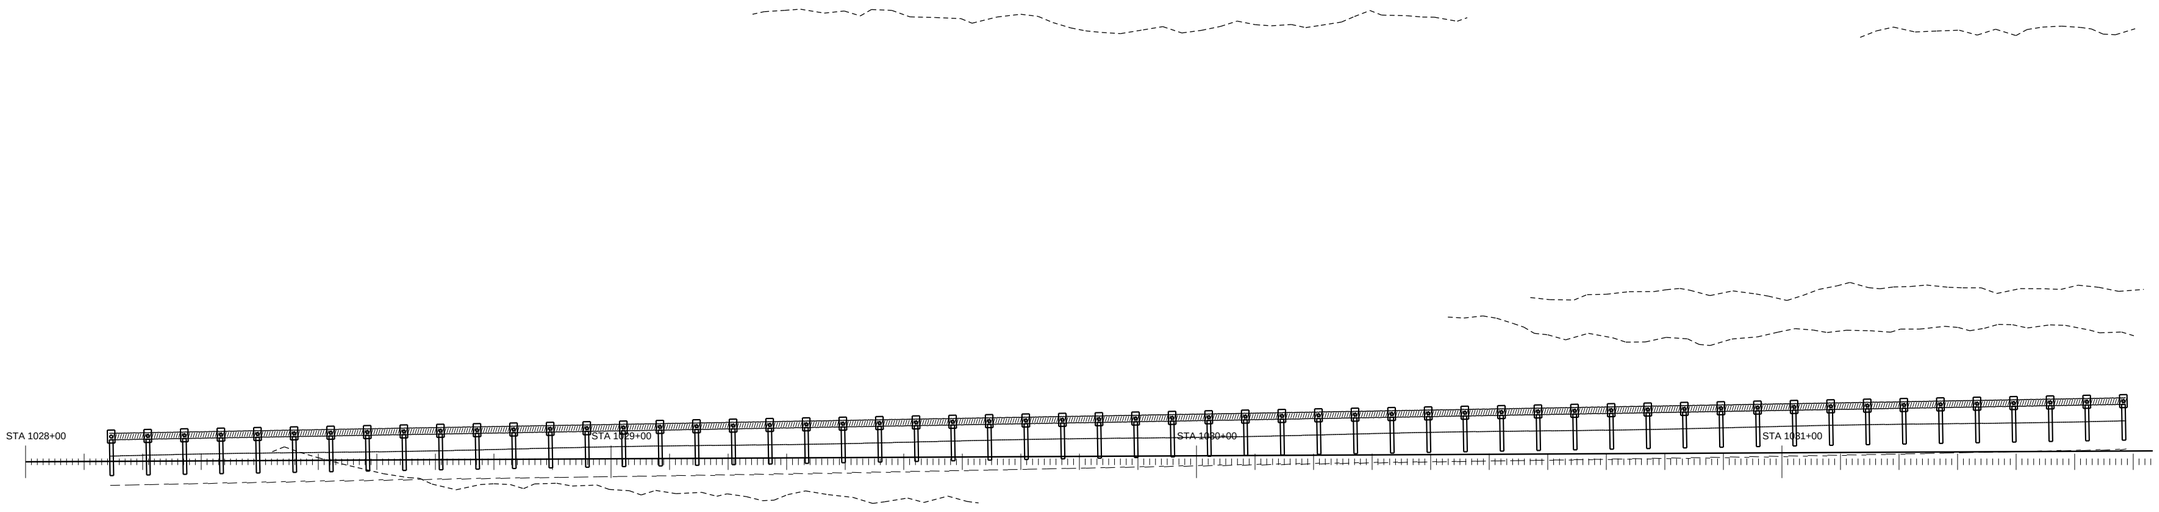


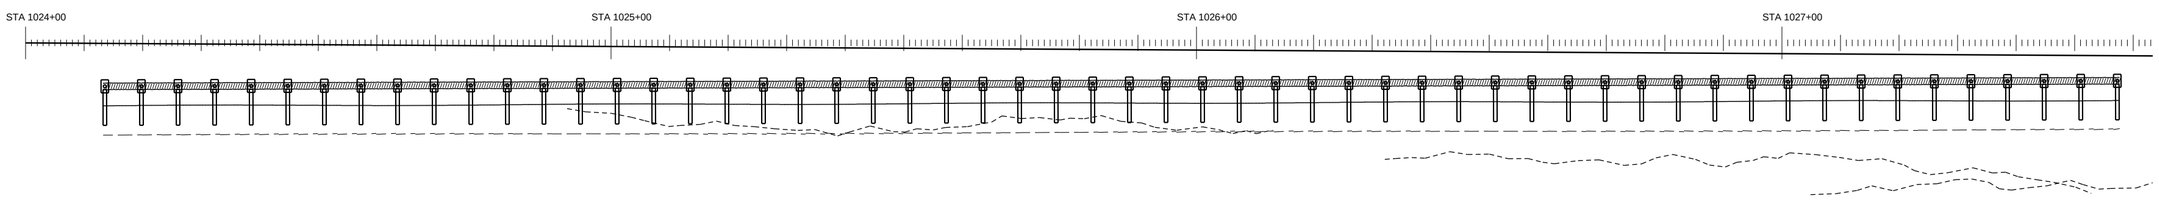


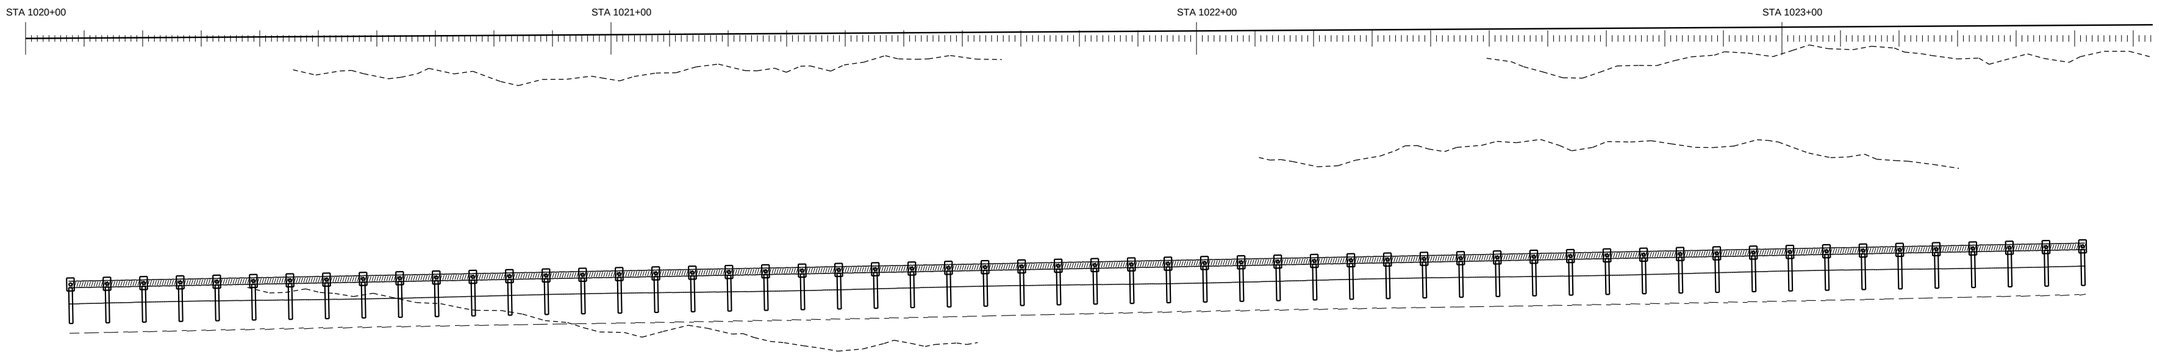


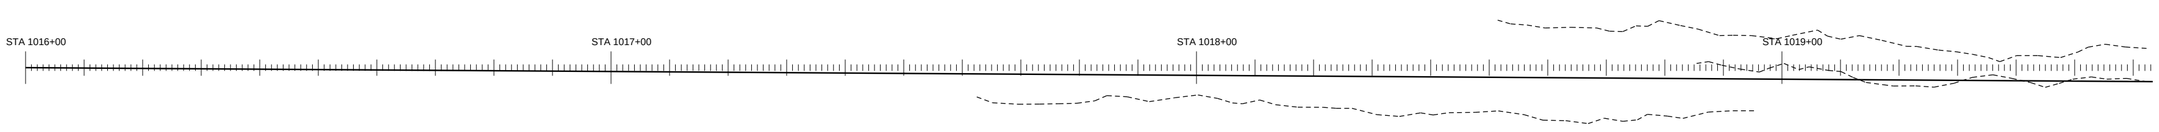


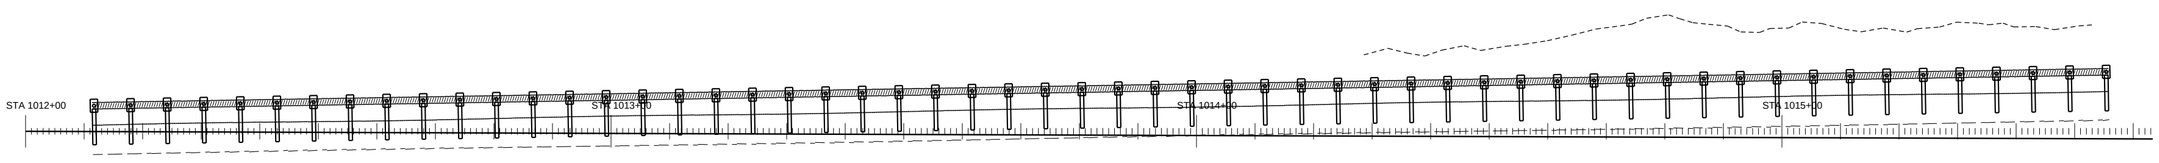

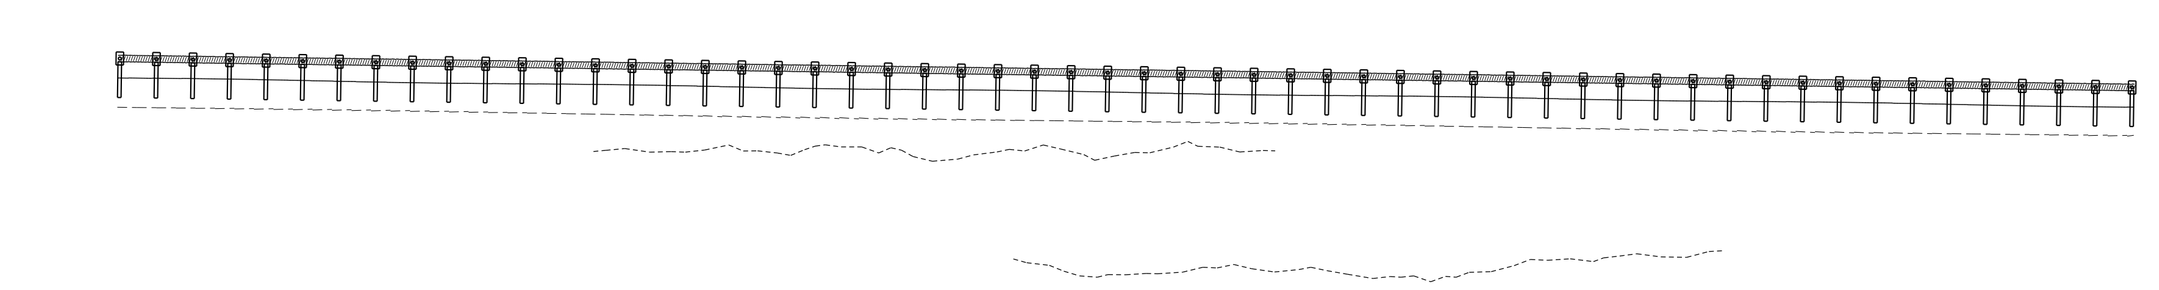


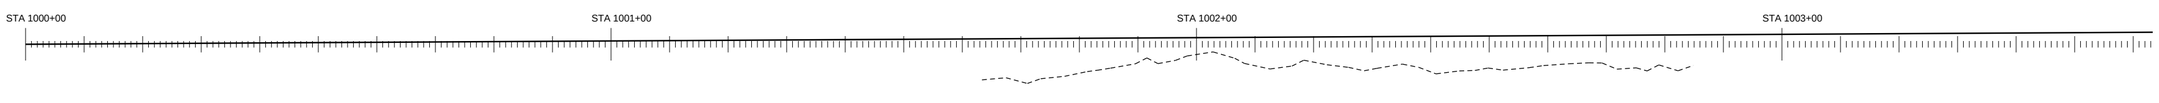


PAY ITEM 536-1-1 GUARDRAIL ROADWAY (TL-3)

PAY ITEM 536-85-24 END TREATMENT

GUARANTEED FENCE CORP

FIN. PROJ. ID 441234-1-52-01

SHEET 61 OF 120

SHEET NO. 161

ROADWAY PLAN SCALE: 1" = 20'

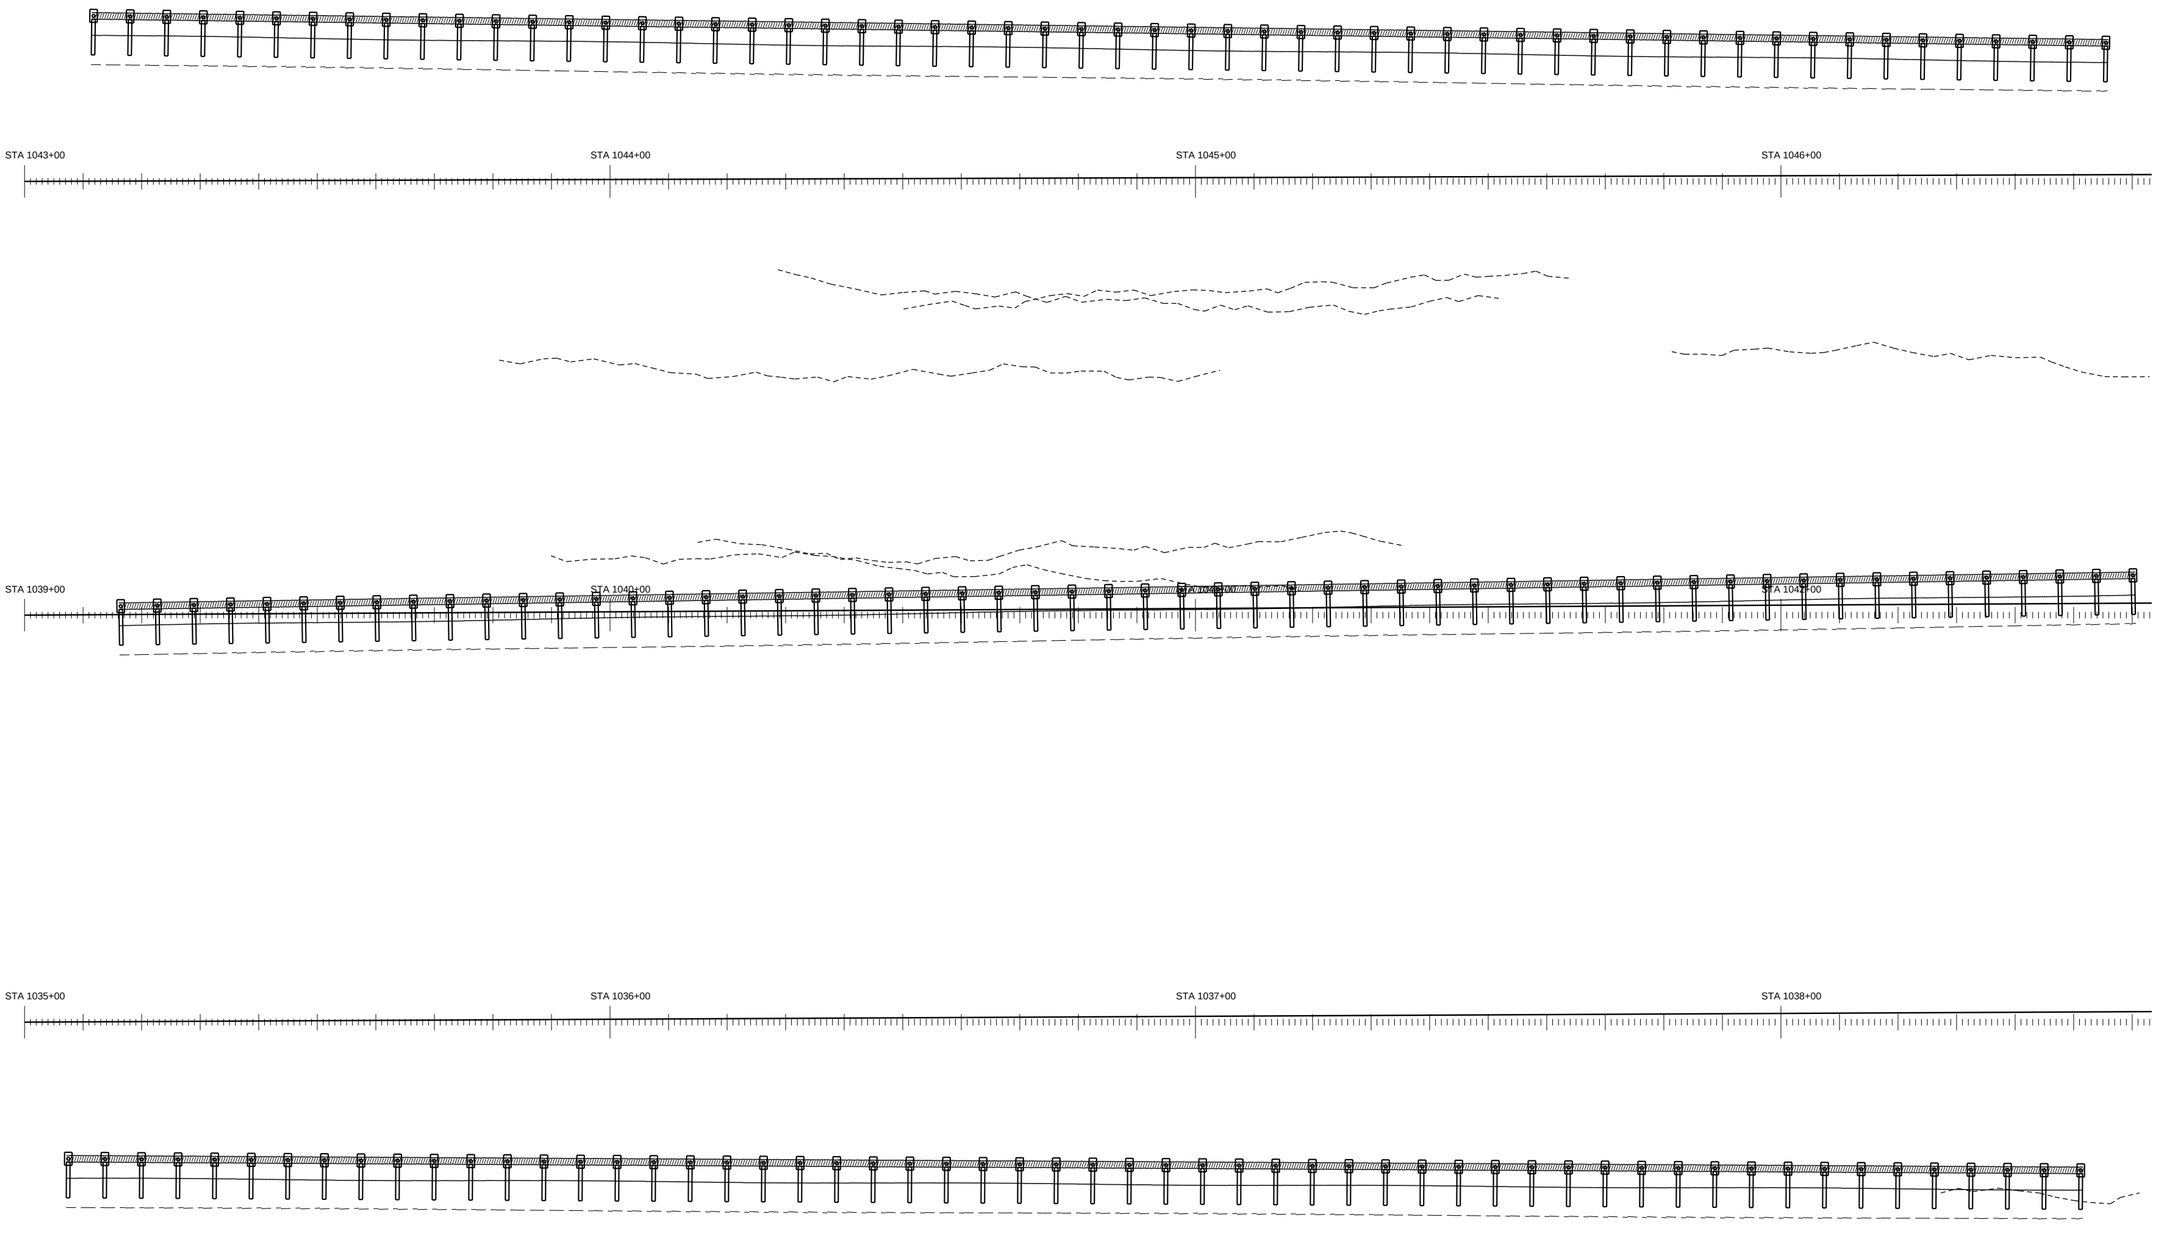


PAY ITEM 536-1-1 GUARDRAIL ROADWAY (TL-3)

PAY ITEM 536-85-24 END TREATMENT

GUARANTEED FENCE CORP

FIN. PROJ. ID 441234-1-52-01

SHEET 62 OF 120

SHEET NO. 162

ROADWAY PLAN SCALE: 1" = 20'

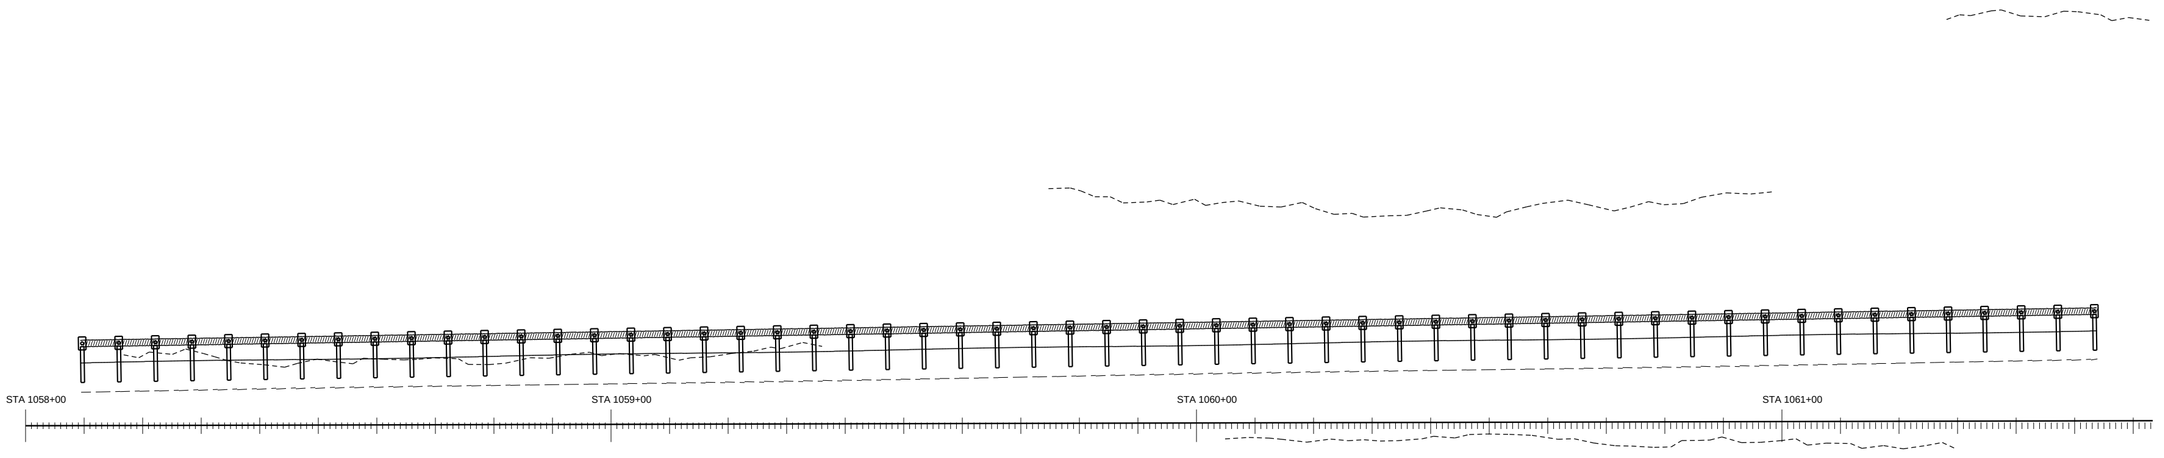


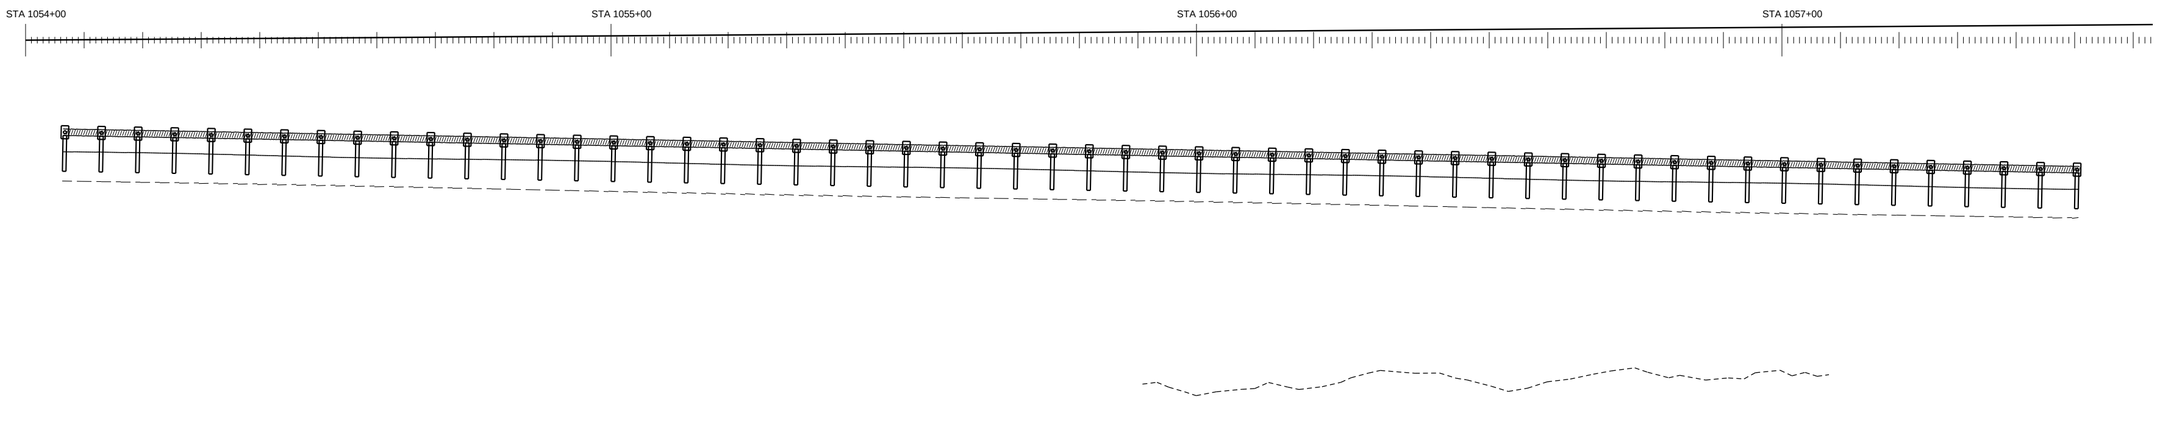


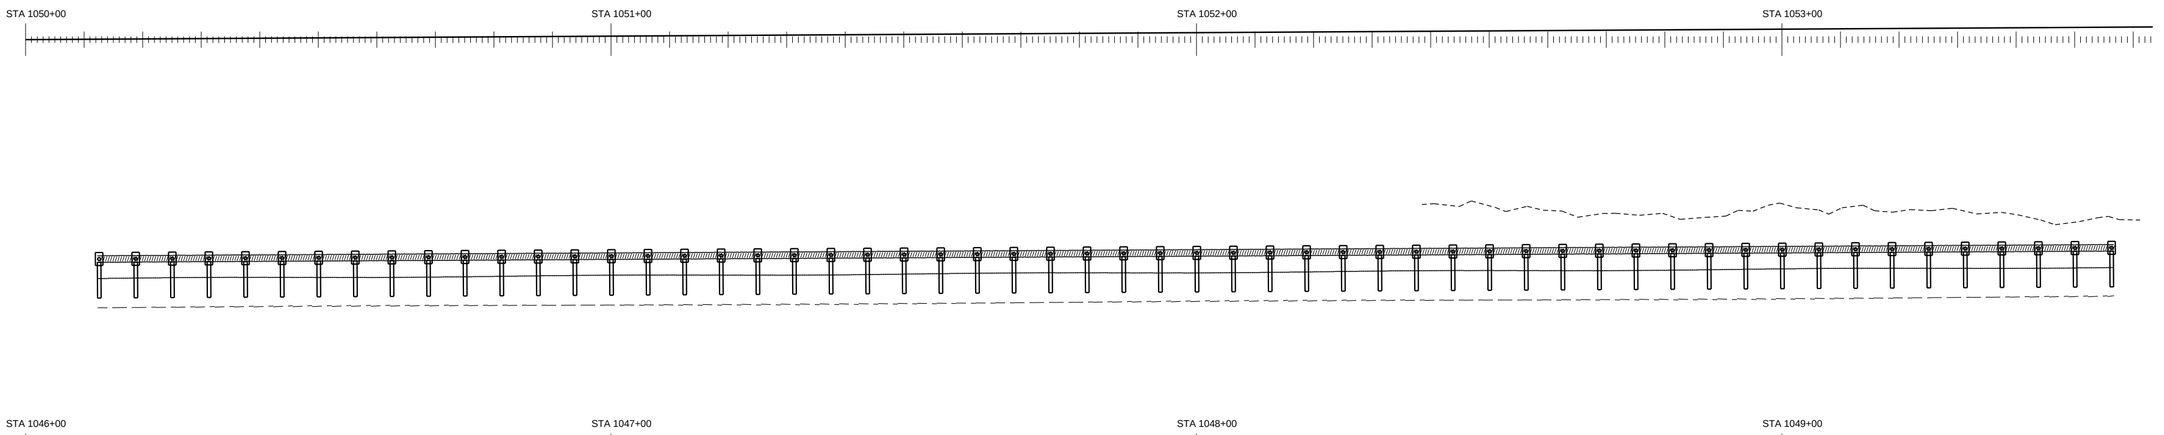


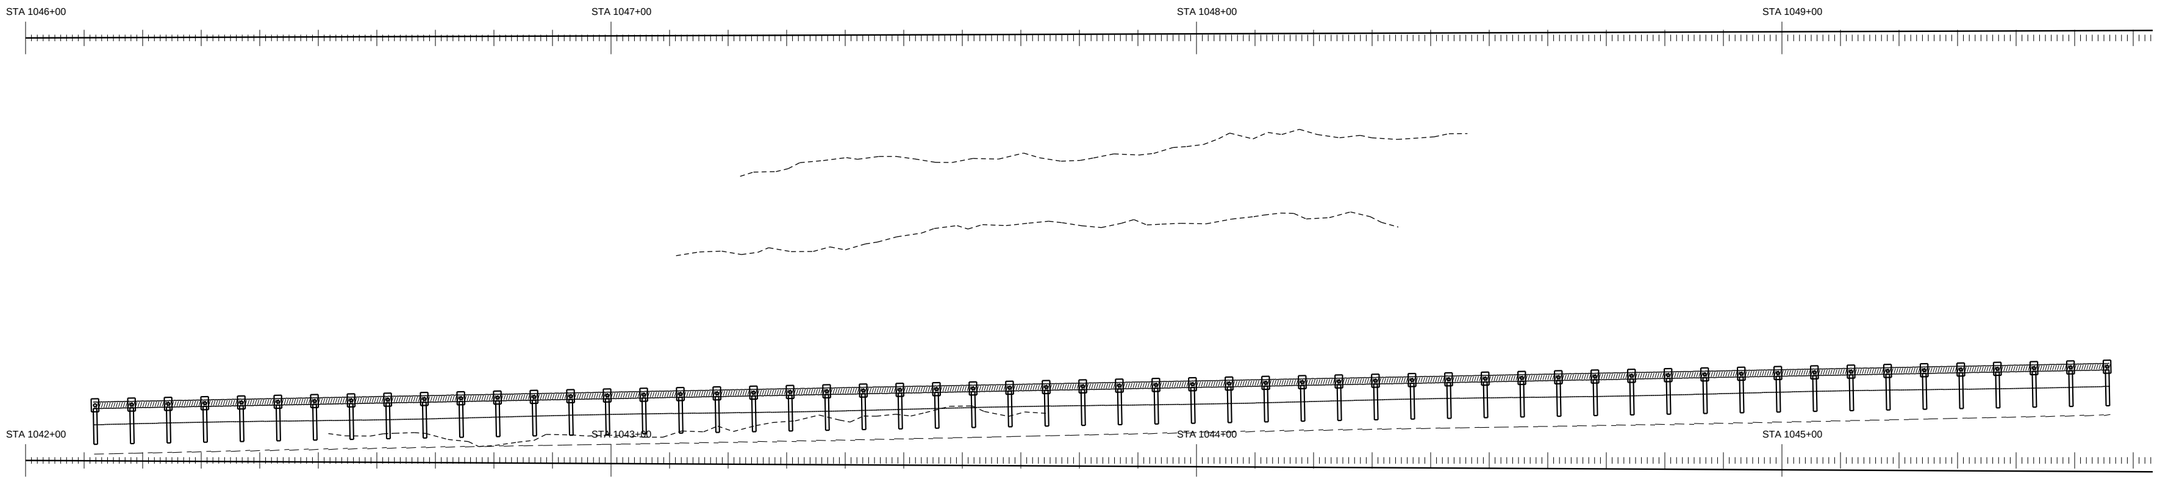


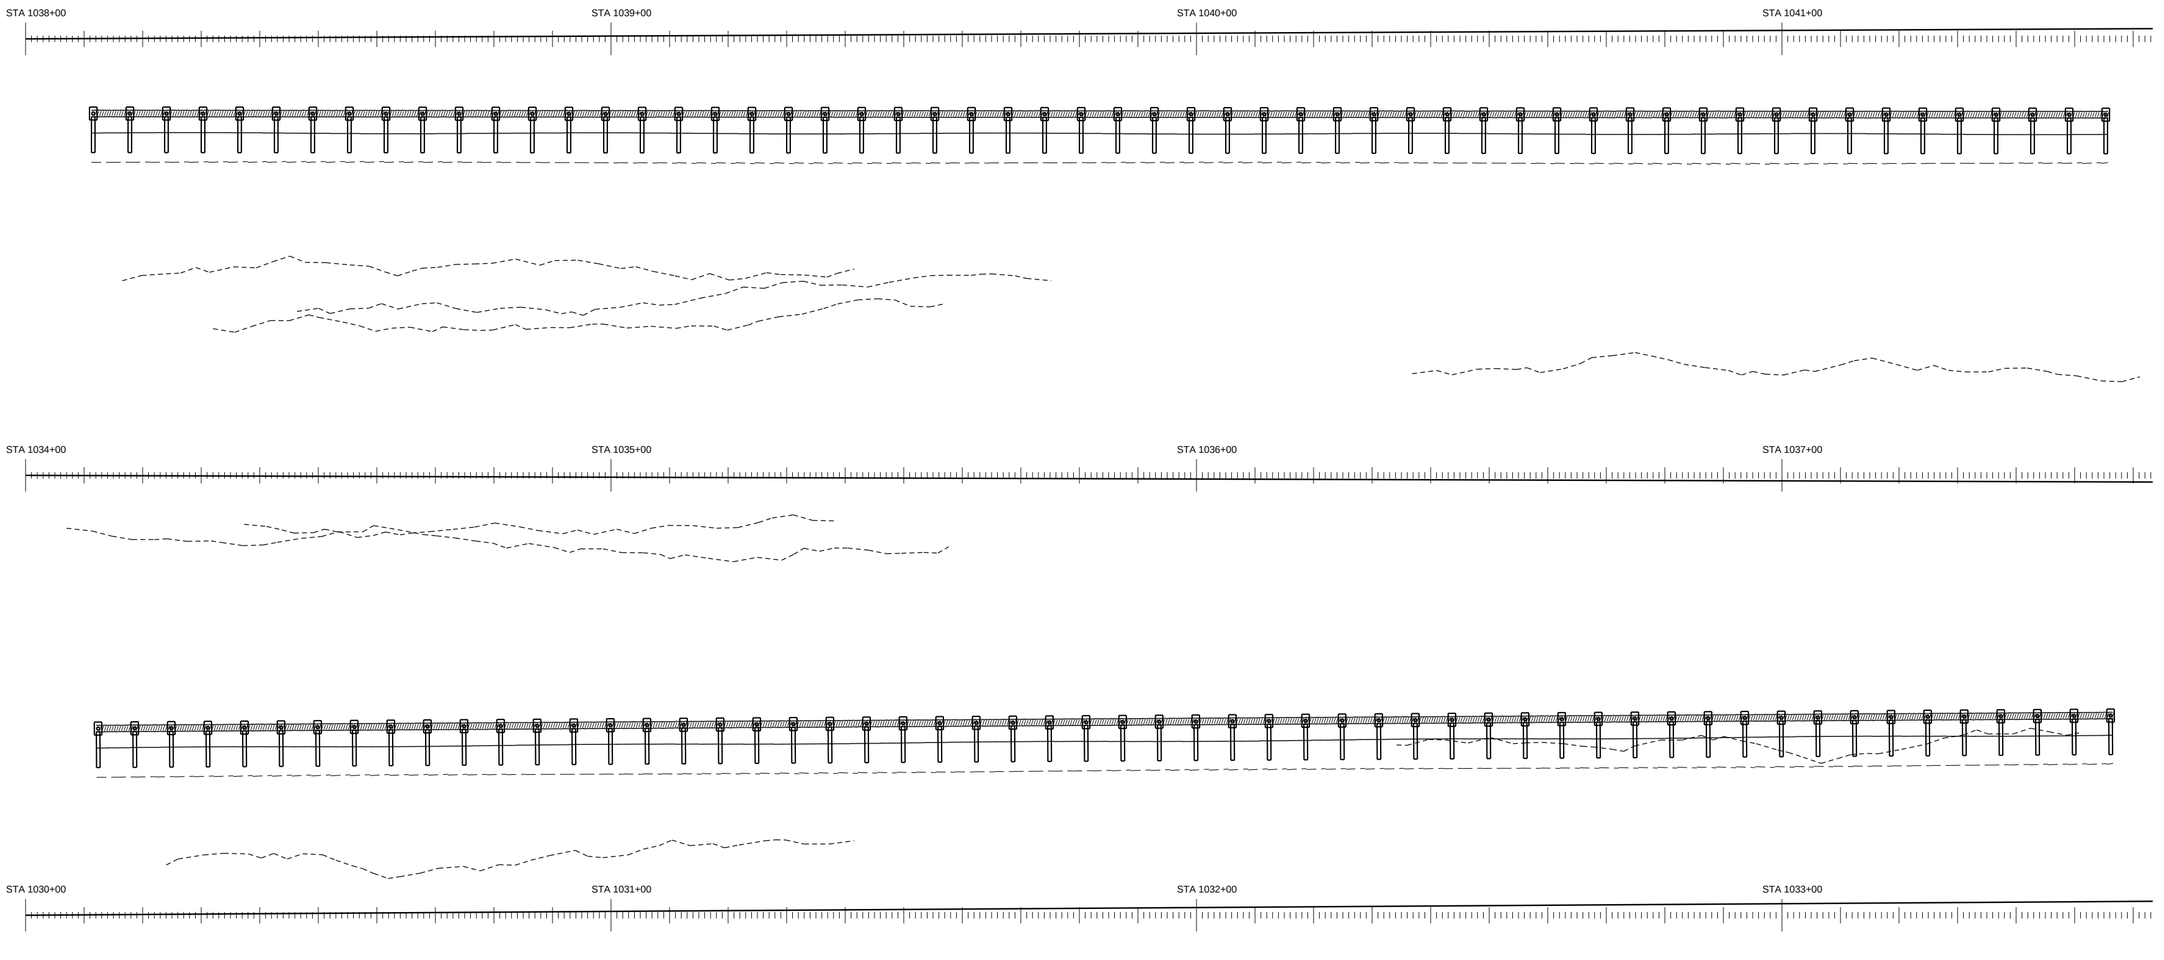


PAY ITEM 536-1-1 GUARDRAIL ROADWAY (TL-3)

PAY ITEM 536-85-24 END TREATMENT

GUARANTEED FENCE CORP

FIN. PROJ. ID 441234-1-52-01

SHEET 63 OF 120

SHEET NO. 163

ROADWAY PLAN SCALE: 1" = 20'

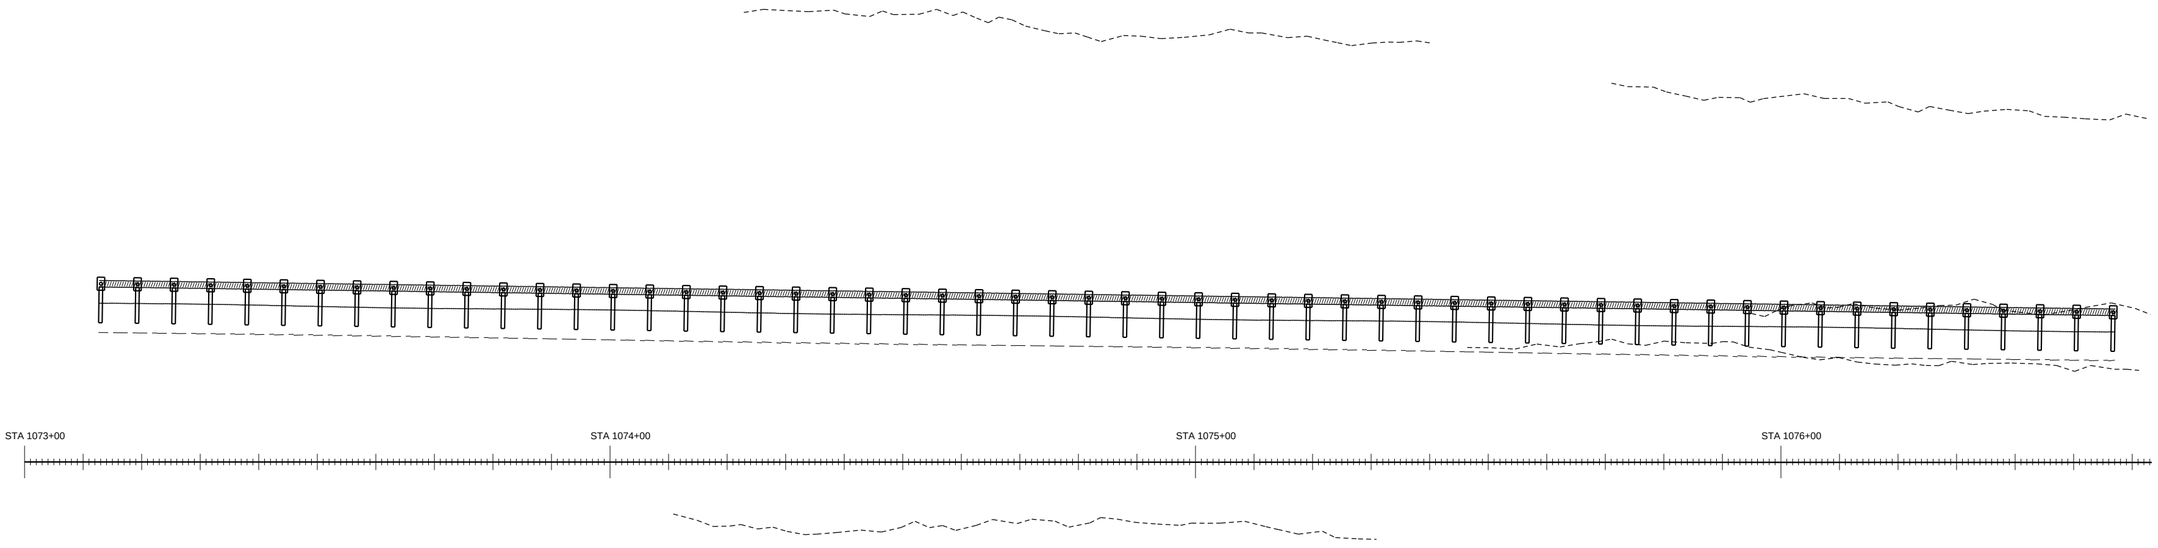


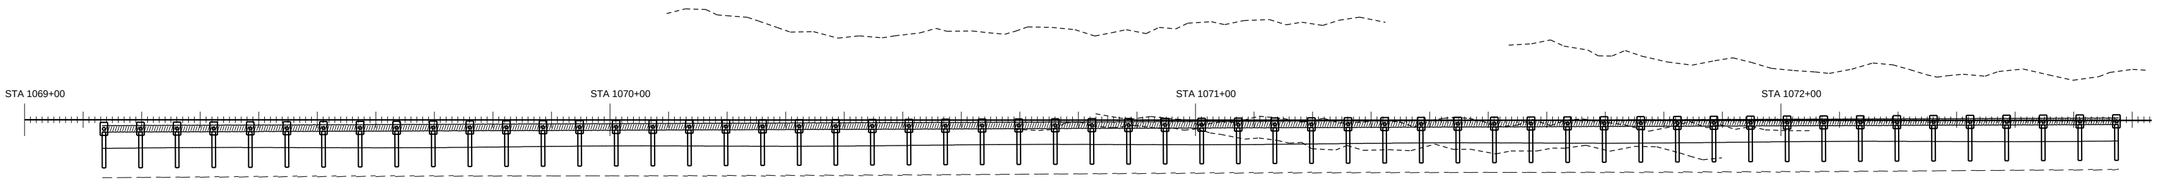


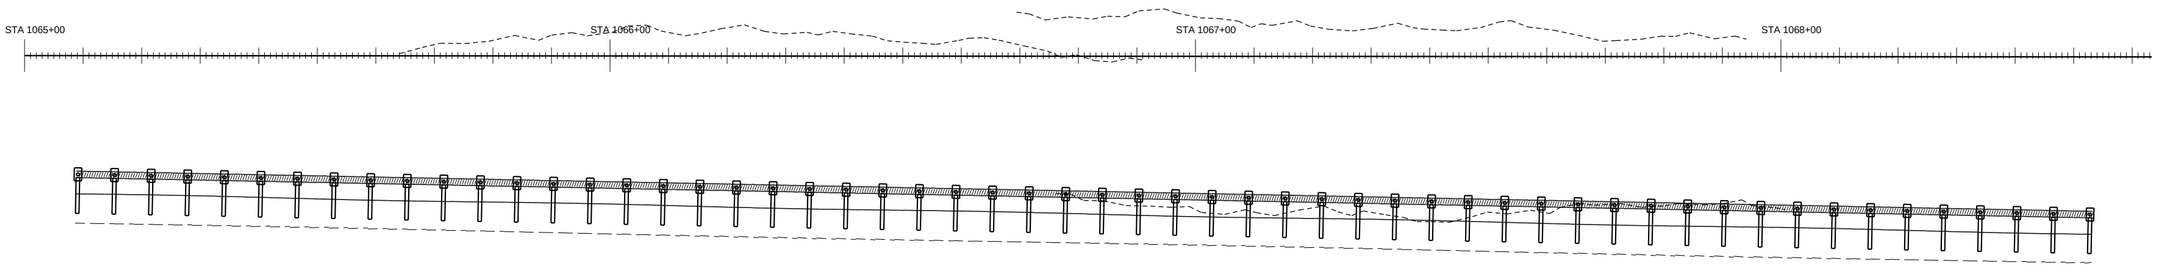


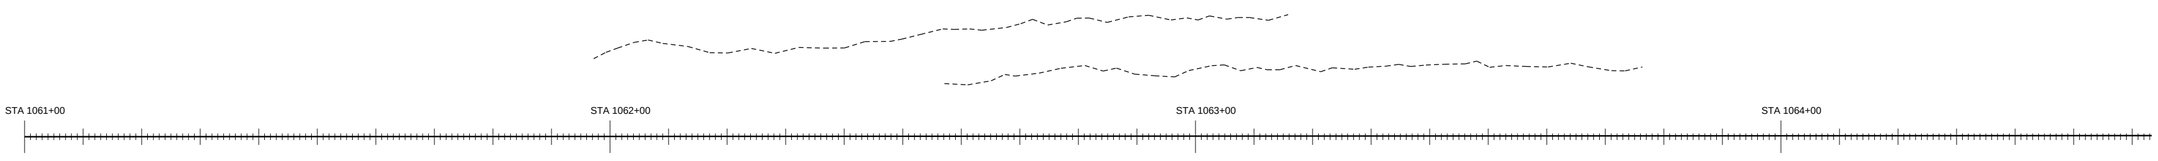


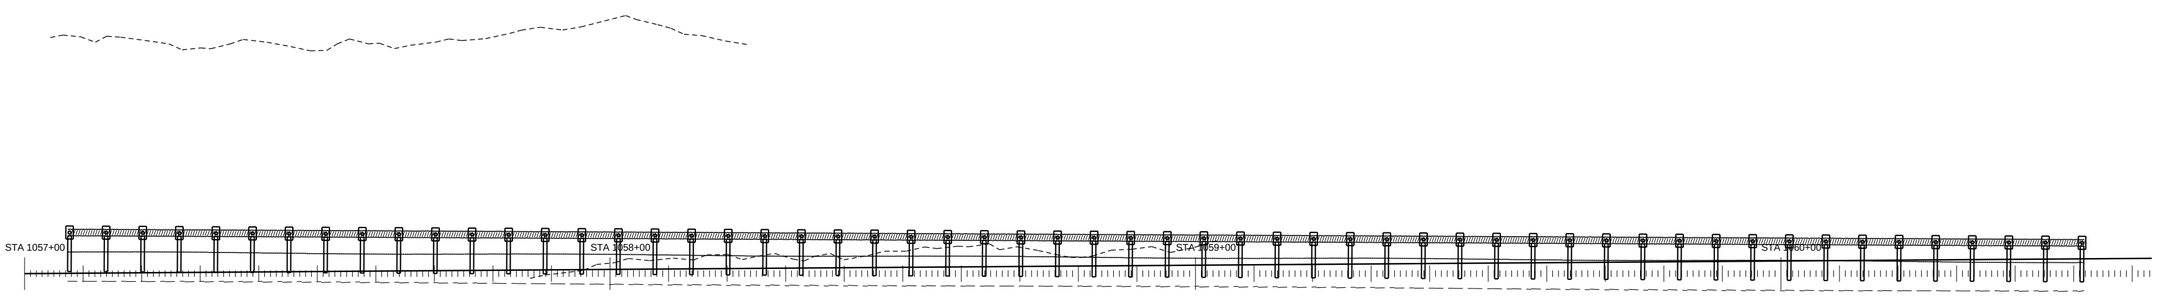


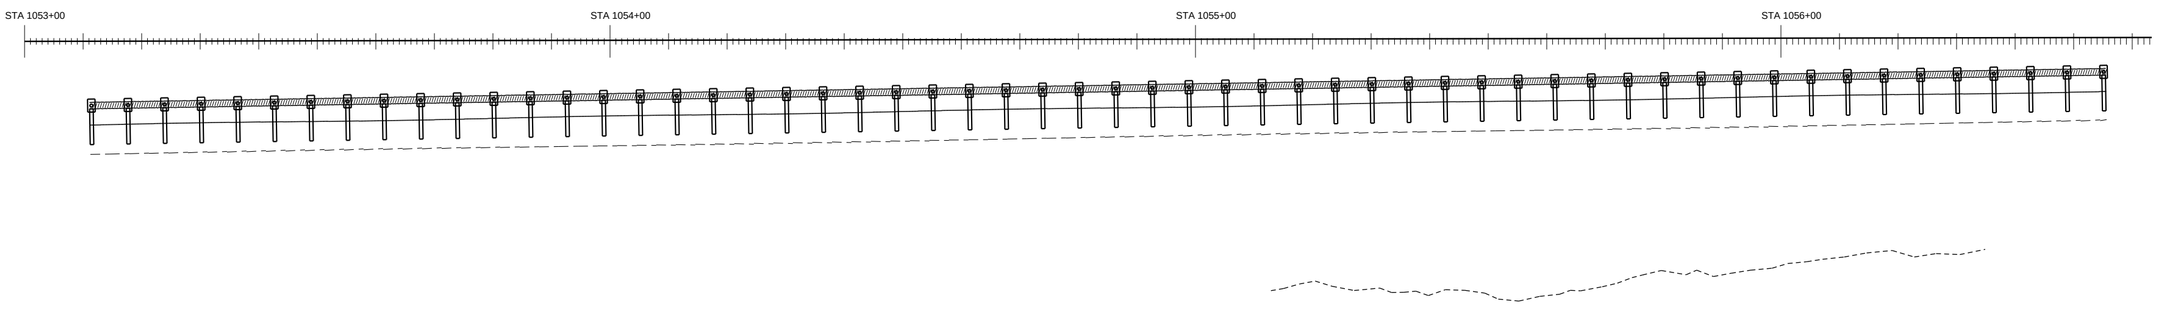


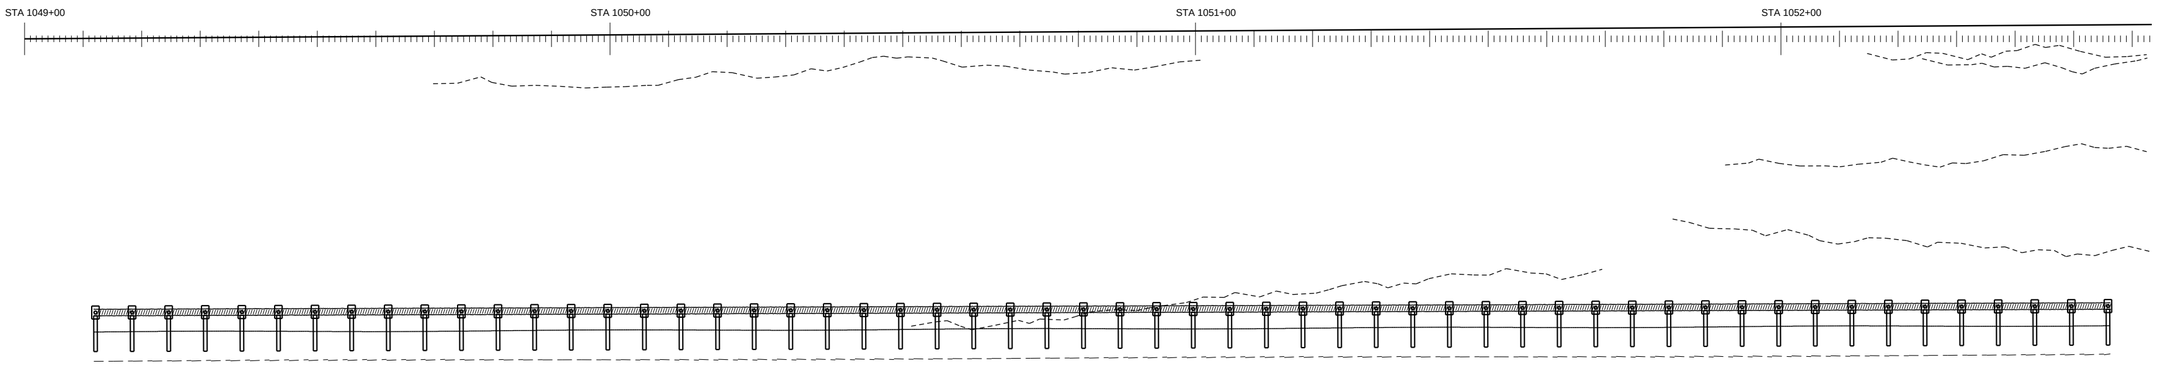


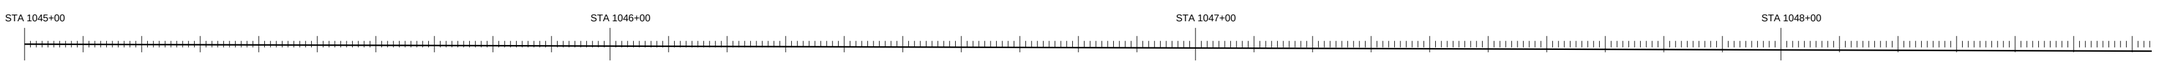


PAY ITEM 536-1-1 GUARDRAIL ROADWAY (TL-3)

PAY ITEM 536-85-24 END TREATMENT

GUARANTEED FENCE CORP

FIN. PROJ. ID 441234-1-52-01

SHEET 64 OF 120

SHEET NO. 164

ROADWAY PLAN SCALE: 1" = 20'

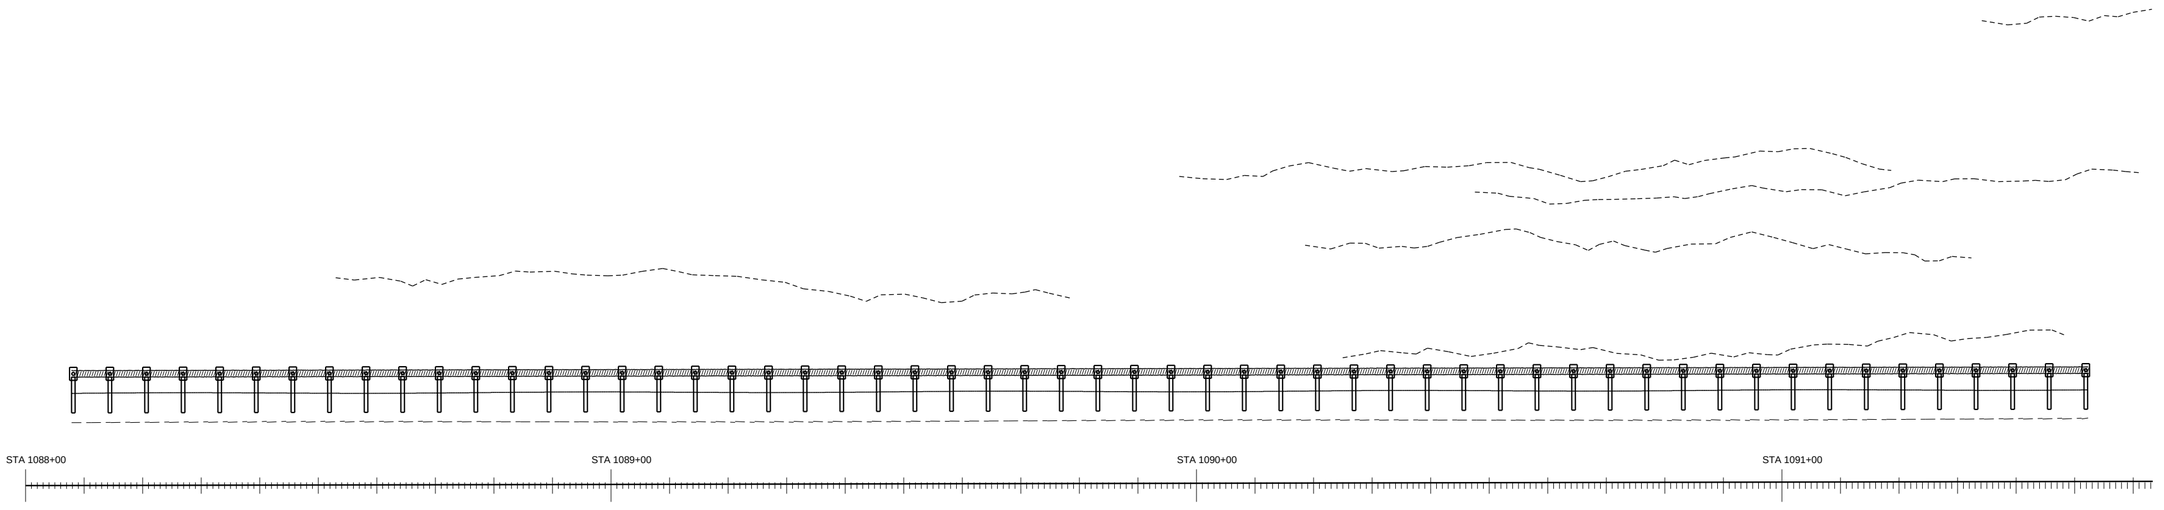


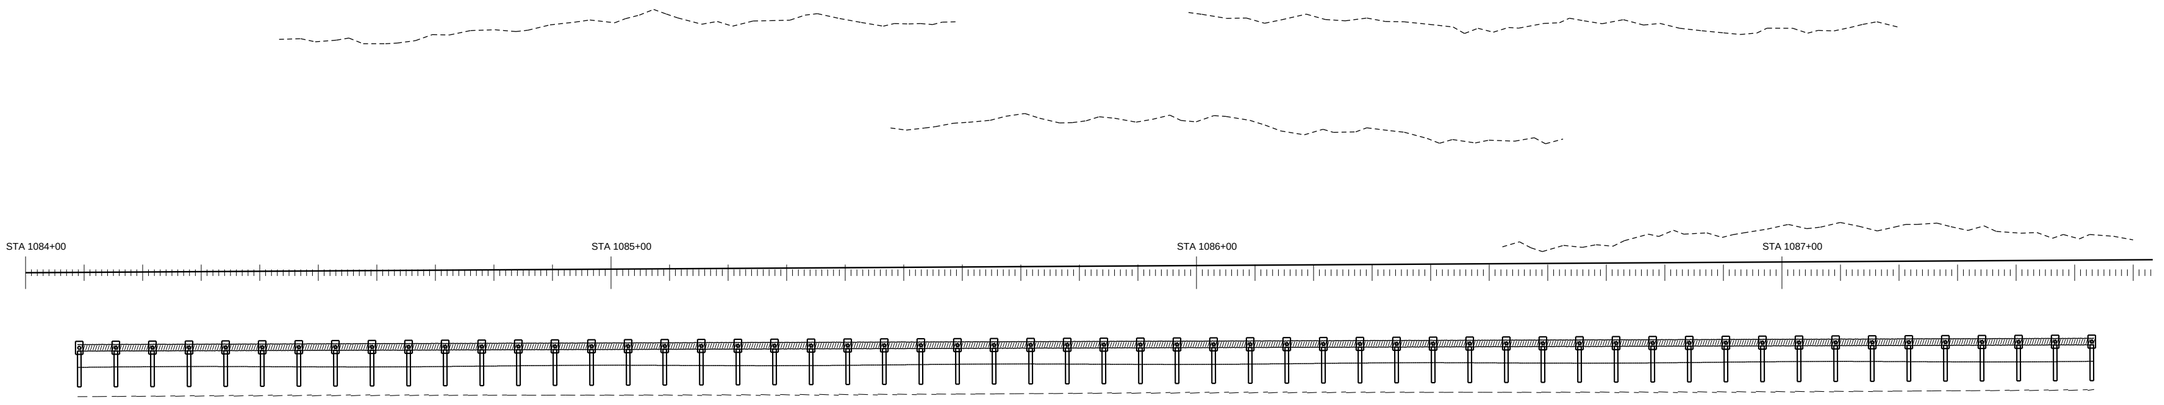


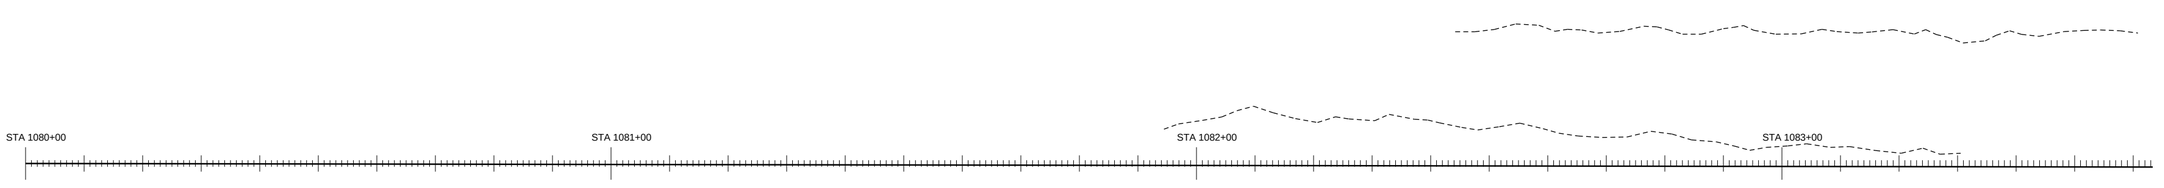


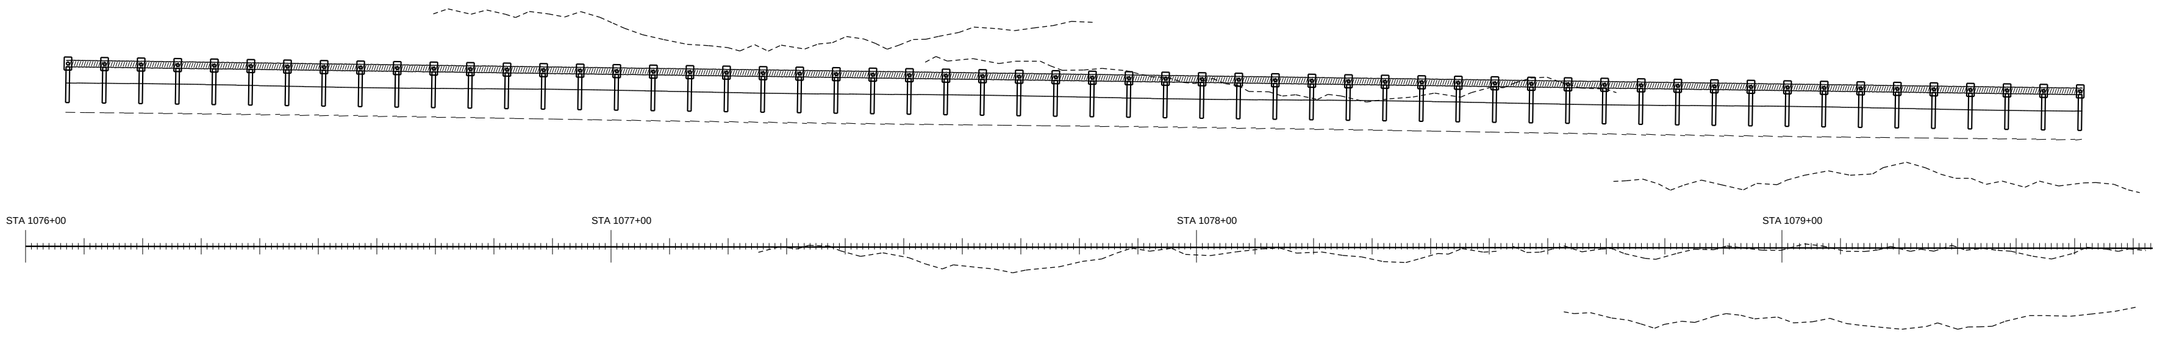


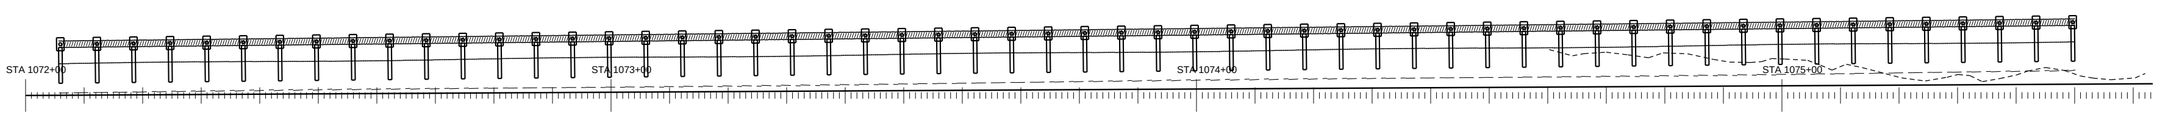


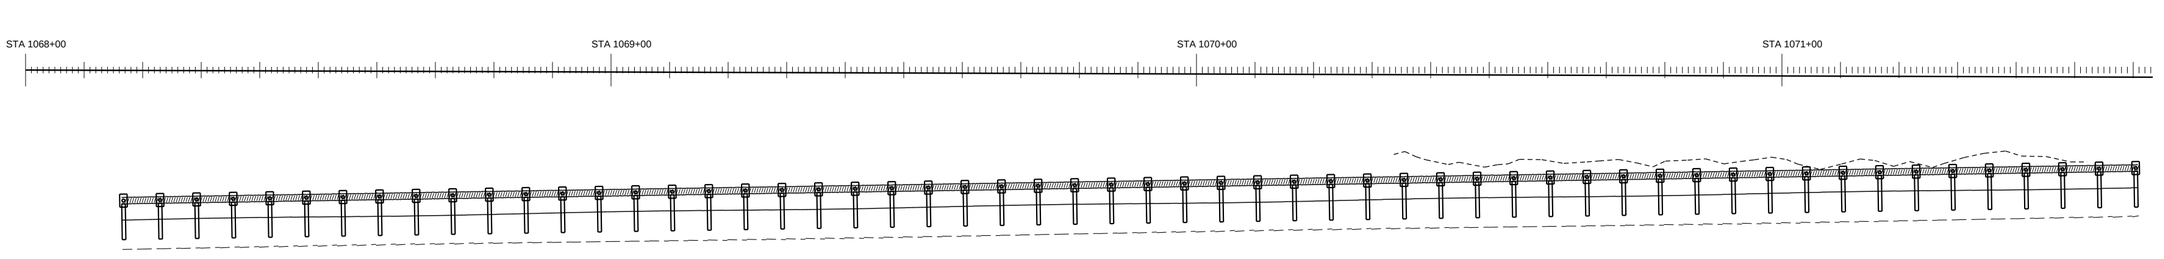


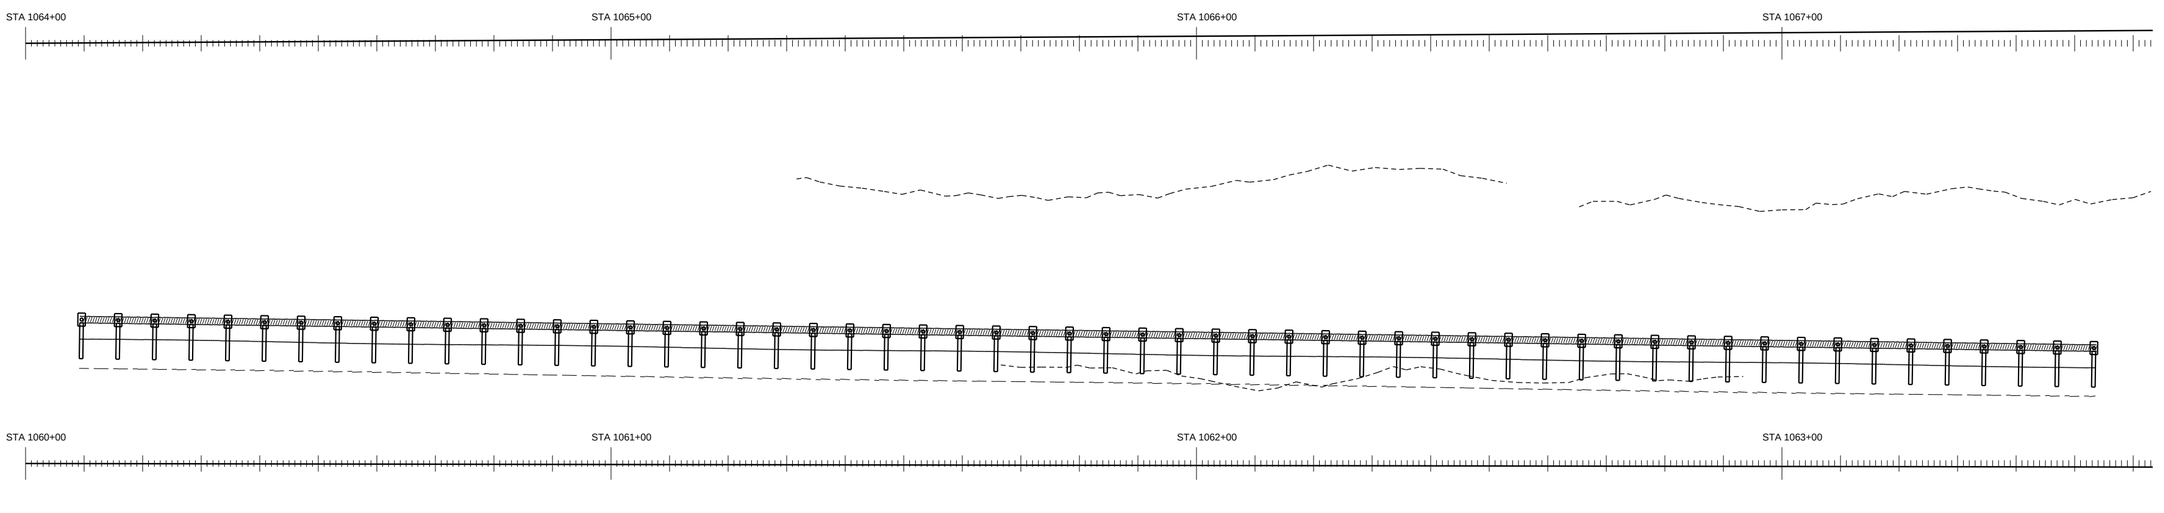


PAY ITEM 536-1-1 GUARDRAIL ROADWAY (TL-3)

PAY ITEM 536-85-24 END TREATMENT

GUARANTEED FENCE CORP

FIN. PROJ. ID 441234-1-52-01

SHEET 65 OF 120

SHEET NO. 165

ROADWAY PLAN SCALE: 1" = 20'

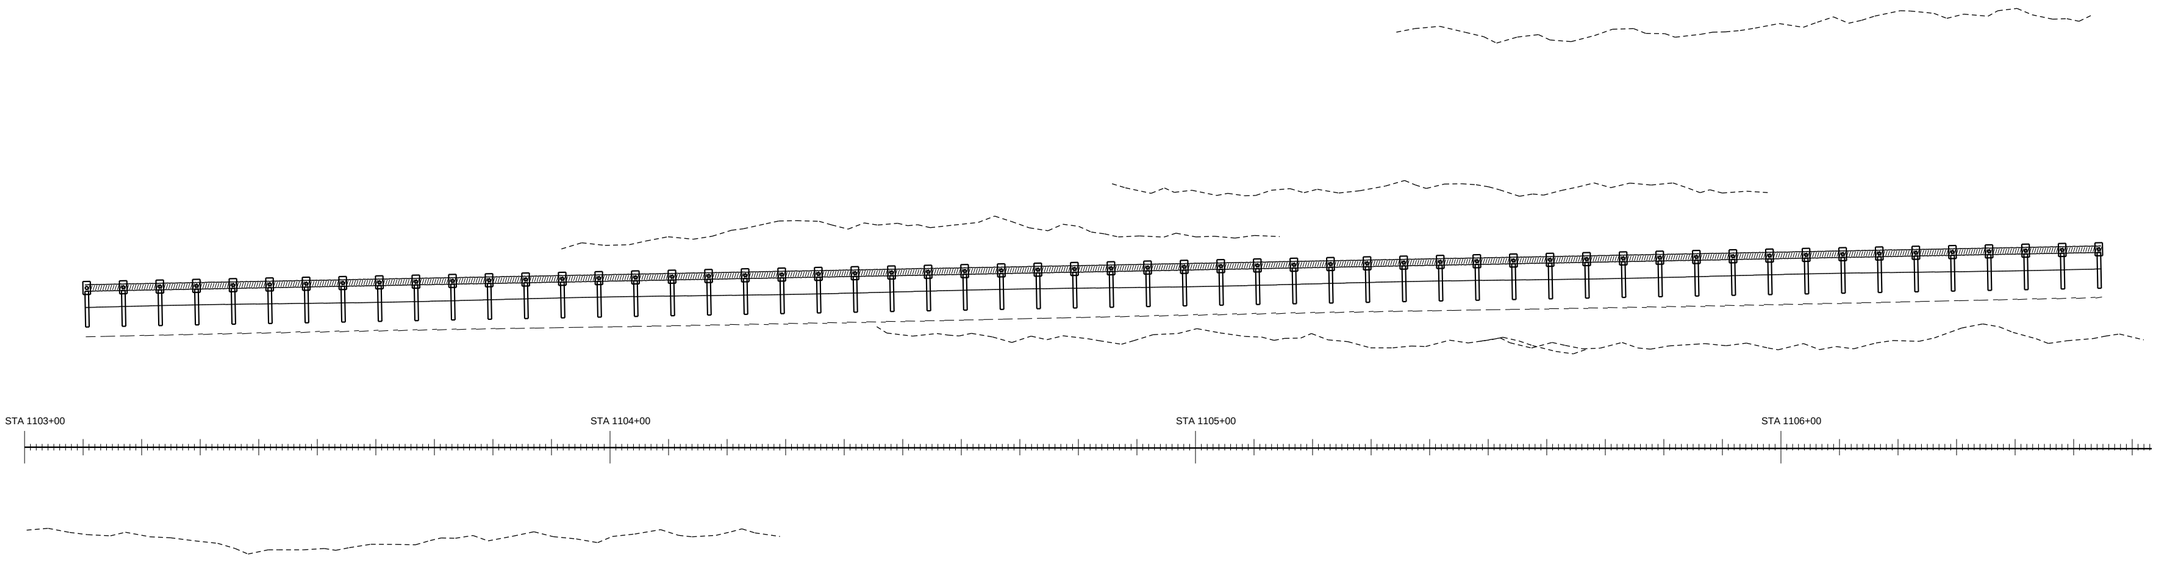


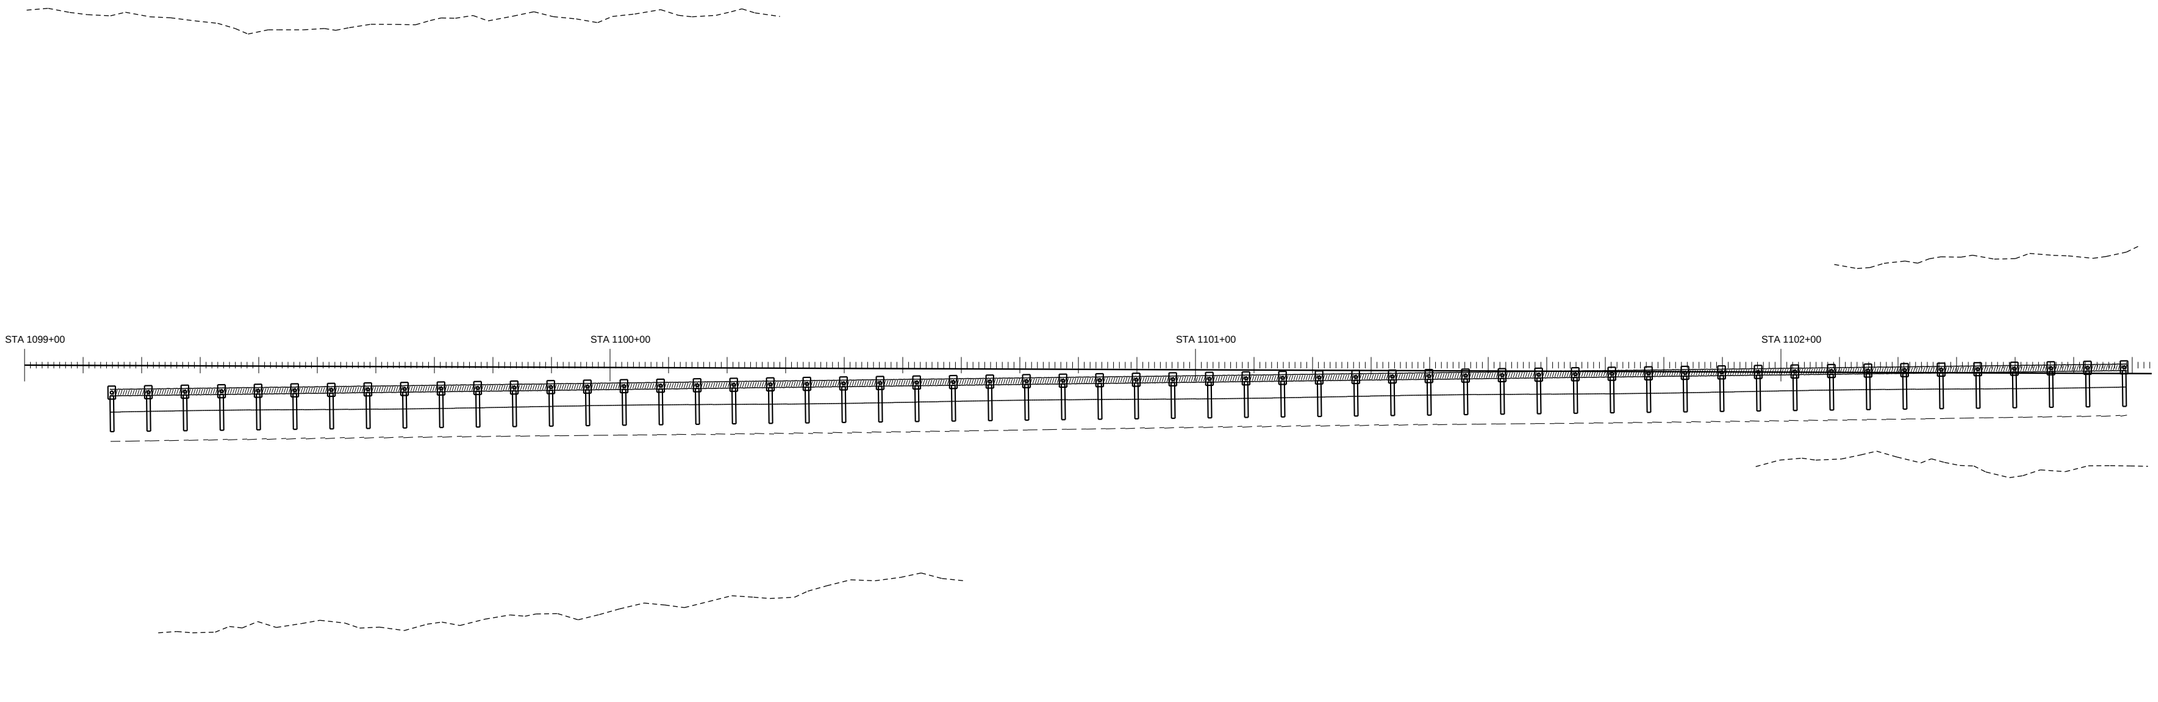


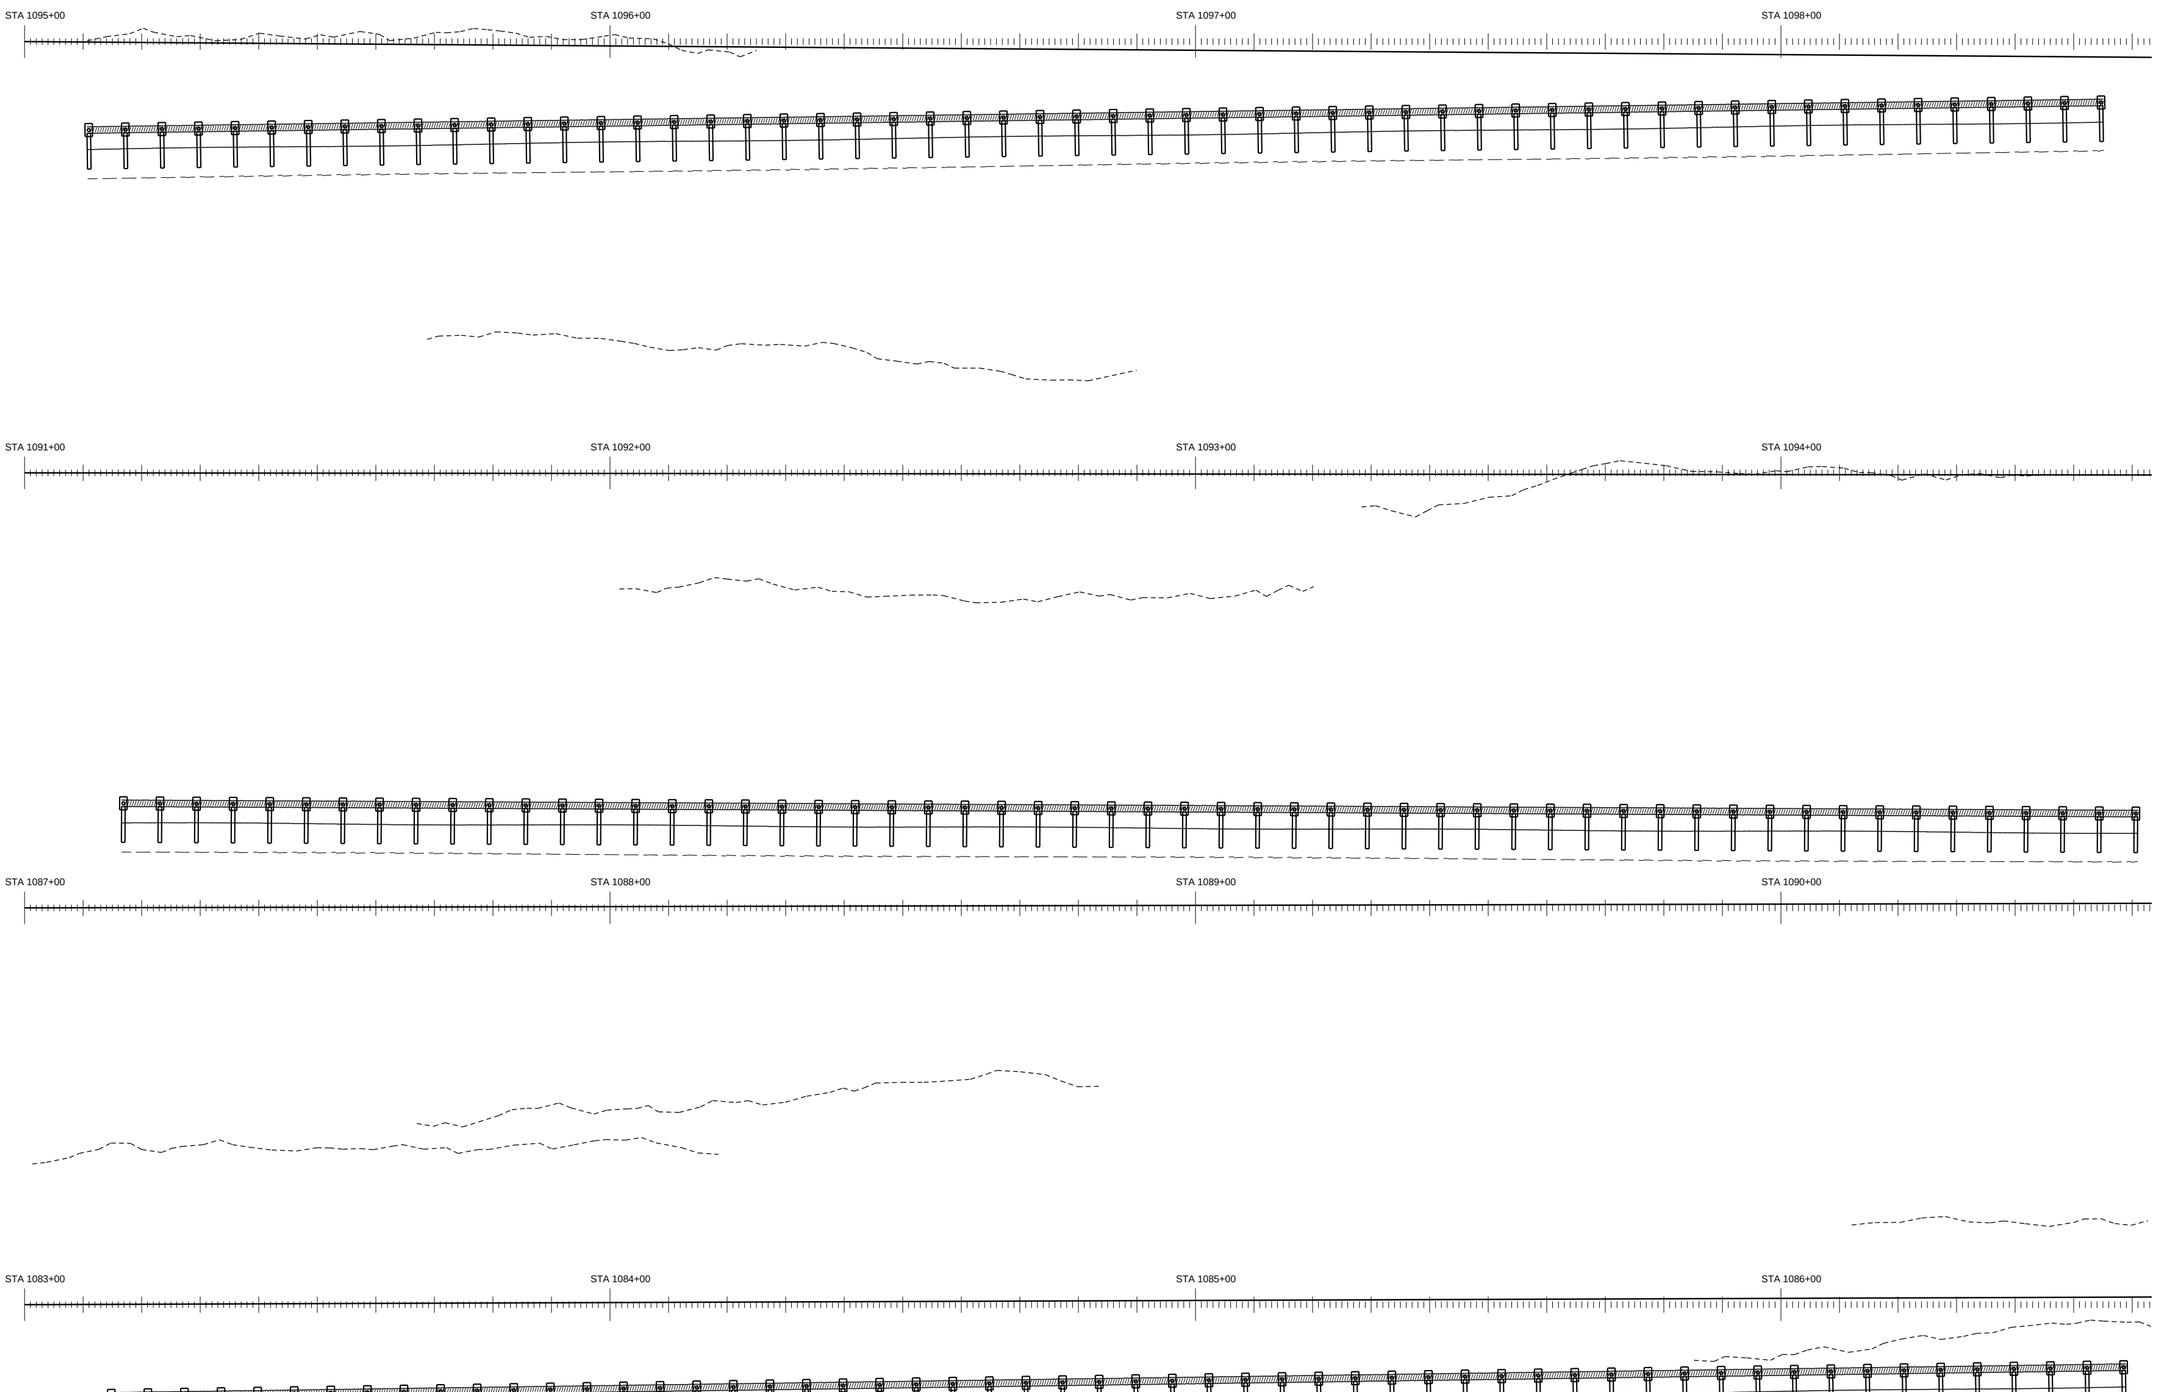





PAY ITEM 536-1-1 GUARDRAIL ROADWAY (TL-3)

PAY ITEM 536-85-24 END TREATMENT

GUARANTEED FENCE CORP

FIN. PROJ. ID 441234-1-52-01

SHEET 66 OF 120

SHEET NO. 166

ROADWAY PLAN SCALE: 1" = 20'

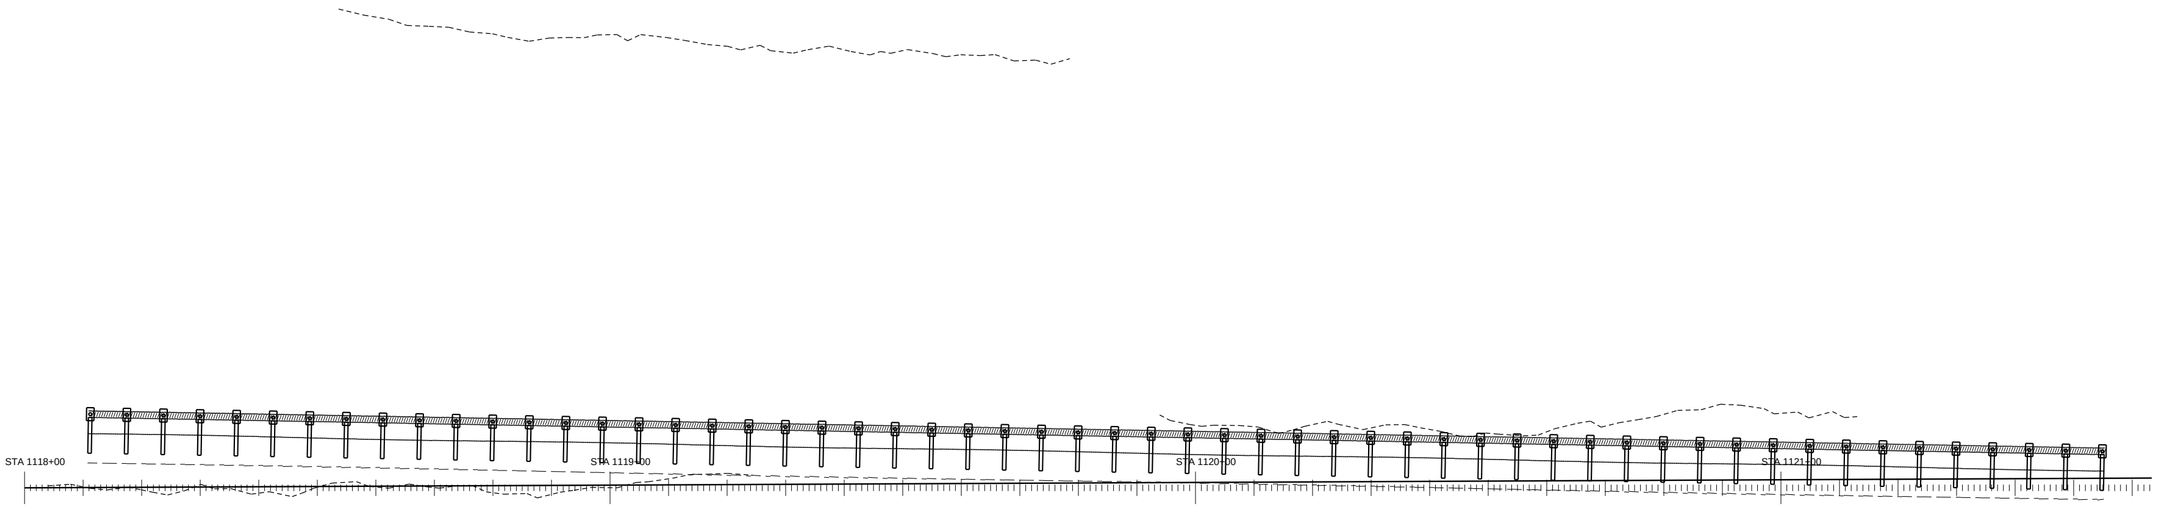


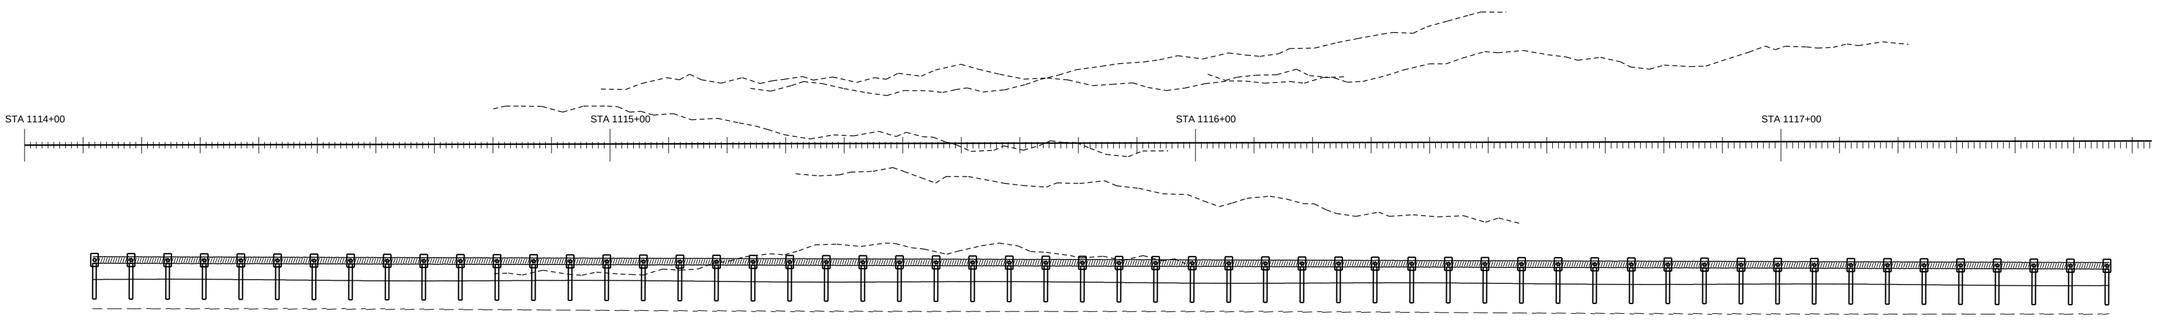


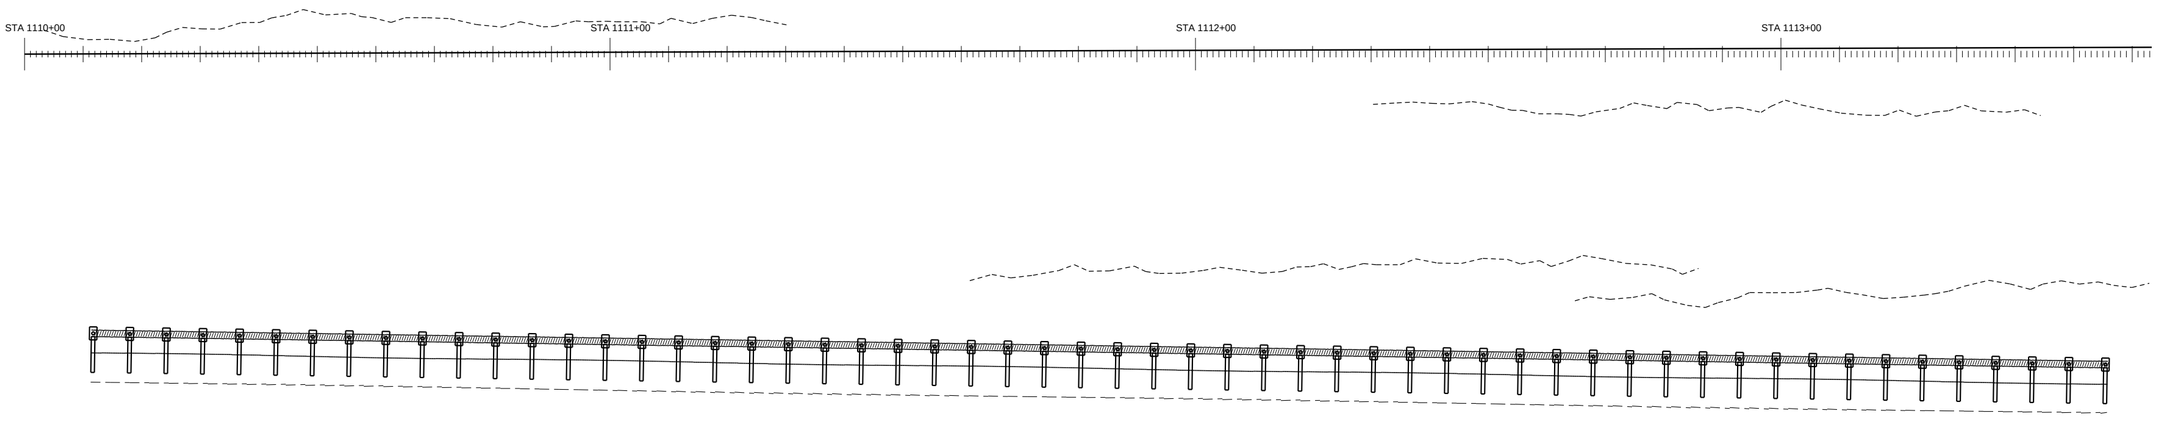


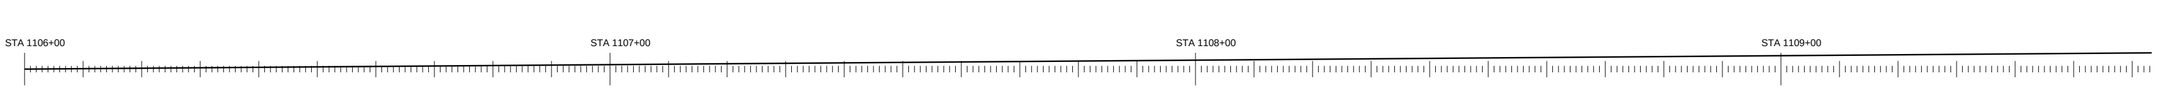


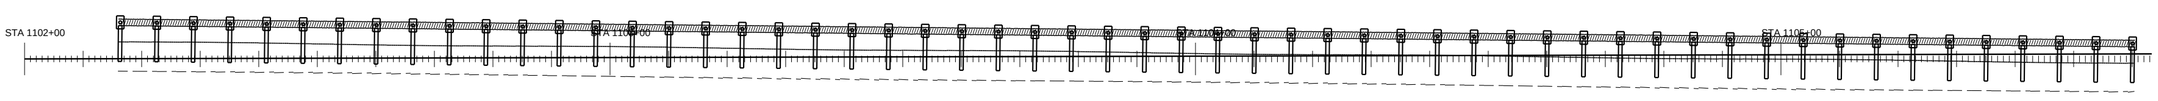


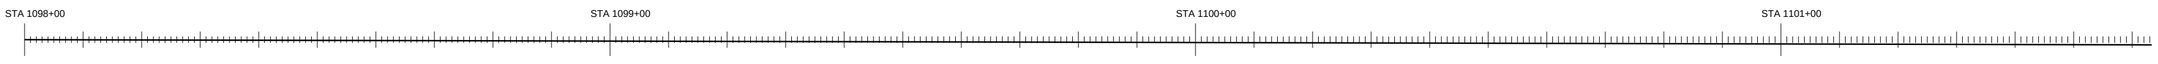


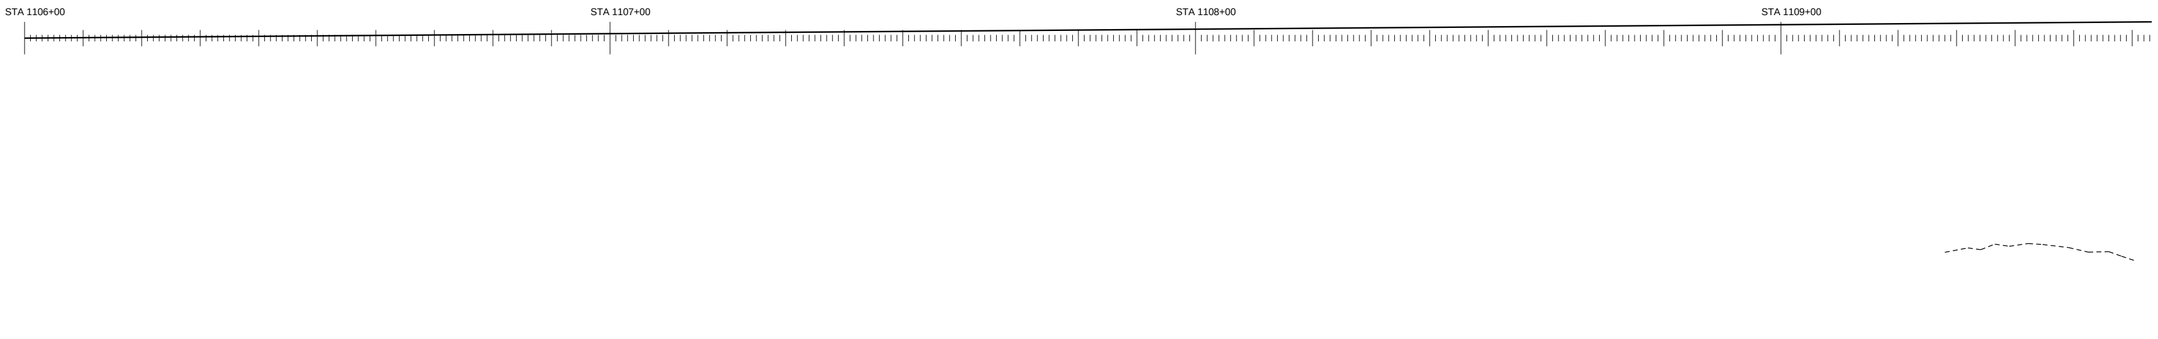


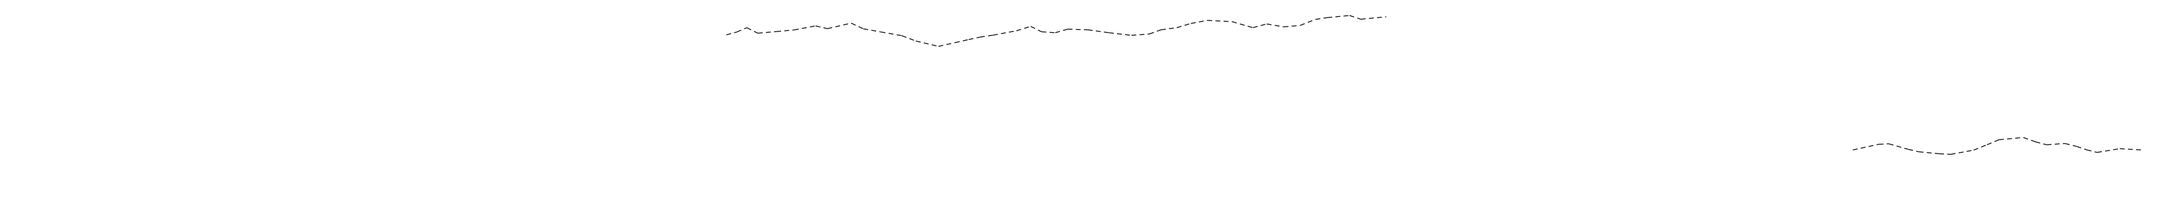


PAY ITEM 536-1-1 GUARDRAIL ROADWAY (TL-3)

PAY ITEM 536-85-24 END TREATMENT

GUARANTEED FENCE CORP

FIN. PROJ. ID 441234-1-52-01

SHEET 67 OF 120

SHEET NO. 167

ROADWAY PLAN SCALE: 1" = 20'




PAY ITEM 536-1-1 GUARDRAIL ROADWAY (TL-3)

PAY ITEM 536-85-24 END TREATMENT

GUARANTEED FENCE CORP

FIN. PROJ. ID 441234-1-52-01

SHEET 68 OF 120

SHEET NO. 168

ROADWAY PLAN SCALE: 1" = 20'

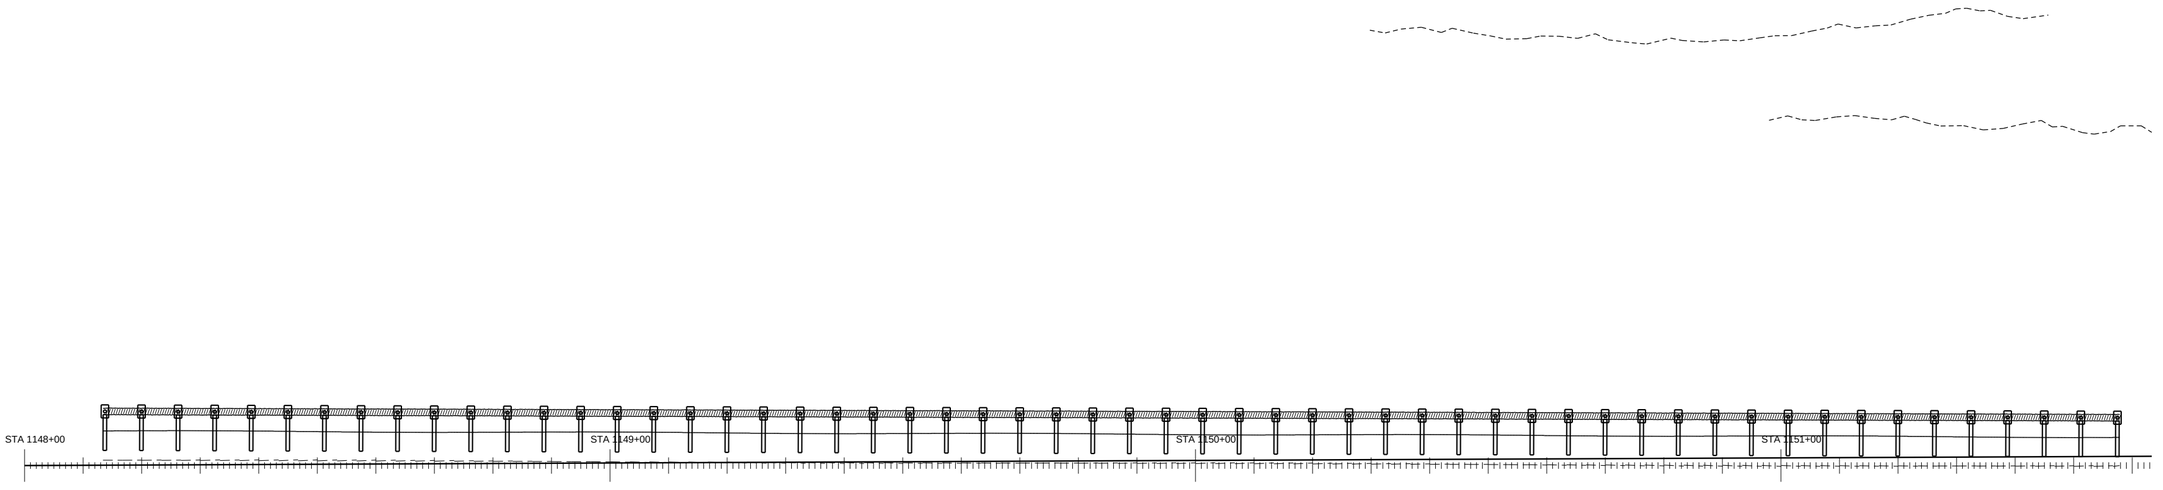


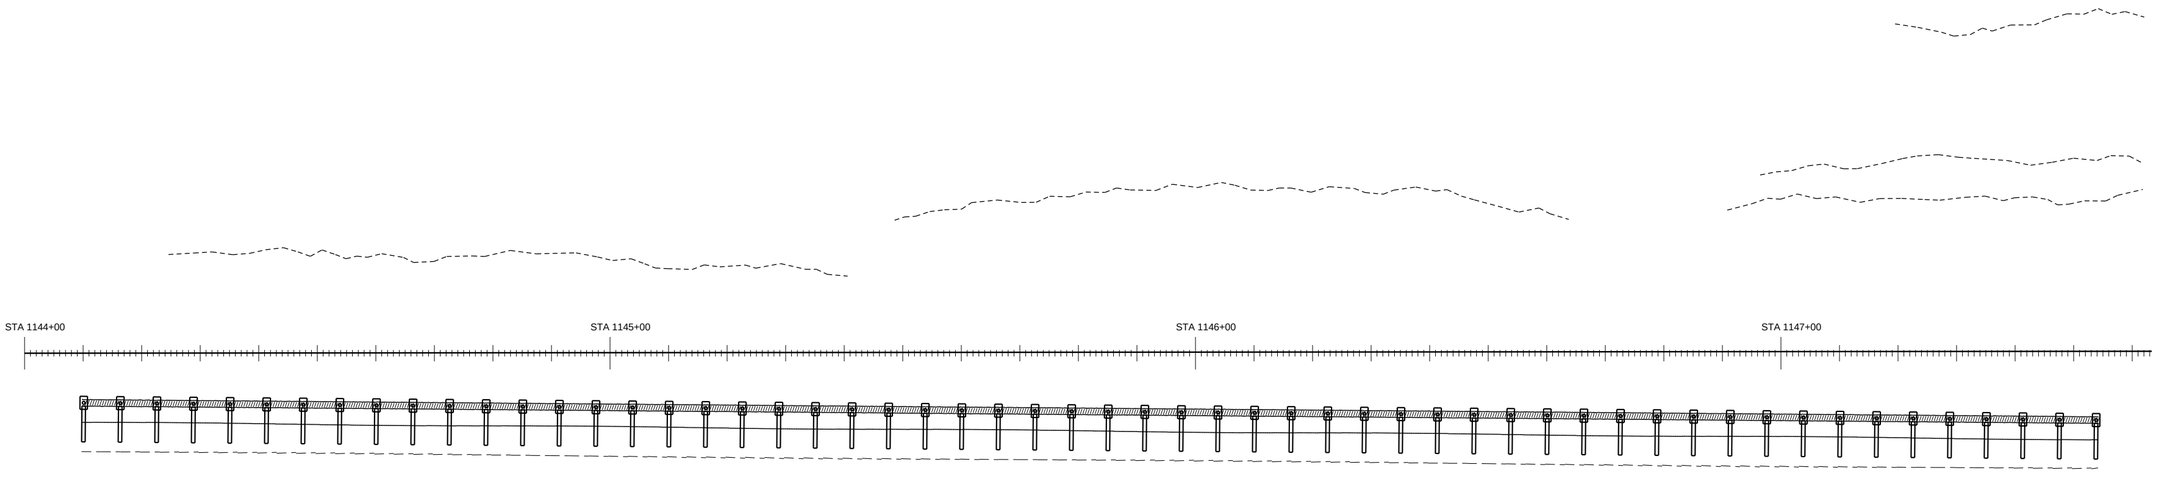


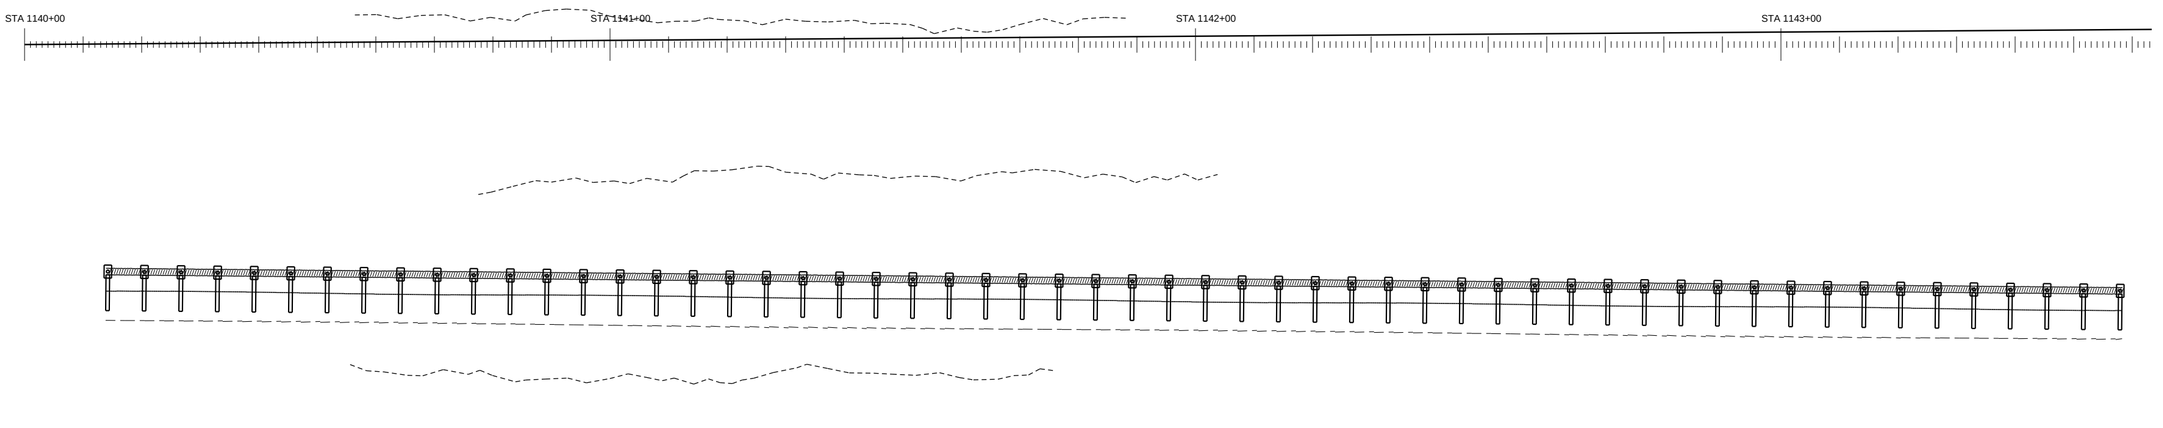


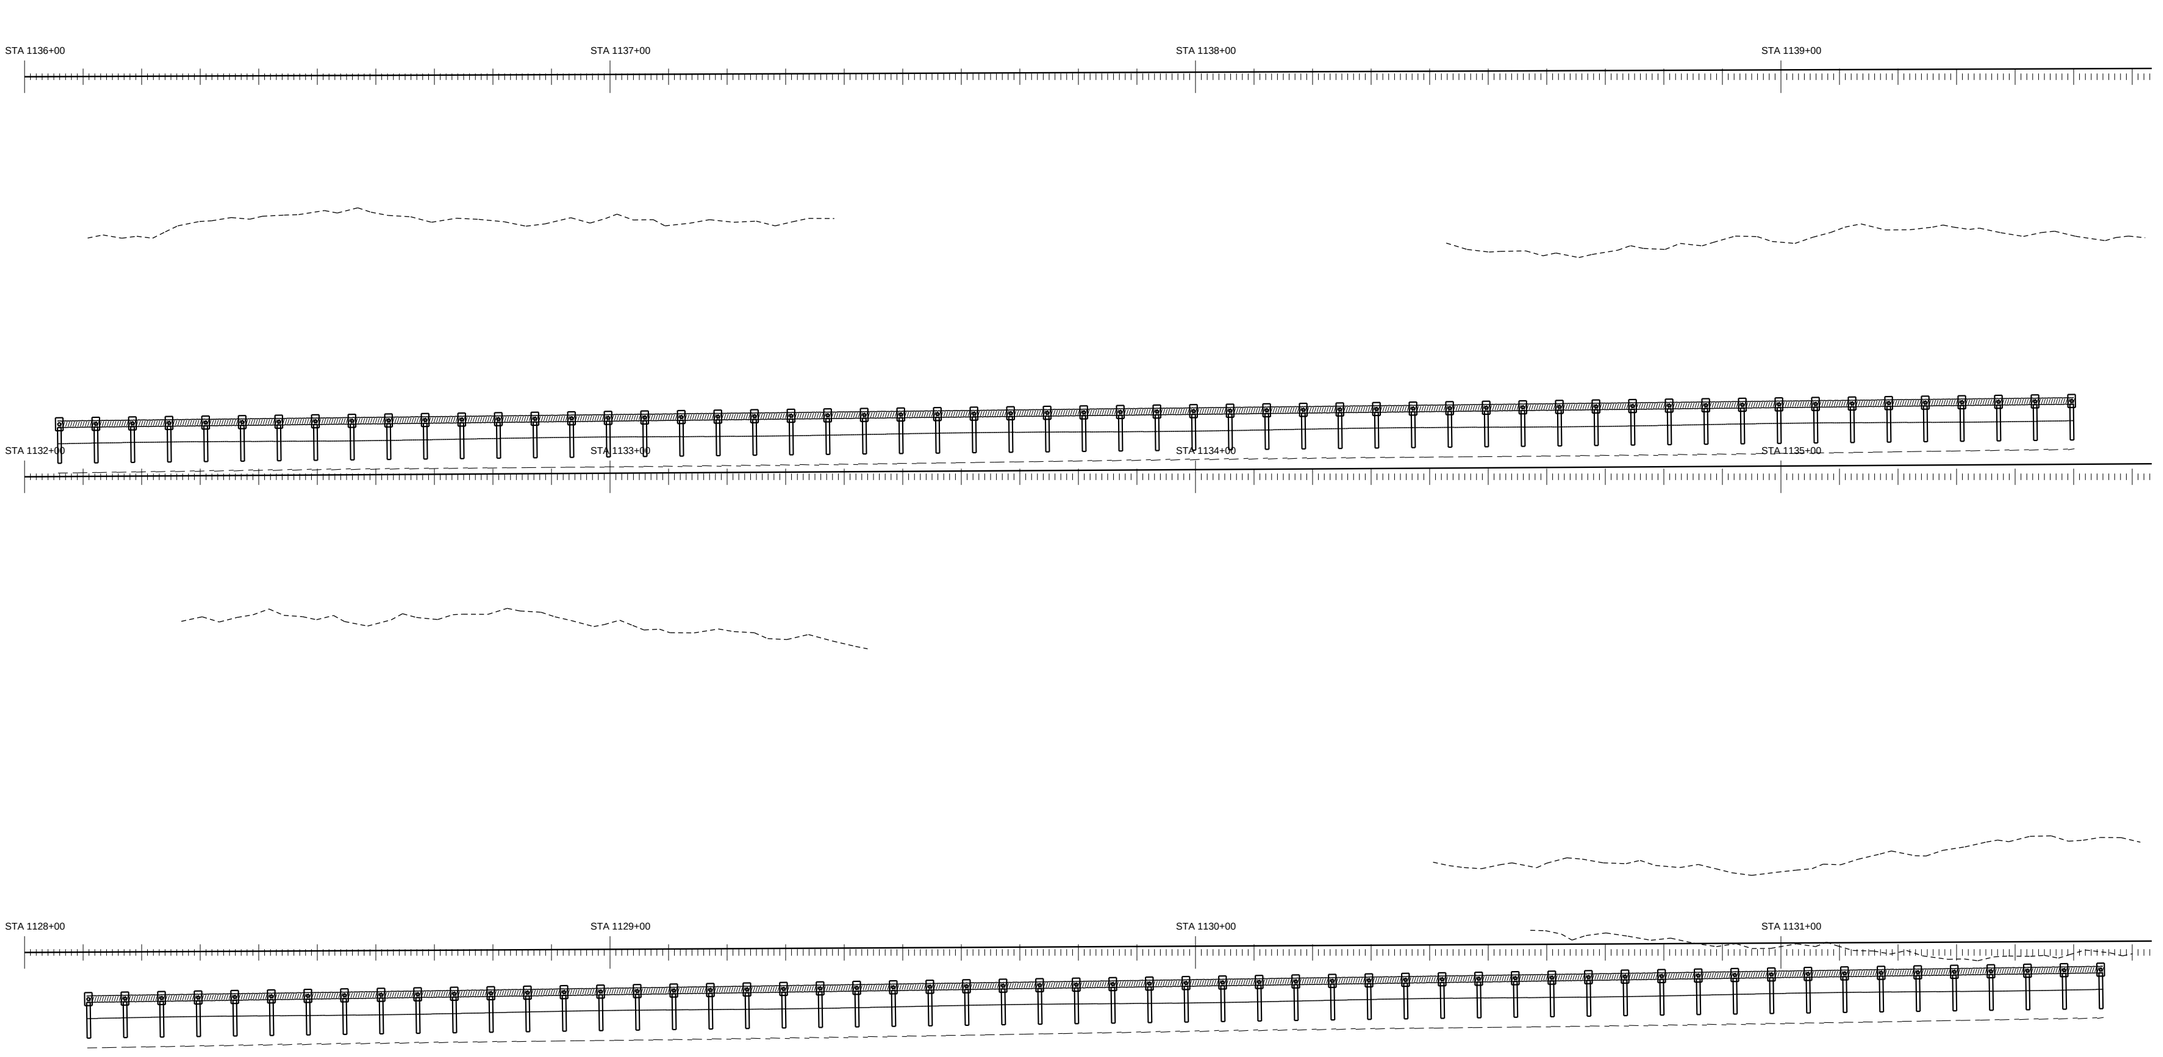


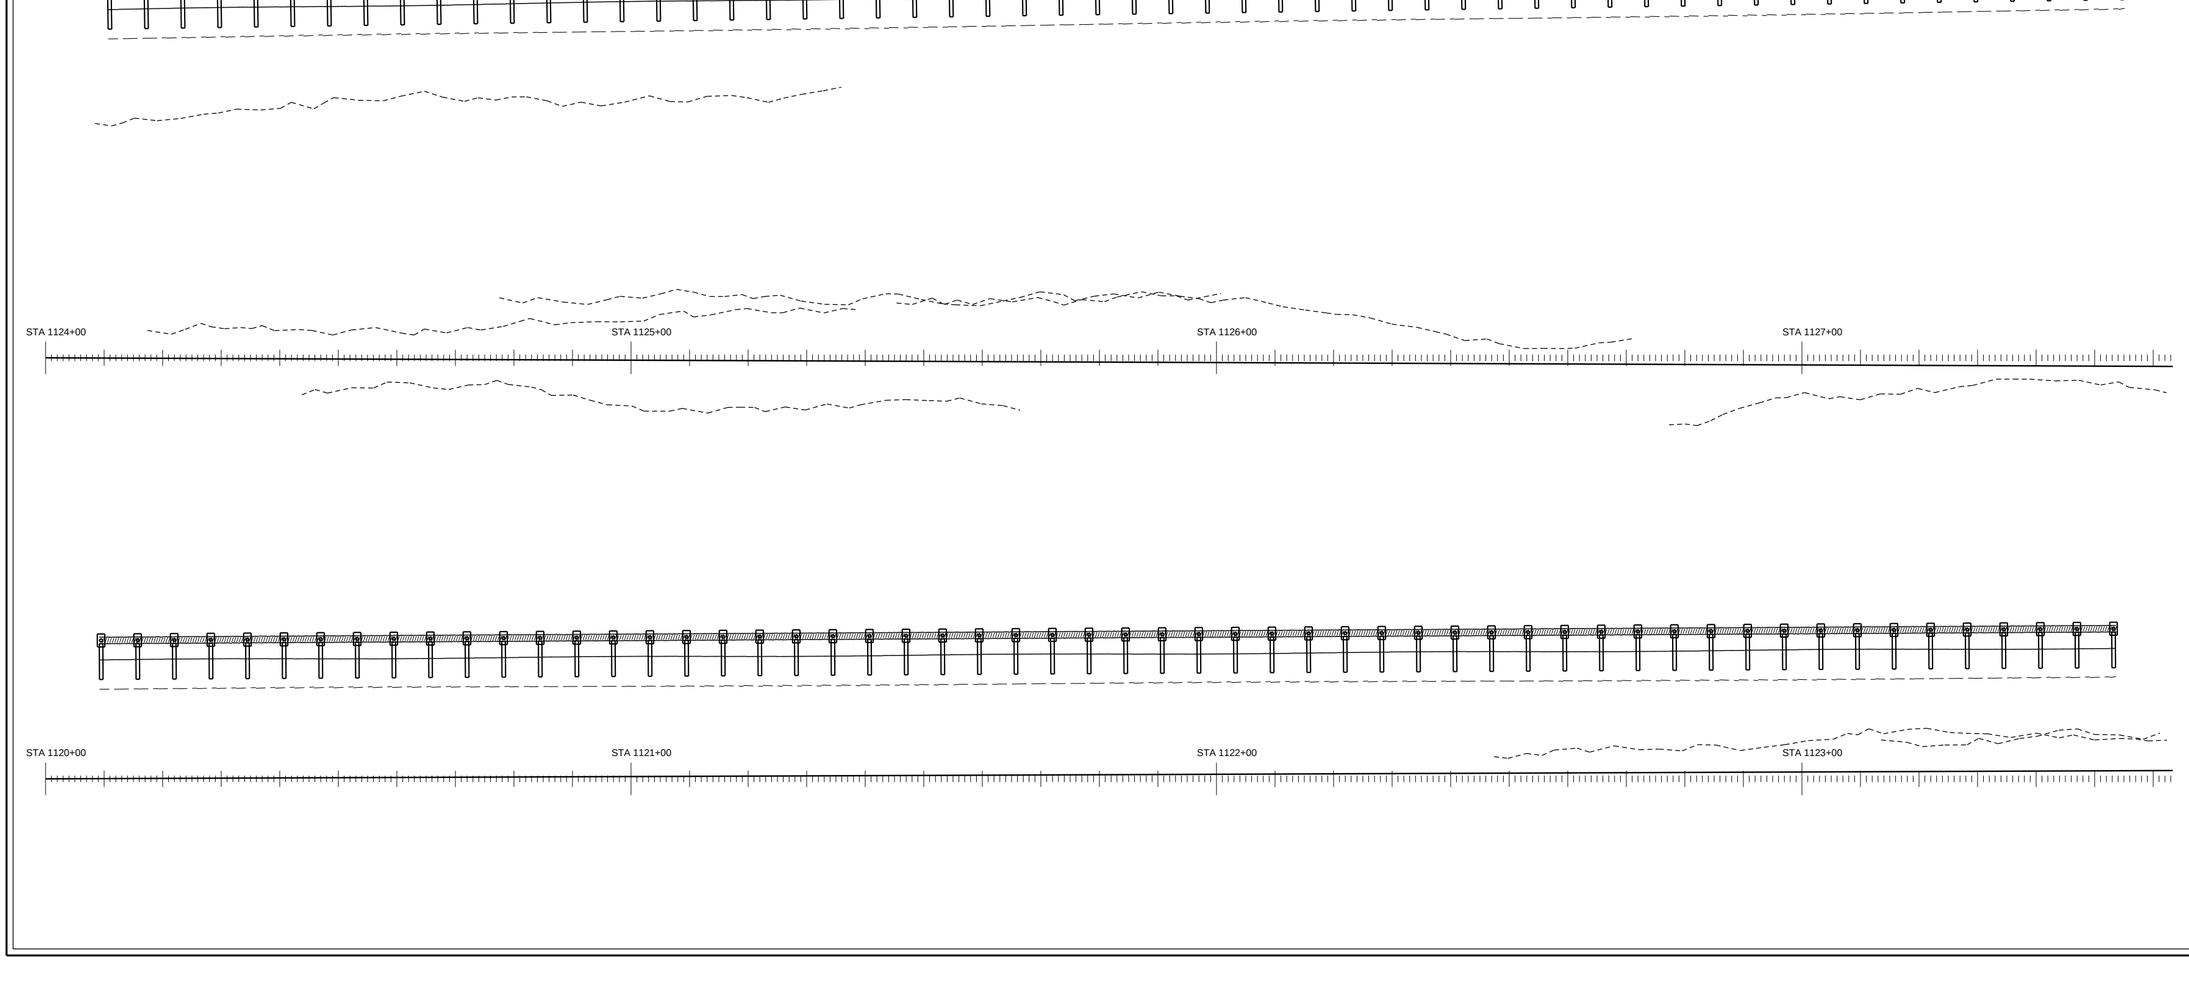











PAY ITEM 536-1-1 GUARDRAIL ROADWAY (TL-3)

PAY ITEM 536-85-24 END TREATMENT

GUARANTEED FENCE CORP

FIN. PROJ. ID 441234-1-52-01

SHEET 69 OF 120

SHEET NO. 169

ROADWAY PLAN SCALE: 1" = 20'




PAY ITEM 536-1-1 GUARDRAIL ROADWAY (TL-3)

PAY ITEM 536-85-24 END TREATMENT

GUARANTEED FENCE CORP

FIN. PROJ. ID 441234-1-52-01

SHEET 70 OF 120

SHEET NO. 170

ROADWAY PLAN SCALE: 1" = 20'

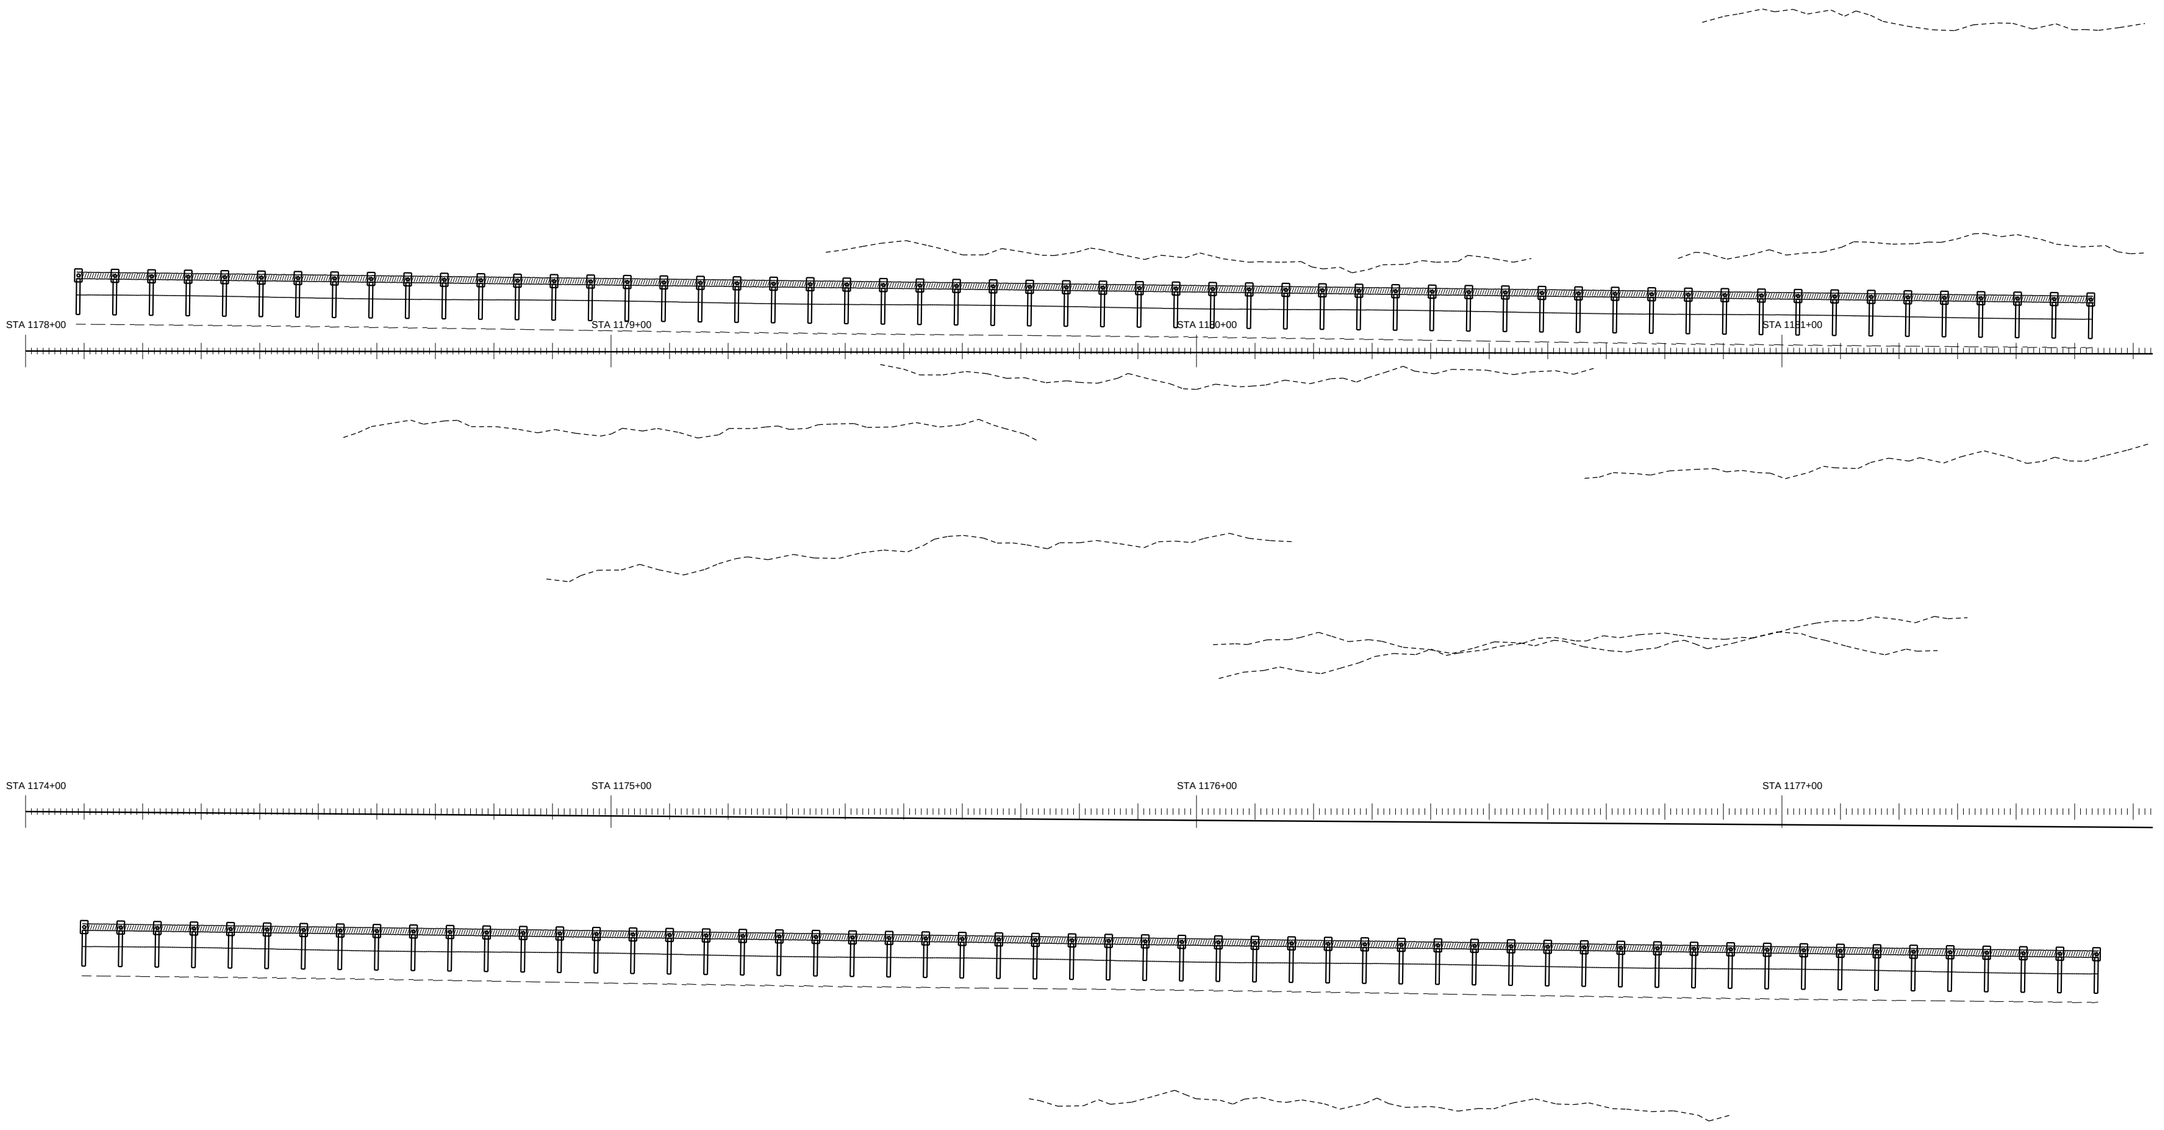





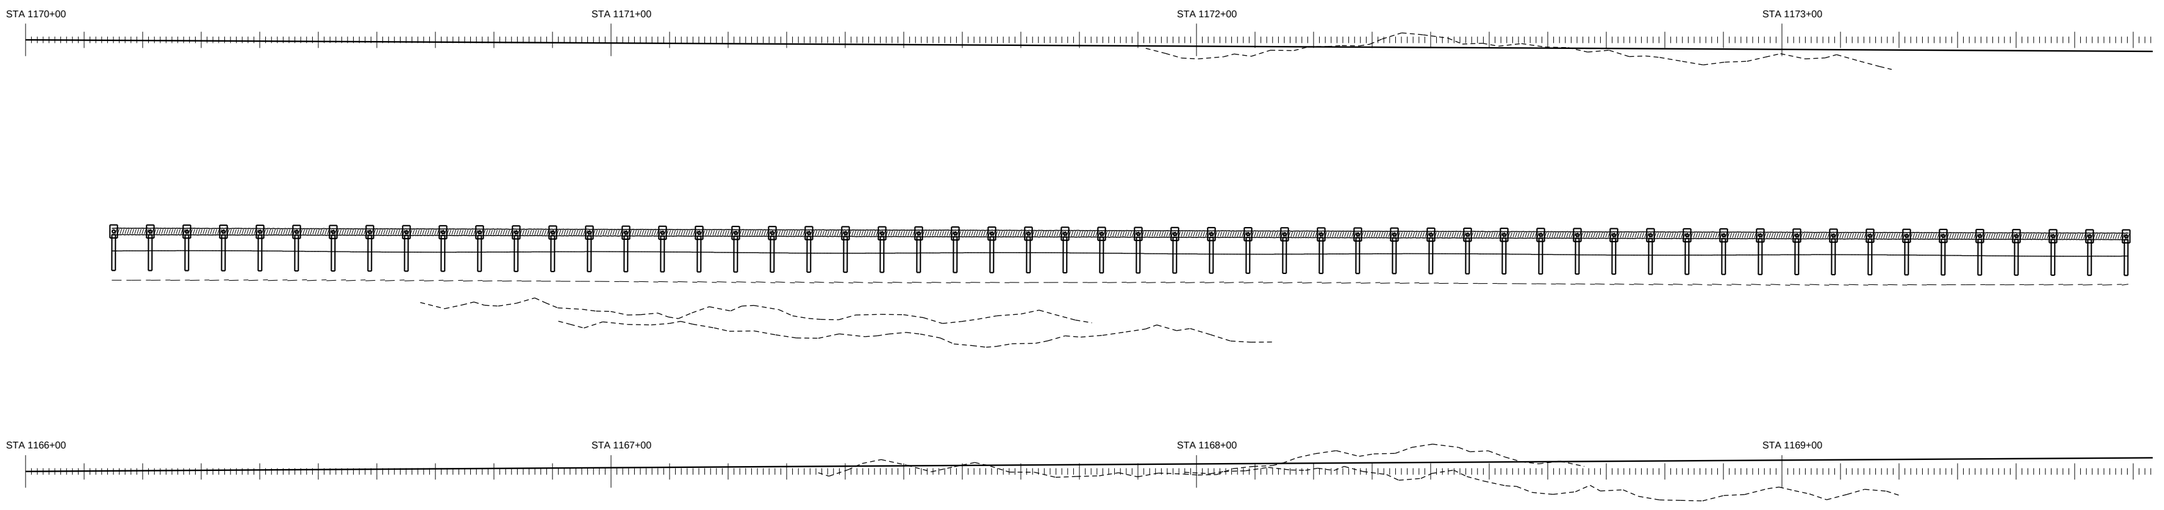


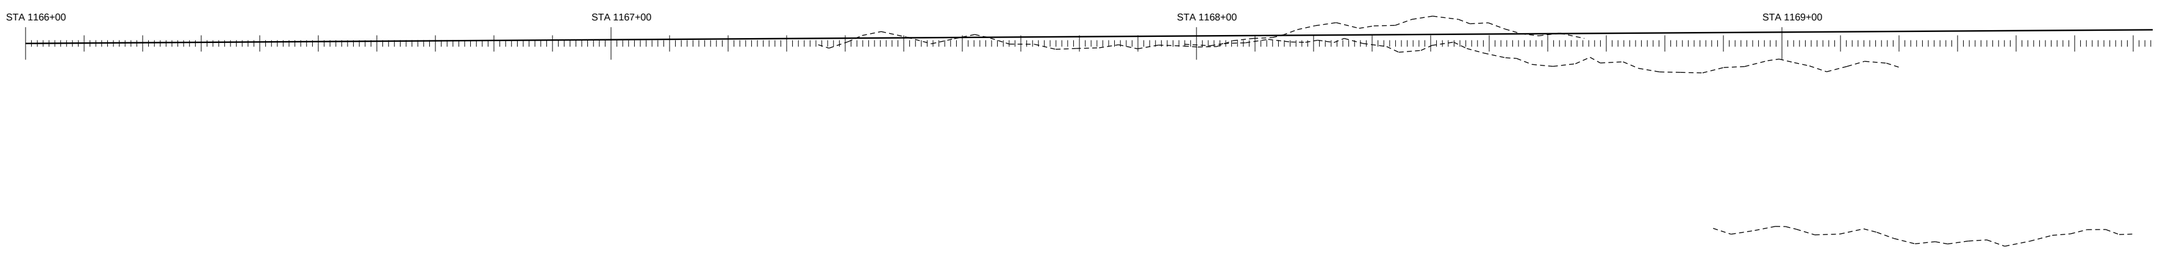


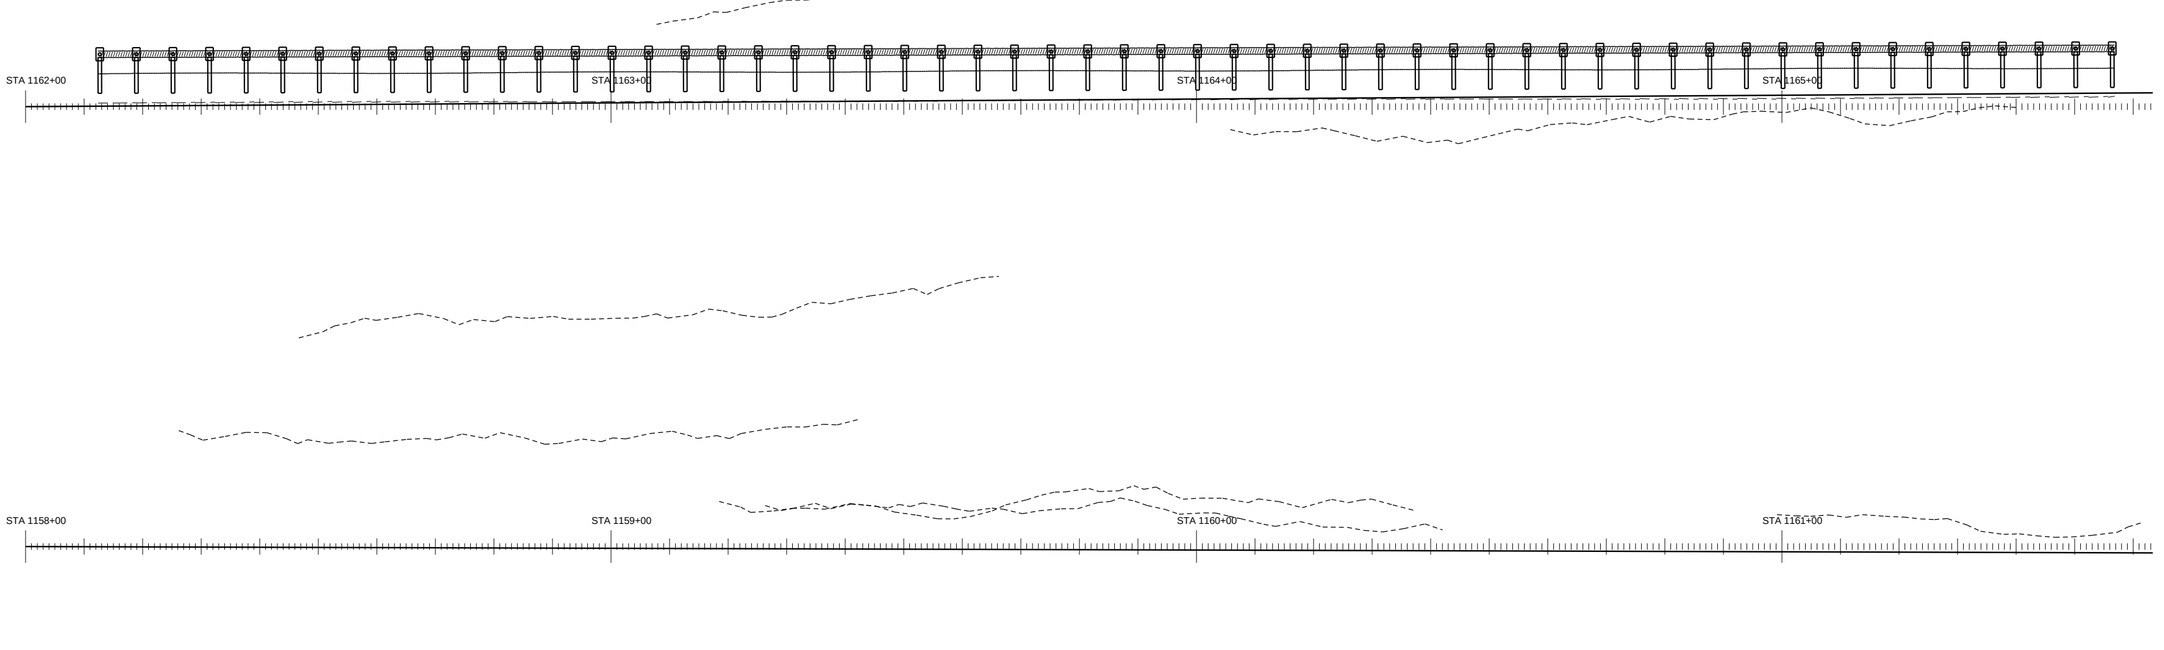


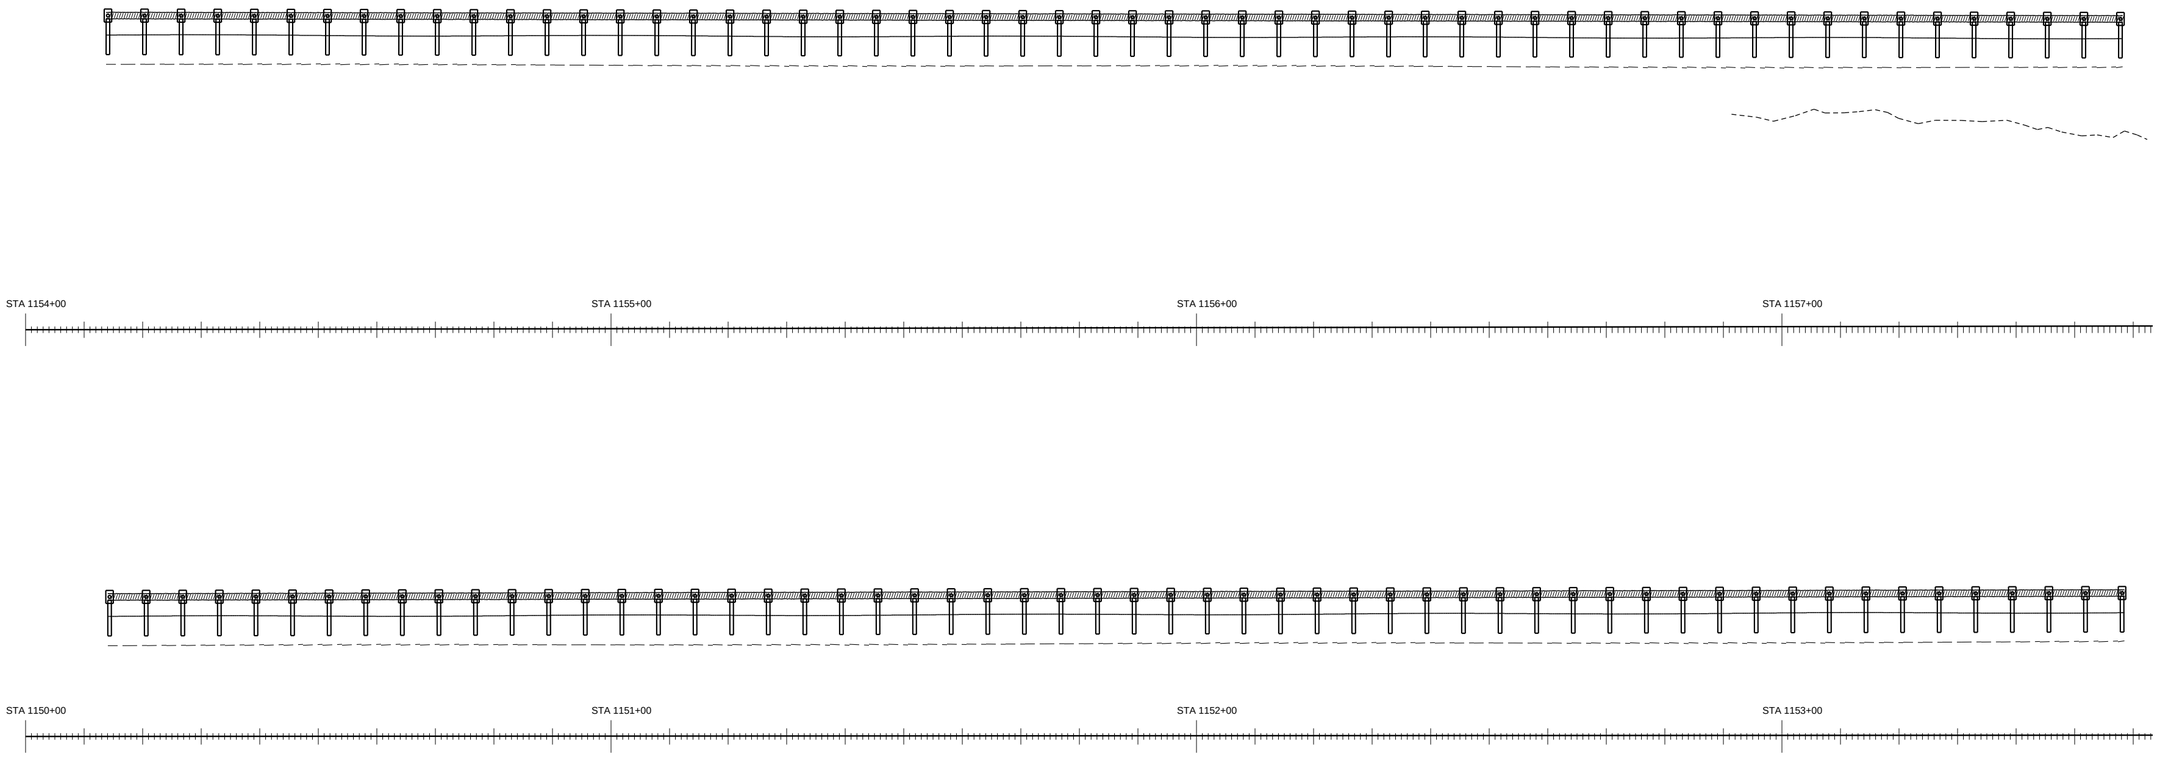








PAY ITEM 536-1-1 GUARDRAIL ROADWAY (TL-3)

PAY ITEM 536-85-24 END TREATMENT

GUARANTEED FENCE CORP

FIN. PROJ. ID 441234-1-52-01

SHEET 71 OF 120

SHEET NO. 171

ROADWAY PLAN SCALE: 1" = 20'




PAY ITEM 536-1-1 GUARDRAIL ROADWAY (TL-3)

PAY ITEM 536-85-24 END TREATMENT

GUARANTEED FENCE CORP

FIN. PROJ. ID 441234-1-52-01

SHEET 72 OF 120

SHEET NO. 172

ROADWAY PLAN SCALE: 1" = 20'

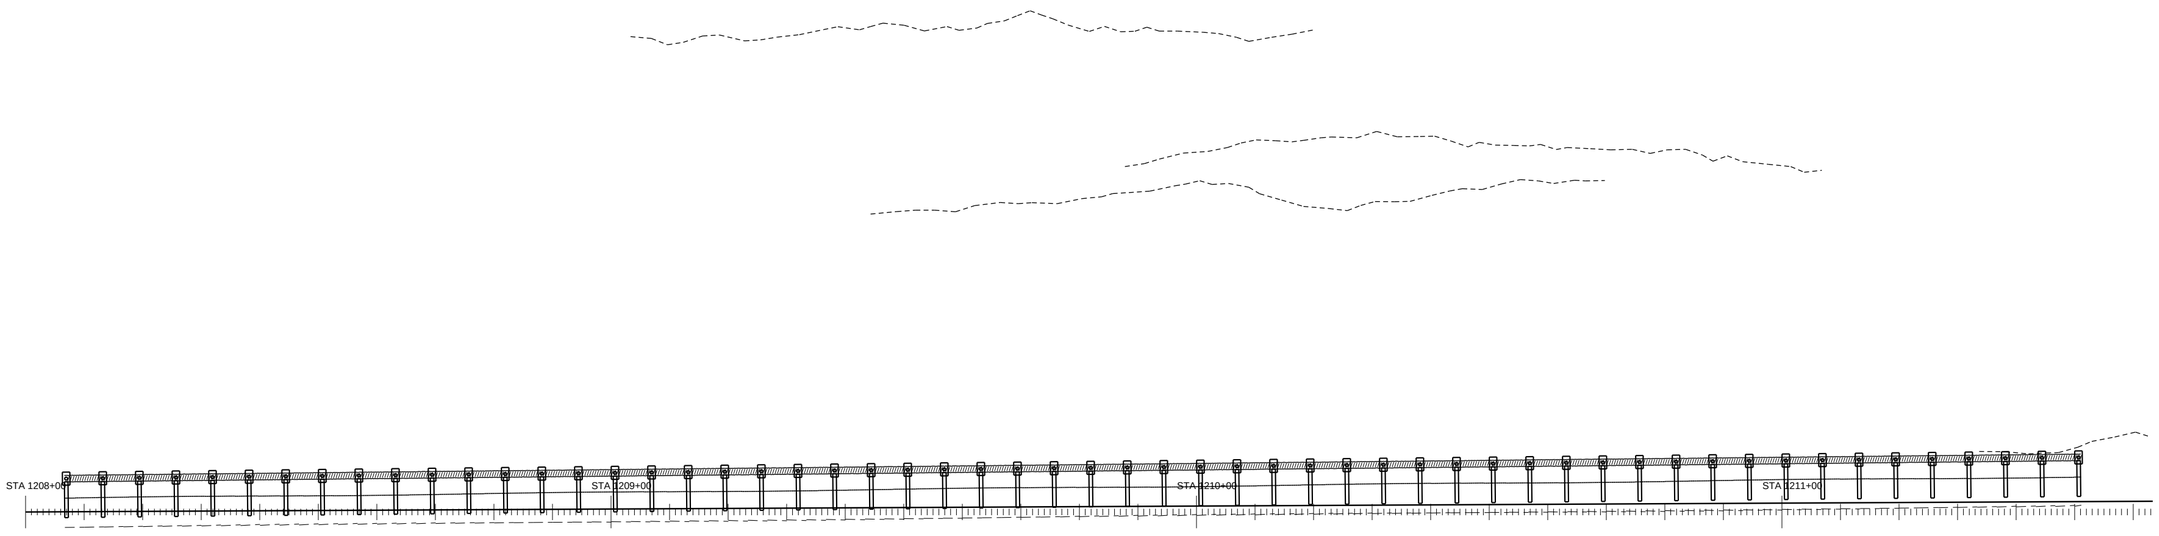


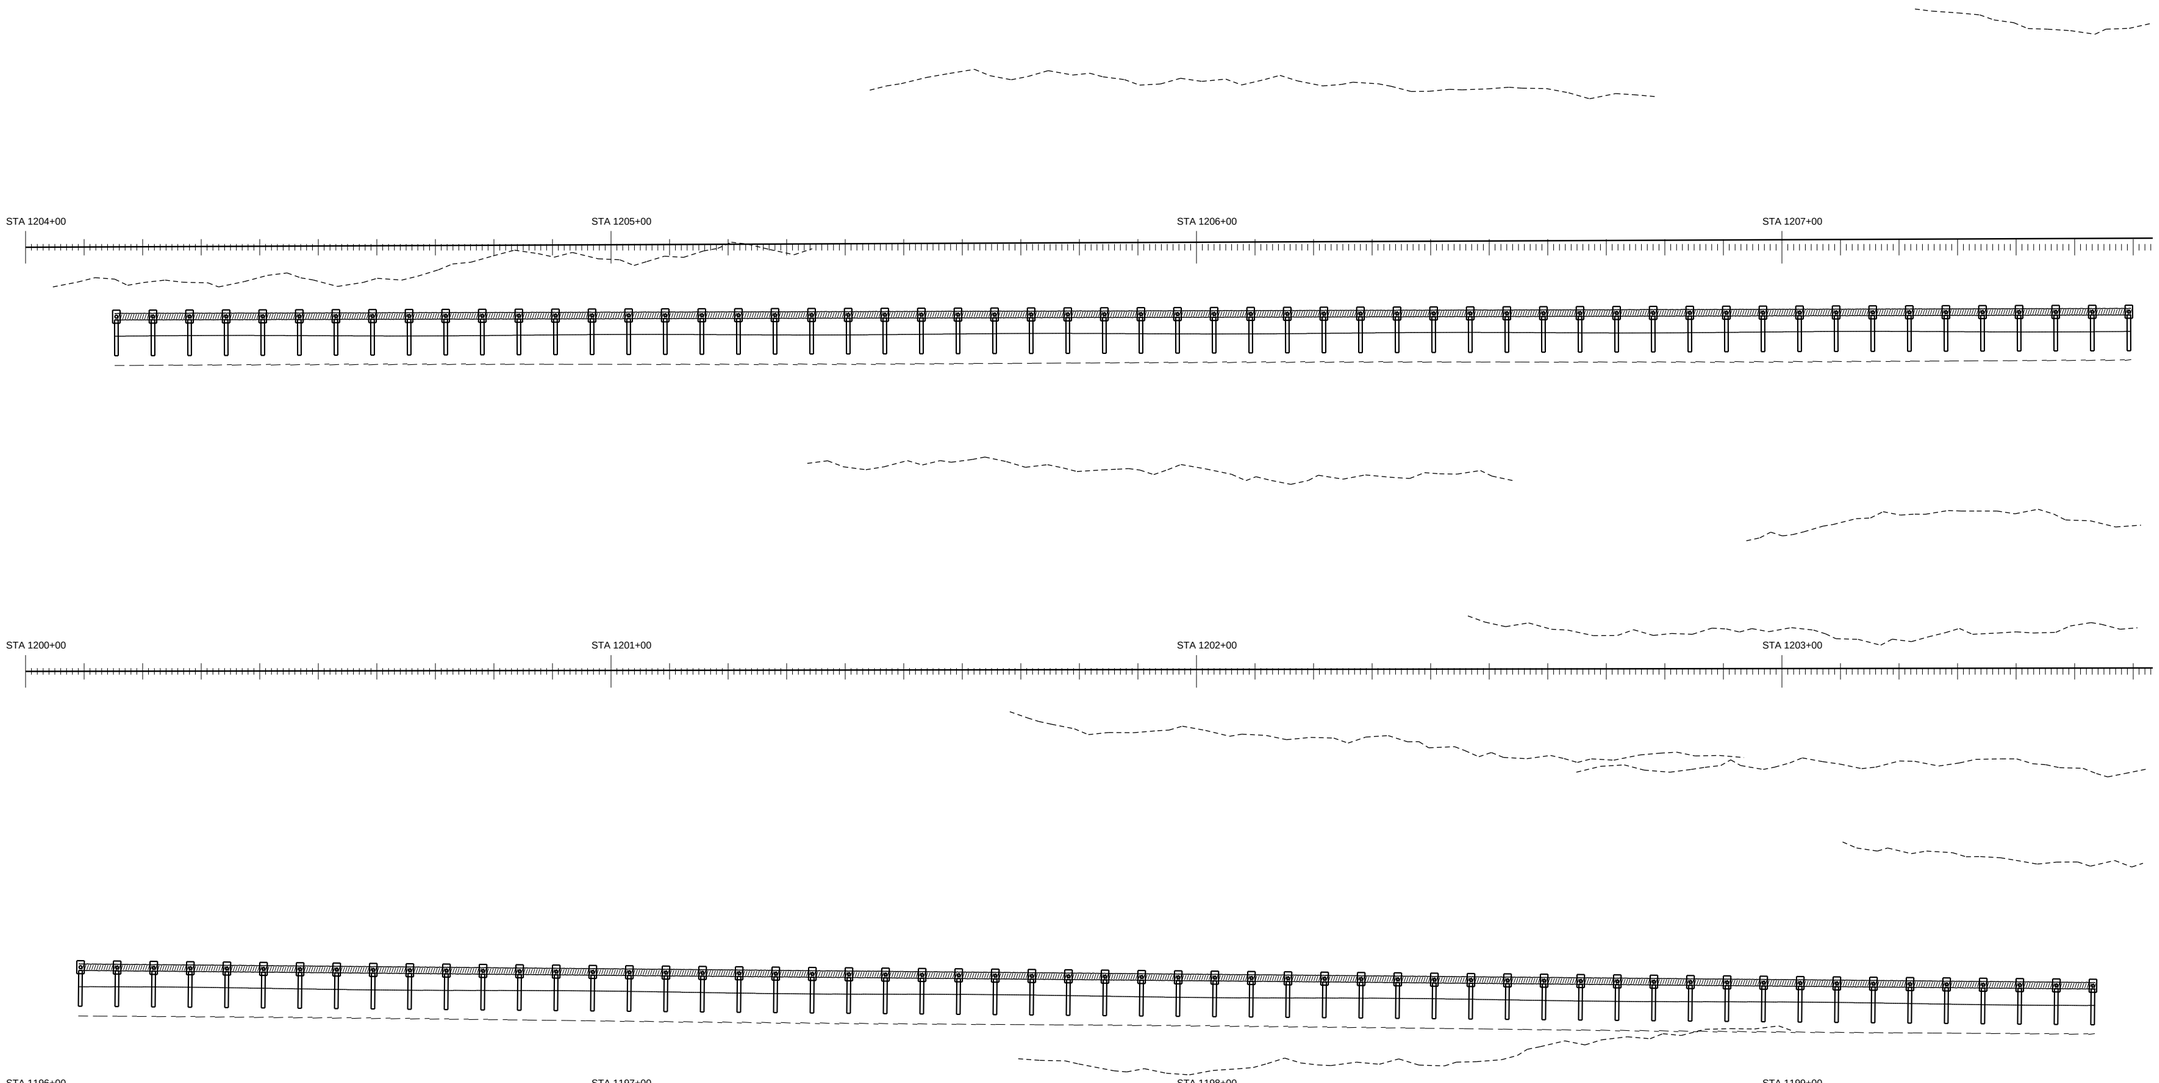


PAY ITEM 536-1-1 GUARDRAIL ROADWAY (TL-3)

PAY ITEM 536-85-24 END TREATMENT

GUARANTEED FENCE CORP

FIN. PROJ. ID 441234-1-52-01

SHEET 73 OF 120

SHEET NO. 173

ROADWAY PLAN SCALE: 1" = 20'

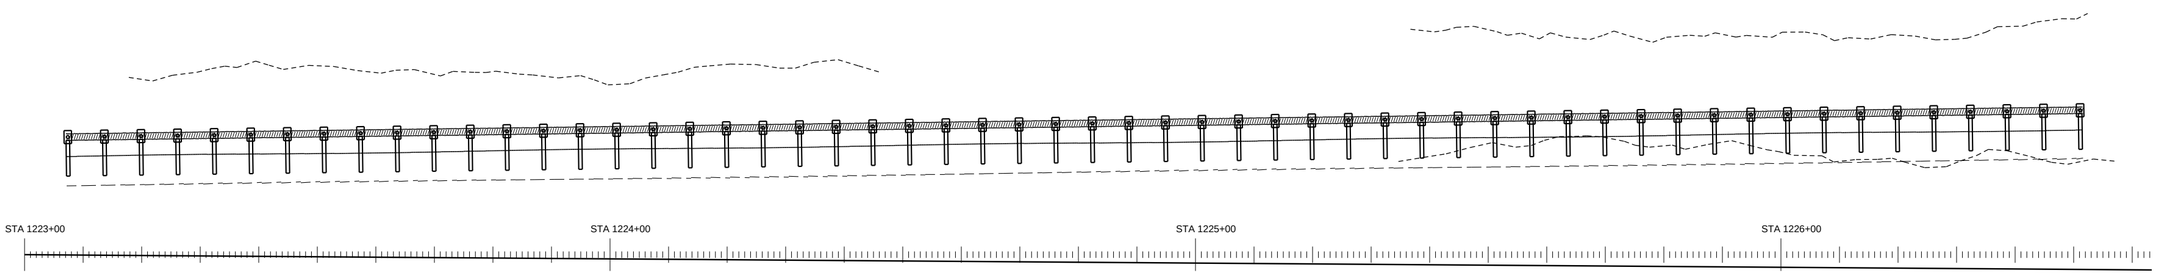


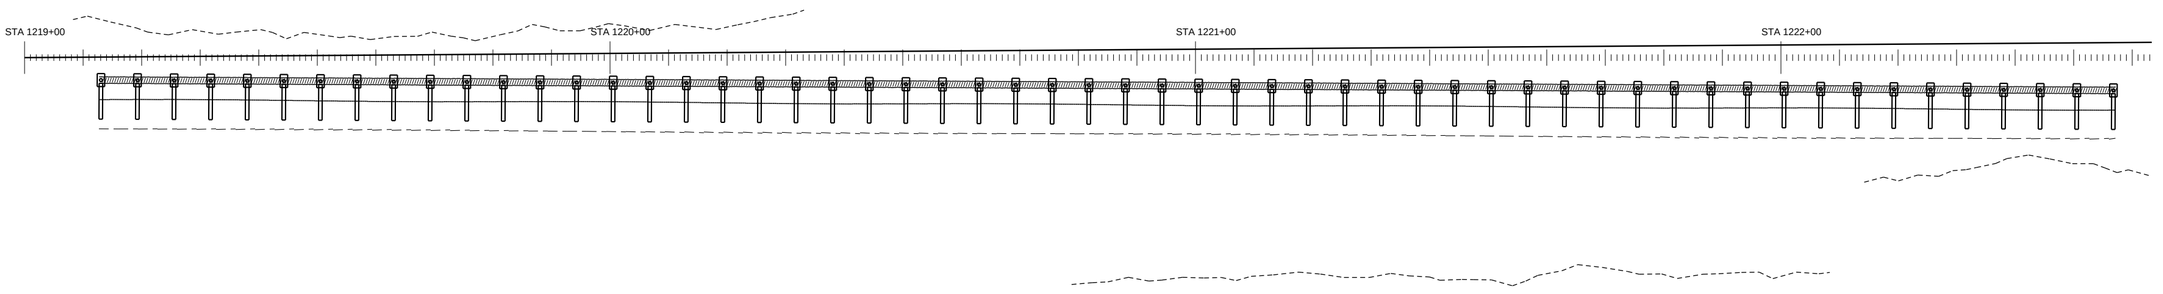


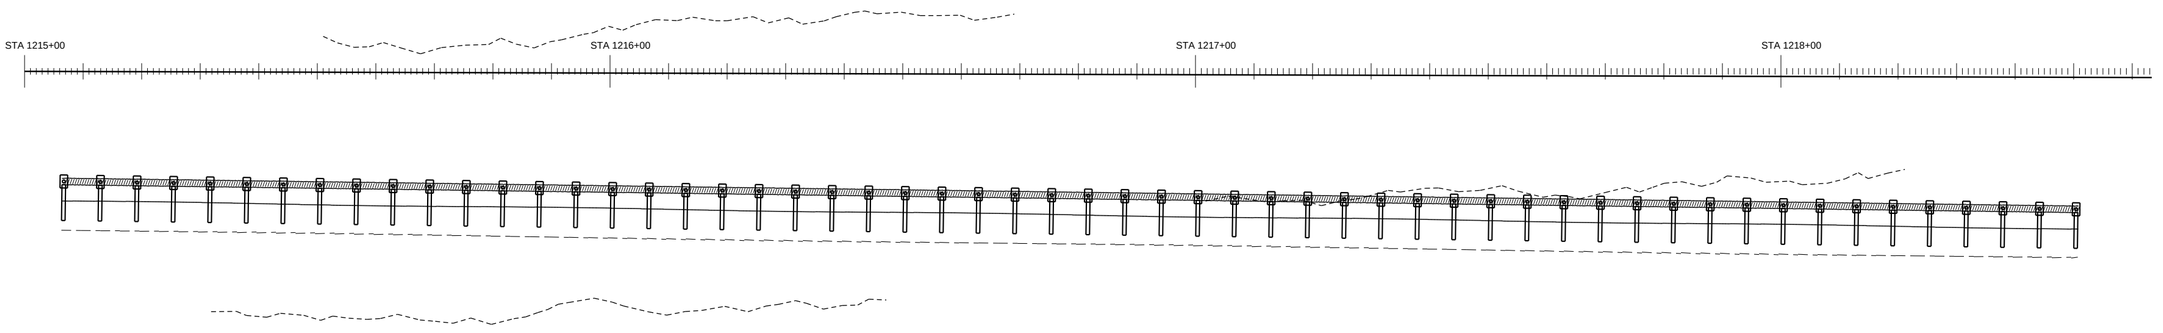


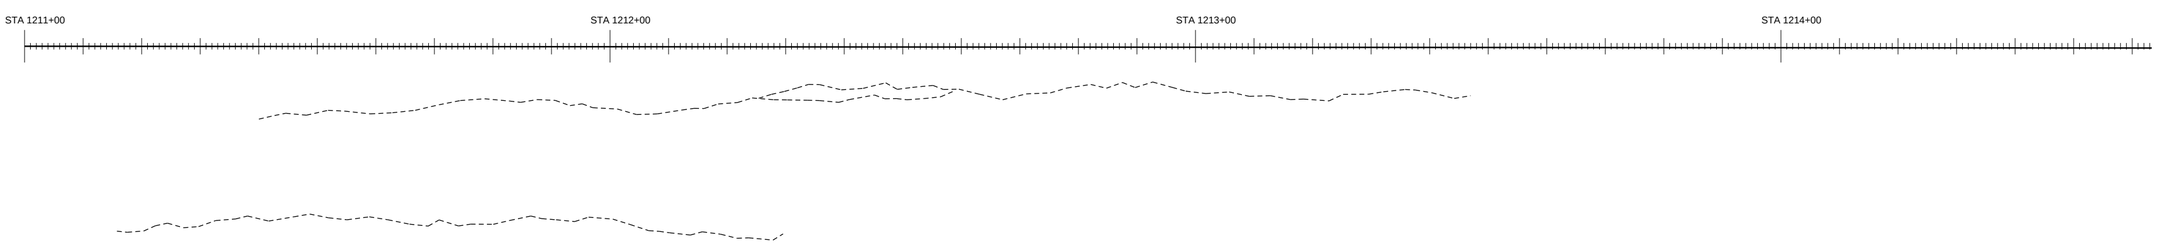


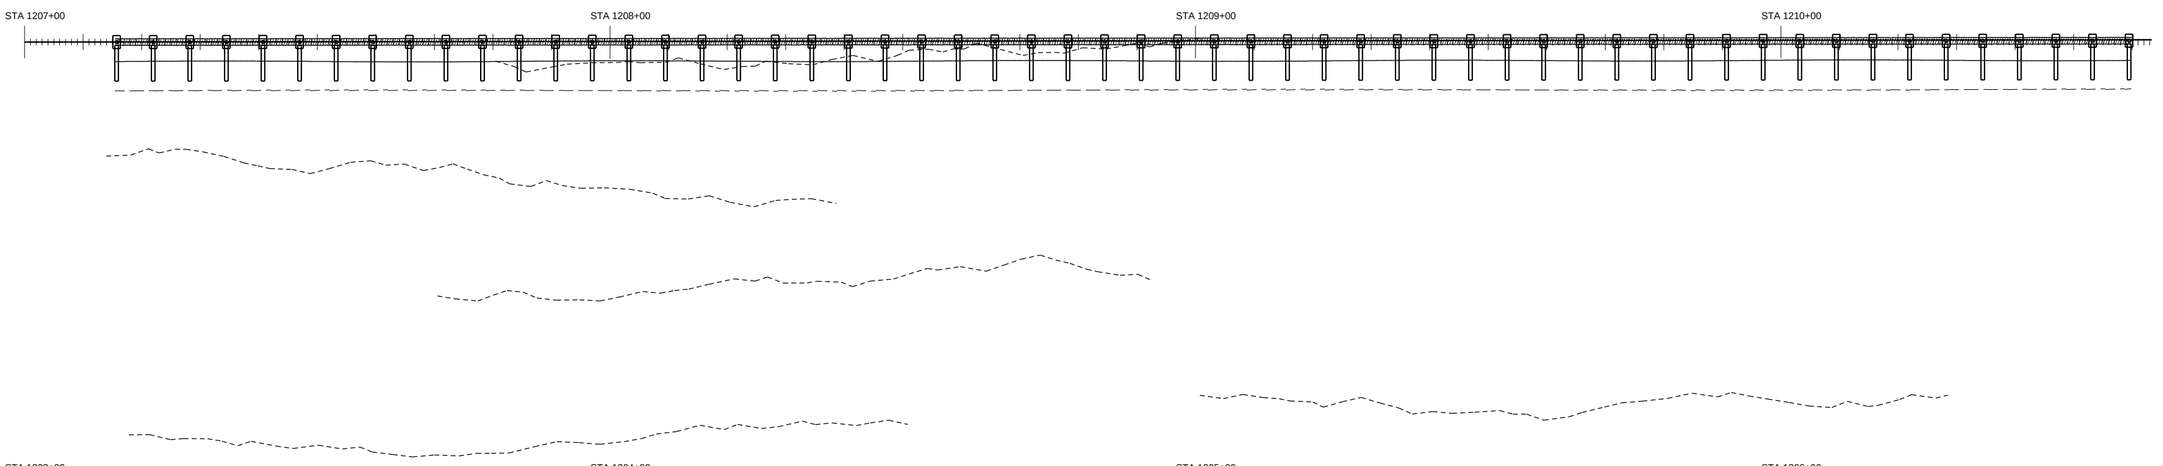


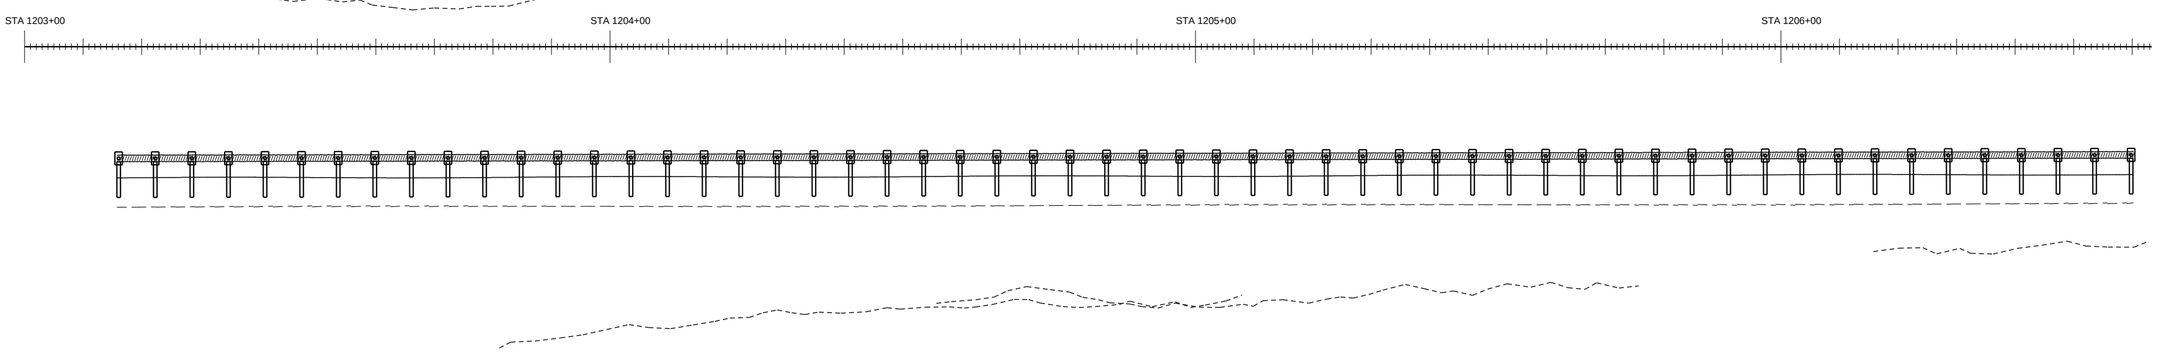


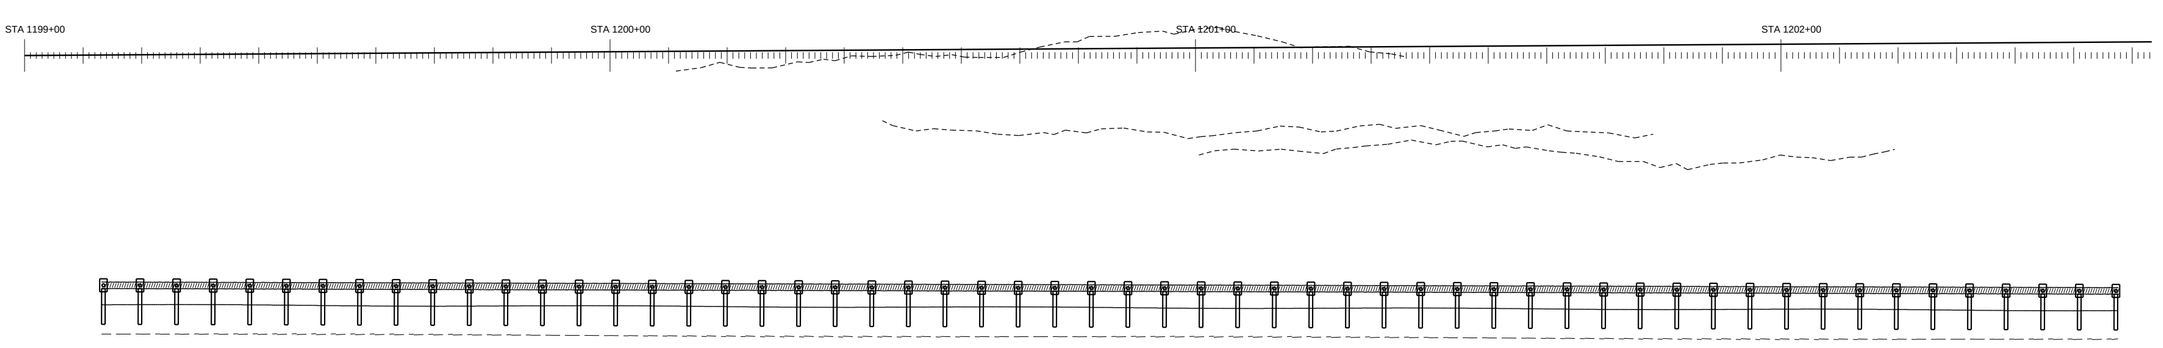


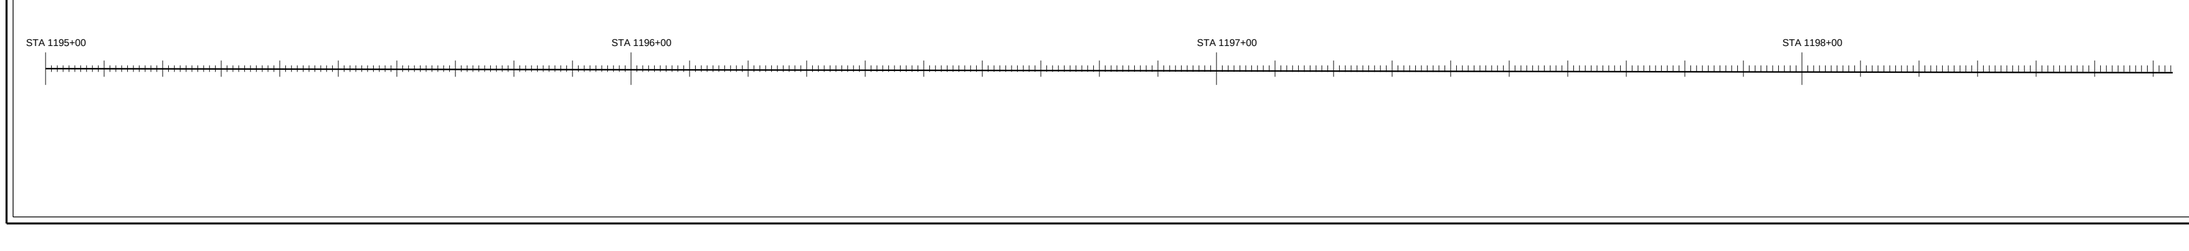


PAY ITEM 536-1-1 GUARDRAIL ROADWAY (TL-3)

PAY ITEM 536-85-24 END TREATMENT

GUARANTEED FENCE CORP

FIN. PROJ. ID 441234-1-52-01

SHEET 74 OF 120

SHEET NO. 174

ROADWAY PLAN SCALE: 1" = 20'

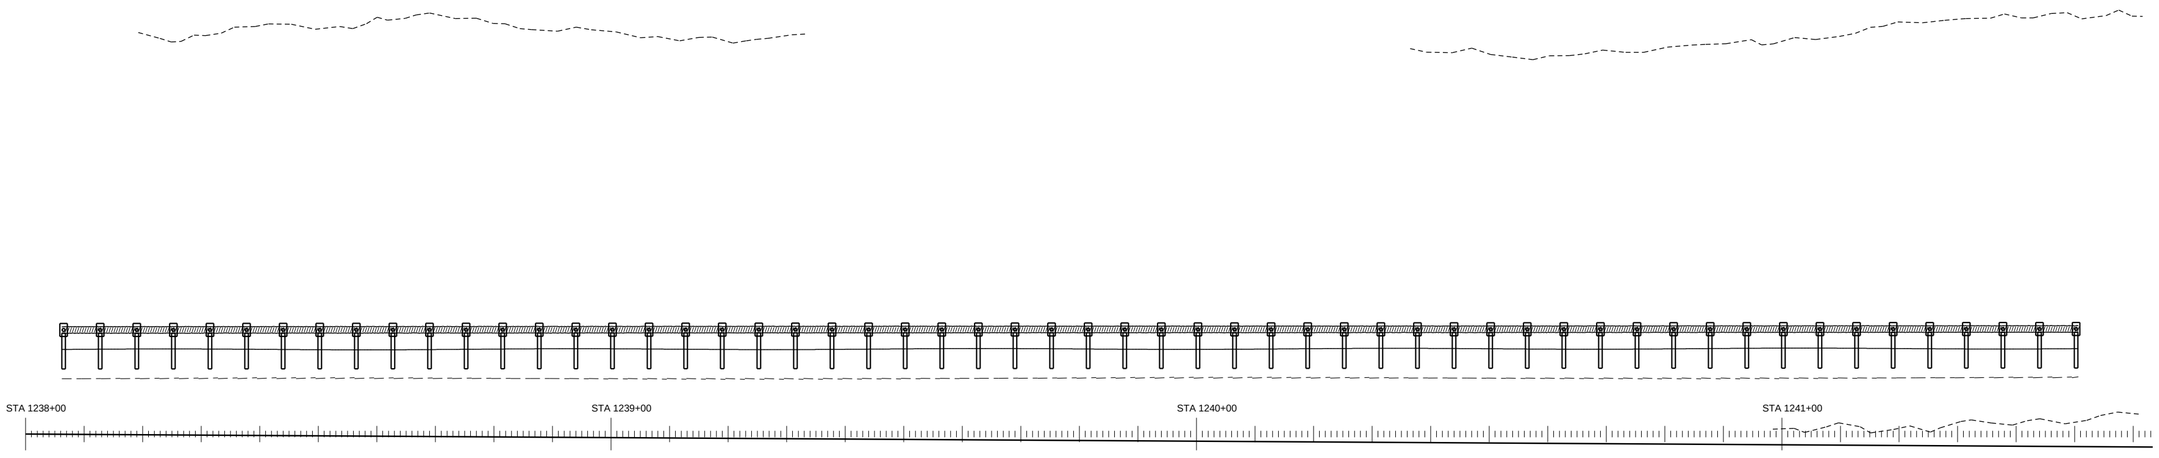


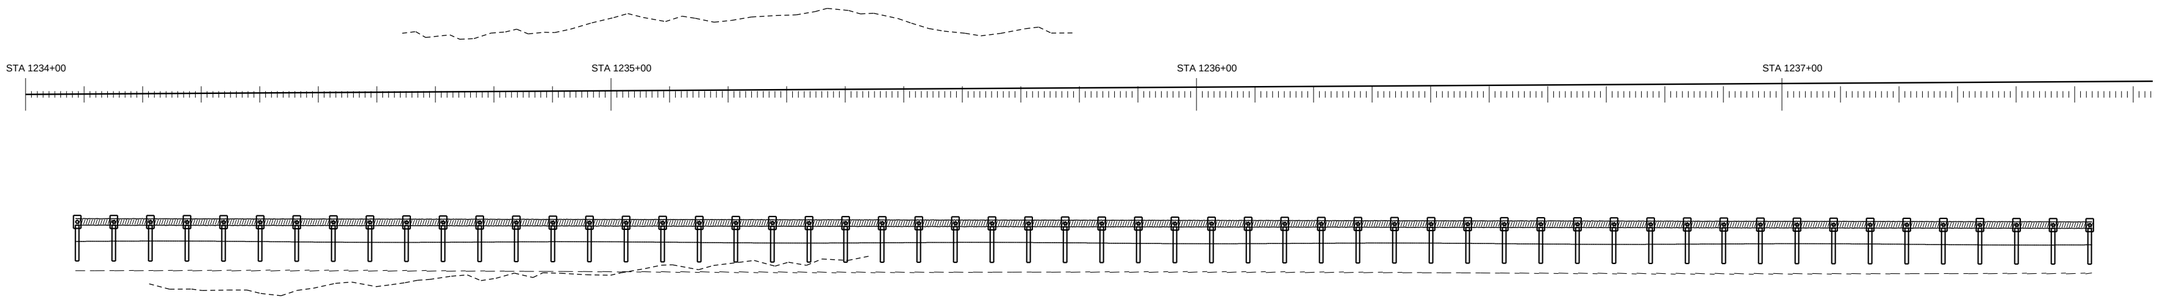


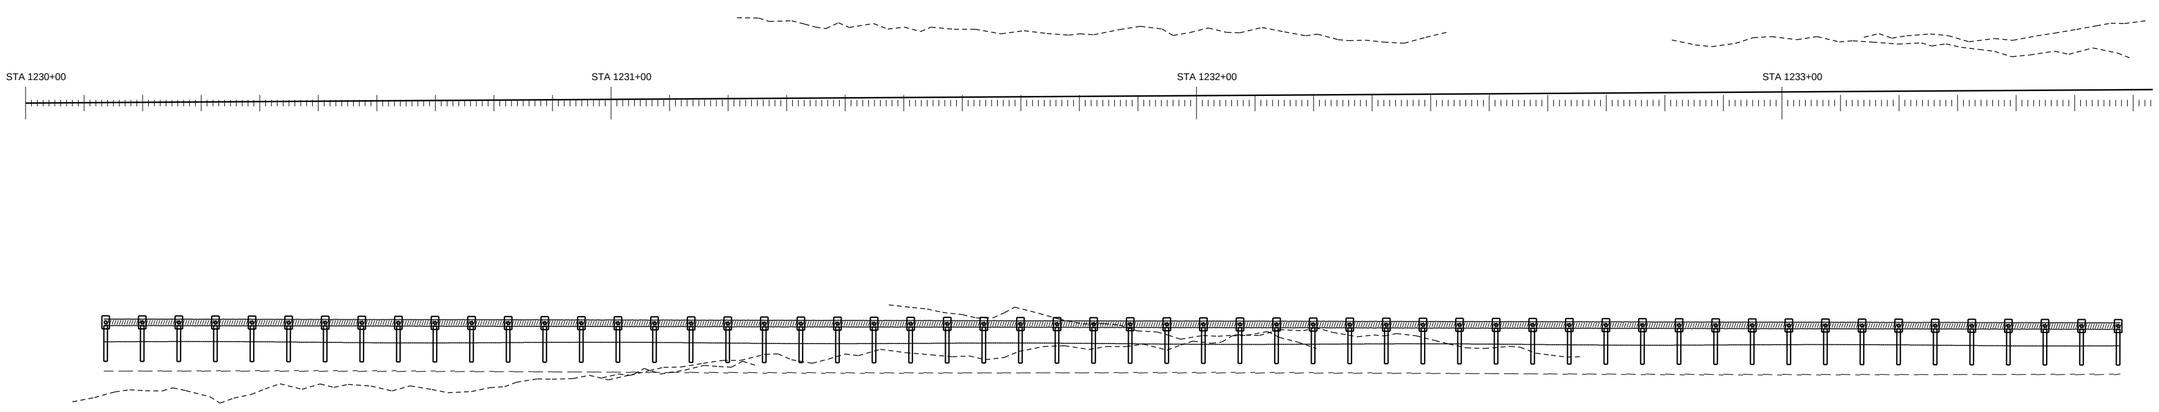


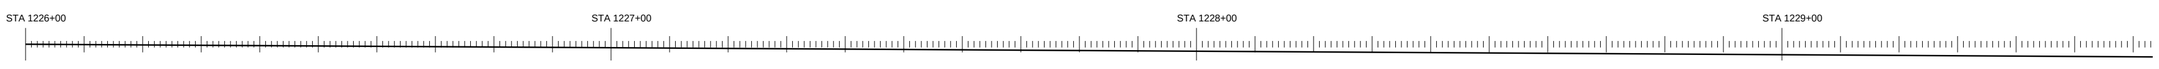


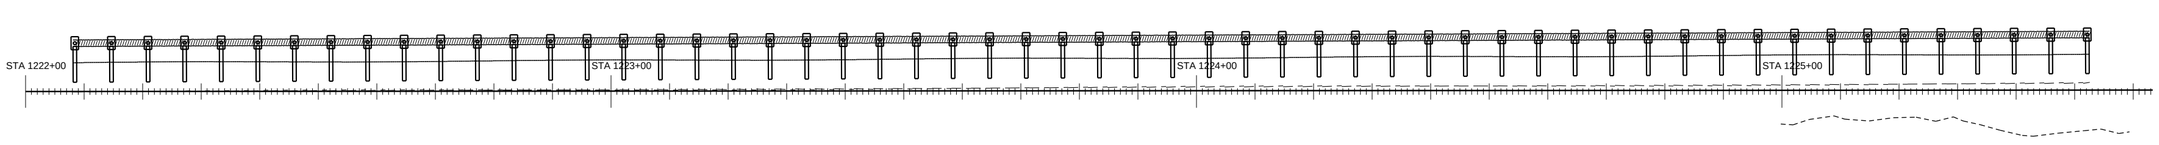


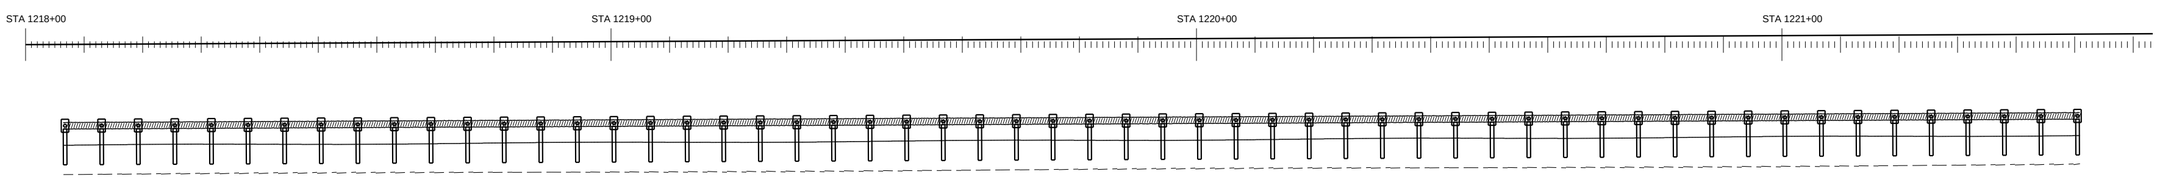


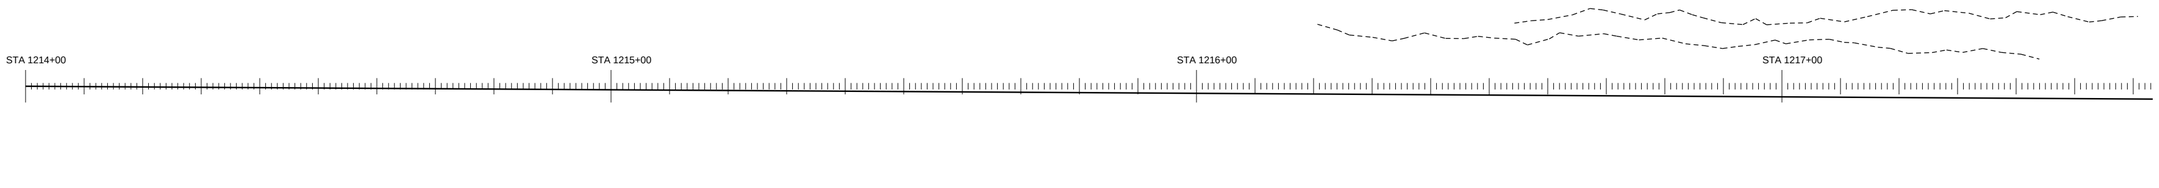


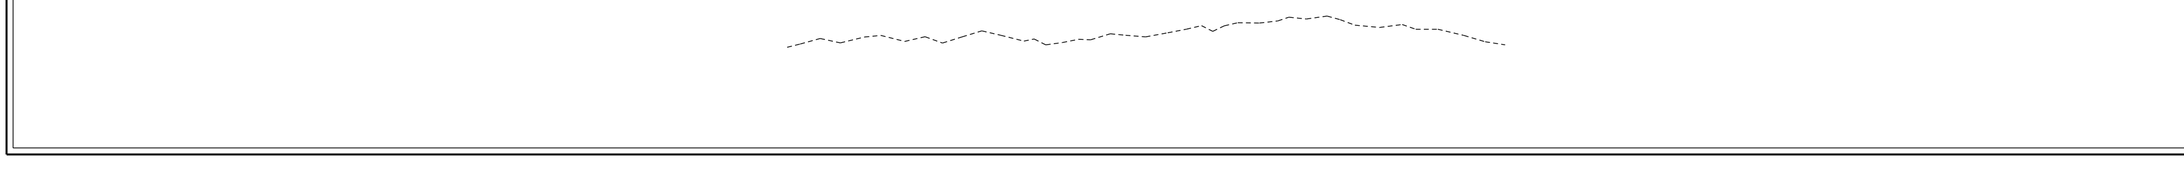


PAY ITEM 536-1-1 GUARDRAIL ROADWAY (TL-3)

PAY ITEM 536-85-24 END TREATMENT

GUARANTEED FENCE CORP

FIN. PROJ. ID 441234-1-52-01

SHEET 75 OF 120

SHEET NO. 175

ROADWAY PLAN SCALE: 1" = 20'




PAY ITEM 536-1-1 GUARDRAIL ROADWAY (TL-3)

PAY ITEM 536-85-24 END TREATMENT

GUARANTEED FENCE CORP

FIN. PROJ. ID 441234-1-52-01

SHEET 76 OF 120

SHEET NO. 176

ROADWAY PLAN SCALE: 1" = 20'

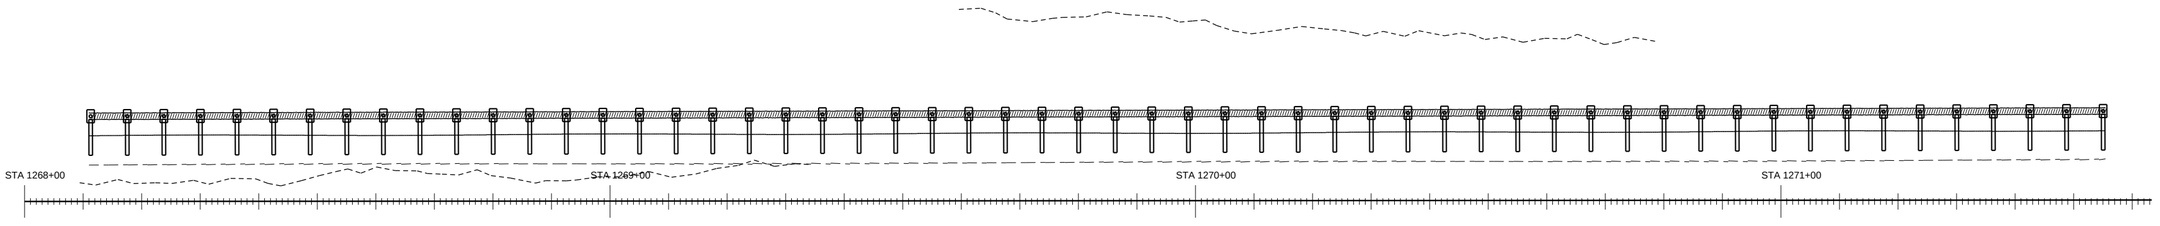


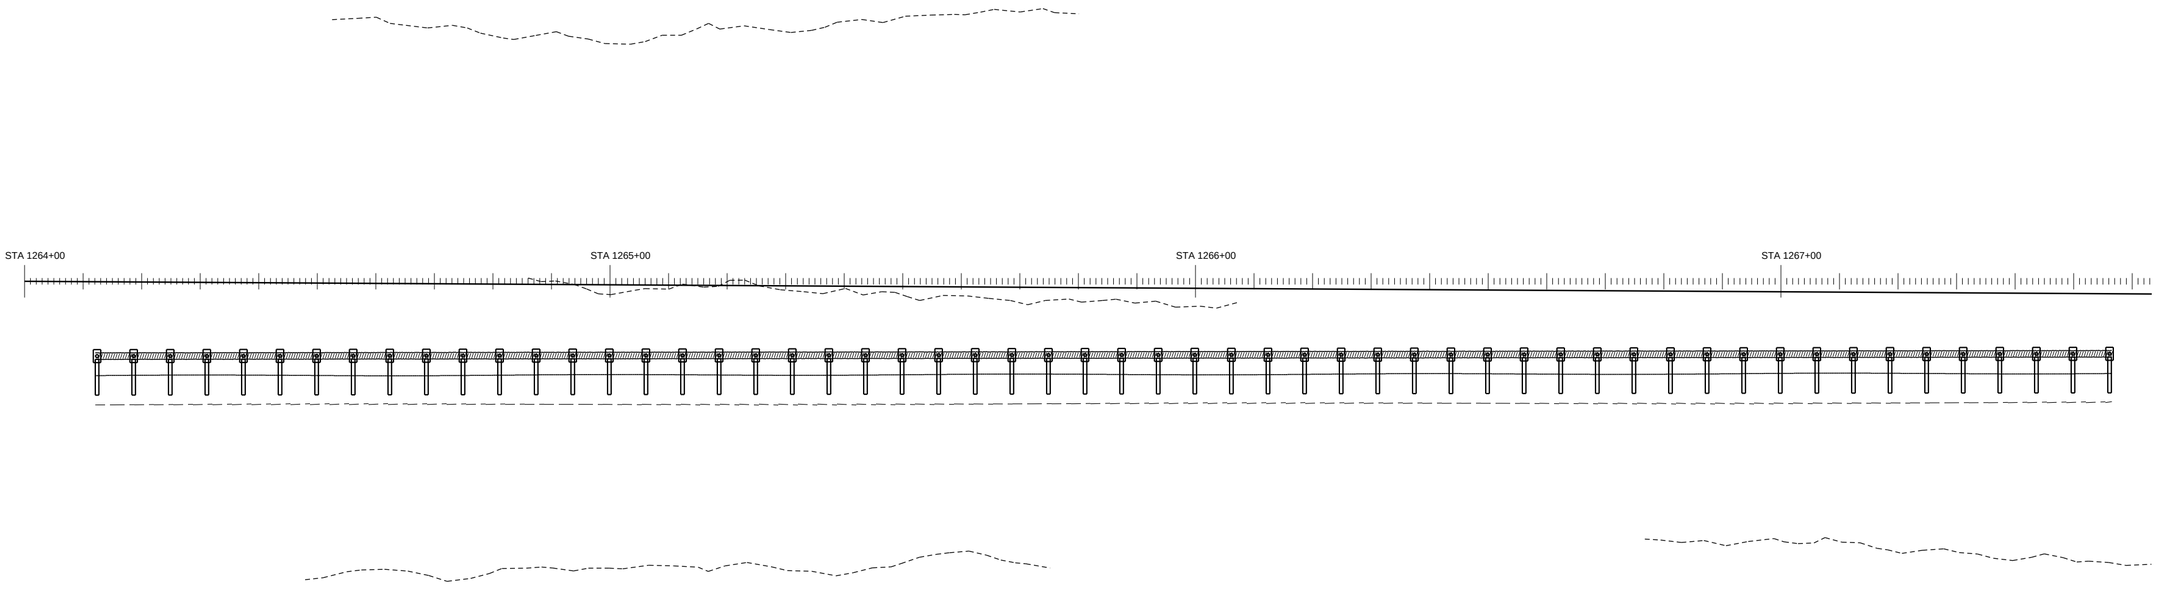


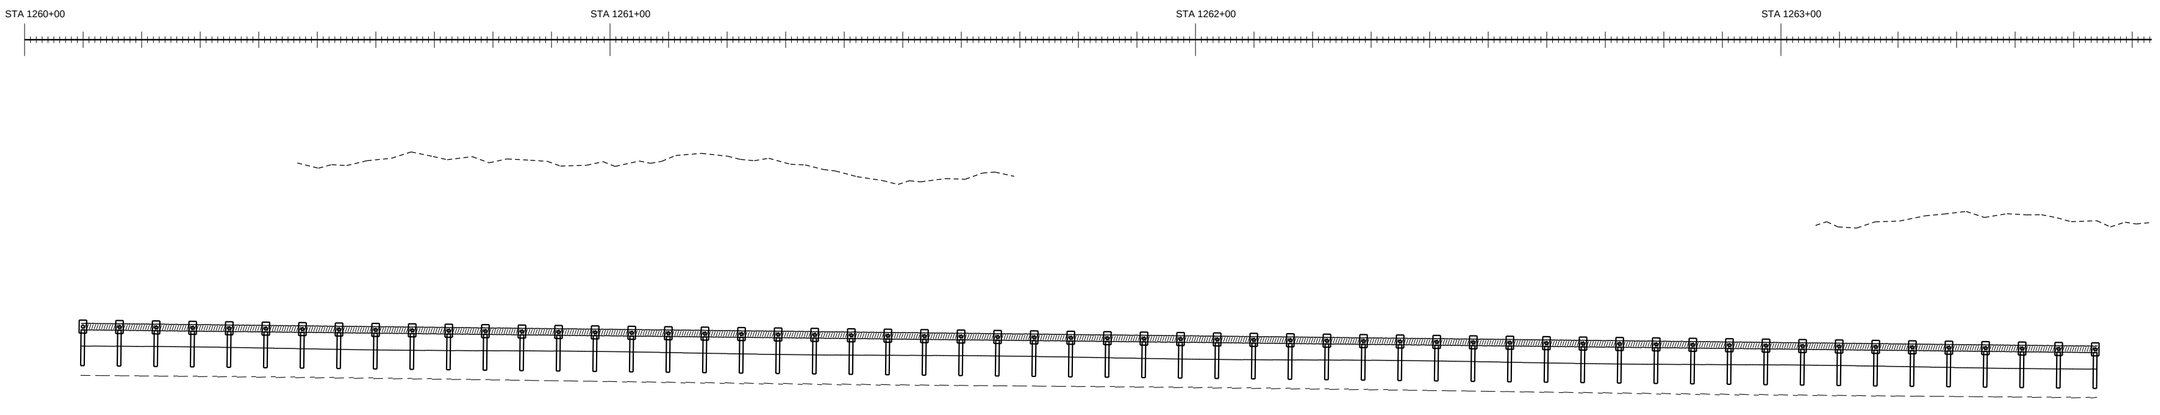


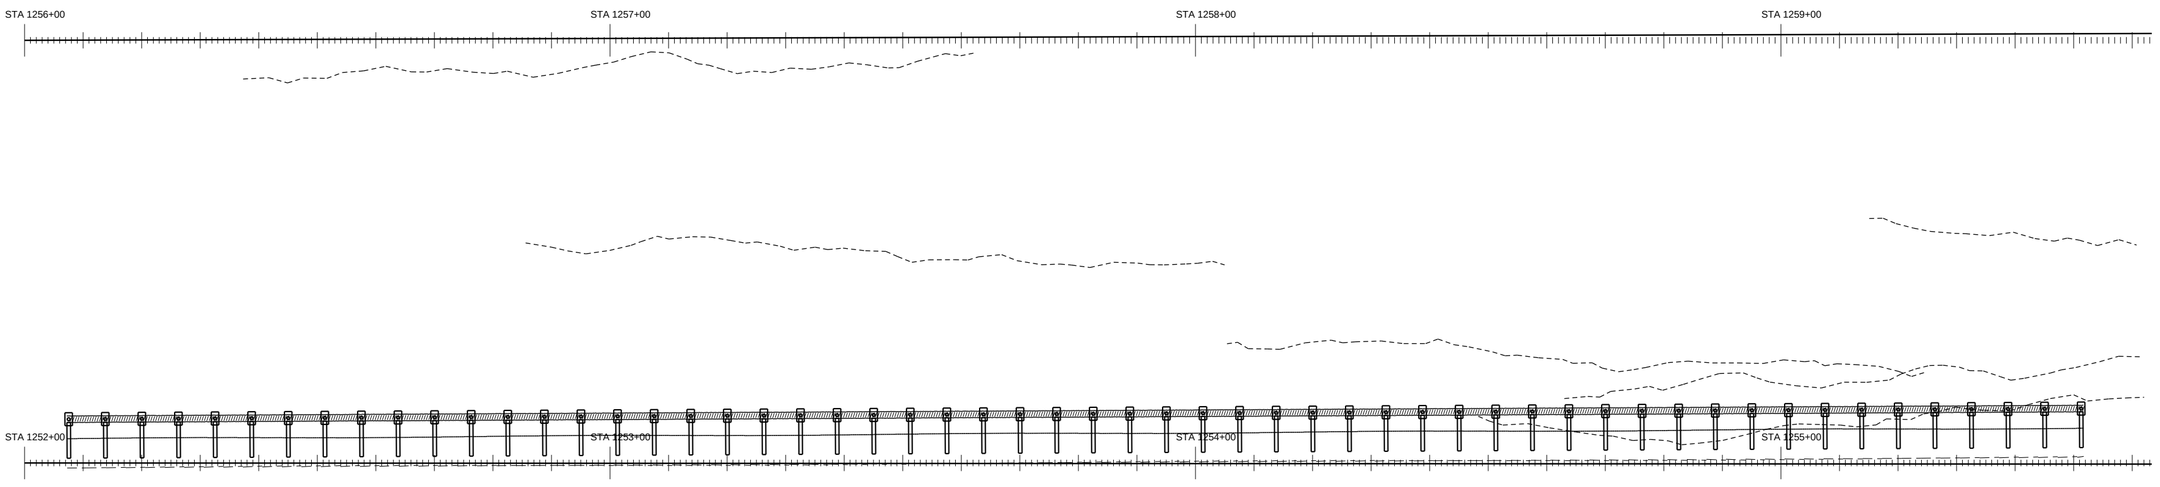


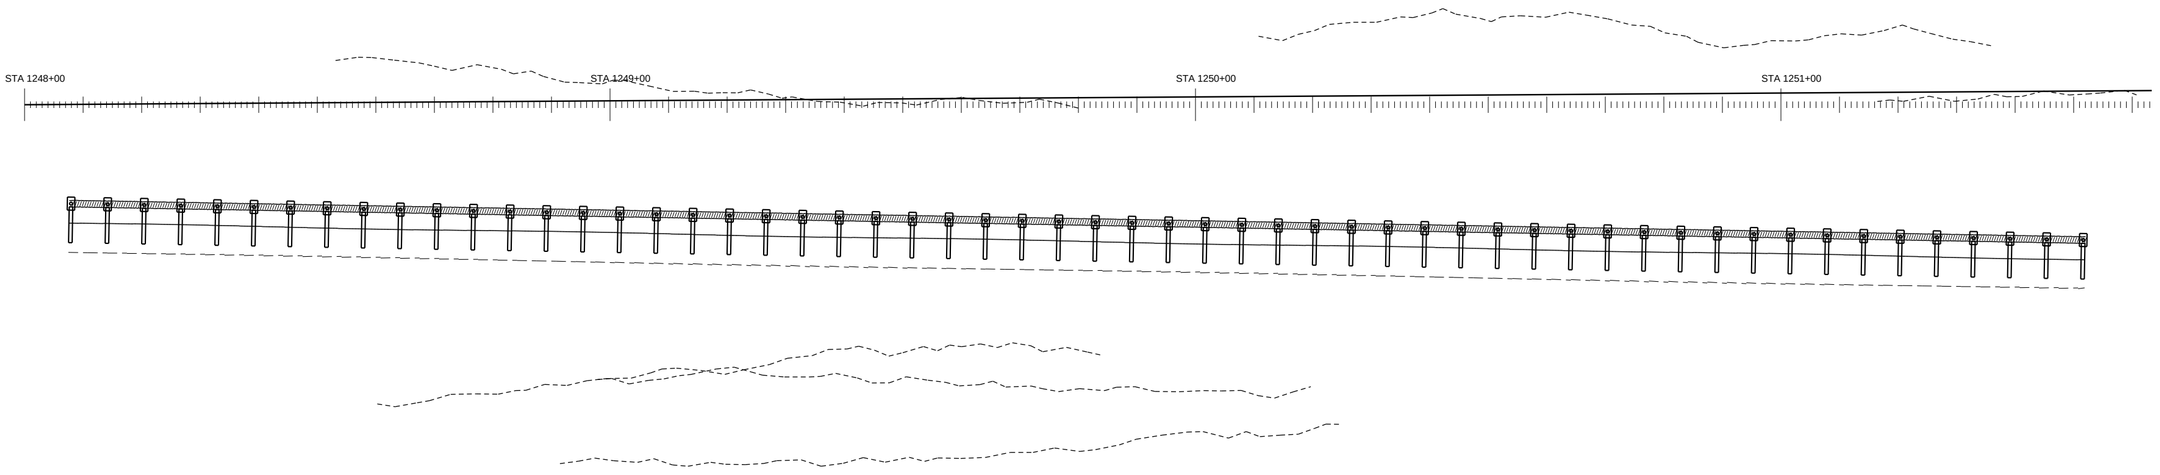


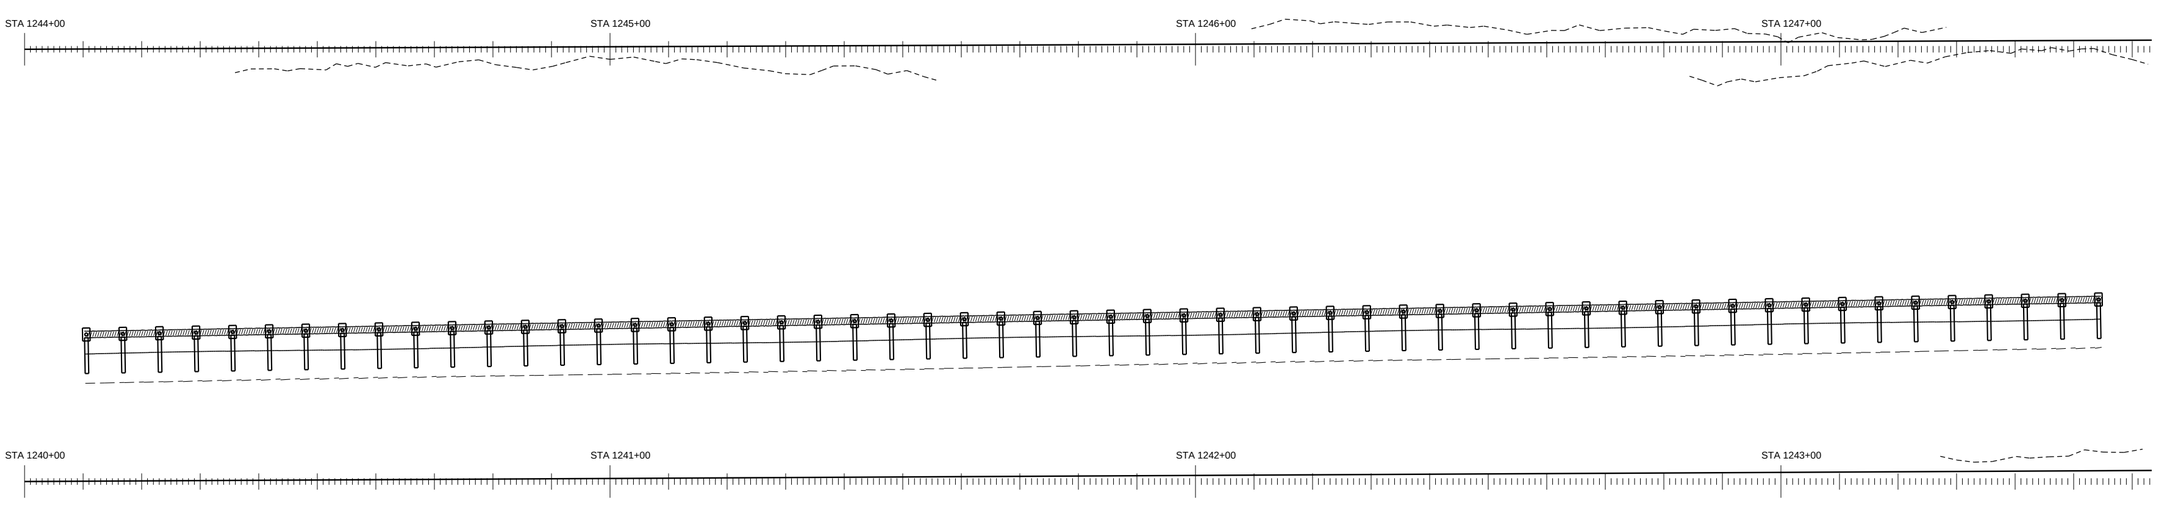


PAY ITEM 536-1-1 GUARDRAIL ROADWAY (TL-3)

PAY ITEM 536-85-24 END TREATMENT

GUARANTEED FENCE CORP

FIN. PROJ. ID 441234-1-52-01

SHEET 77 OF 120

SHEET NO. 177

ROADWAY PLAN SCALE: 1" = 20'

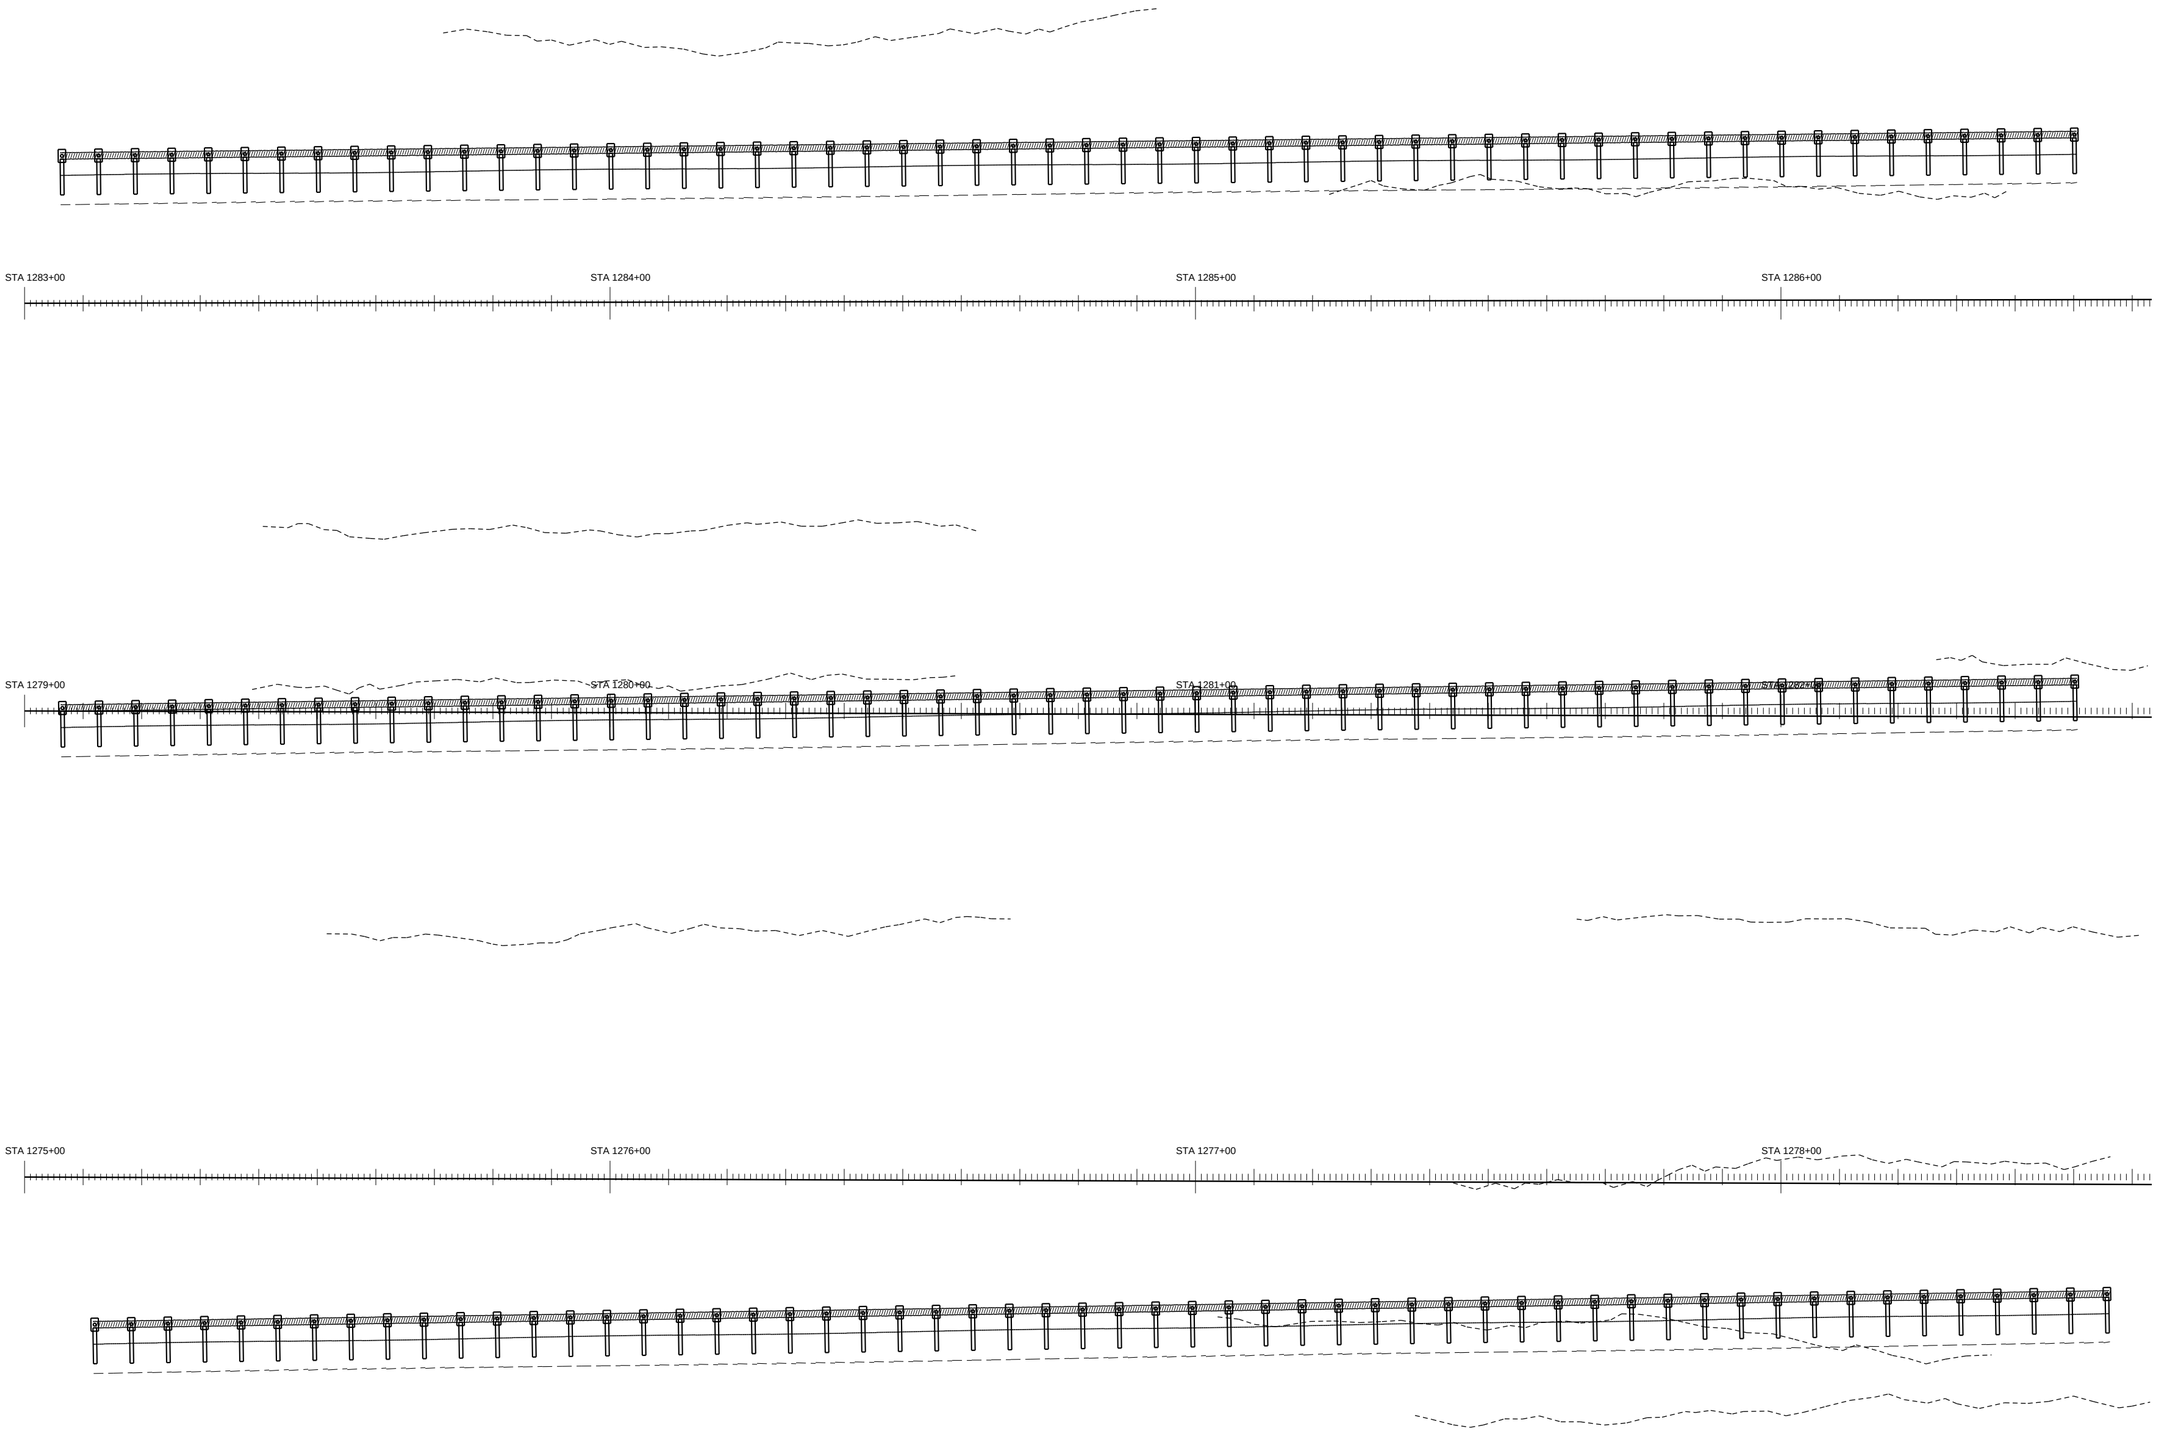


PAY ITEM 536-1-1 GUARDRAIL ROADWAY (TL-3)

PAY ITEM 536-85-24 END TREATMENT

GUARANTEED FENCE CORP

FIN. PROJ. ID 441234-1-52-01

SHEET 78 OF 120

SHEET NO. 178

ROADWAY PLAN SCALE: 1" = 20'

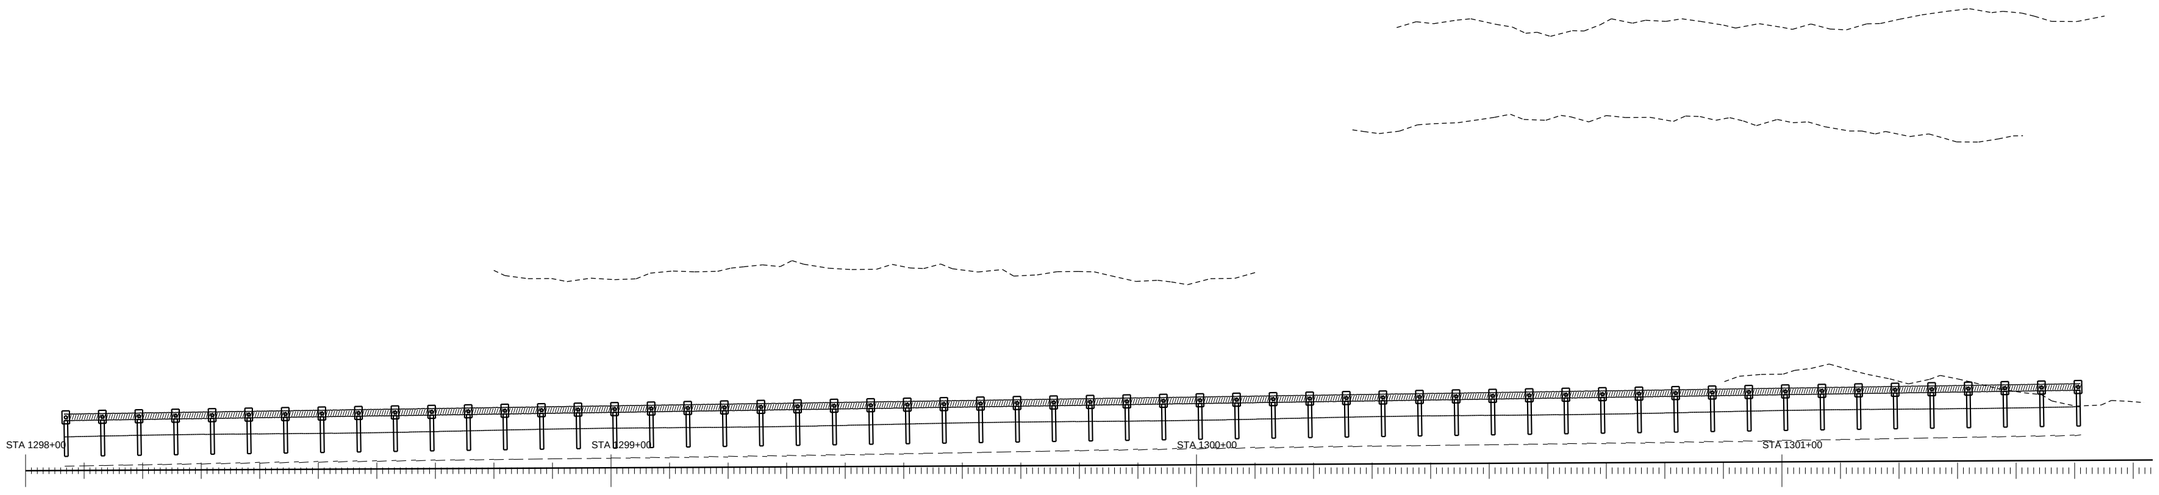


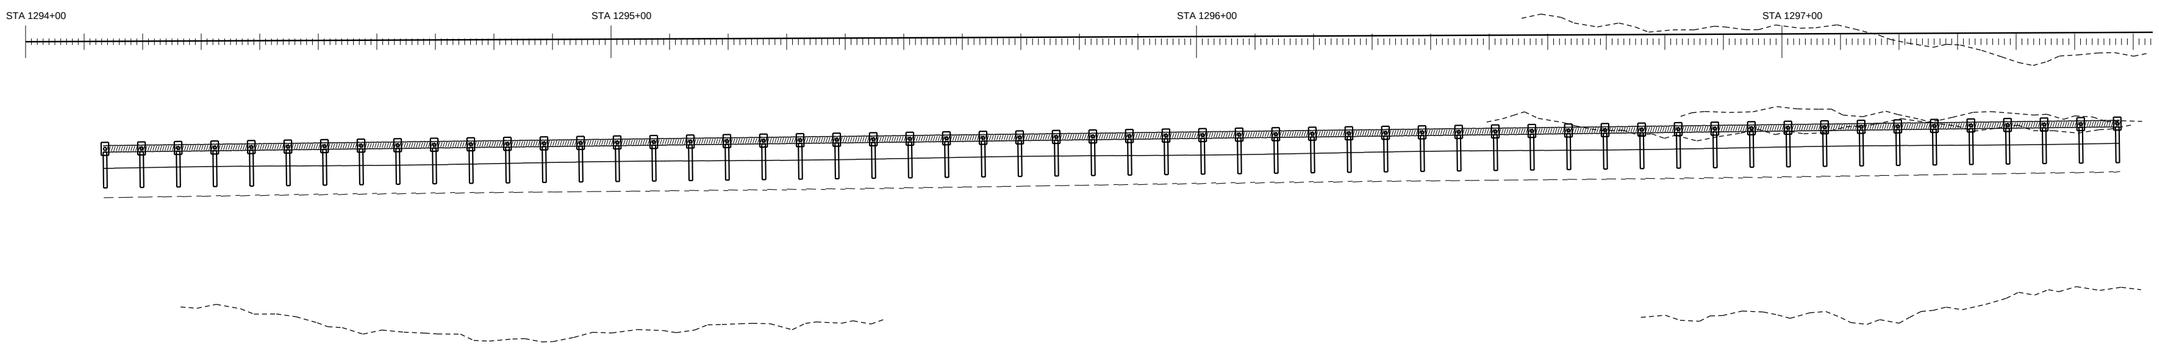


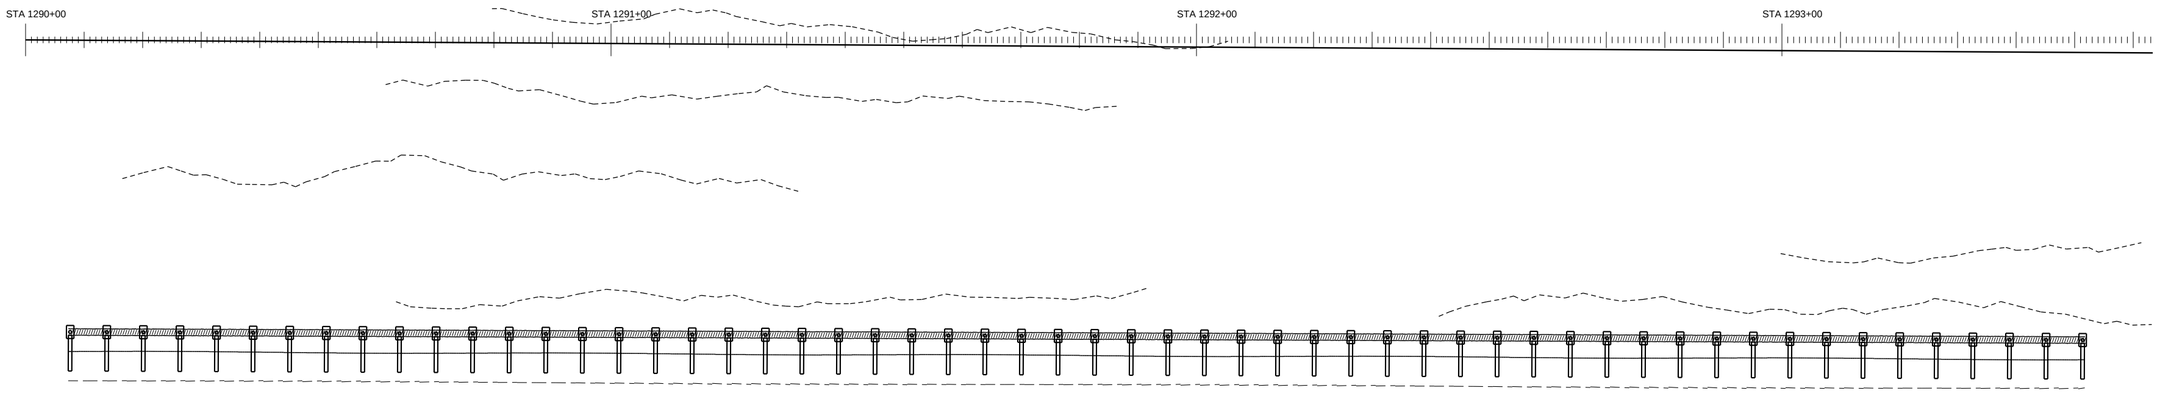


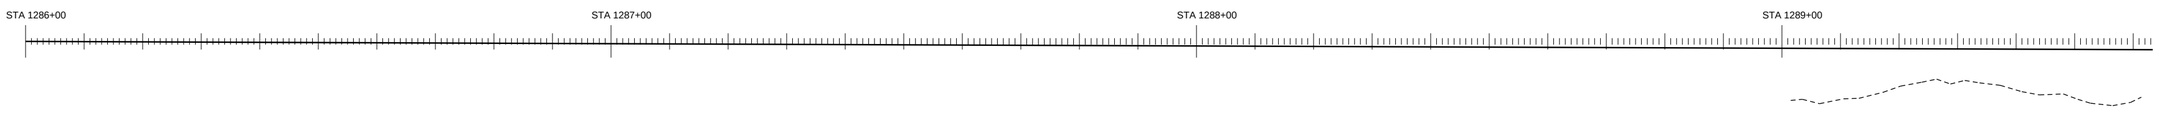


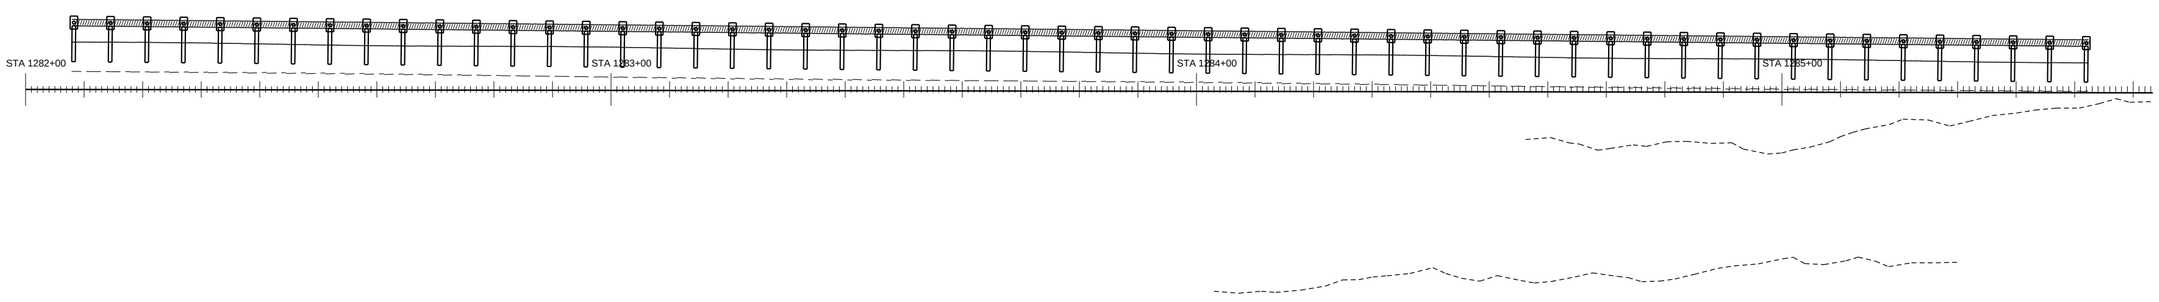


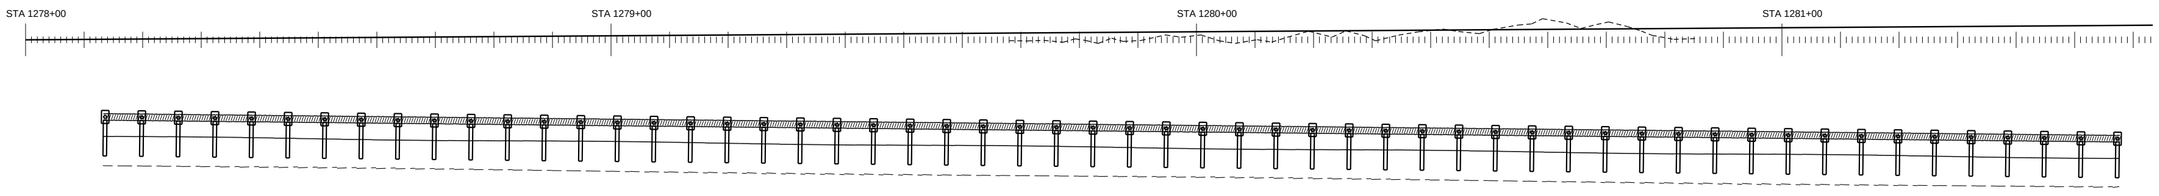


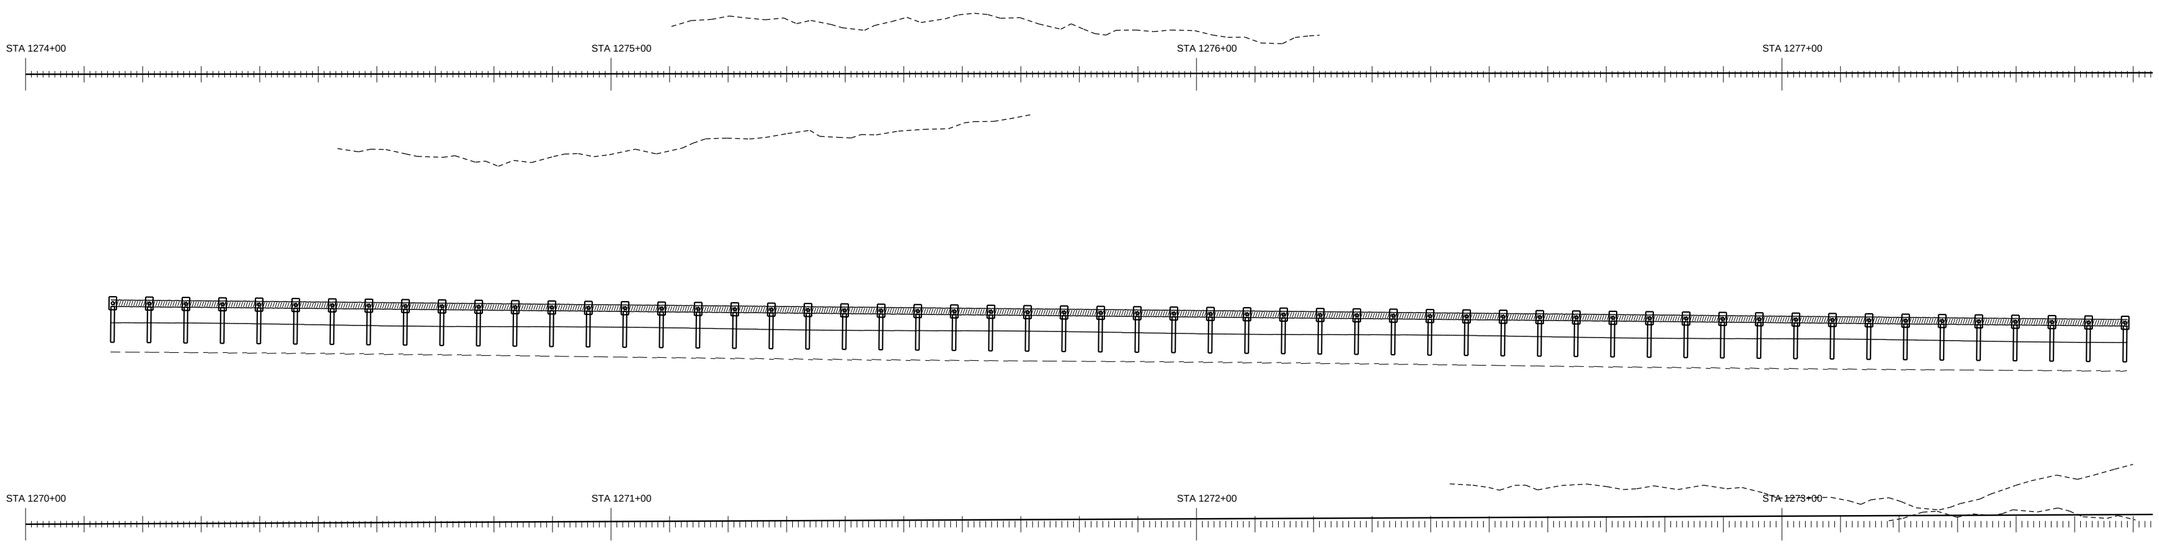


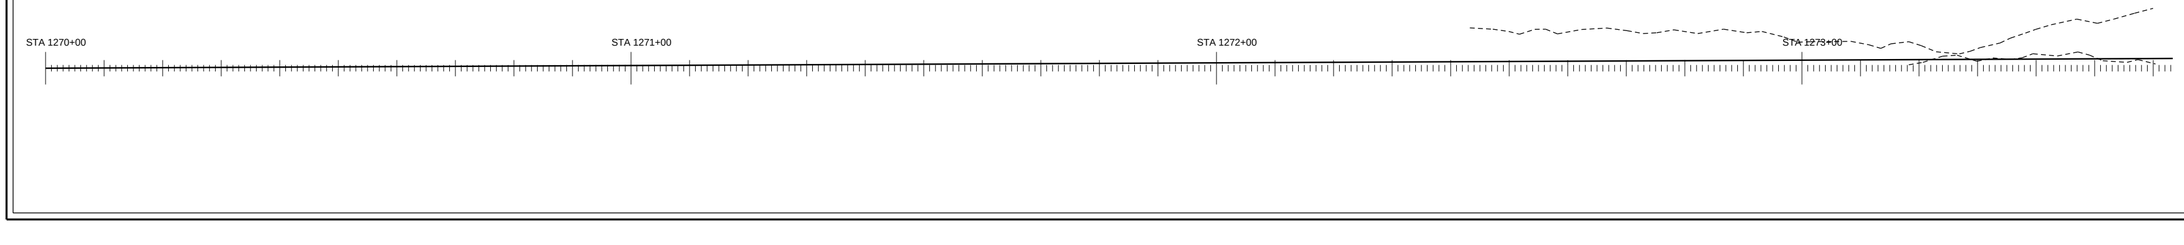


PAY ITEM 536-1-1 GUARDRAIL ROADWAY (T-3)

PAY ITEM 536-85-24 END TREATMENT

GUARANTEED FENCE CORP

FIN. PROJ. ID 441234-1-52-01

SHEET 79 OF 120

SHEET NO. 179

ROADWAY PLAN SCALE: 1" = 20'

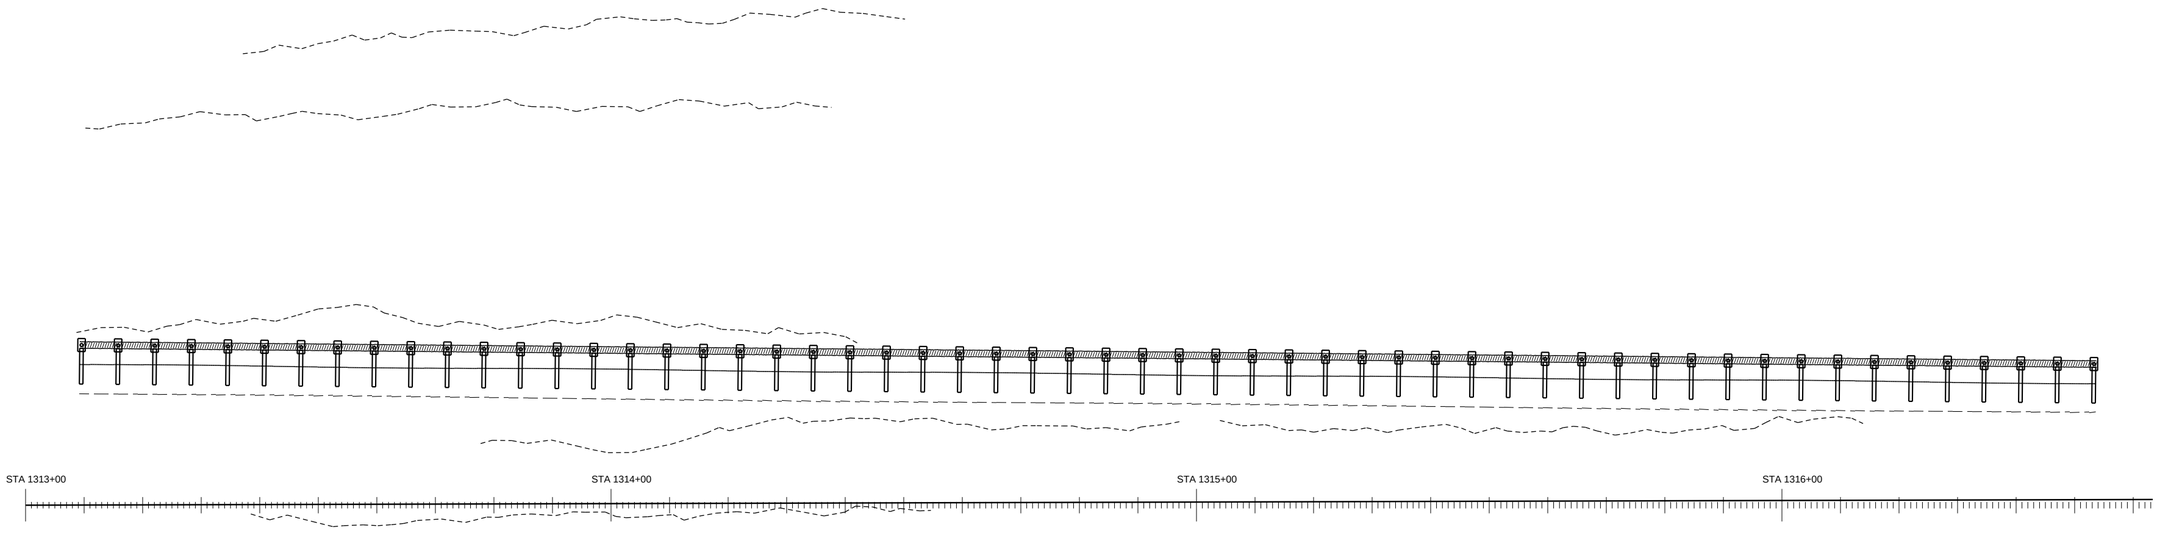


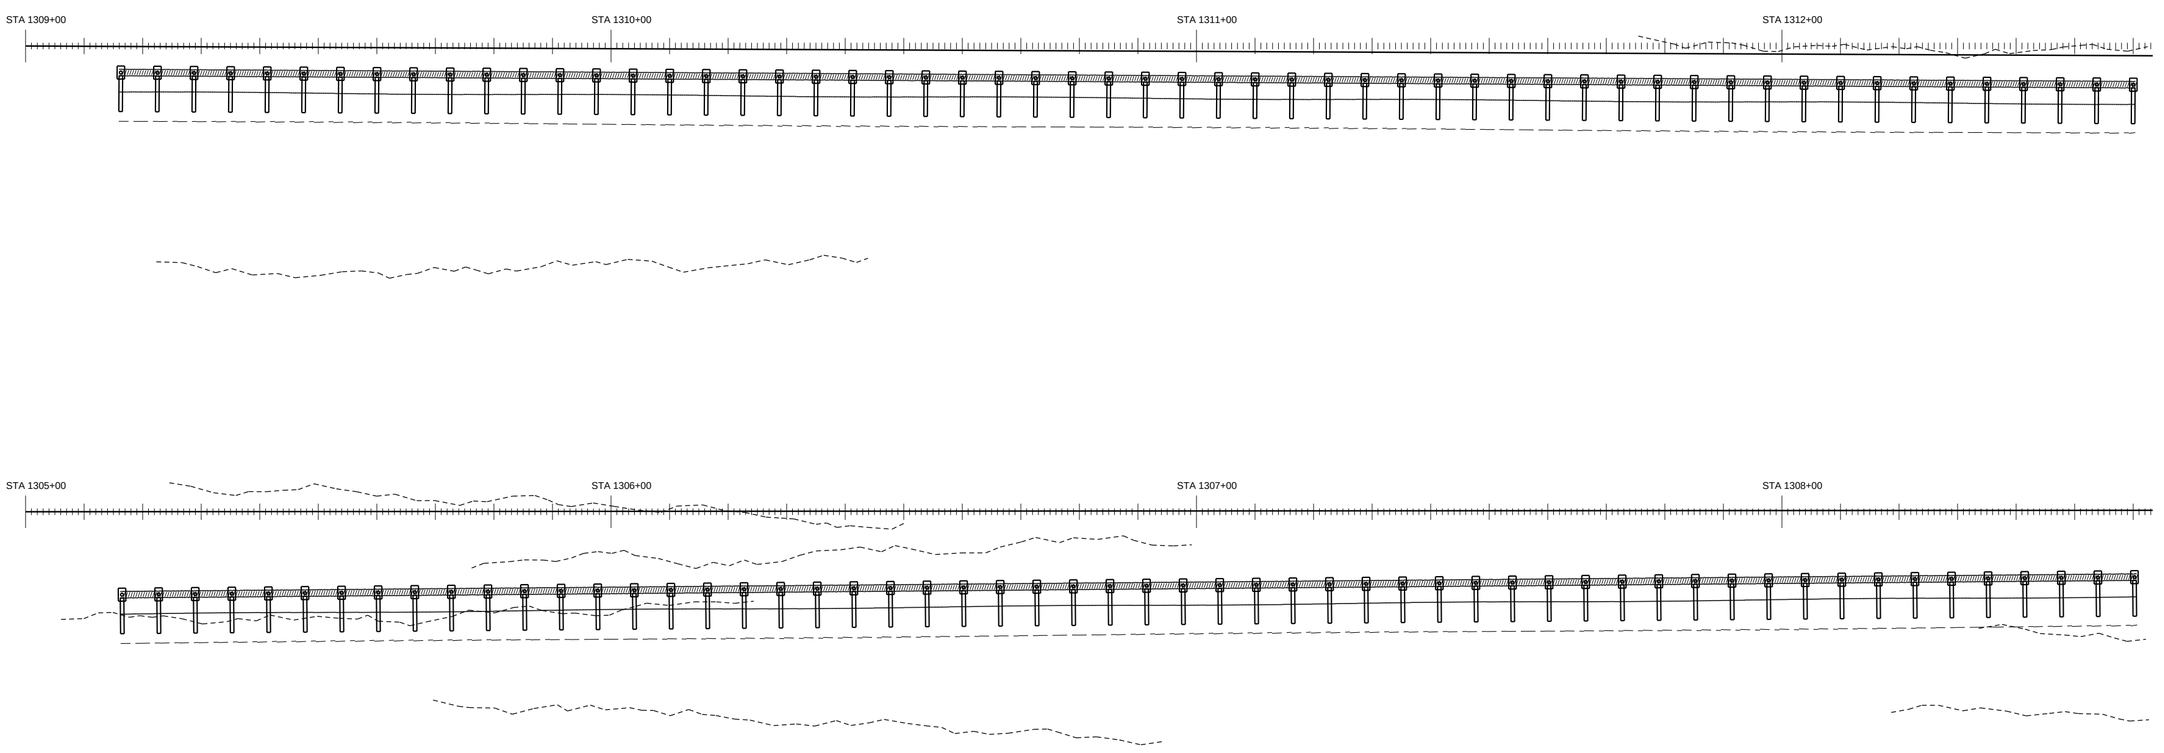


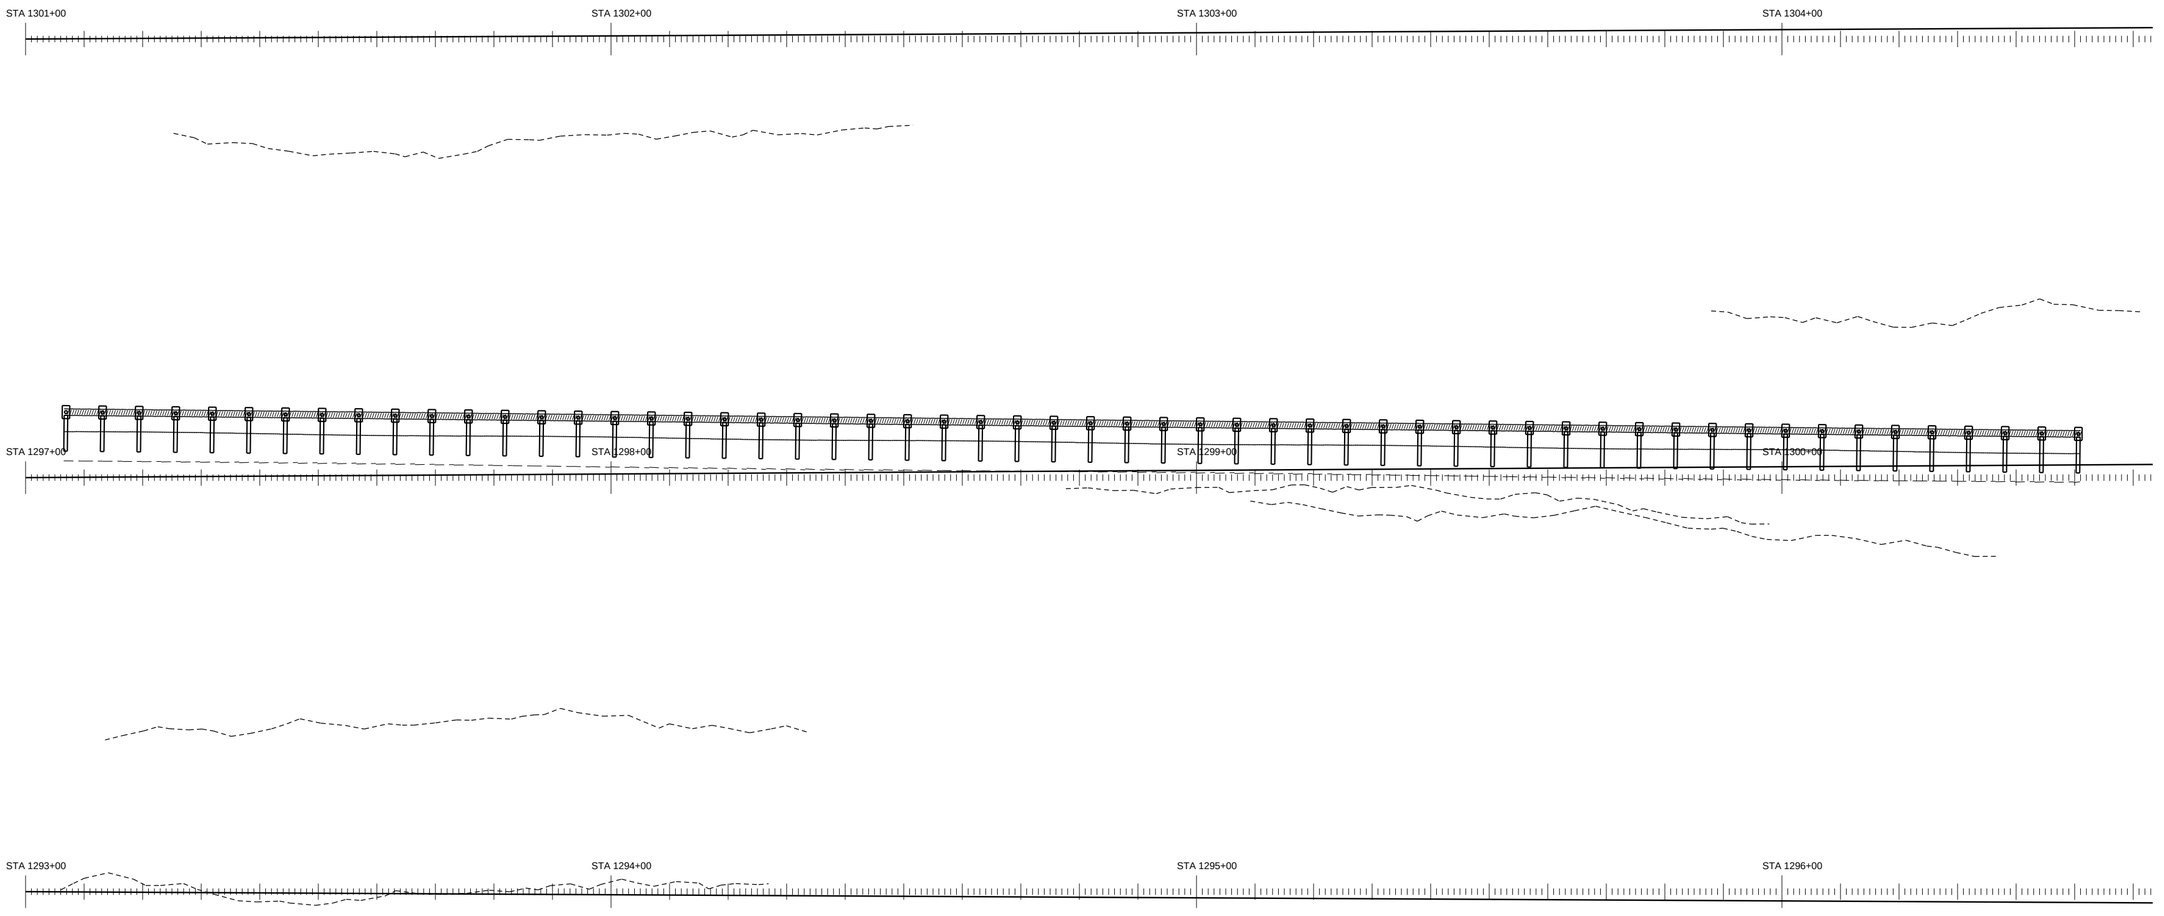





PAY ITEM 536-1-1 GUARDRAIL ROADWAY (TL-3)

PAY ITEM 536-85-24 END TREATMENT

GUARANTEED FENCE CORP

FIN. PROJ. ID 441234-1-52-01

SHEET 80 OF 120

SHEET NO. 180

ROADWAY PLAN SCALE: 1" = 20'

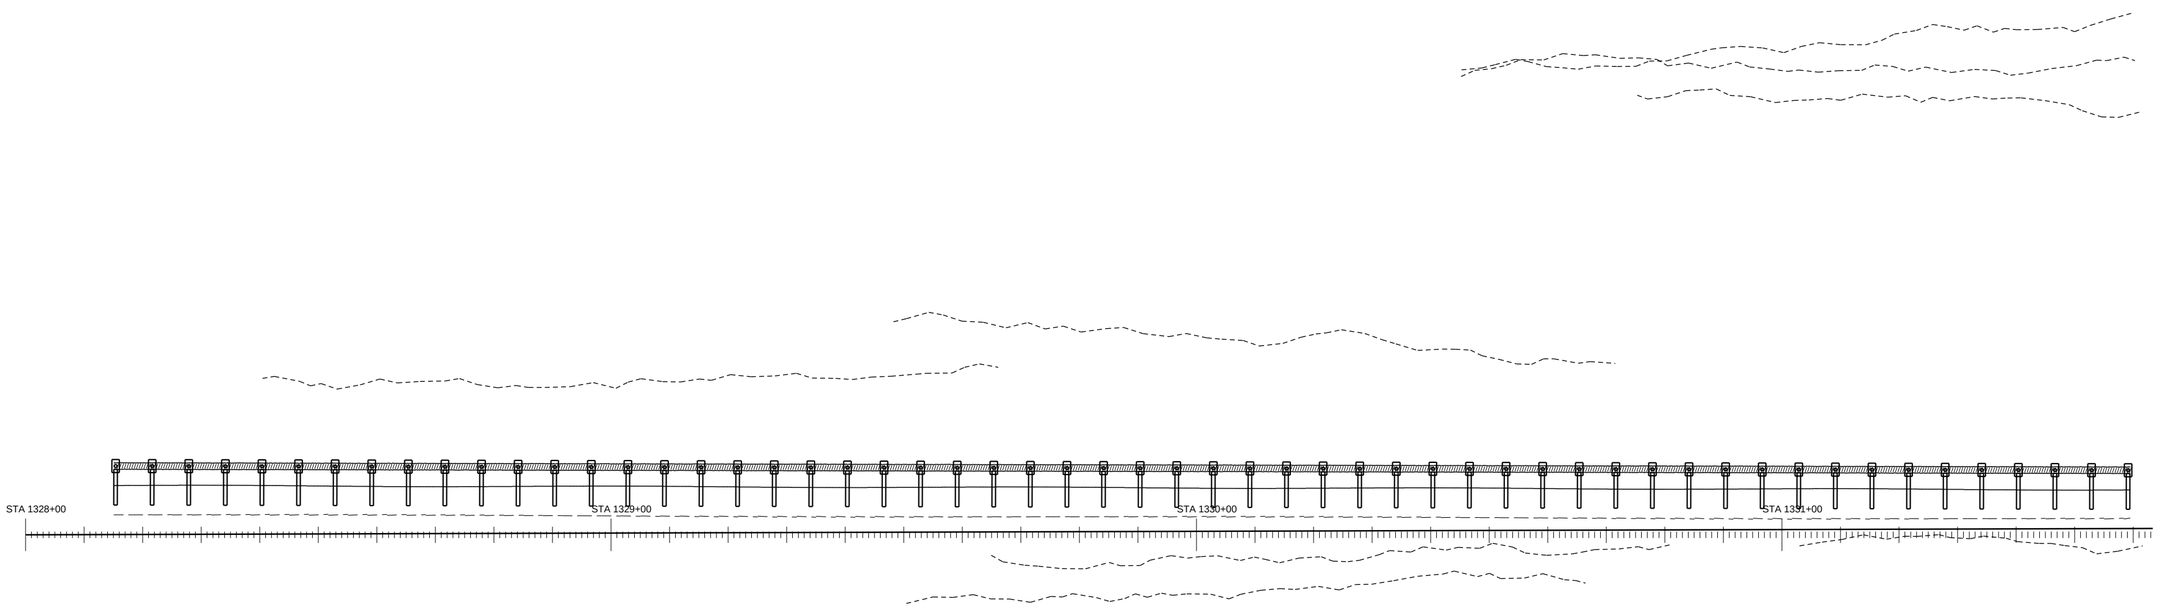

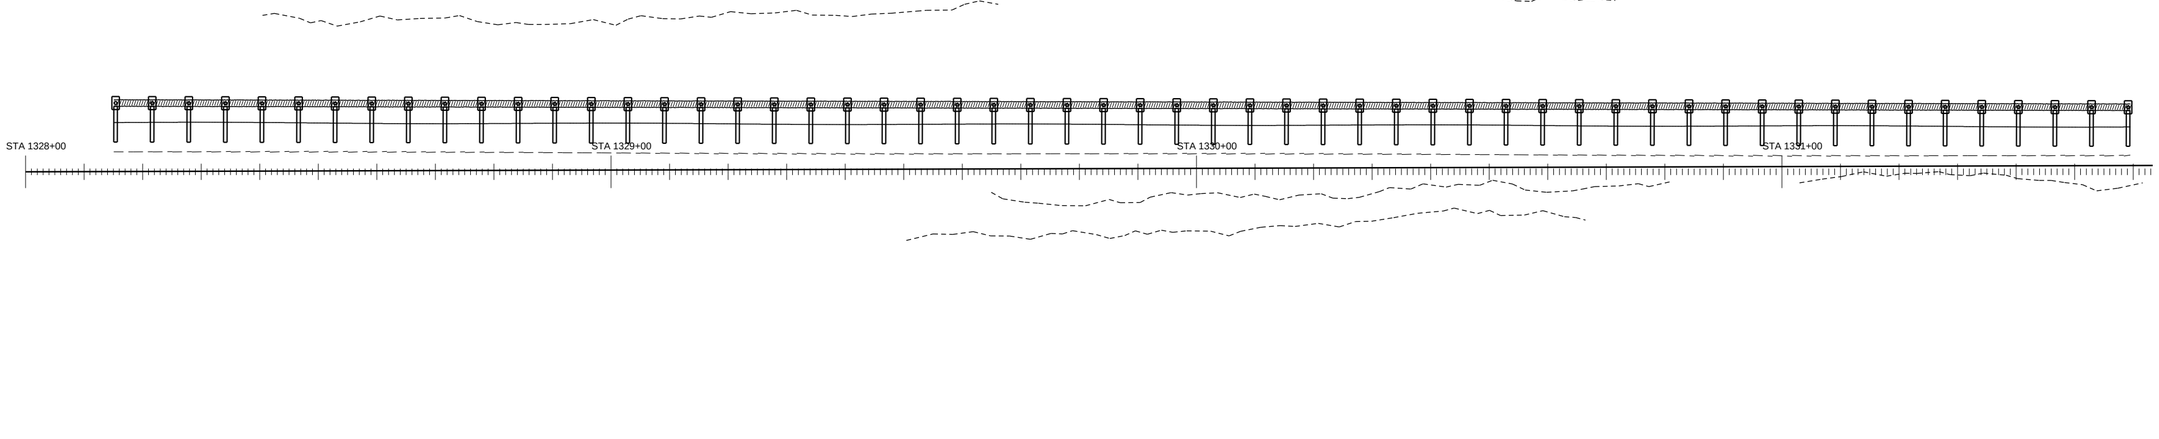


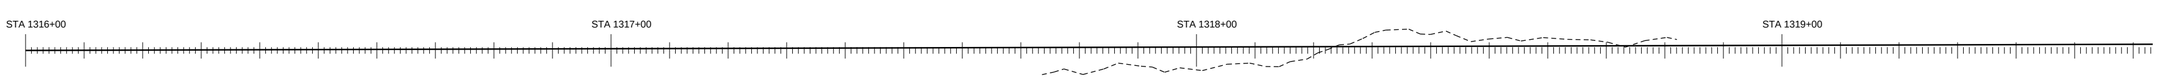


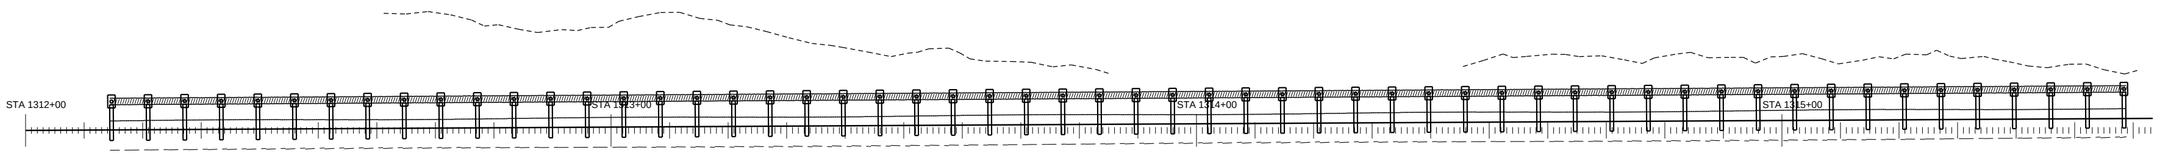


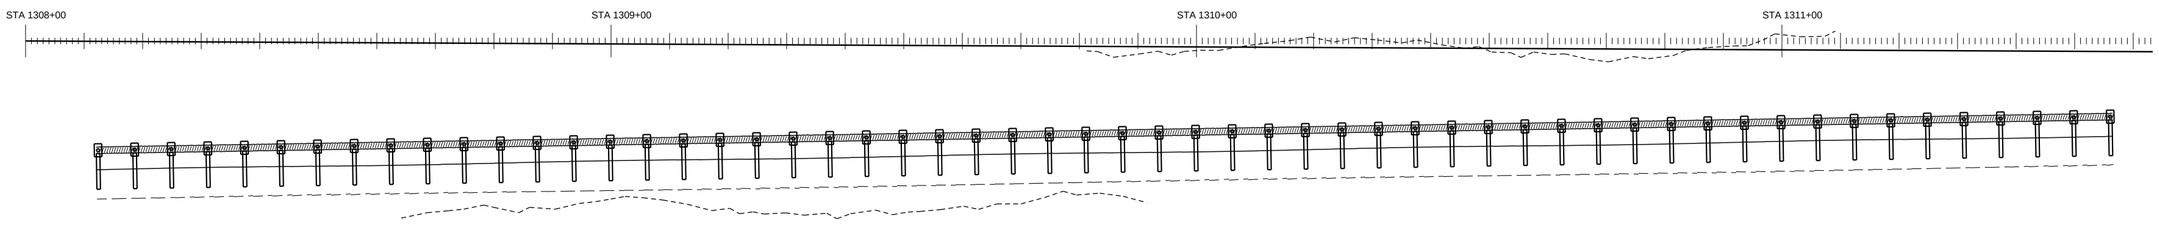


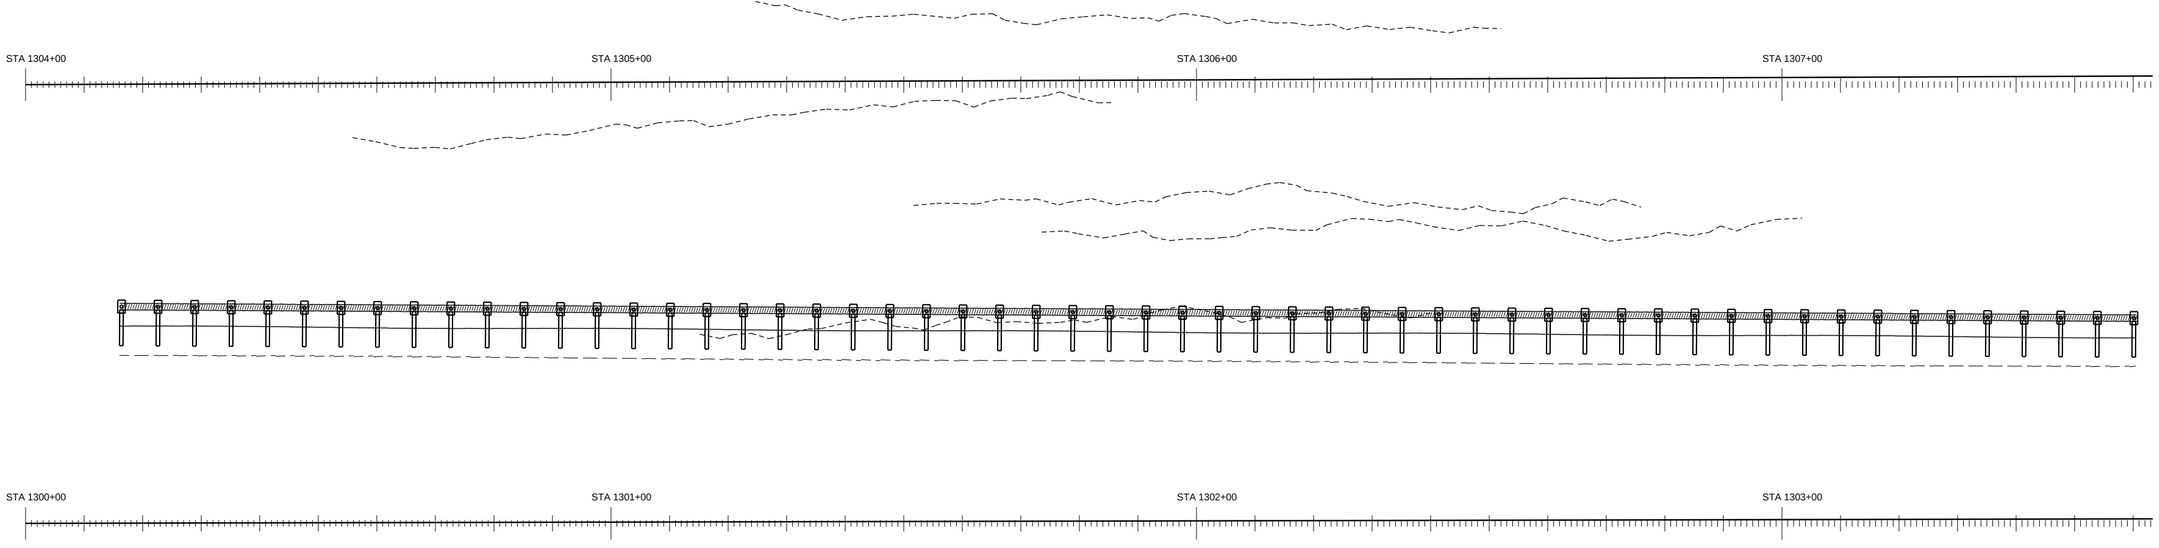





PAY ITEM 536-1-1 GUARDRAIL ROADWAY (TL-3)

PAY ITEM 536-85-24 END TREATMENT

GUARANTEED FENCE CORP

FIN. PROJ. ID 441234-1-52-01

SHEET 81 OF 120

SHEET NO. 181

ROADWAY PLAN SCALE: 1" = 20'

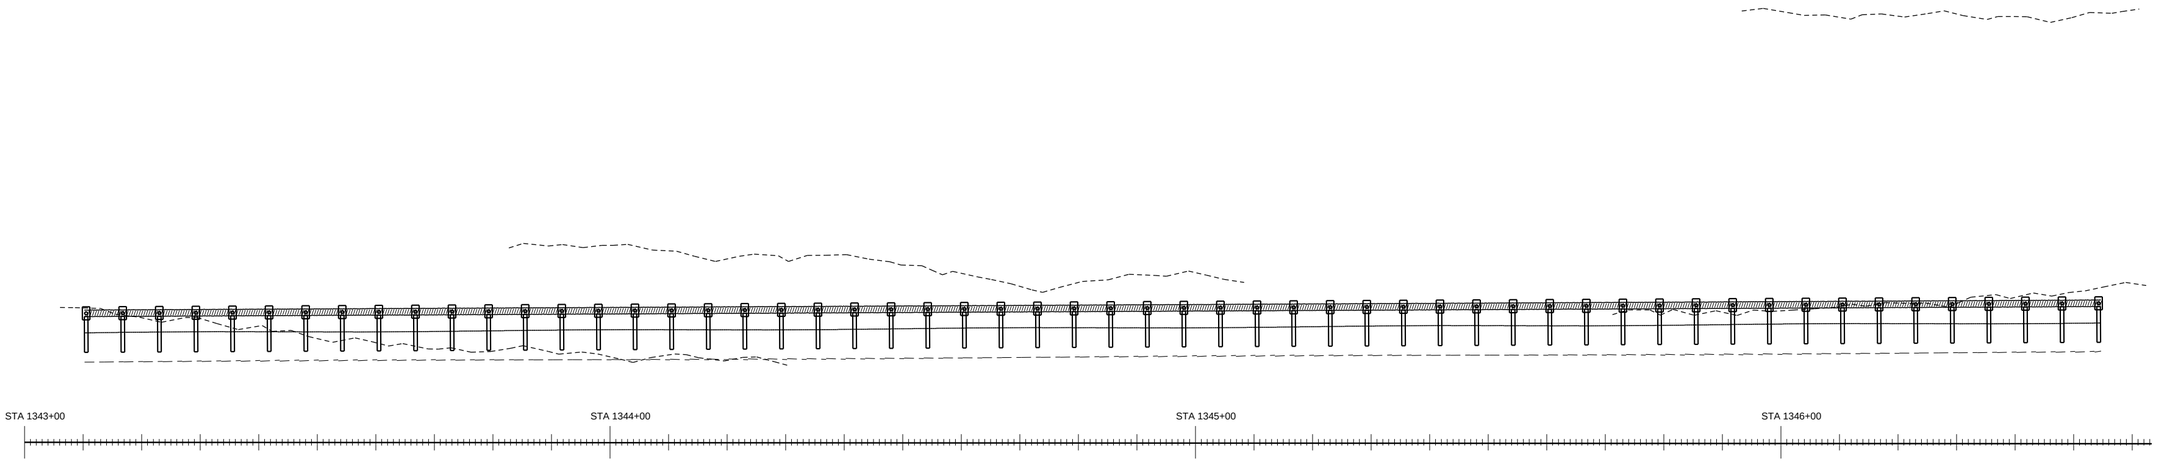


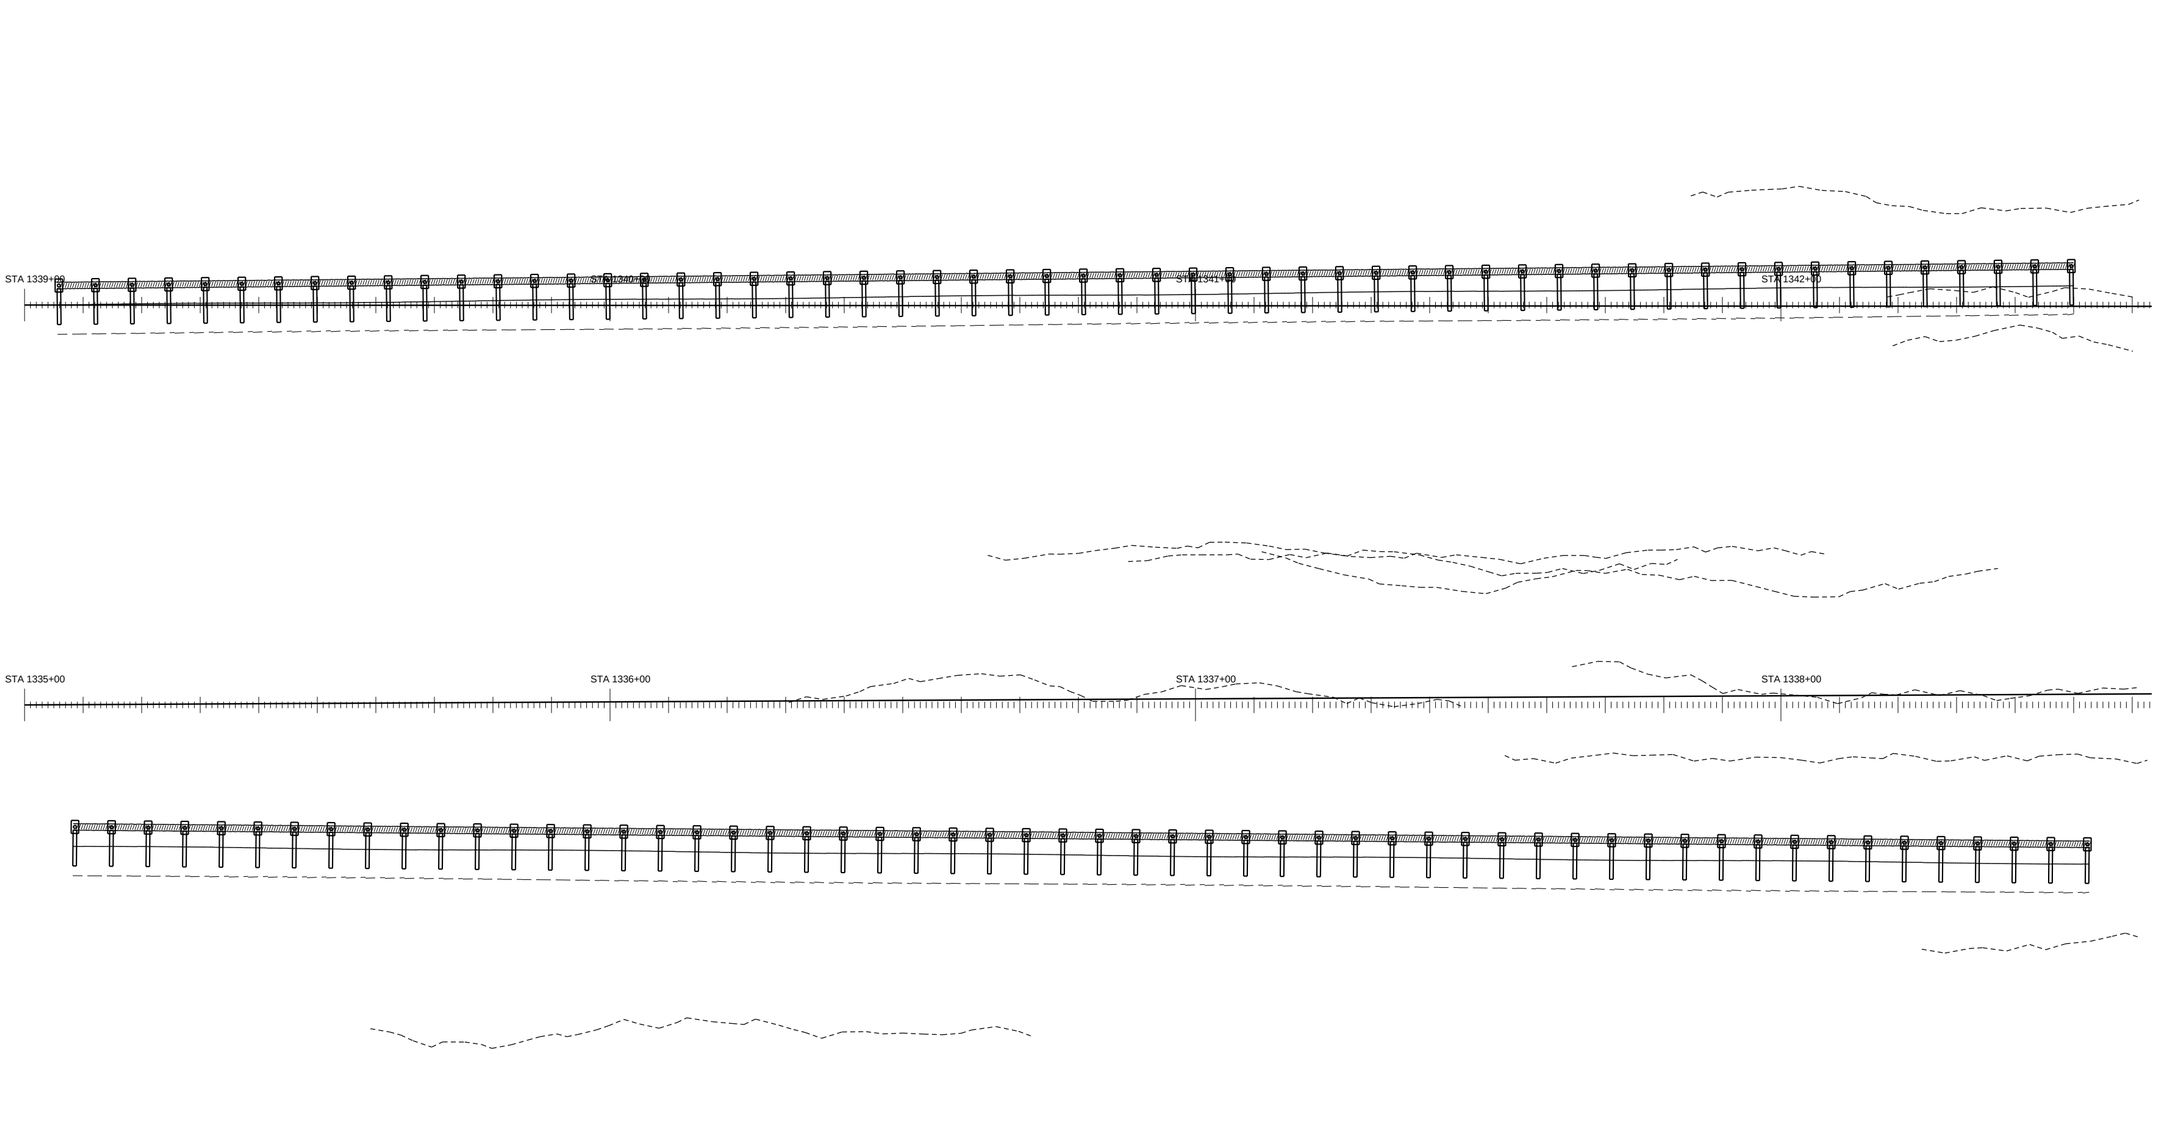


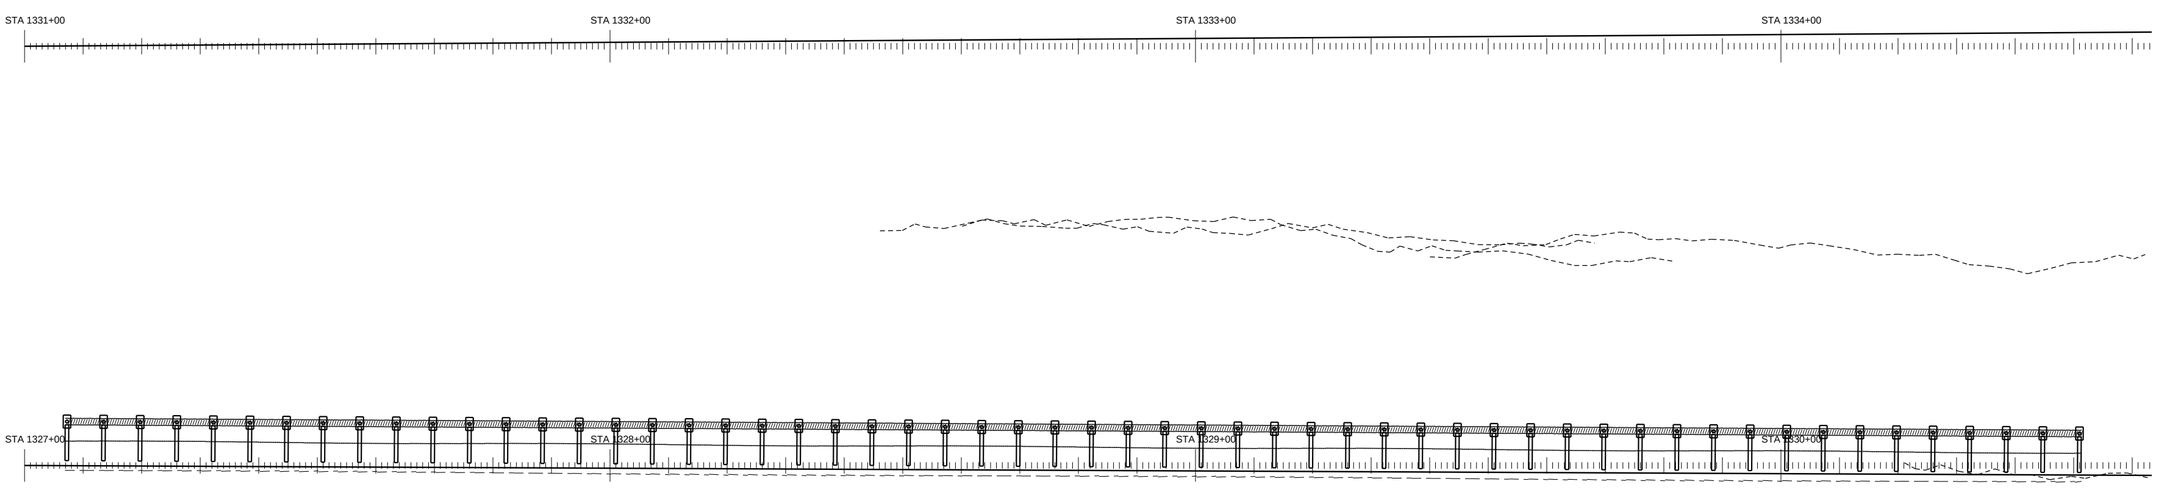


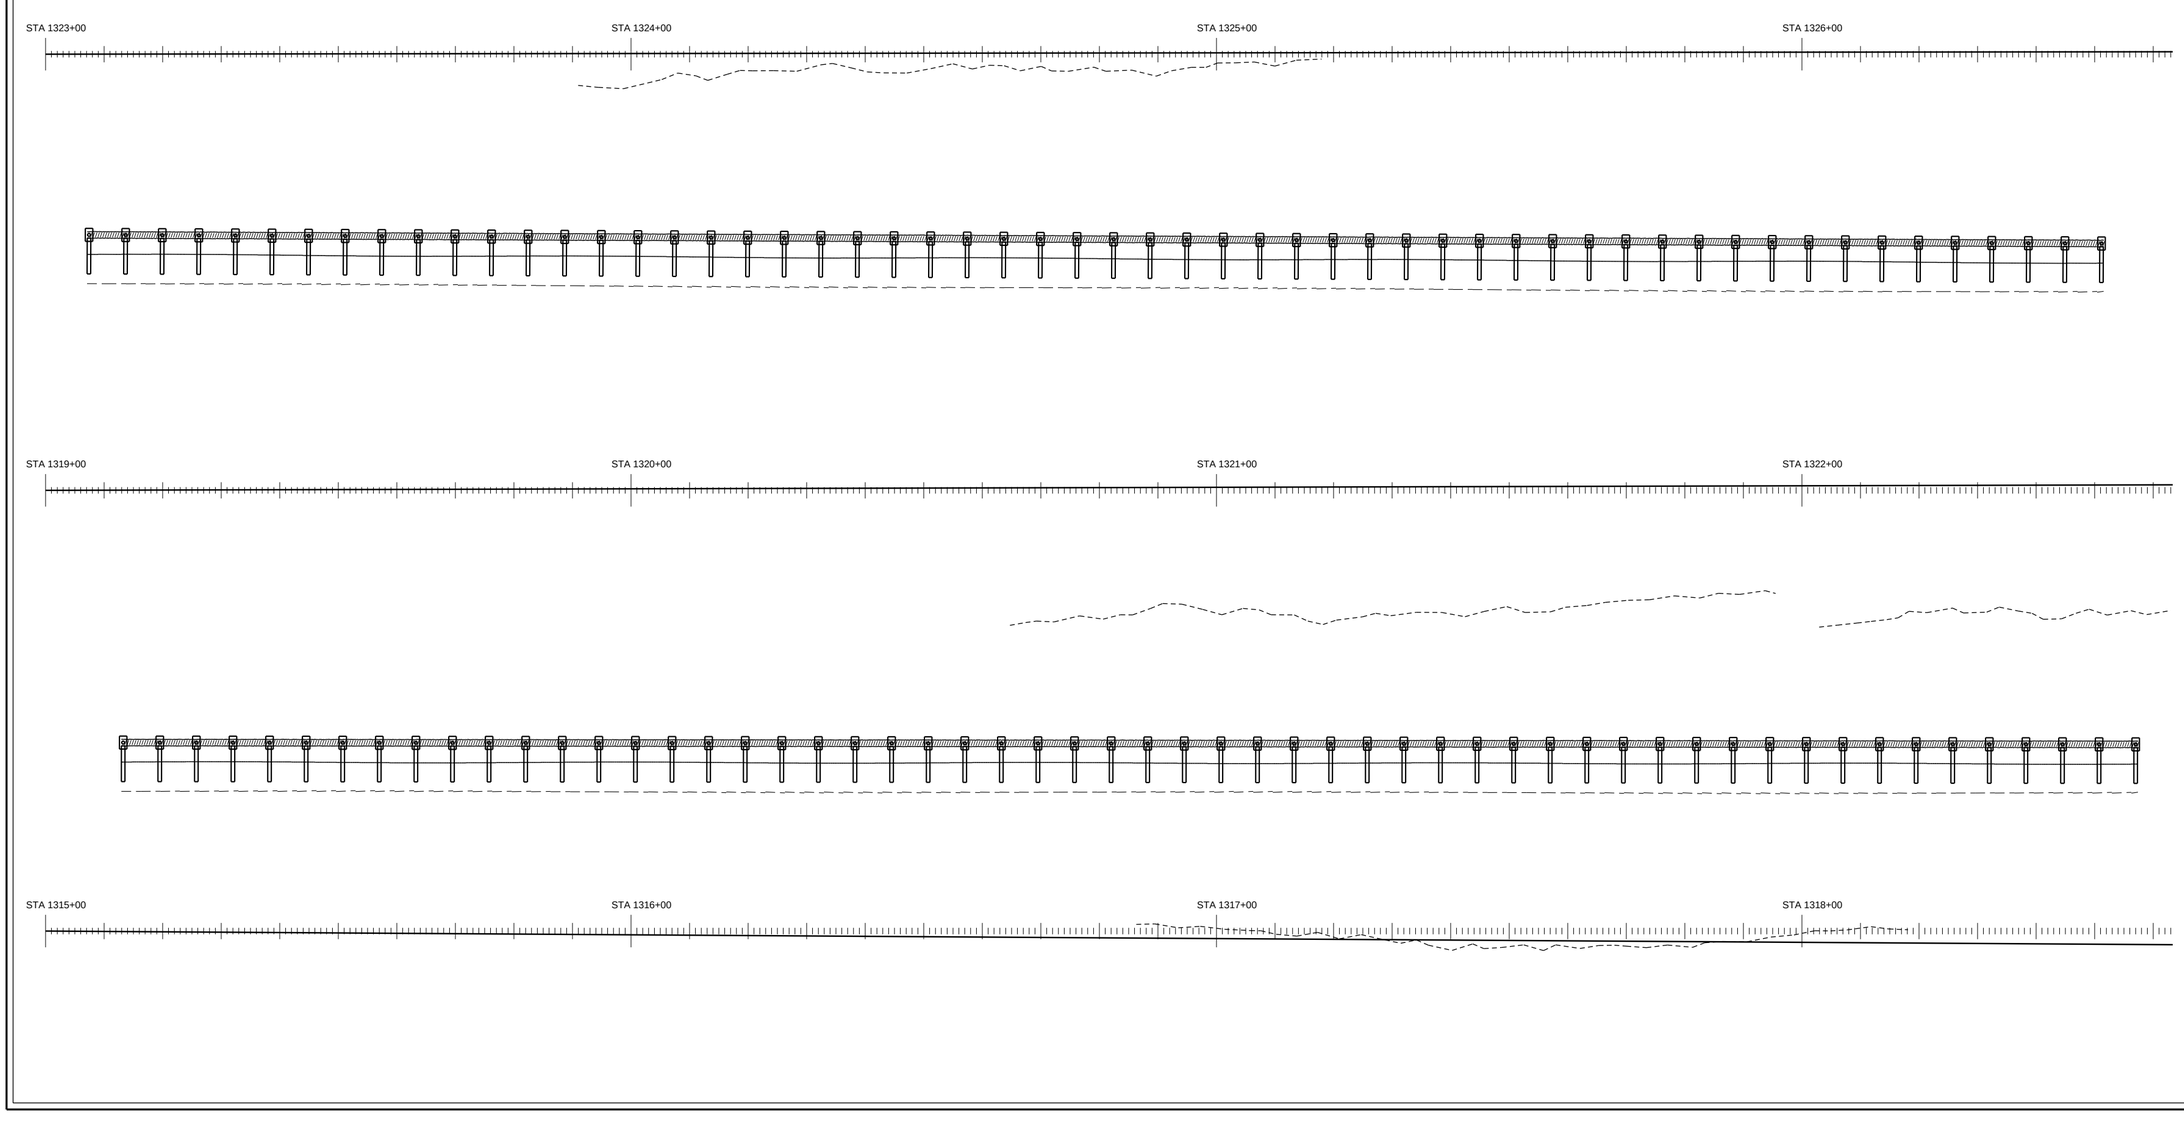


PAY ITEM 536-1-1 GUARDRAIL ROADWAY (TL-3)

PAY ITEM 536-85-24 END TREATMENT

GUARANTEED FENCE CORP

FIN. PROJ. ID 441234-1-52-01

SHEET 82 OF 120

SHEET NO. 182

ROADWAY PLAN SCALE: 1" = 20'

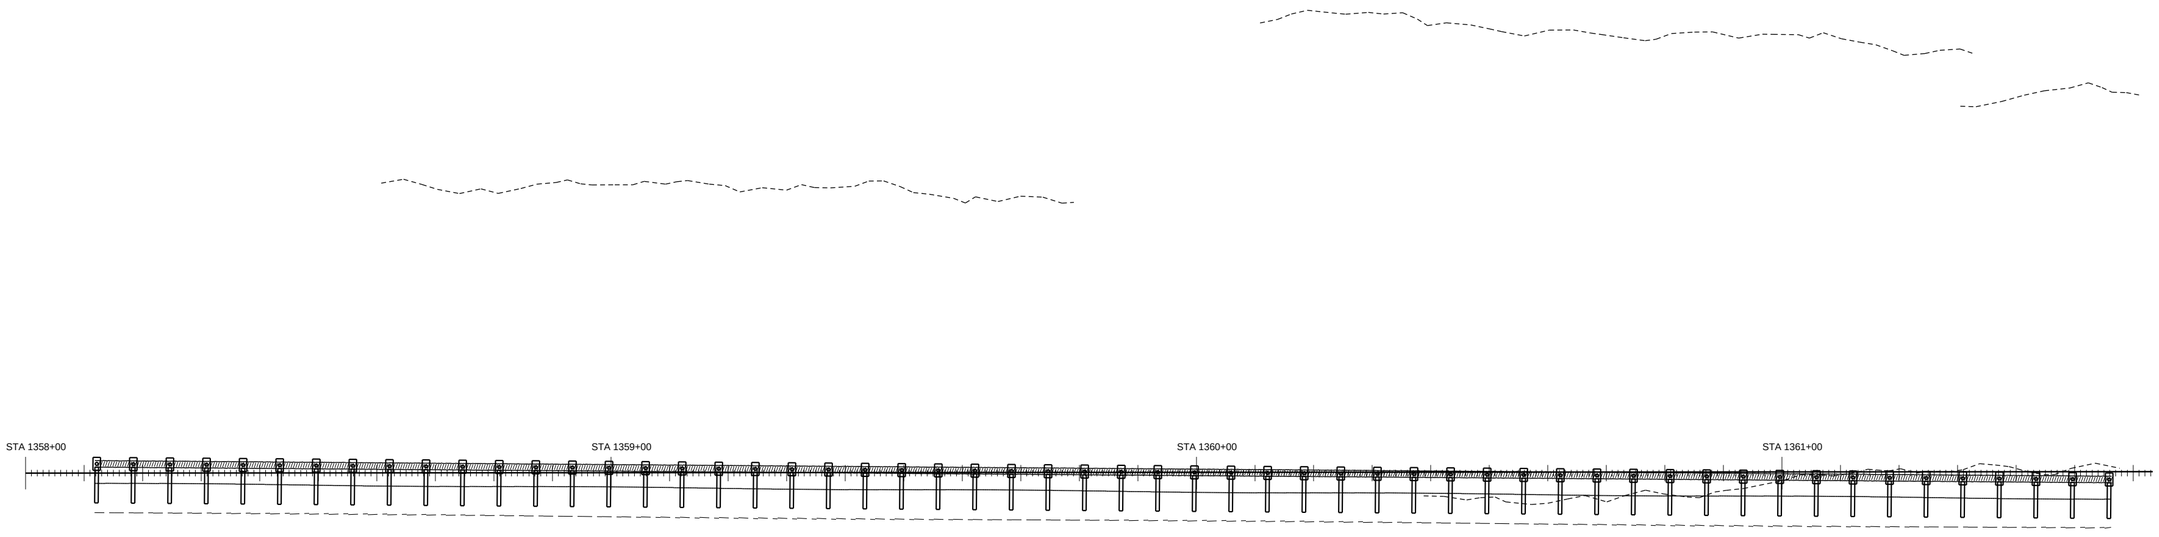


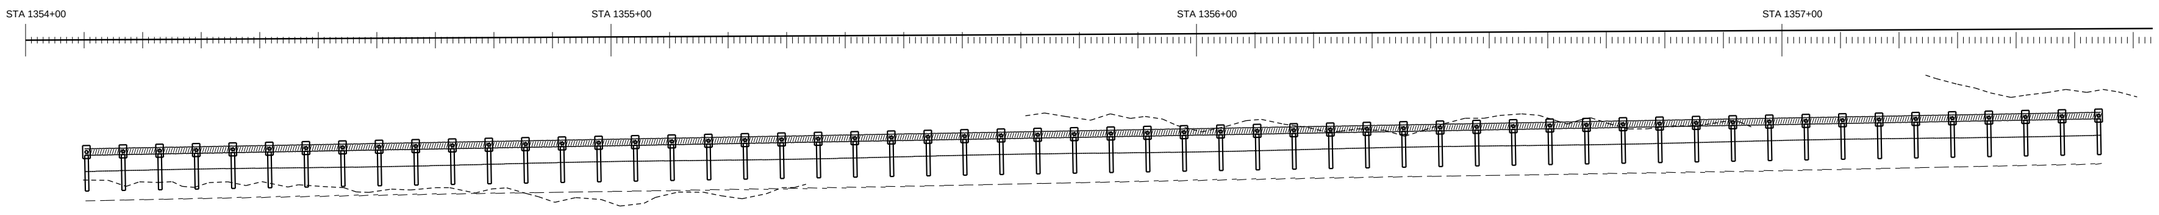


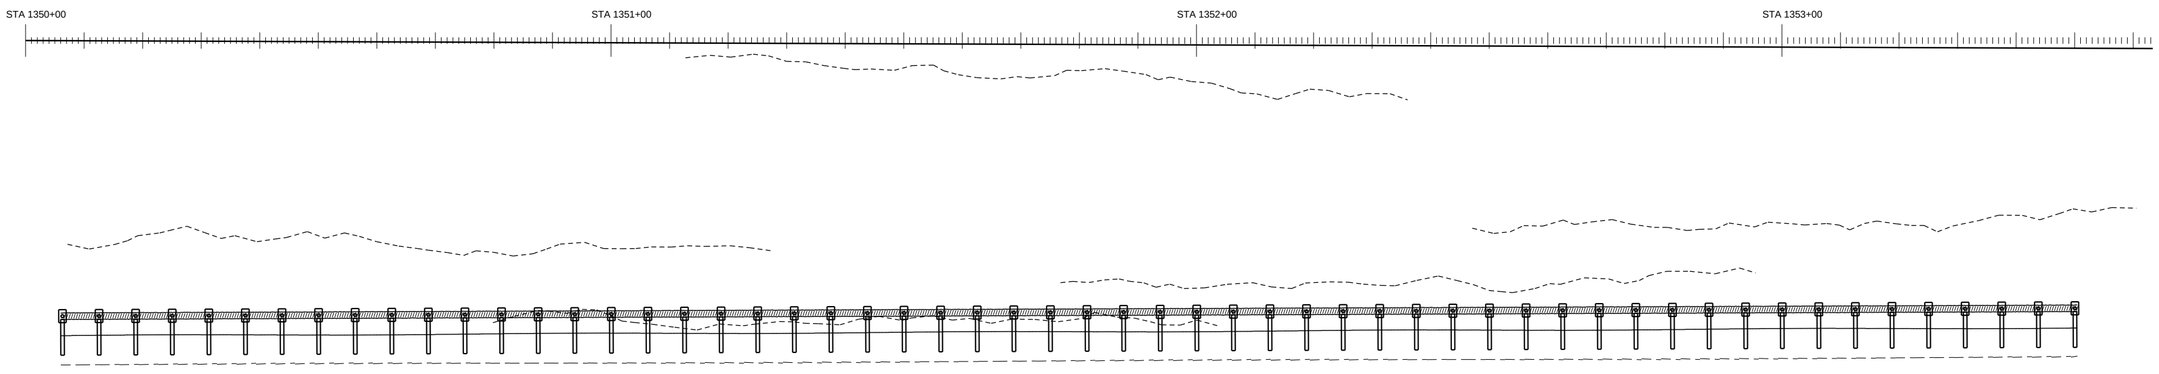


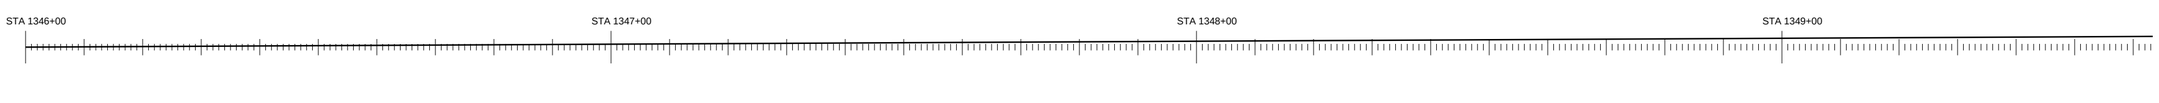


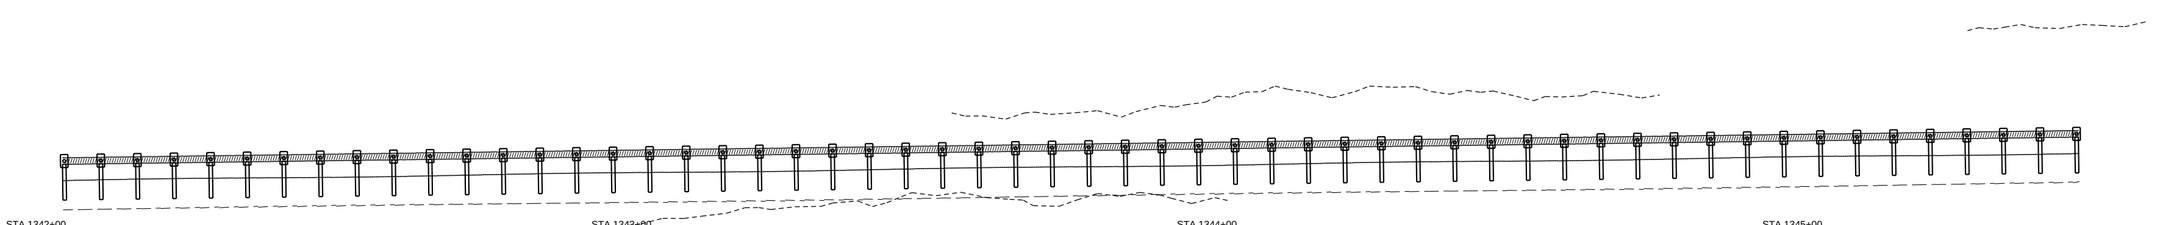


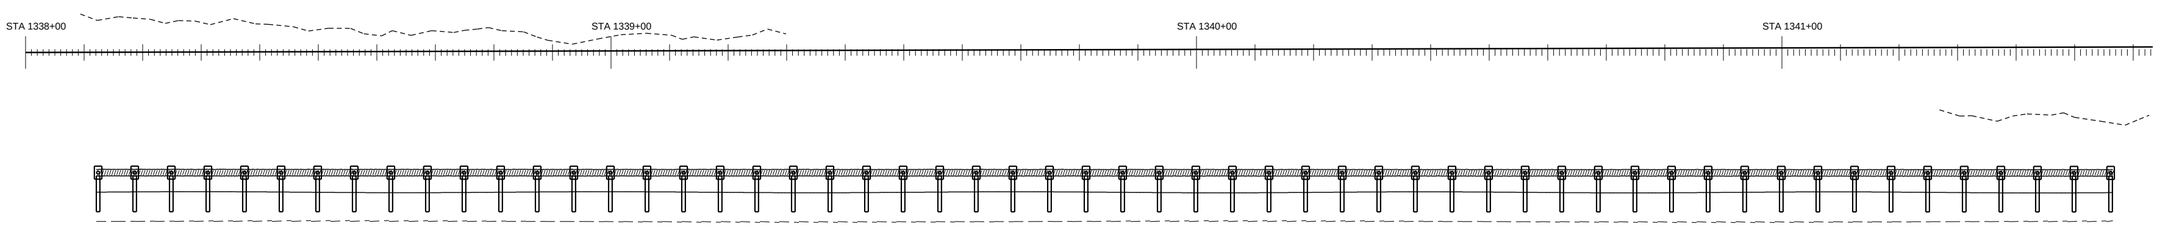


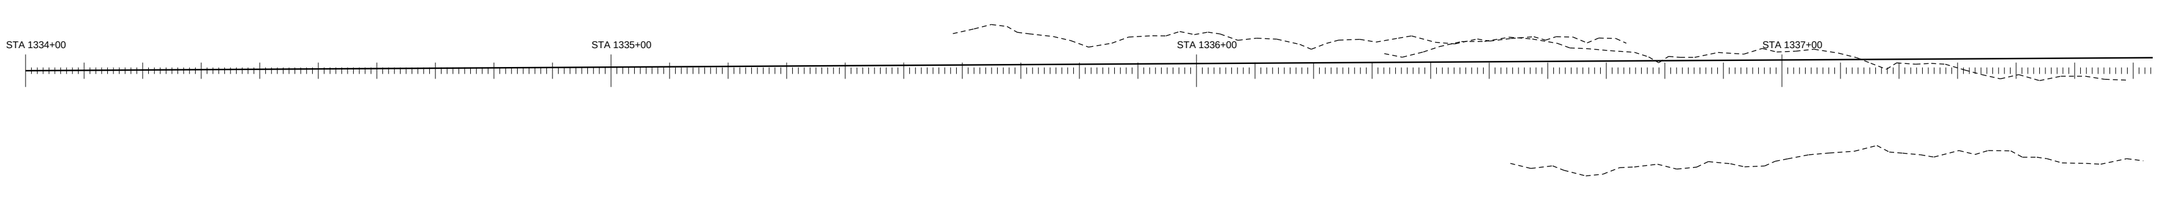


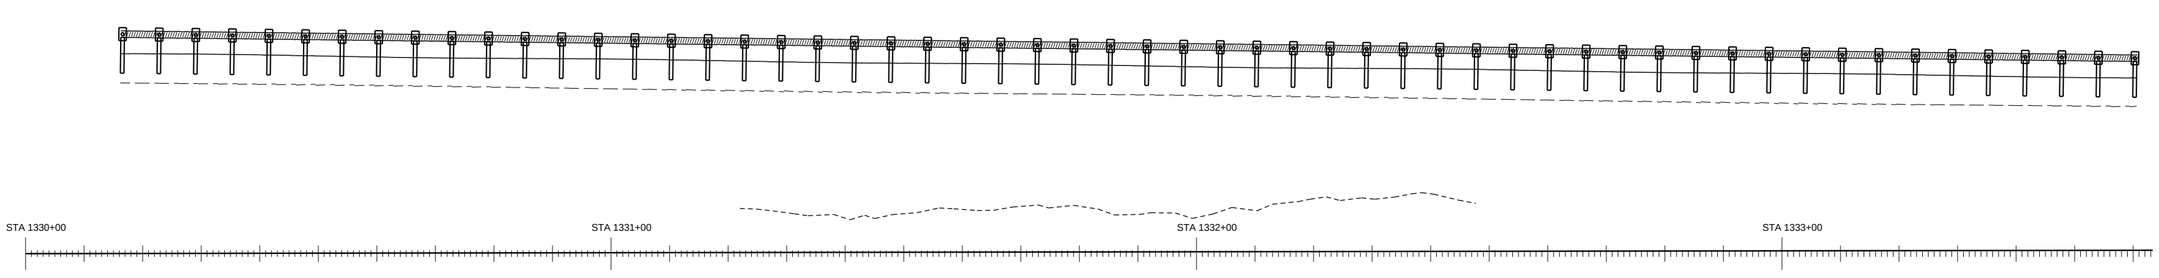


PAY ITEM 536-1-1 GUARDRAIL ROADWAY (TL-3)

PAY ITEM 536-85-24 END TREATMENT

GUARANTEED FENCE CORP

FIN. PROJ. ID 441234-1-52-01

SHEET 83 OF 120

SHEET NO. 183

ROADWAY PLAN SCALE: 1" = 20'

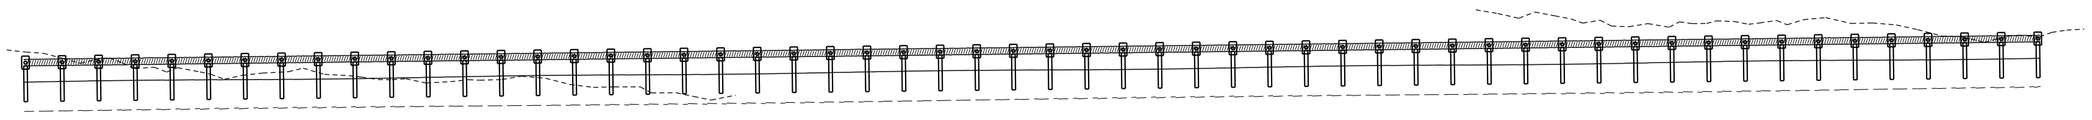

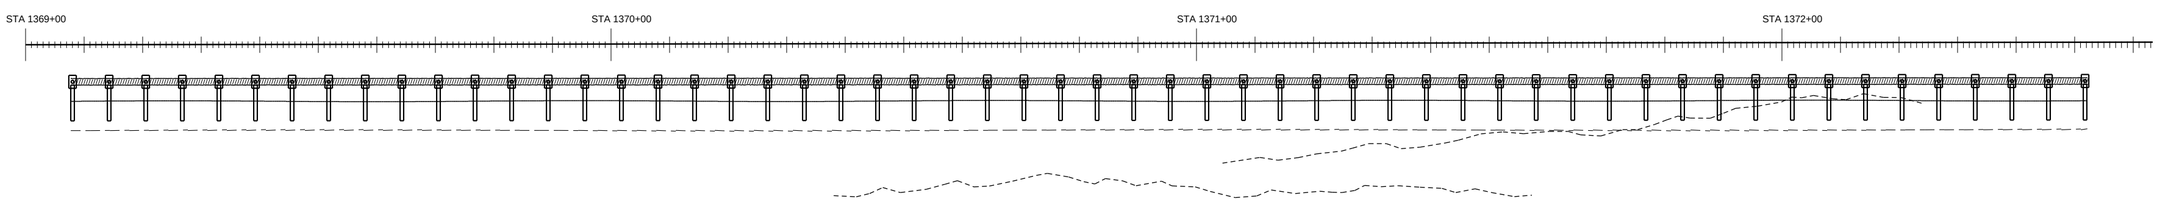


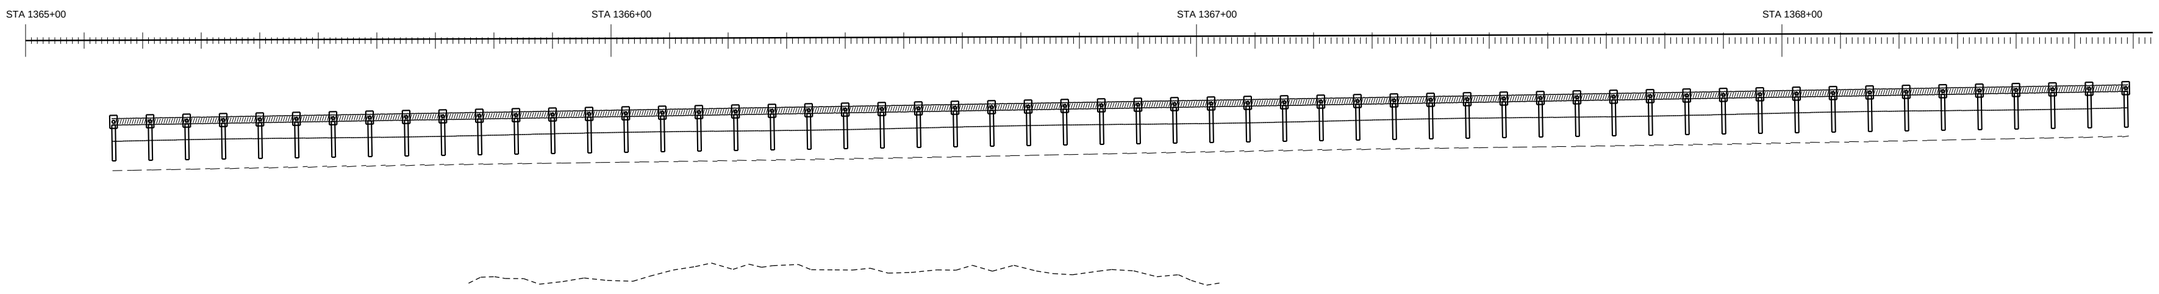


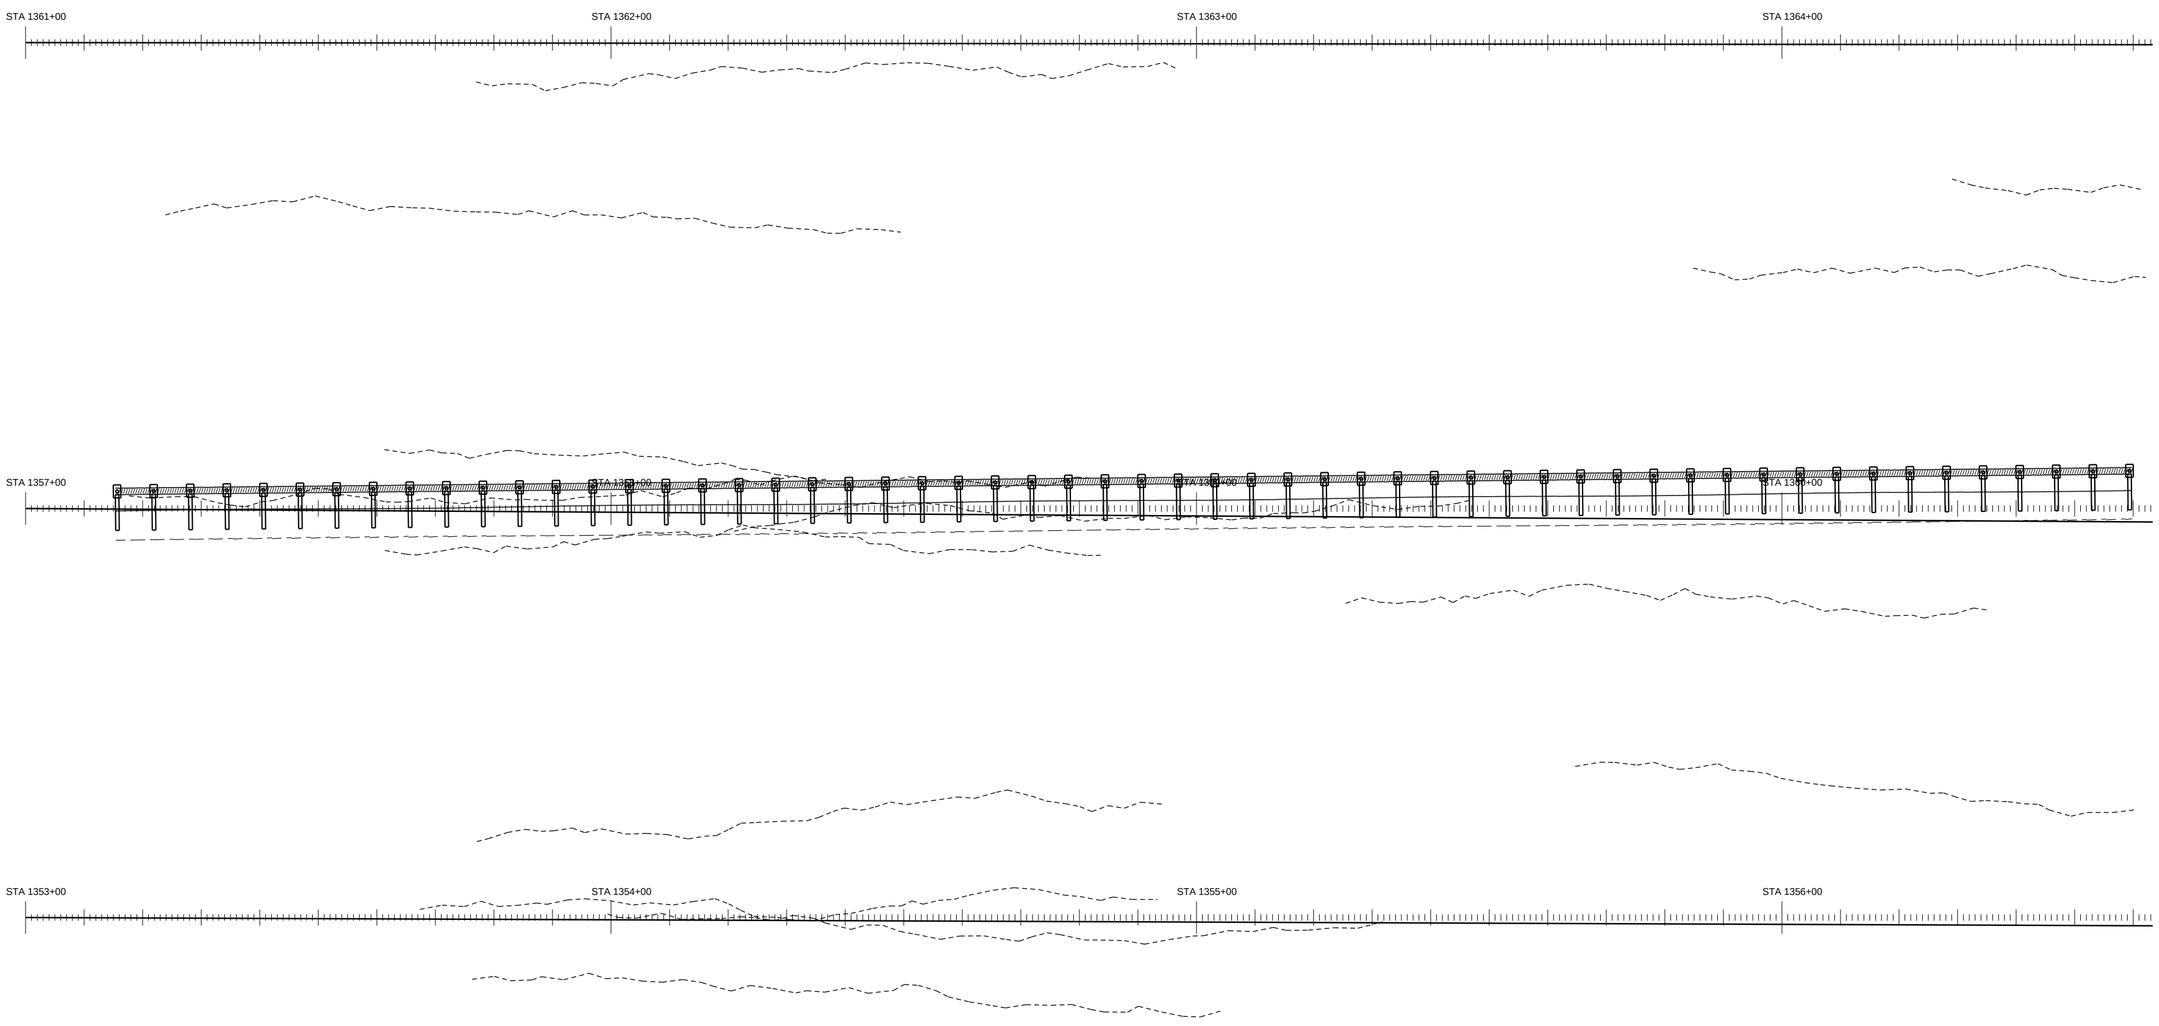


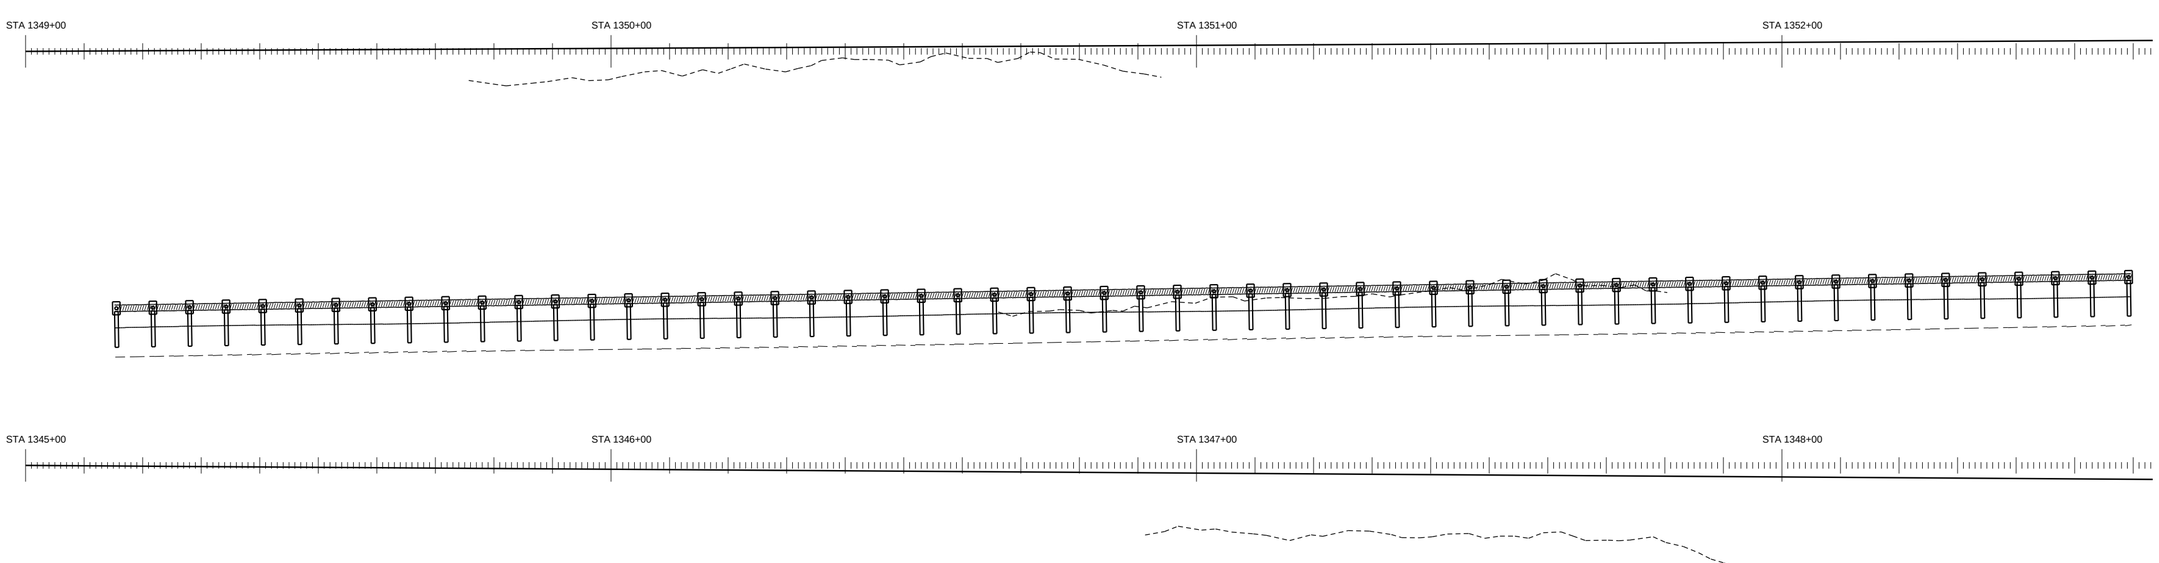


PAY ITEM 536-1-1 GUARDRAIL ROADWAY (TL-3)

PAY ITEM 536-85-24 END TREATMENT

GUARANTEED FENCE CORP

FIN. PROJ. ID 441234-1-52-01

SHEET 84 OF 120

SHEET NO. 184

ROADWAY PLAN SCALE: 1" = 20'

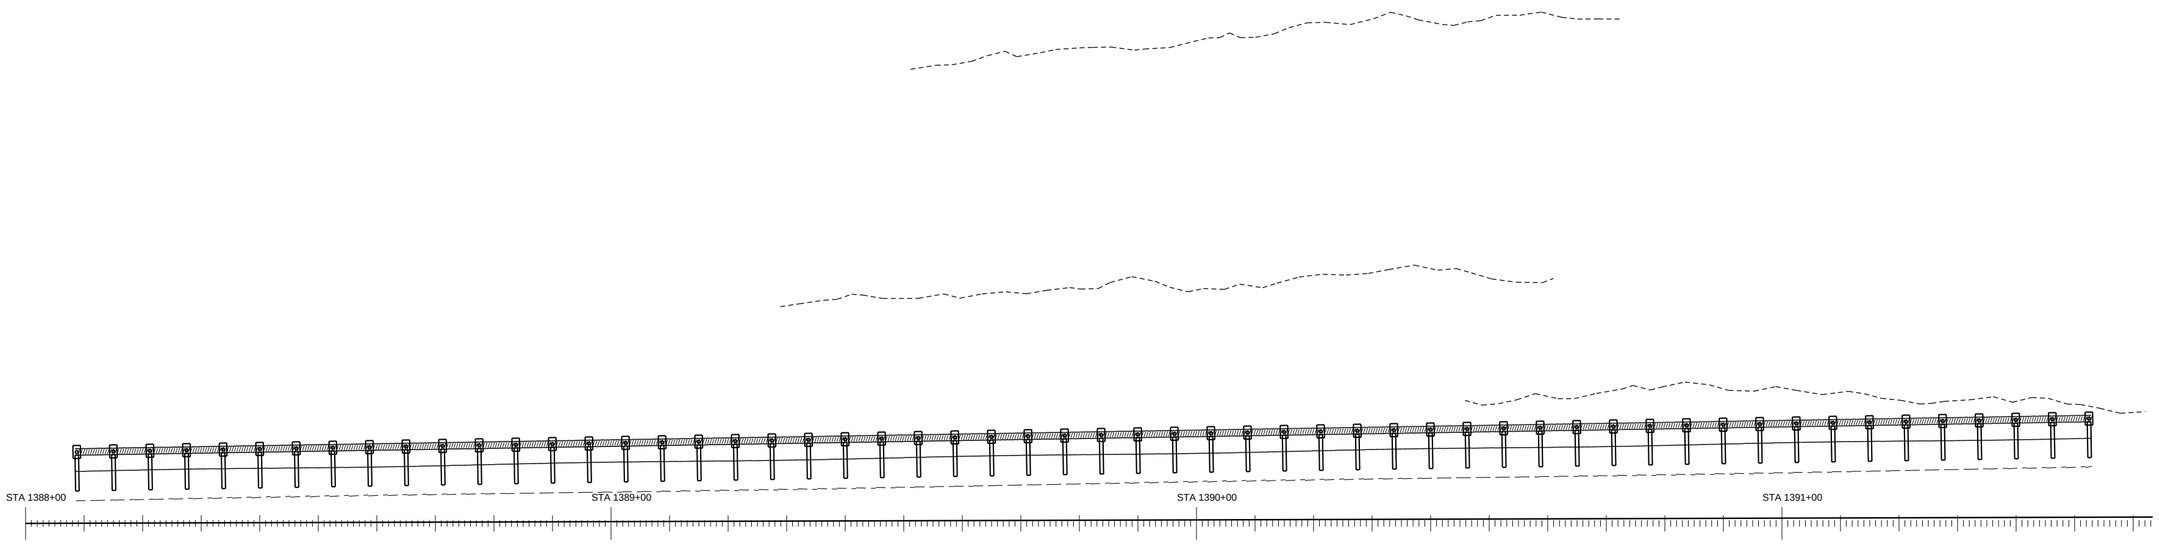


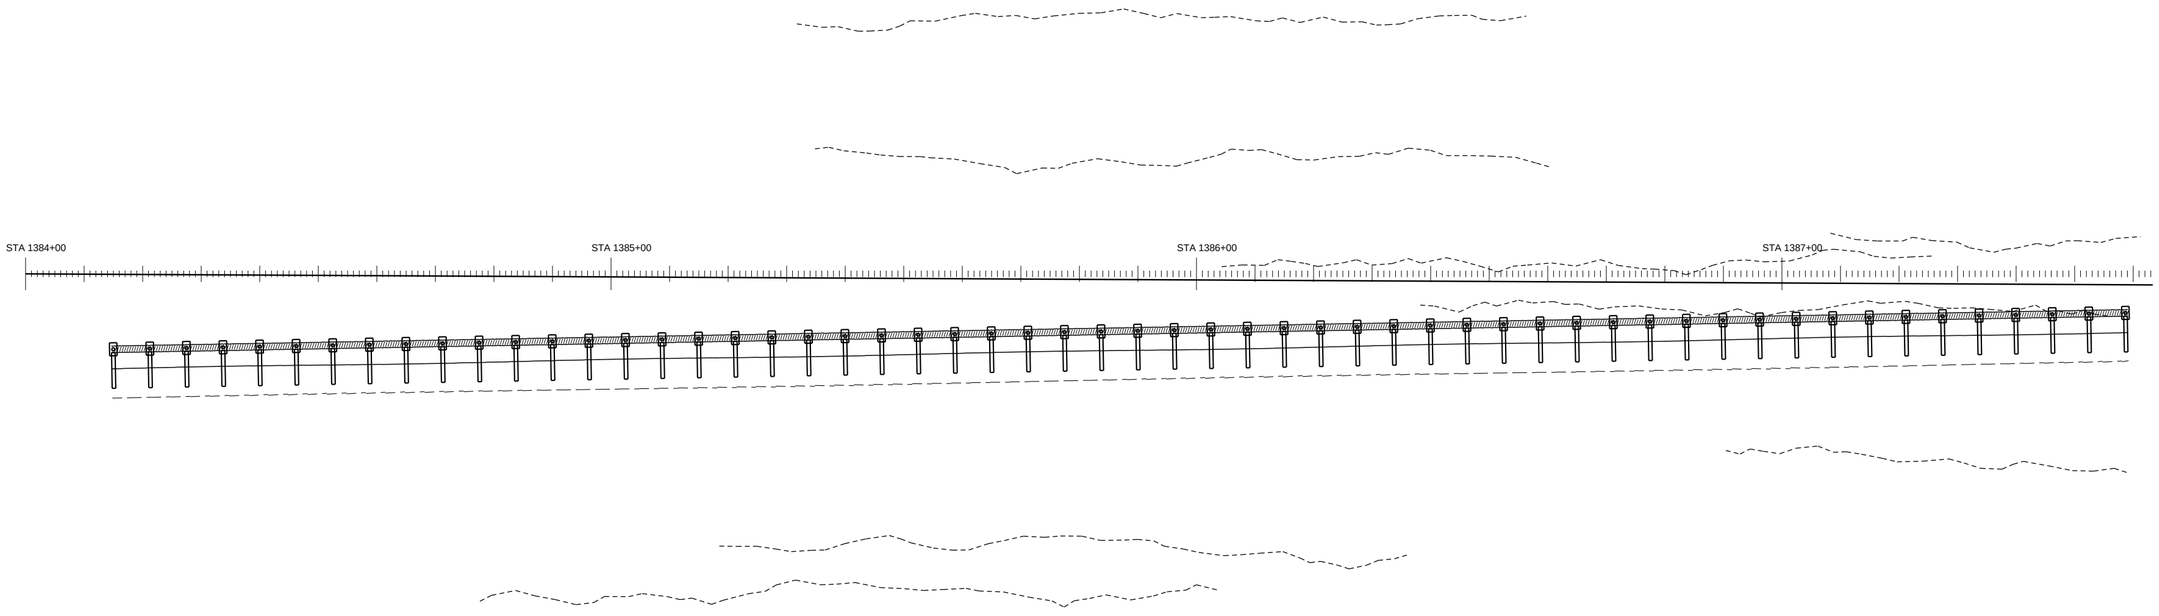


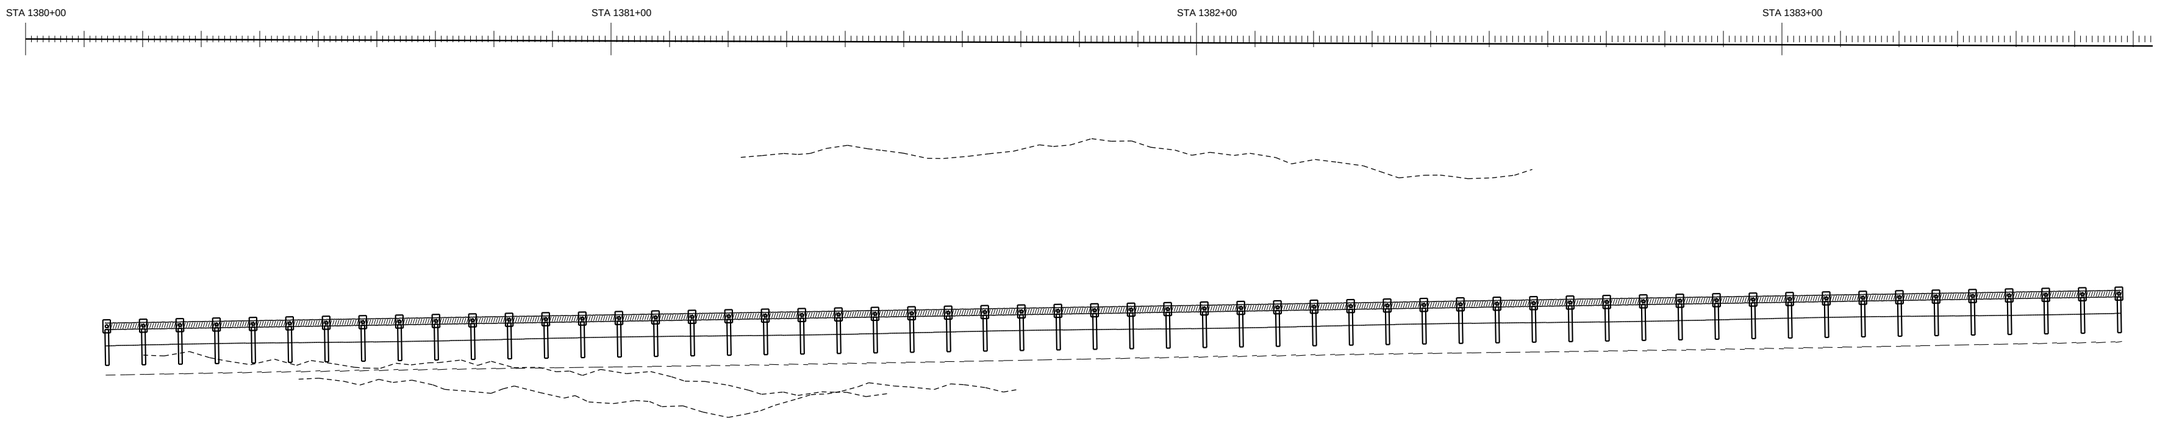


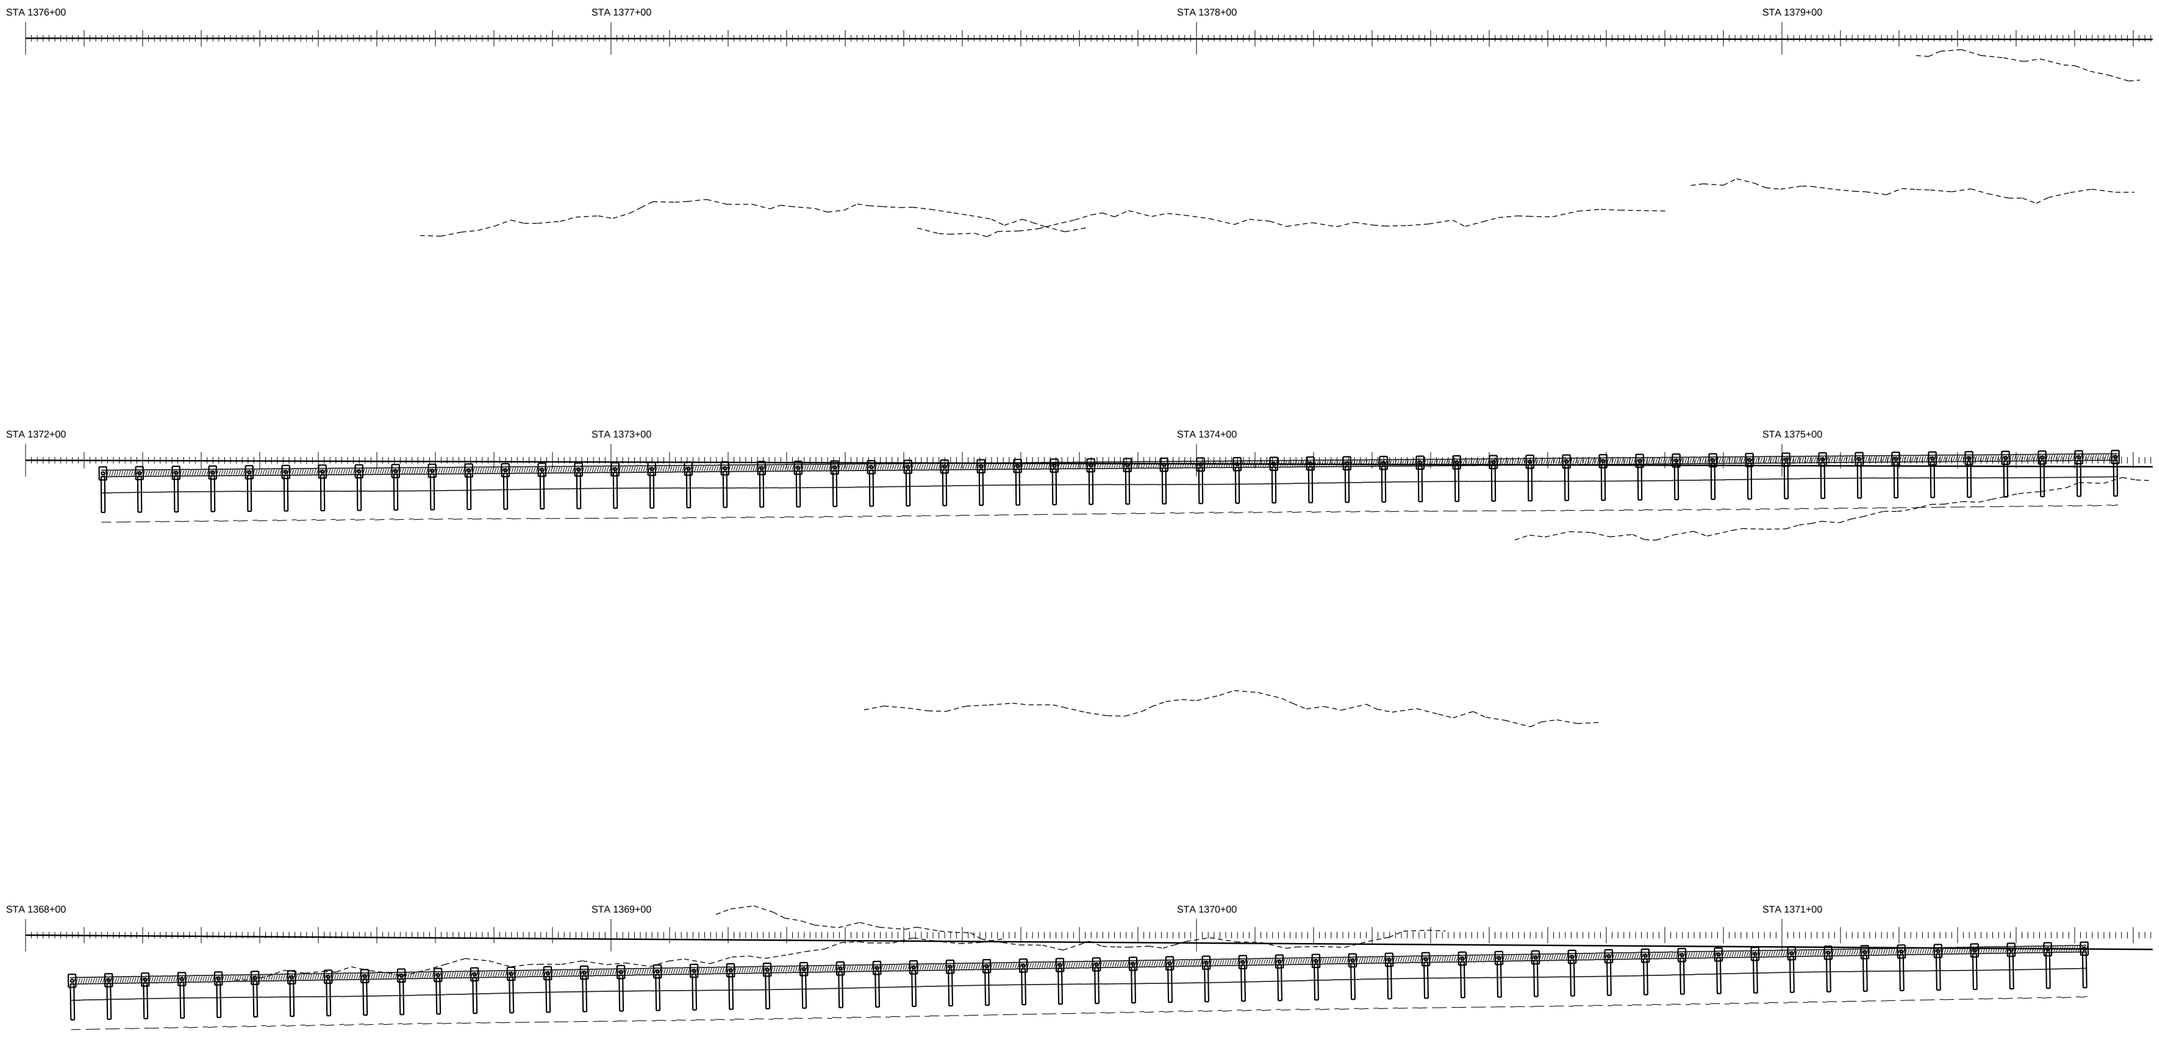








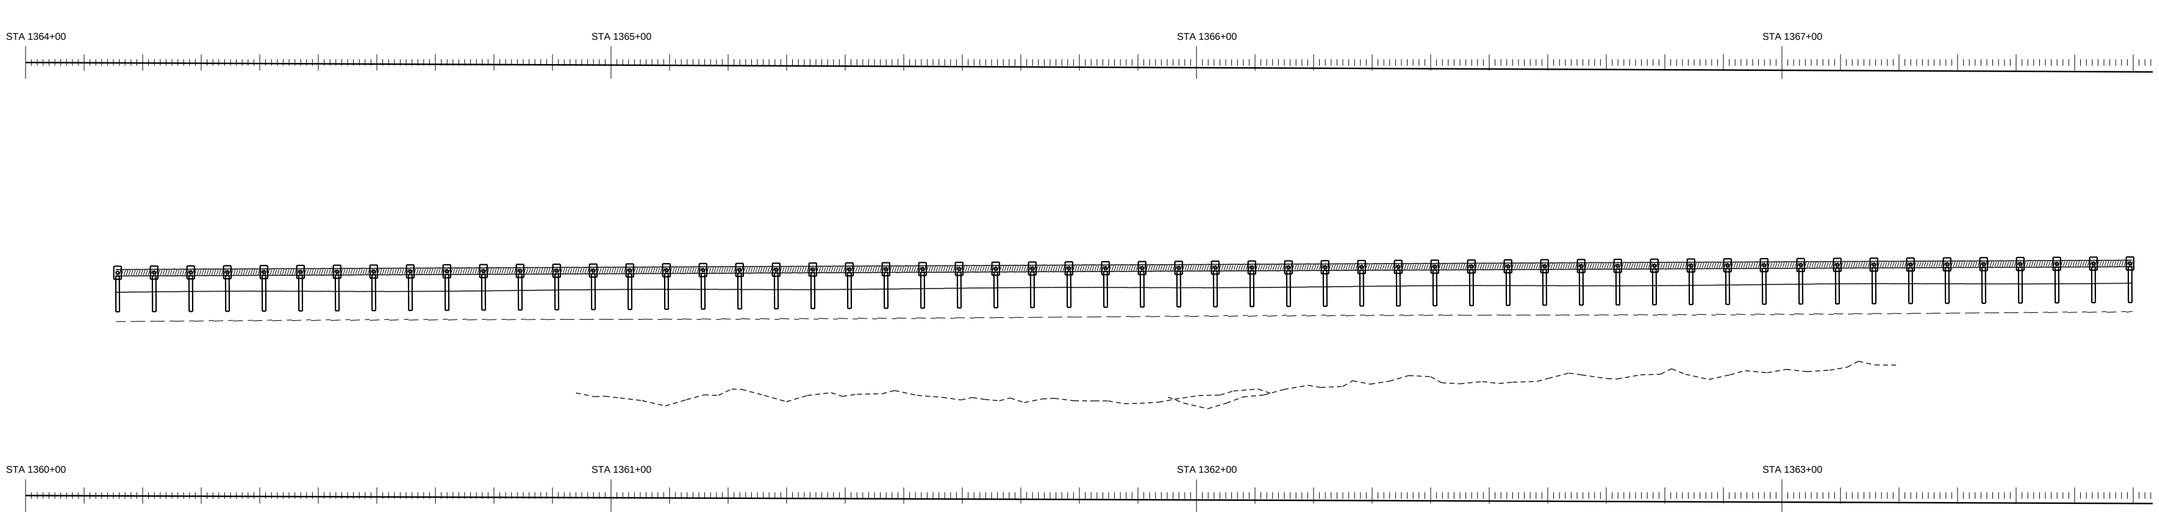


PAY ITEM 536-1-1 GUARDRAIL ROADWAY (T-3)

PAY ITEM 536-85-24 END TREATMENT

GUARANTEED FENCE CORP

FIN. PROJ. ID 441234-1-52-01

SHEET 85 OF 120

SHEET NO. 185

ROADWAY PLAN SCALE: 1" = 20'

GUARANTEED FENCE CORP

FIN. PROJ. ID 441234-1-52-01

SHEET 86 OF 120

SHEET NO. 186

ROADWAY PLAN SCALE: 1" = 20'




PAY ITEM 536-1-1 GUARDRAIL ROADWAY (TL-3)

PAY ITEM 536-85-24 END TREATMENT

GUARANTEED FENCE CORP

FIN. PROJ. ID 441234-1-52-01

SHEET 87 OF 120

SHEET NO. 187

ROADWAY PLAN SCALE: 1" = 20'




PAY ITEM 536-1-1 GUARDRAIL ROADWAY (TL-3)

PAY ITEM 536-85-24 END TREATMENT

GUARANTEED FENCE CORP

FIN. PROJ. ID 441234-1-52-01

SHEET 88 OF 120

SHEET NO. 188

ROADWAY PLAN SCALE: 1" = 20'

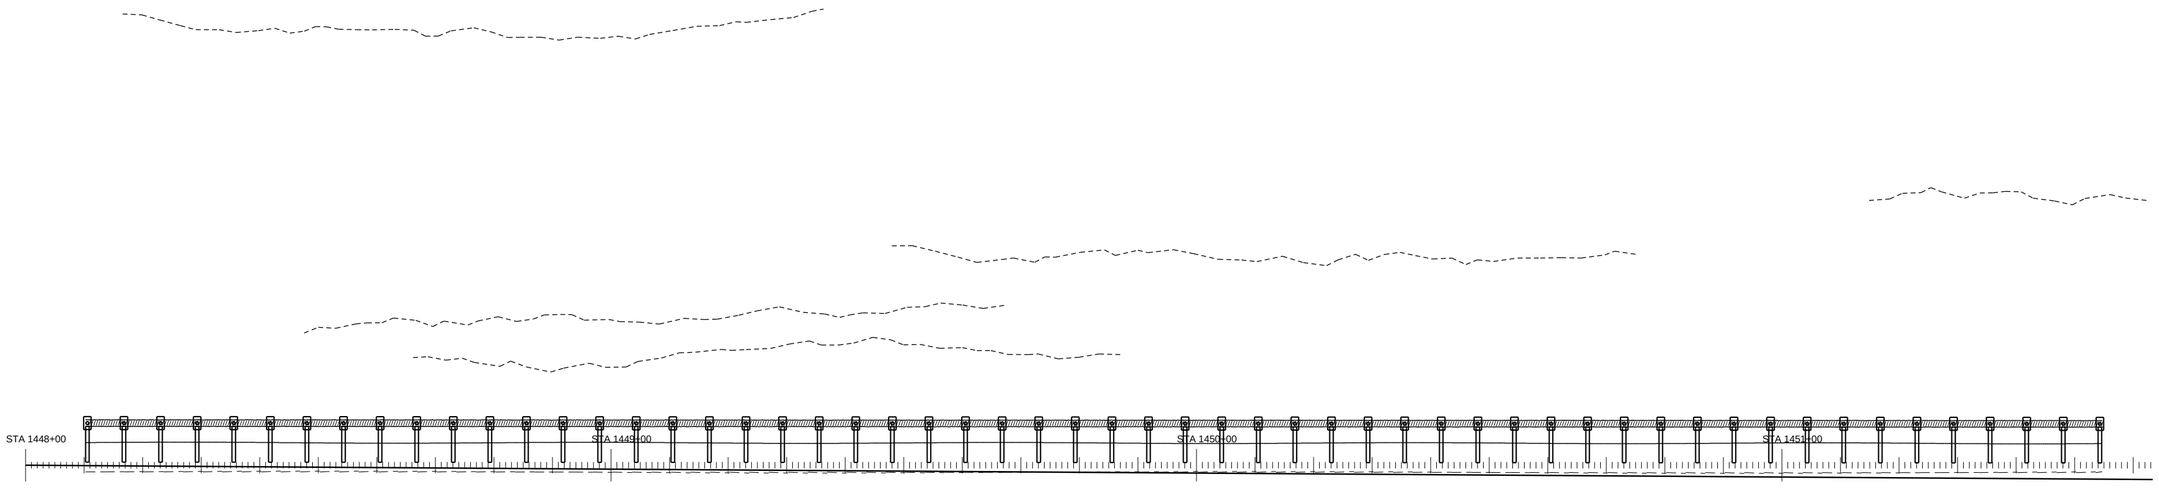


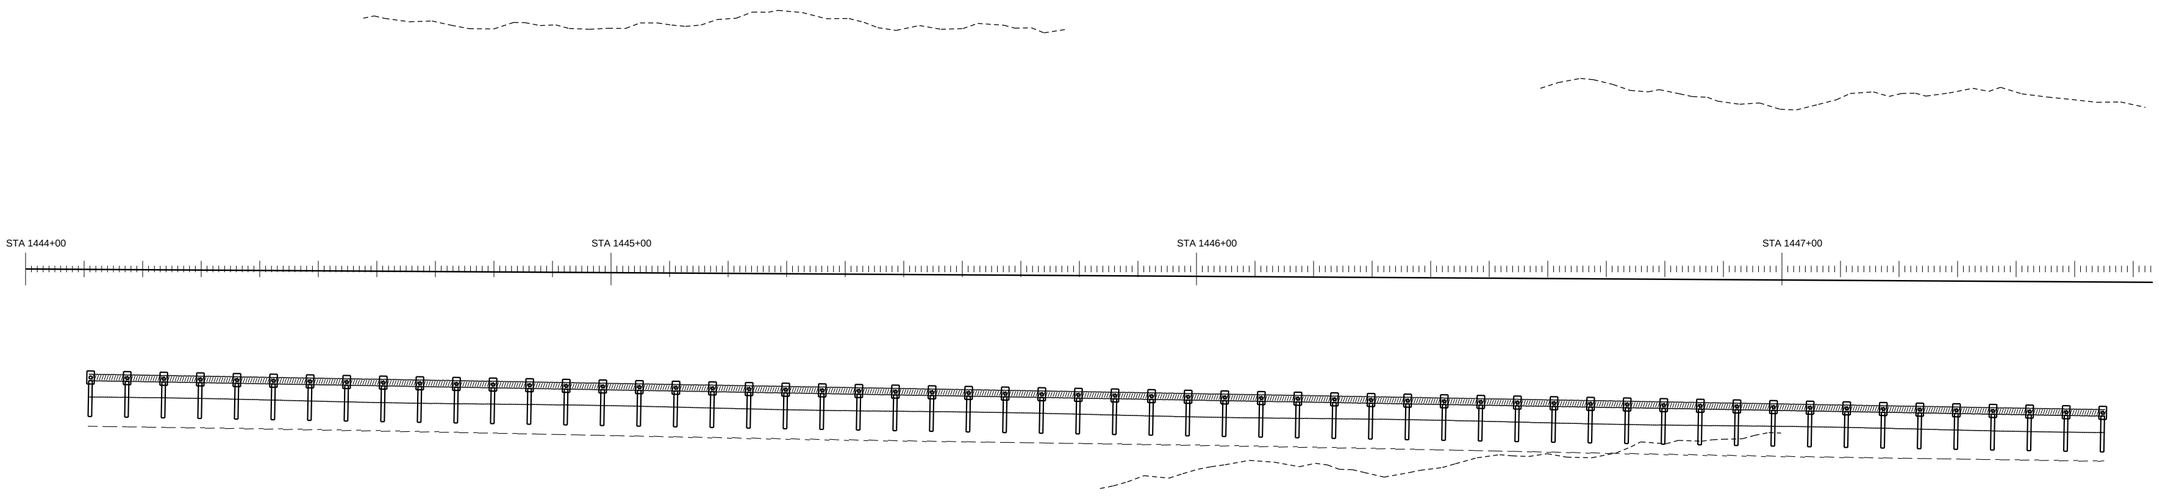


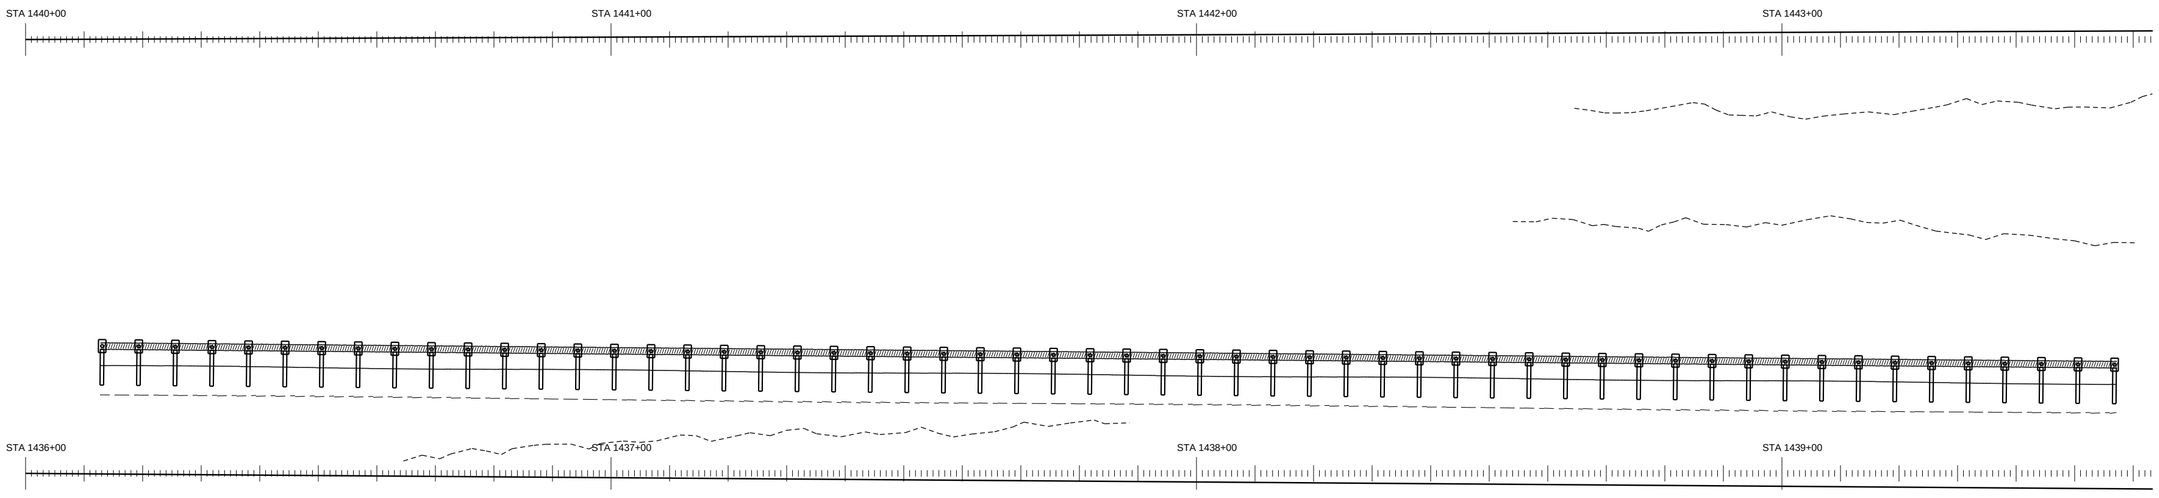


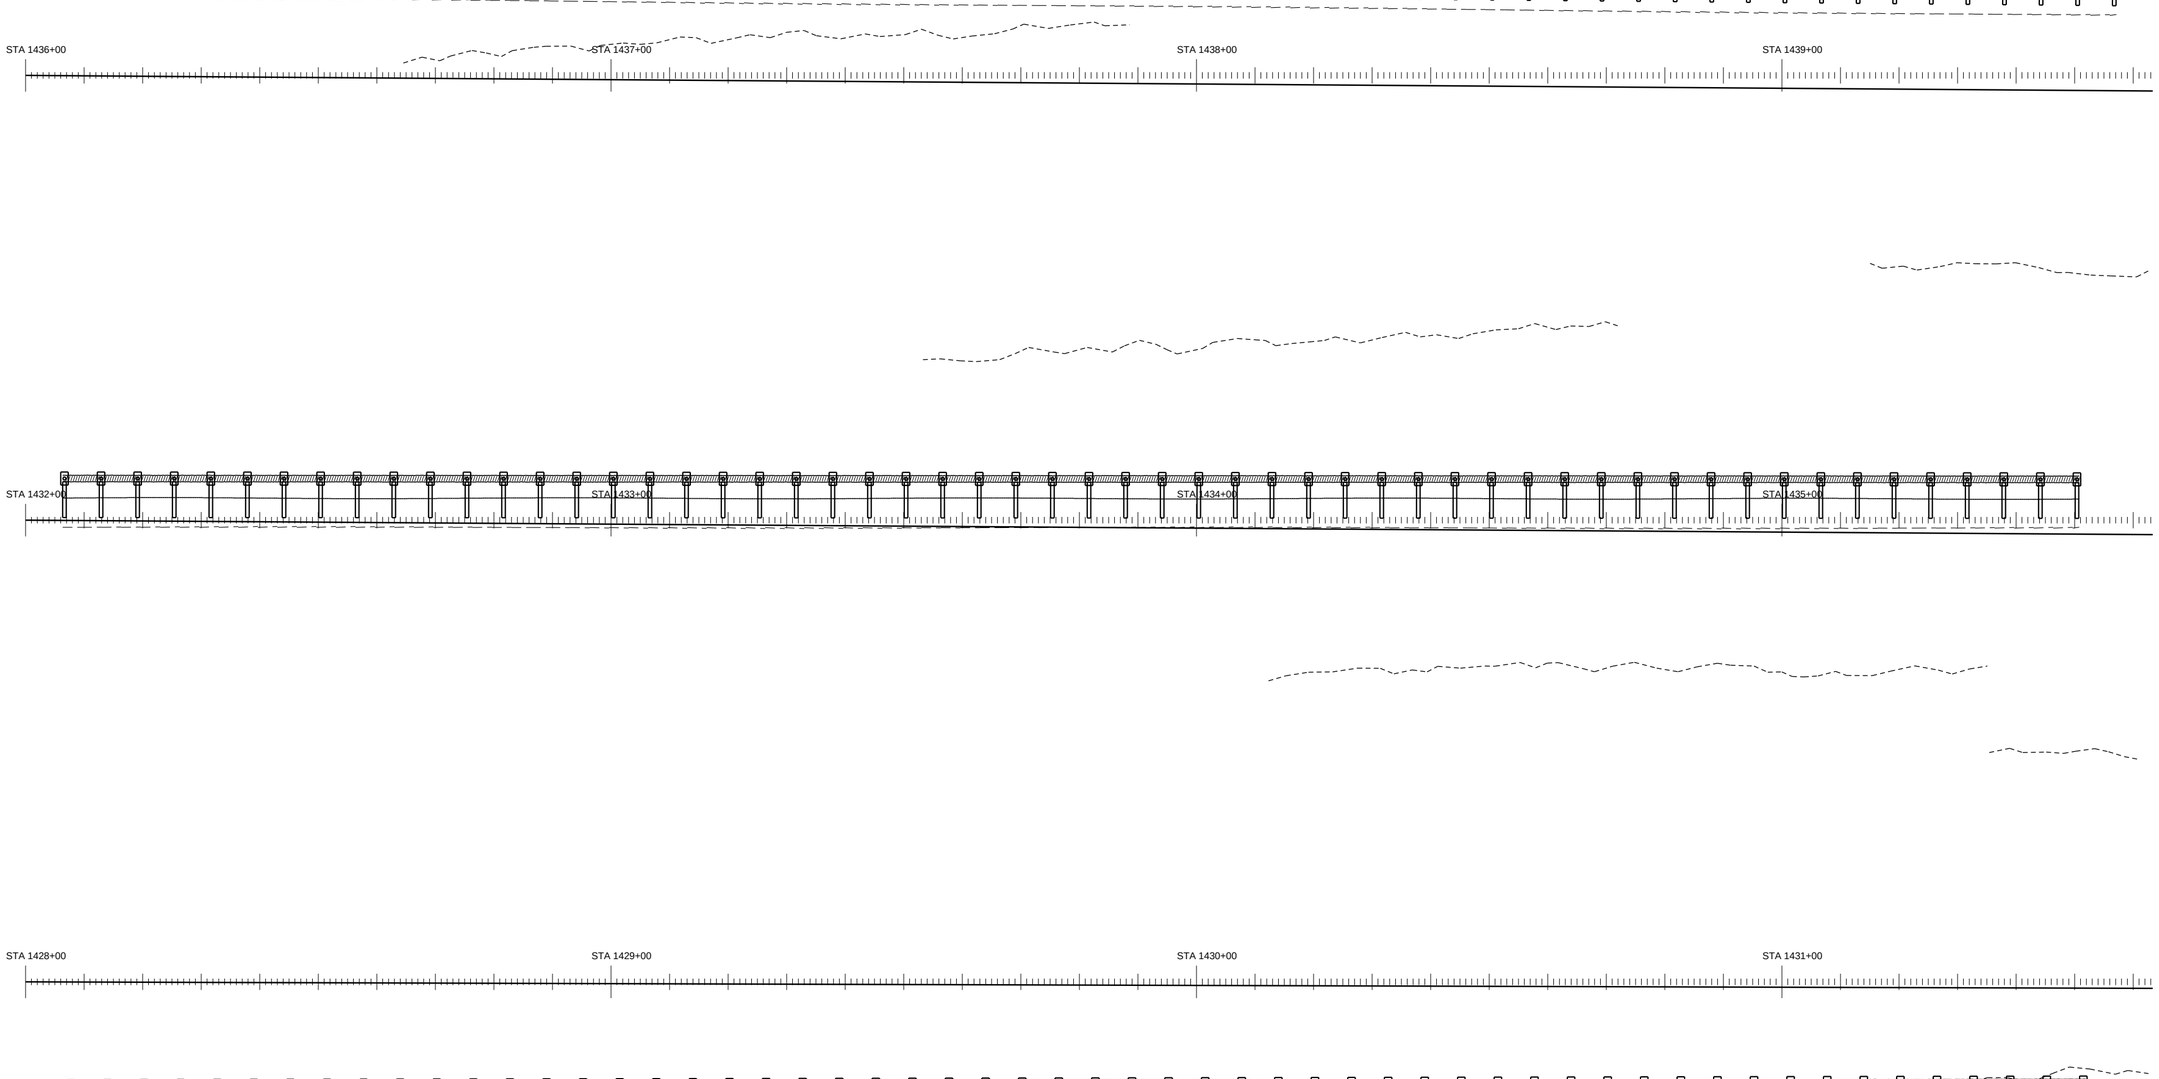


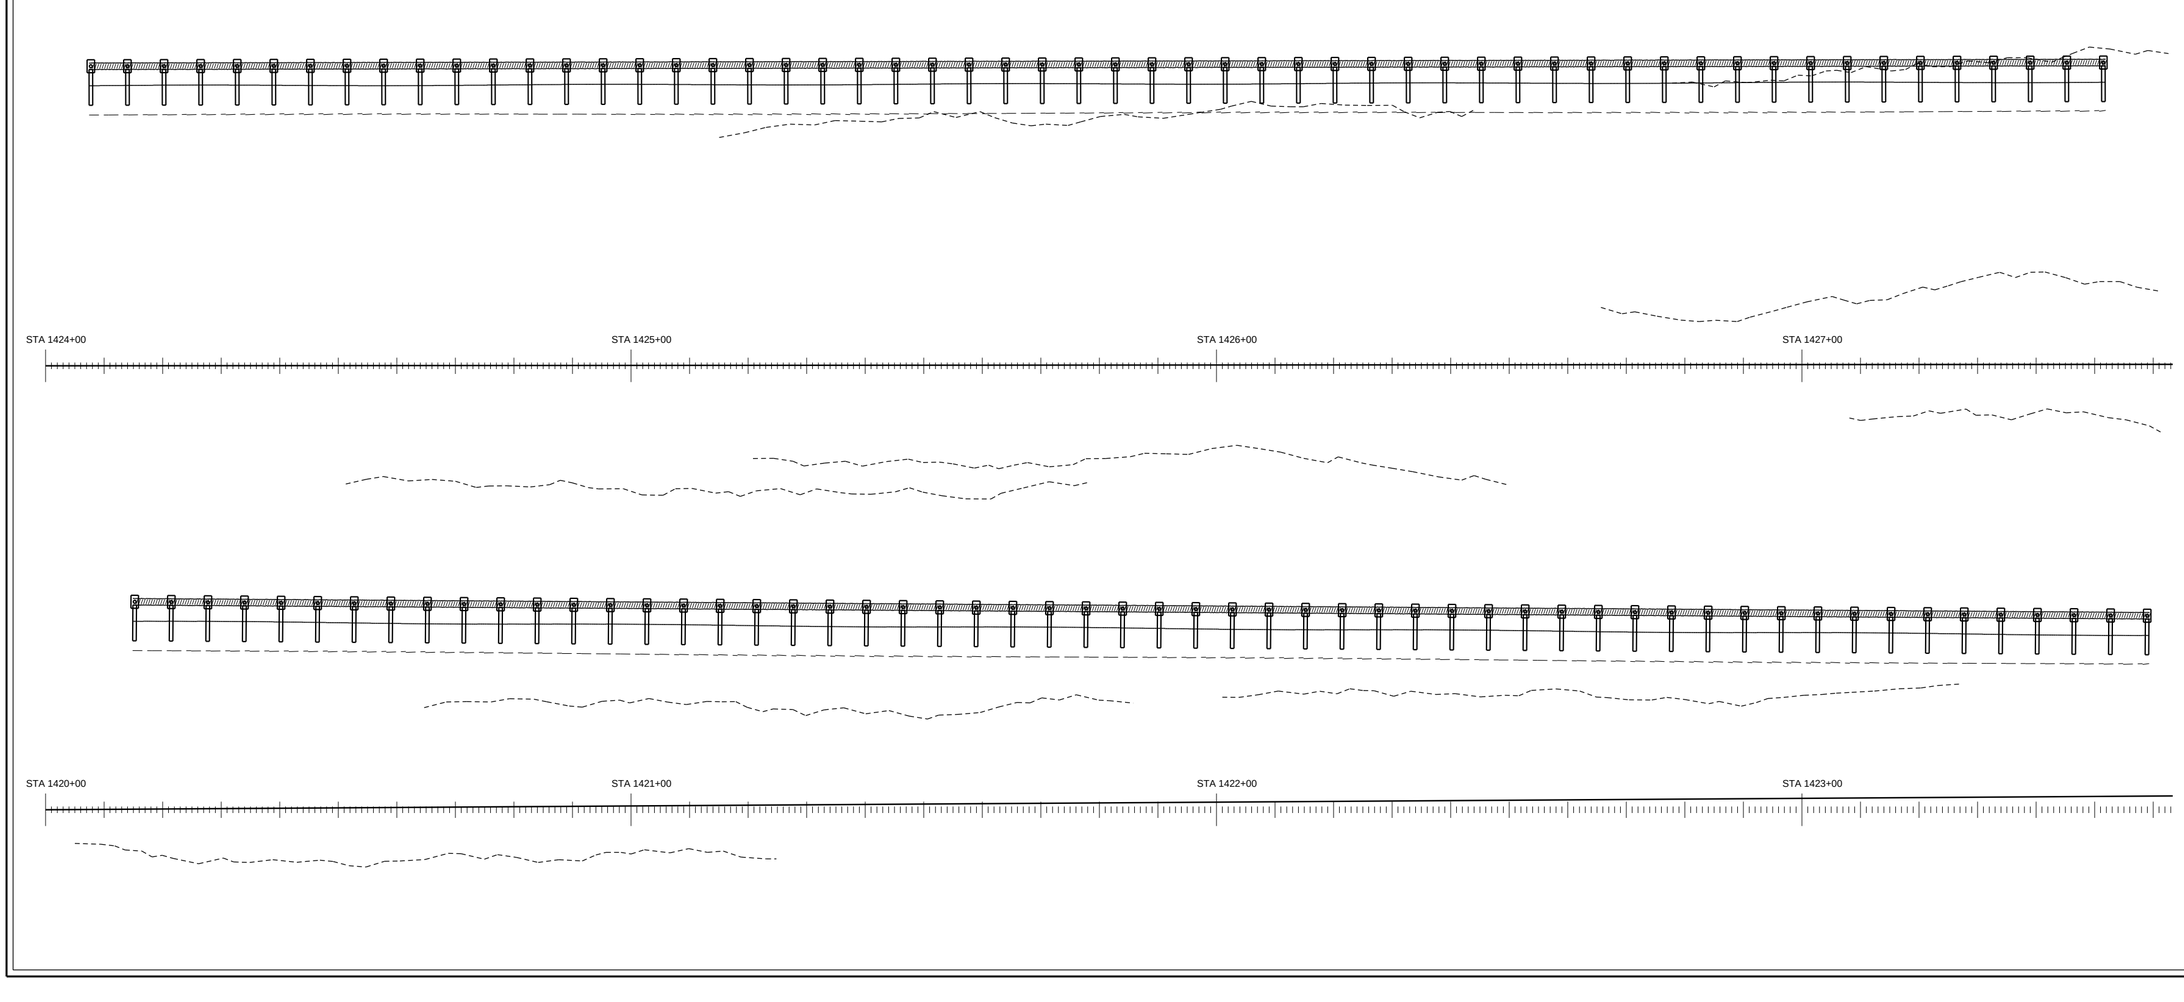











PAY ITEM 536-1-1 GUARDRAIL ROADWAY (TL-3)

PAY ITEM 536-85-24 END TREATMENT

GUARANTEED FENCE CORP

FIN. PROJ. ID 441234-1-52-01

SHEET 89 OF 120

SHEET NO. 189

ROADWAY PLAN SCALE: 1" = 20'

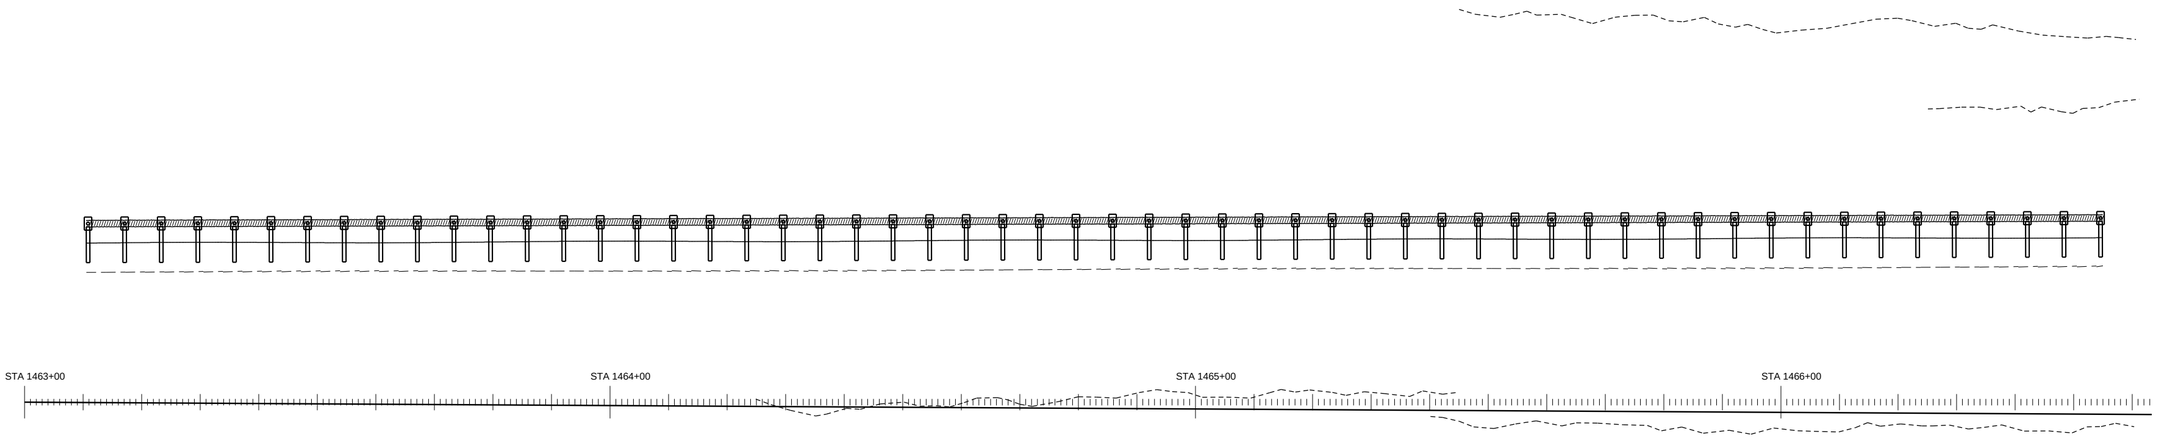


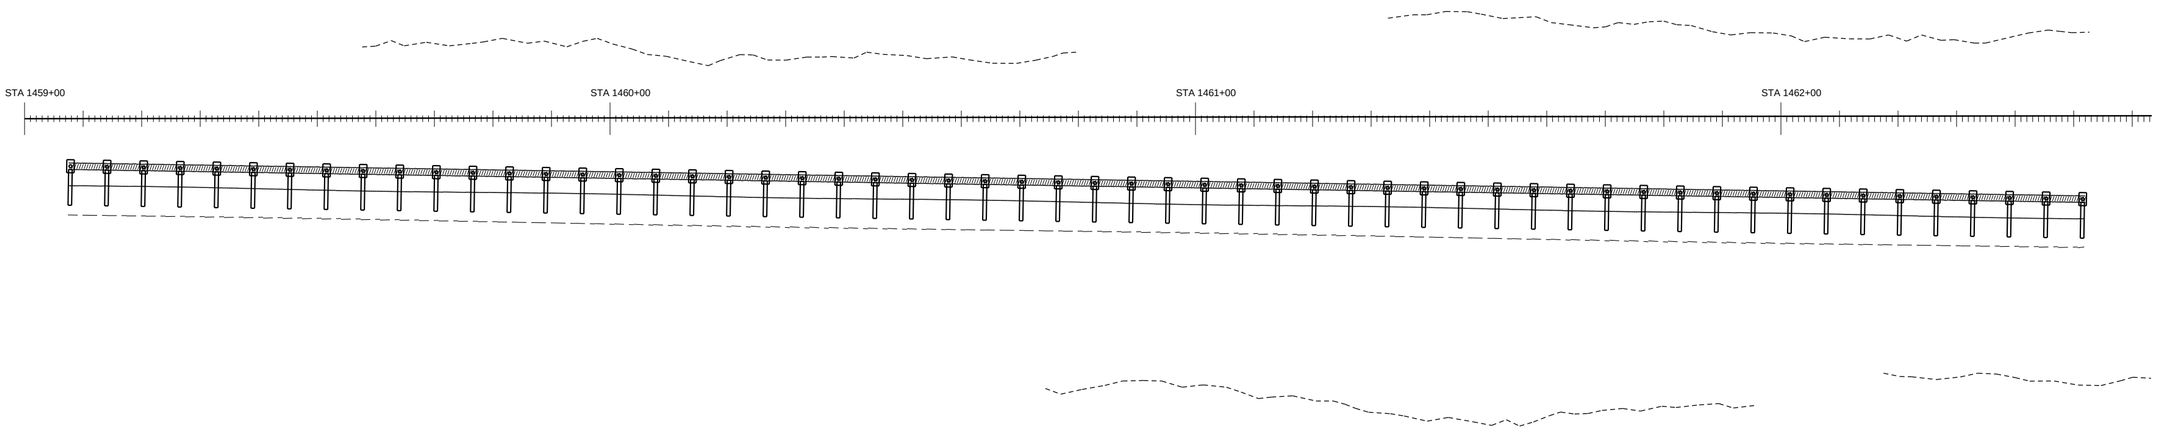


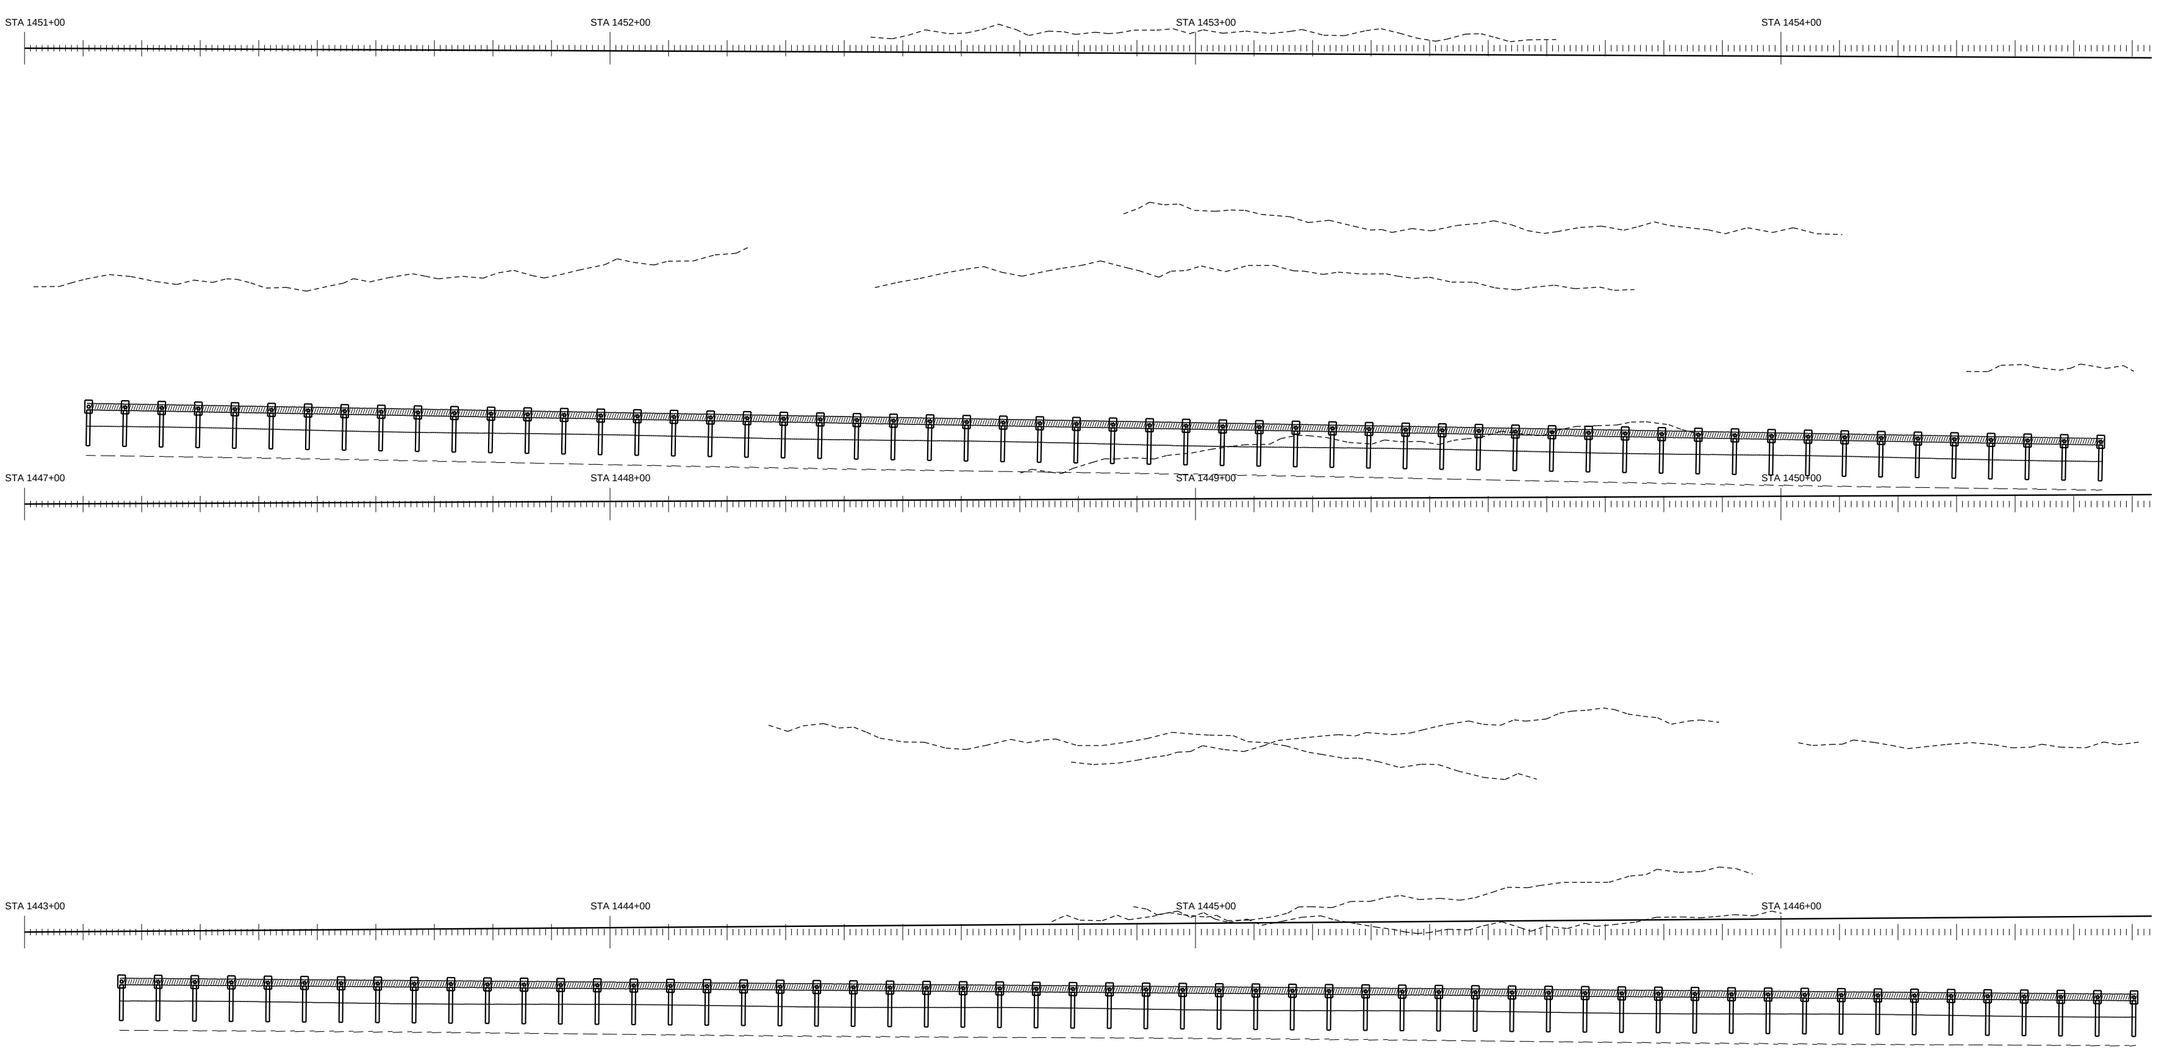


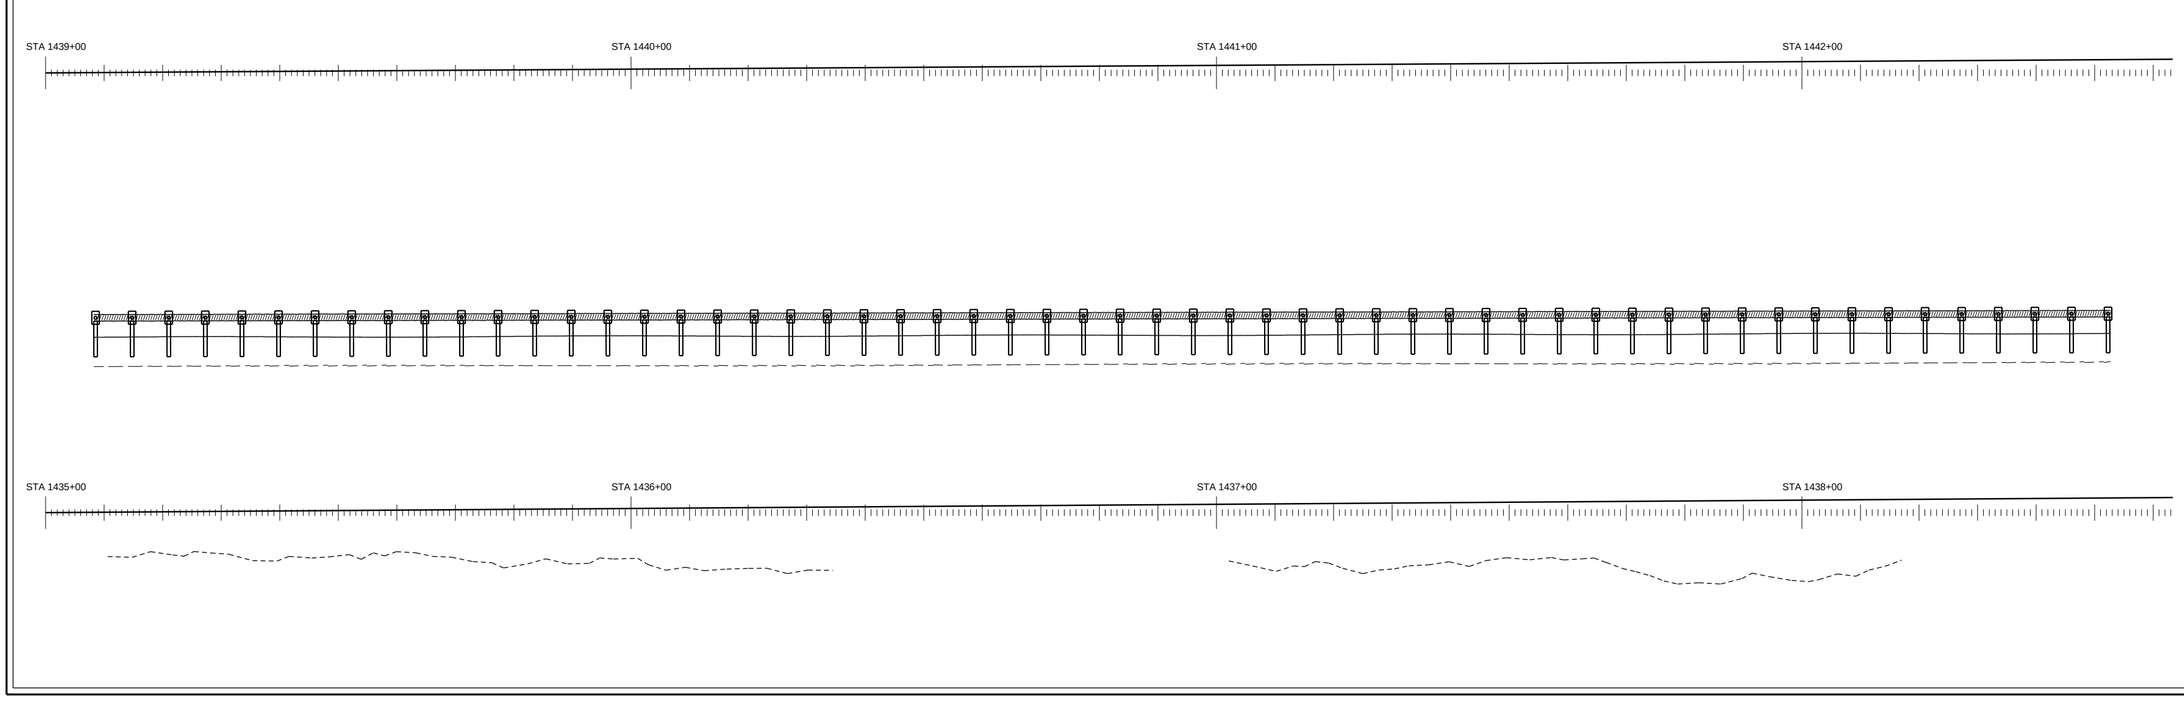


PAY ITEM 536-1-1 GUARDRAIL ROADWAY (TL-3)

PAY ITEM 536-85-24 END TREATMENT

GUARANTEED FENCE CORP

FIN. PROJ. ID 441234-1-52-01

SHEET 90 OF 120

SHEET NO. 190

ROADWAY PLAN SCALE: 1" = 20'

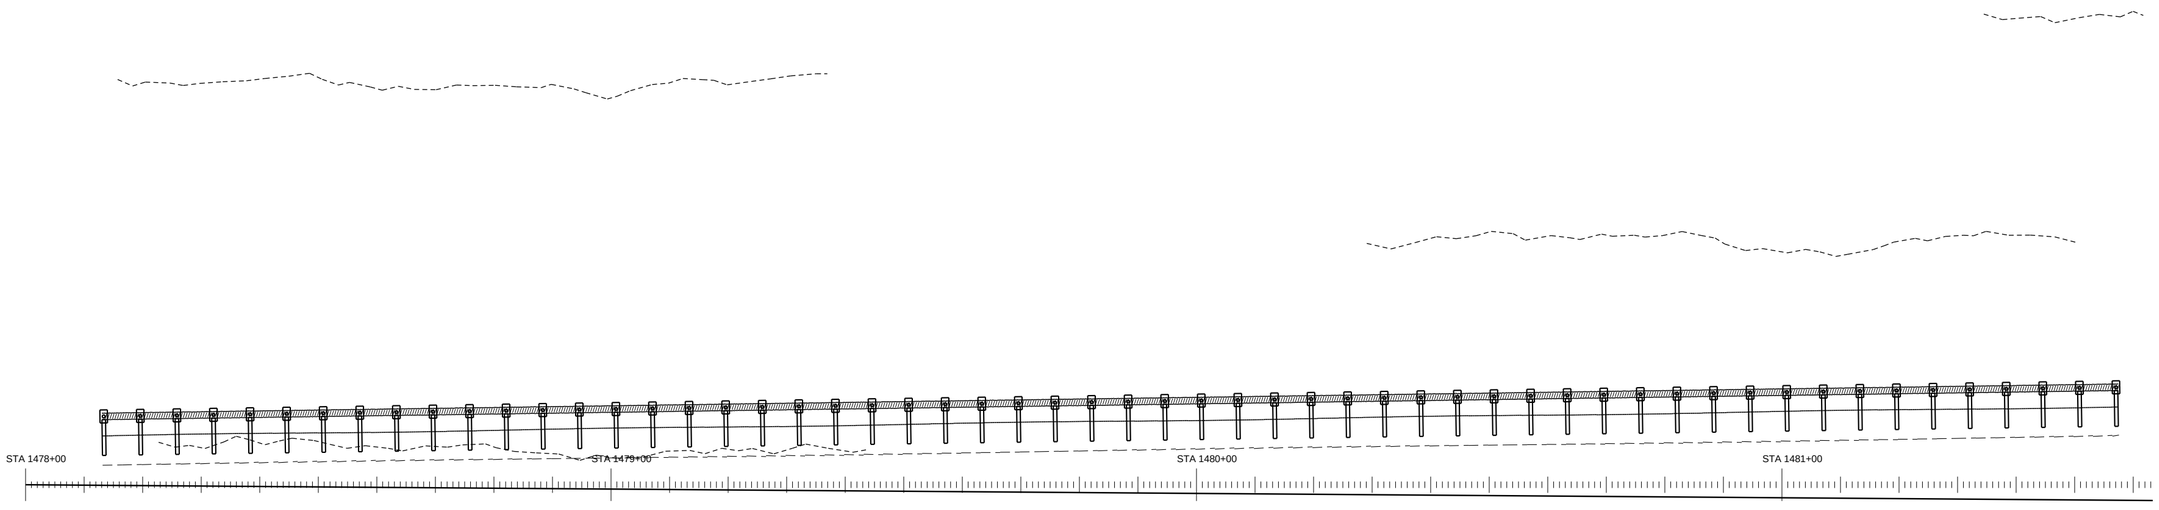


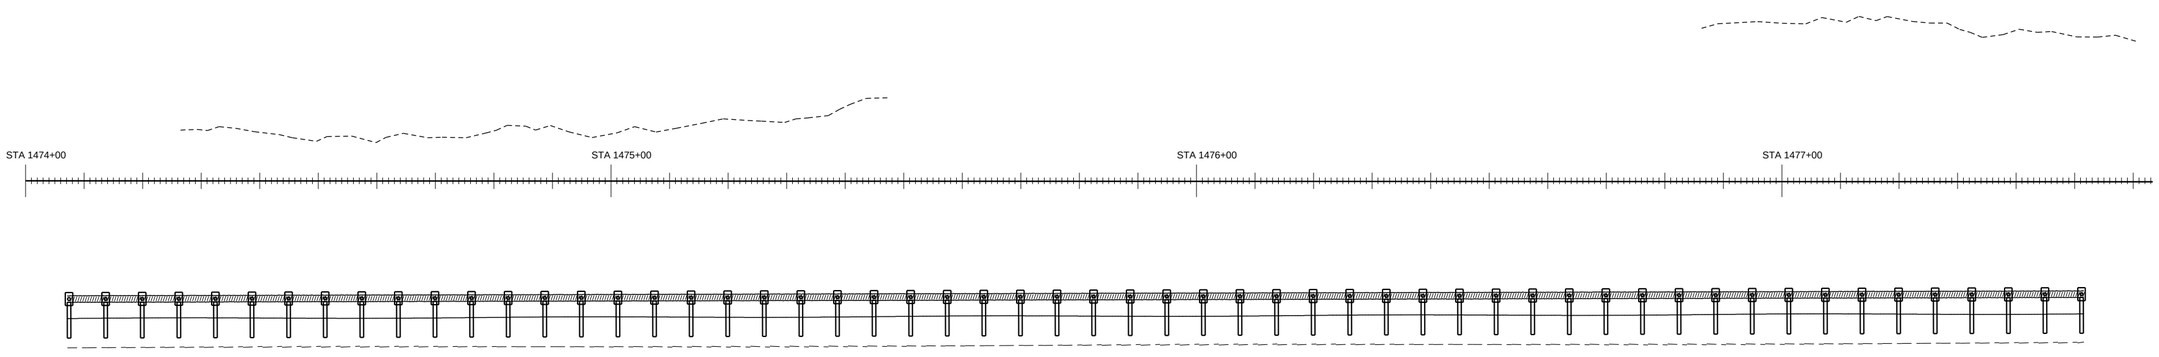


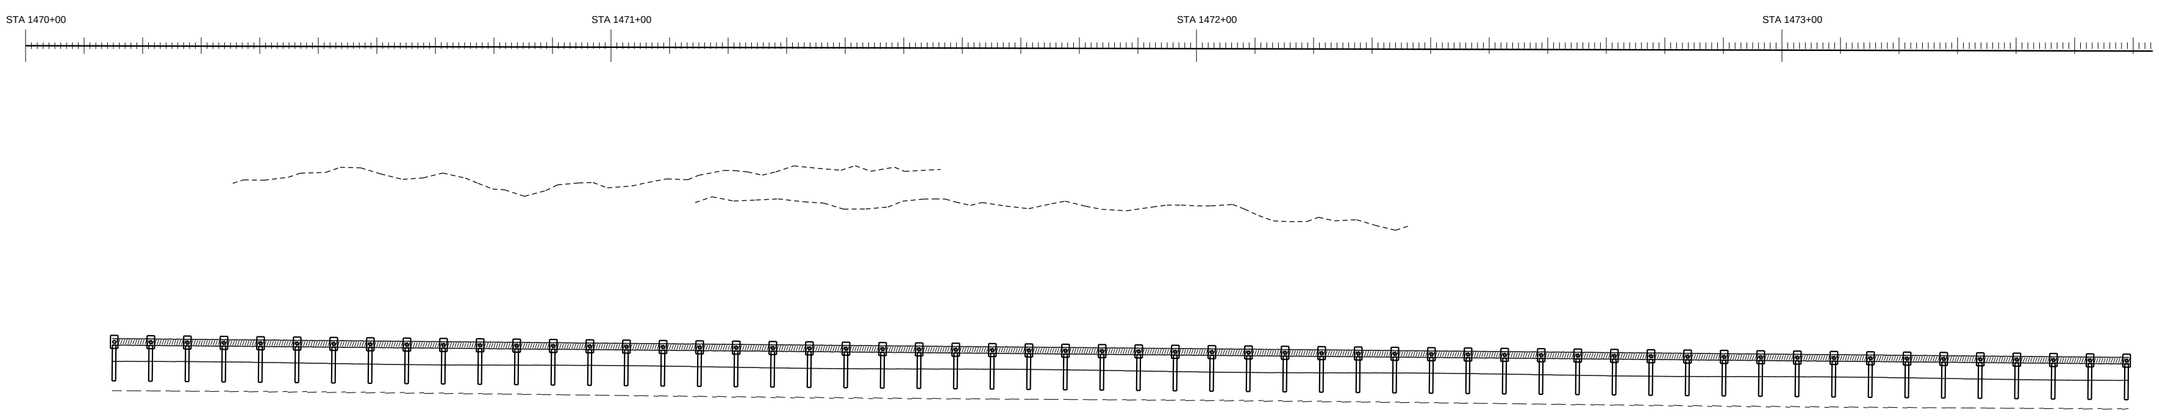


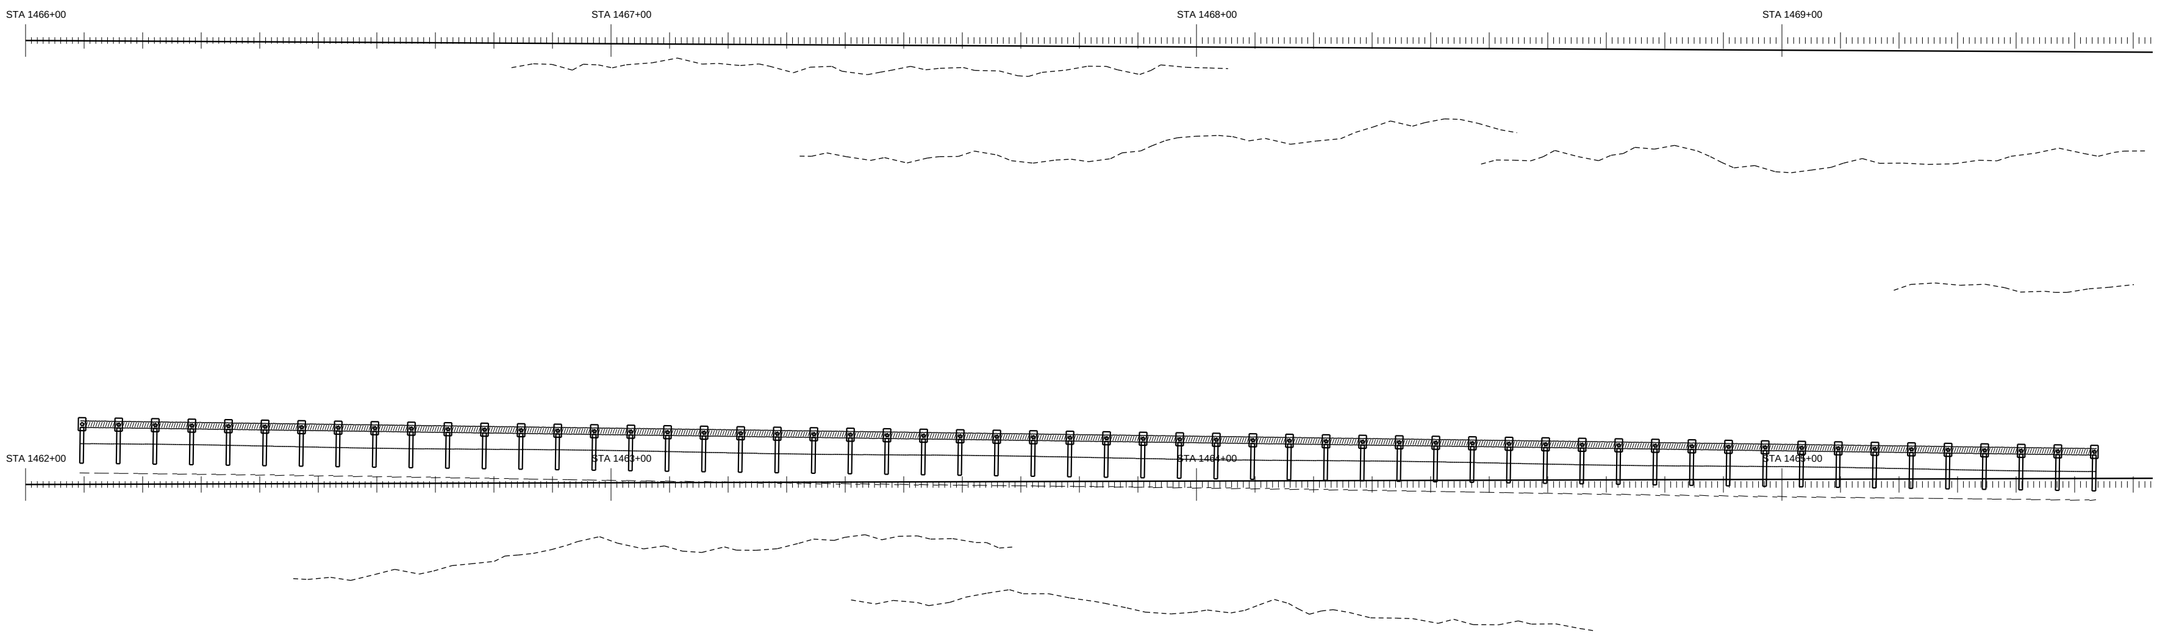





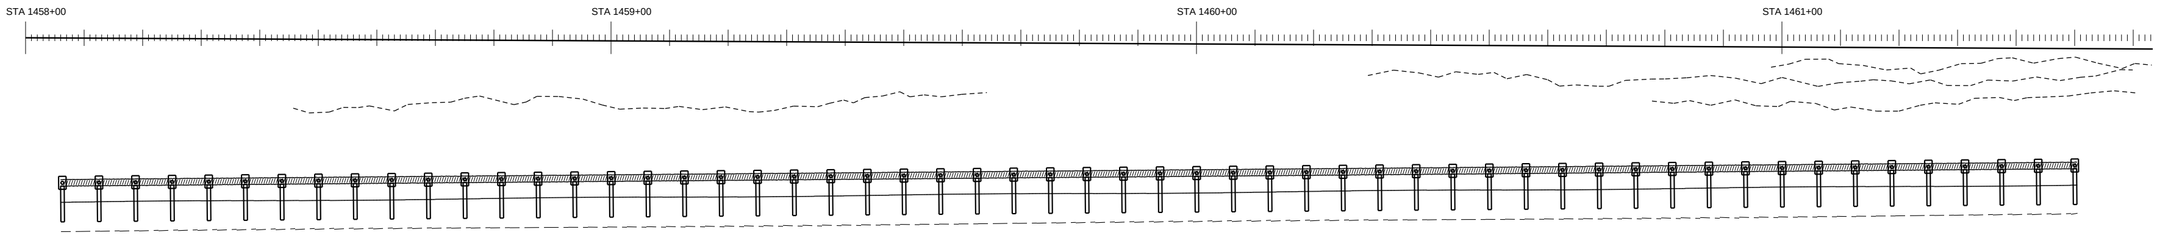


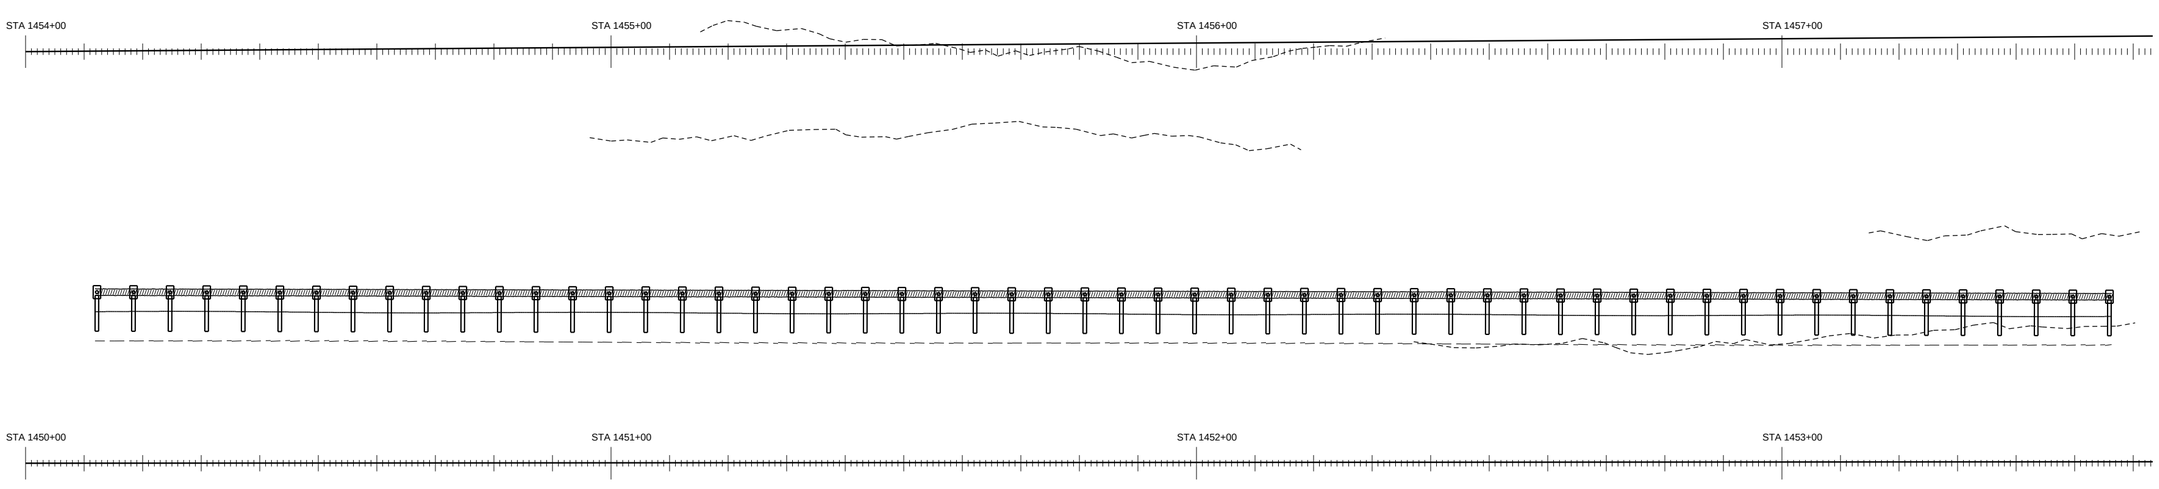





PAY ITEM 536-1-1 GUARDRAIL ROADWAY (TL-3)

PAY ITEM 536-85-24 END TREATMENT

GUARANTEED FENCE CORP

FIN. PROJ. ID 441234-1-52-01

SHEET 91 OF 120

SHEET NO. 191

ROADWAY PLAN SCALE: 1" = 20'

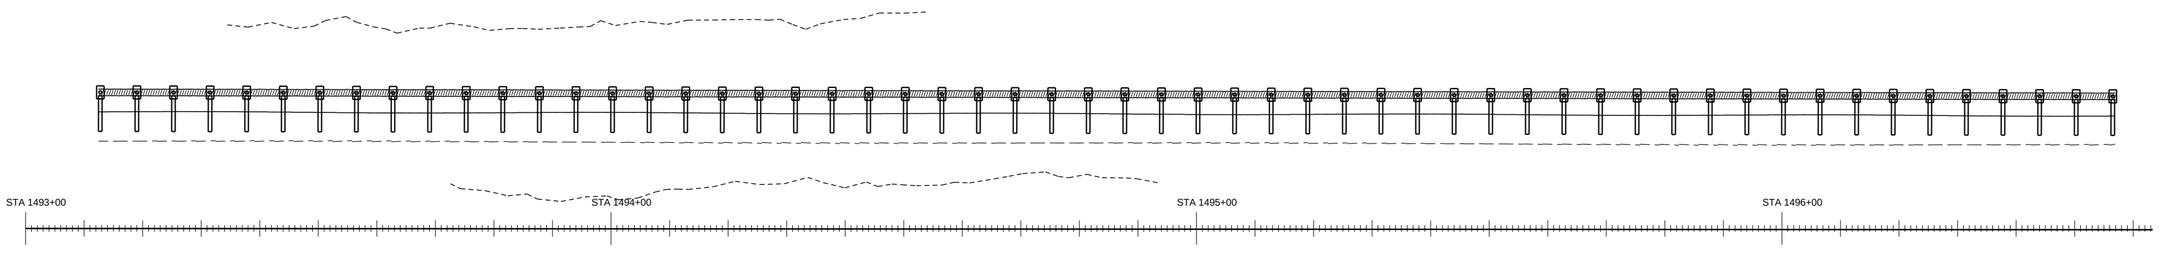


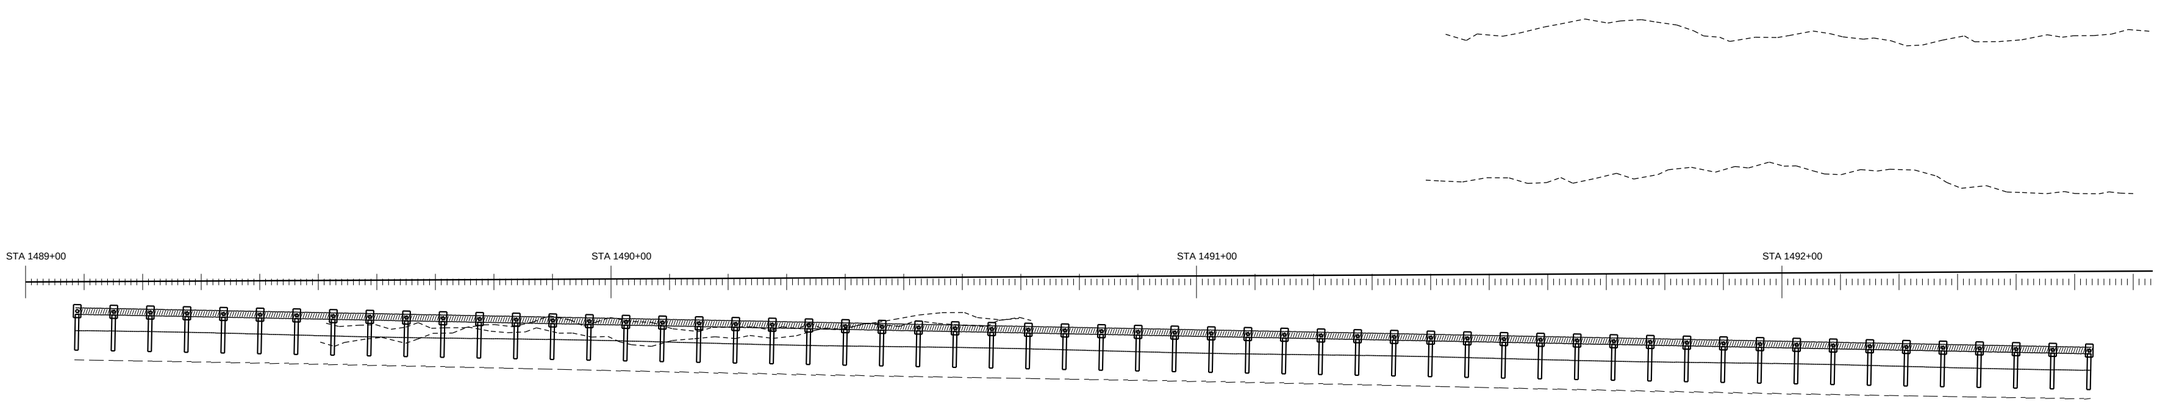


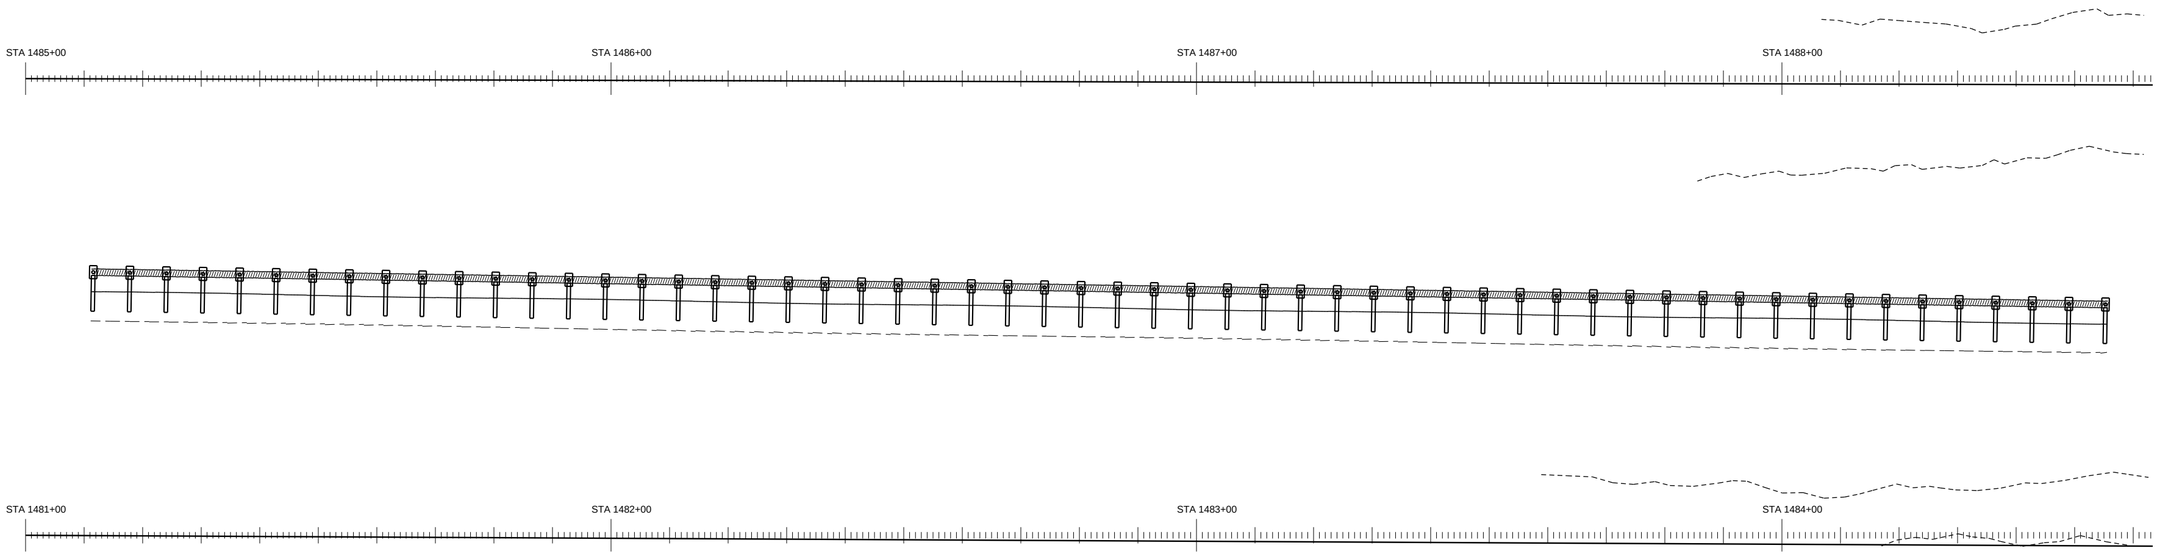


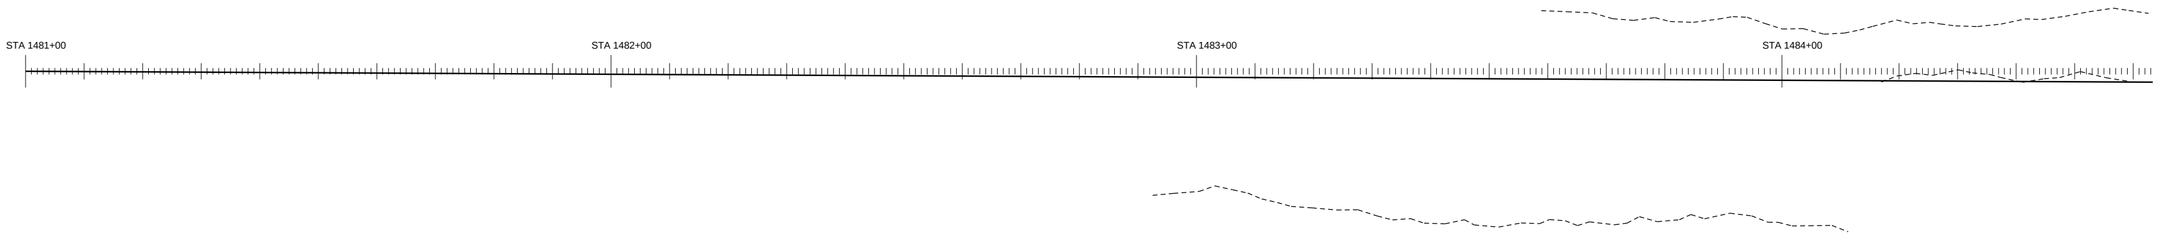


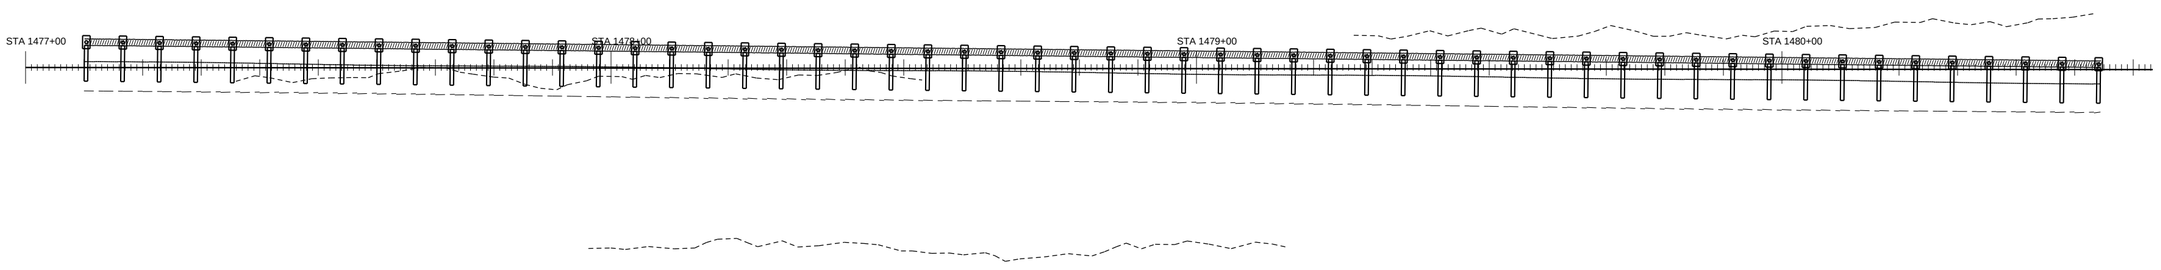


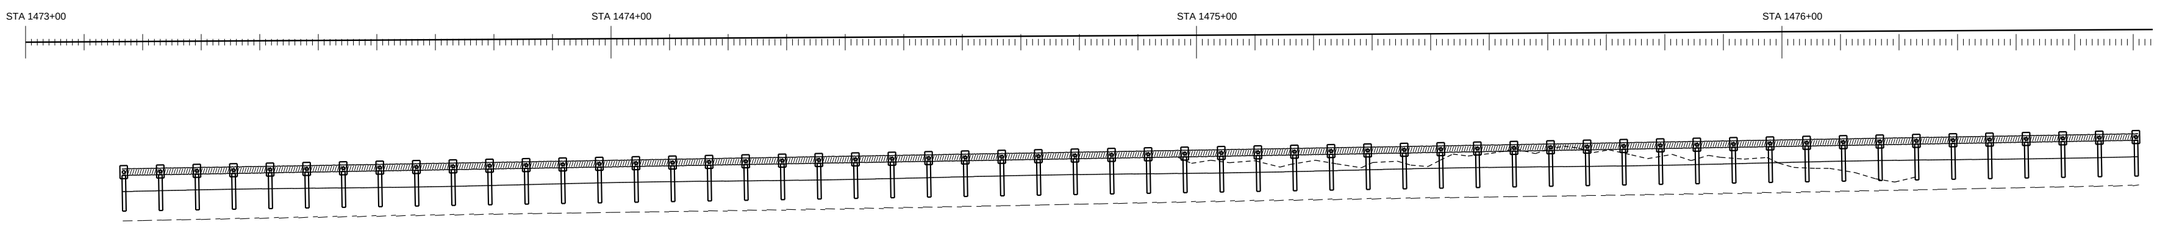


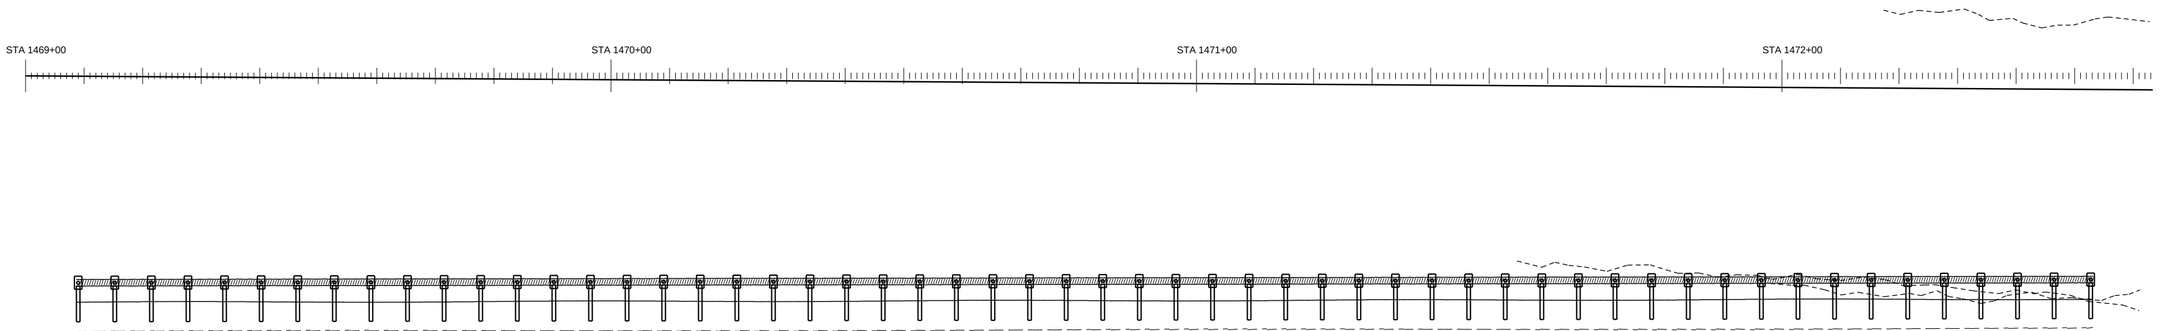


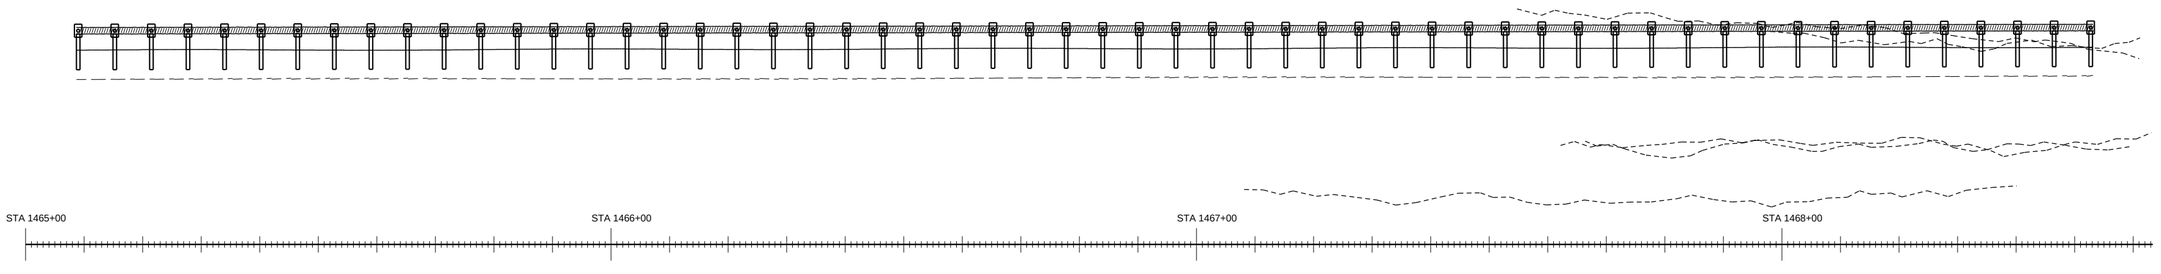


PAY ITEM 536-1-1 GUARDRAIL ROADWAY (TL-3)

PAY ITEM 536-85-24 END TREATMENT

GUARANTEED FENCE CORP

FIN. PROJ. ID 441234-1-52-01

SHEET 92 OF 120

SHEET NO. 192

ROADWAY PLAN SCALE: 1" = 20'

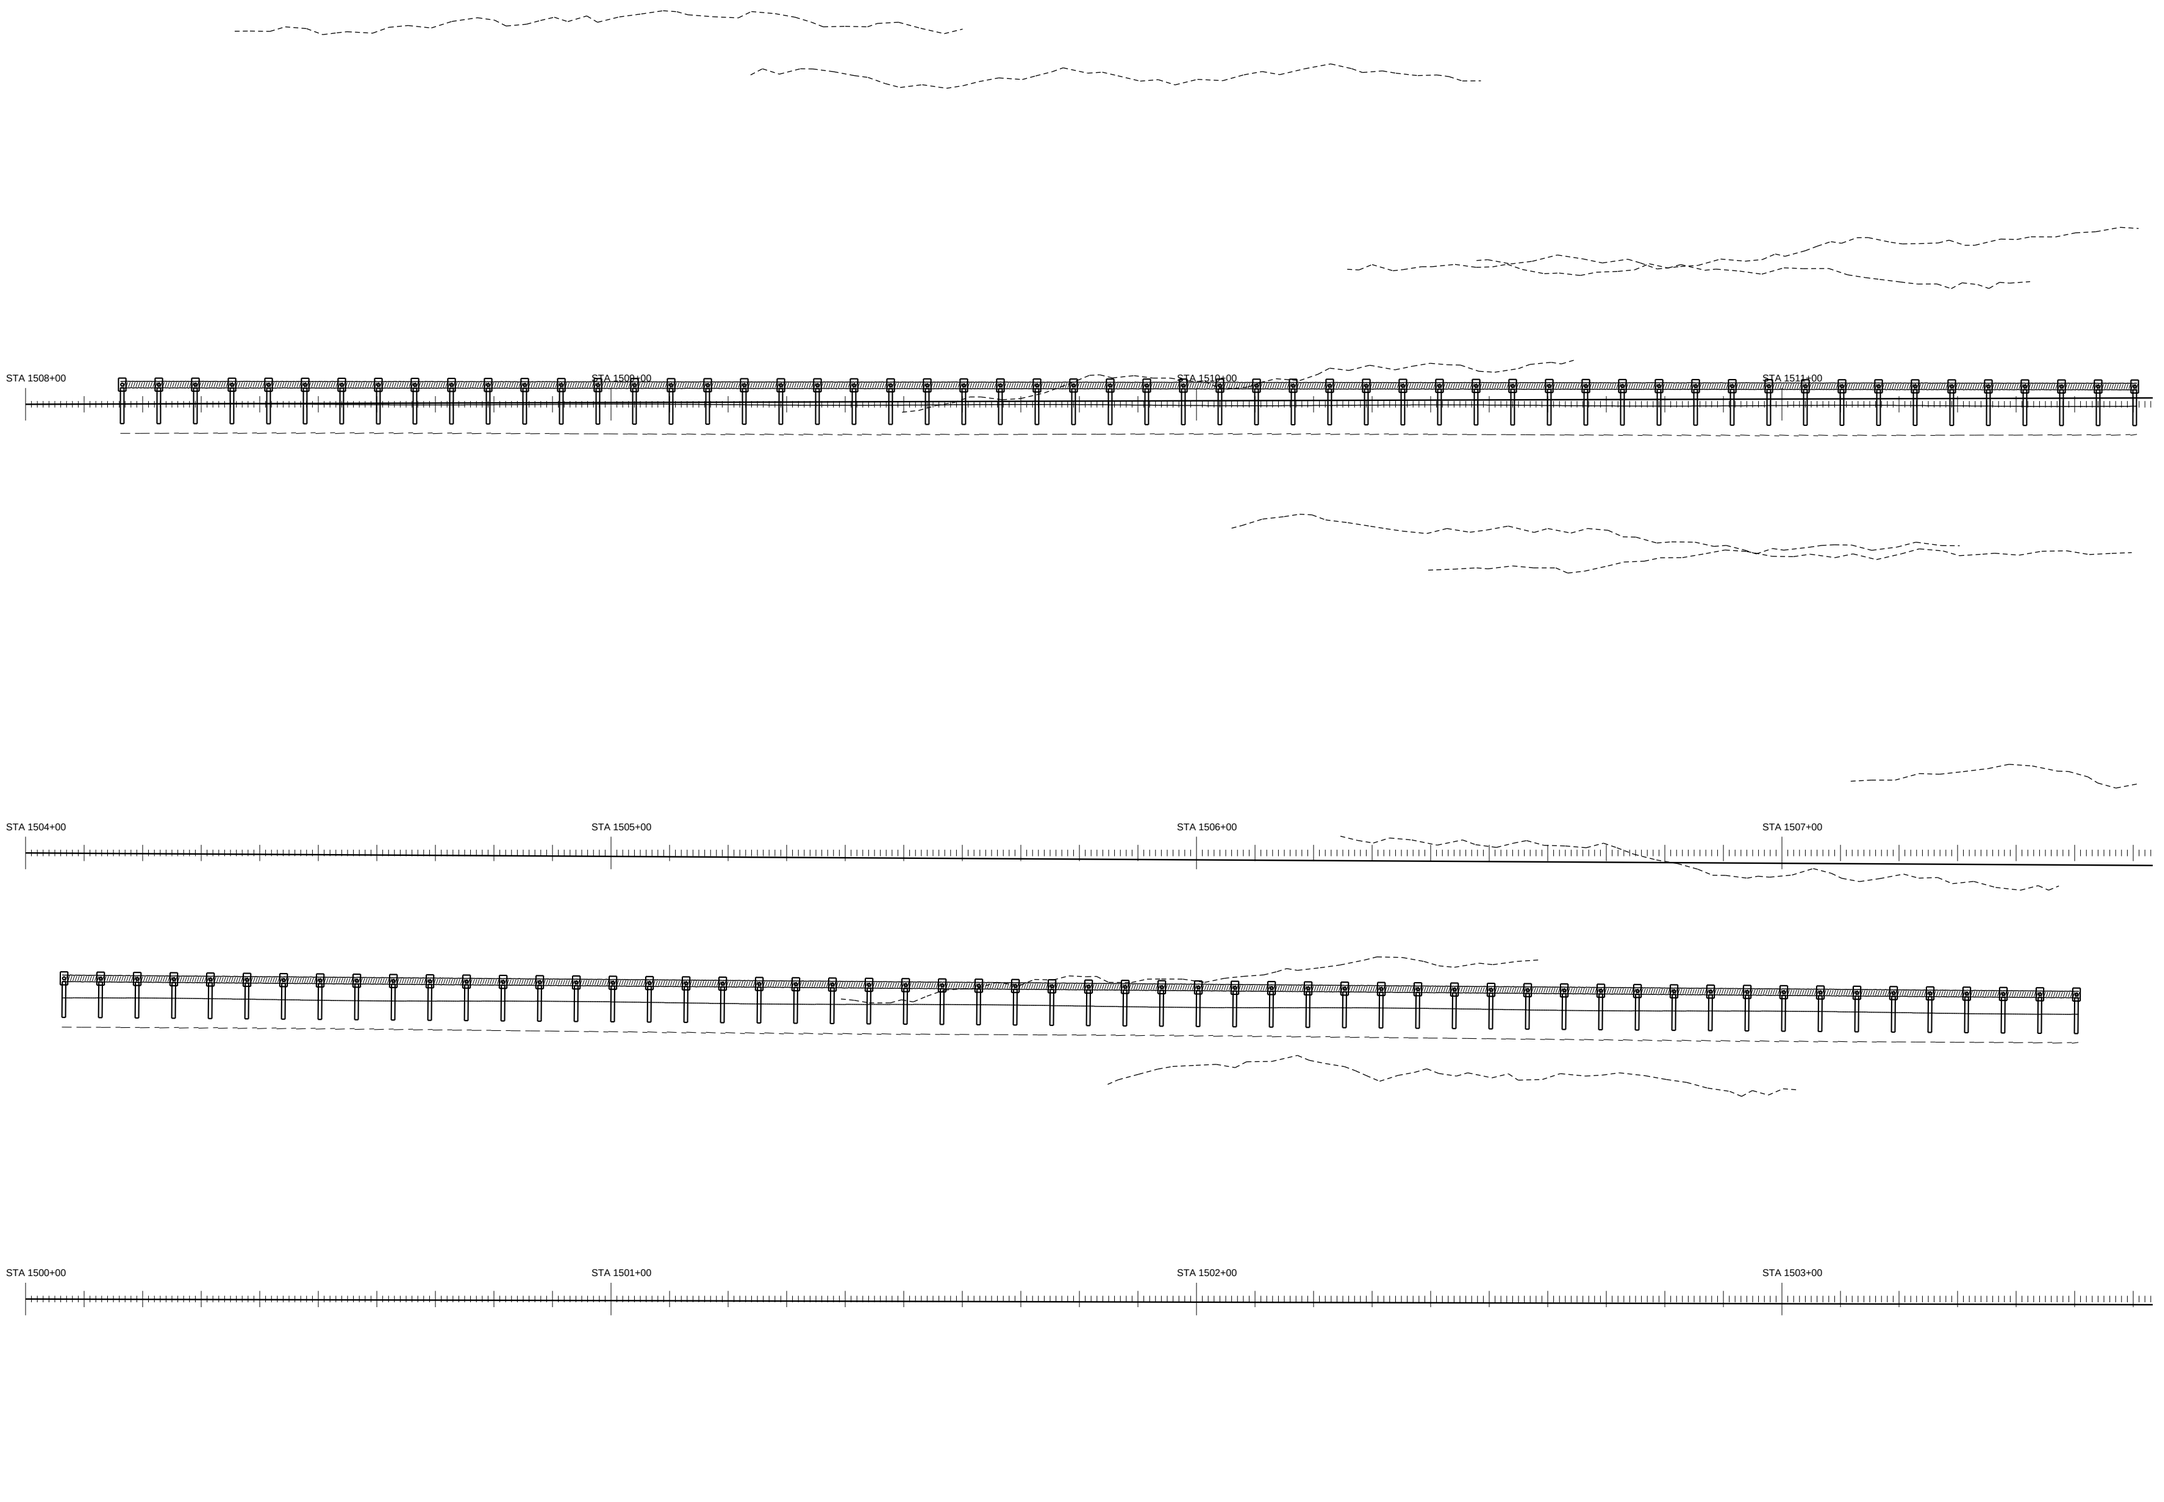


PAY ITEM 536-1-1 GUARDRAIL ROADWAY (TL-3)

PAY ITEM 536-85-24 END TREATMENT

GUARANTEED FENCE CORP

FIN. PROJ. ID 441234-1-52-01

SHEET 93 OF 120

SHEET NO. 193

ROADWAY PLAN SCALE: 1" = 20'

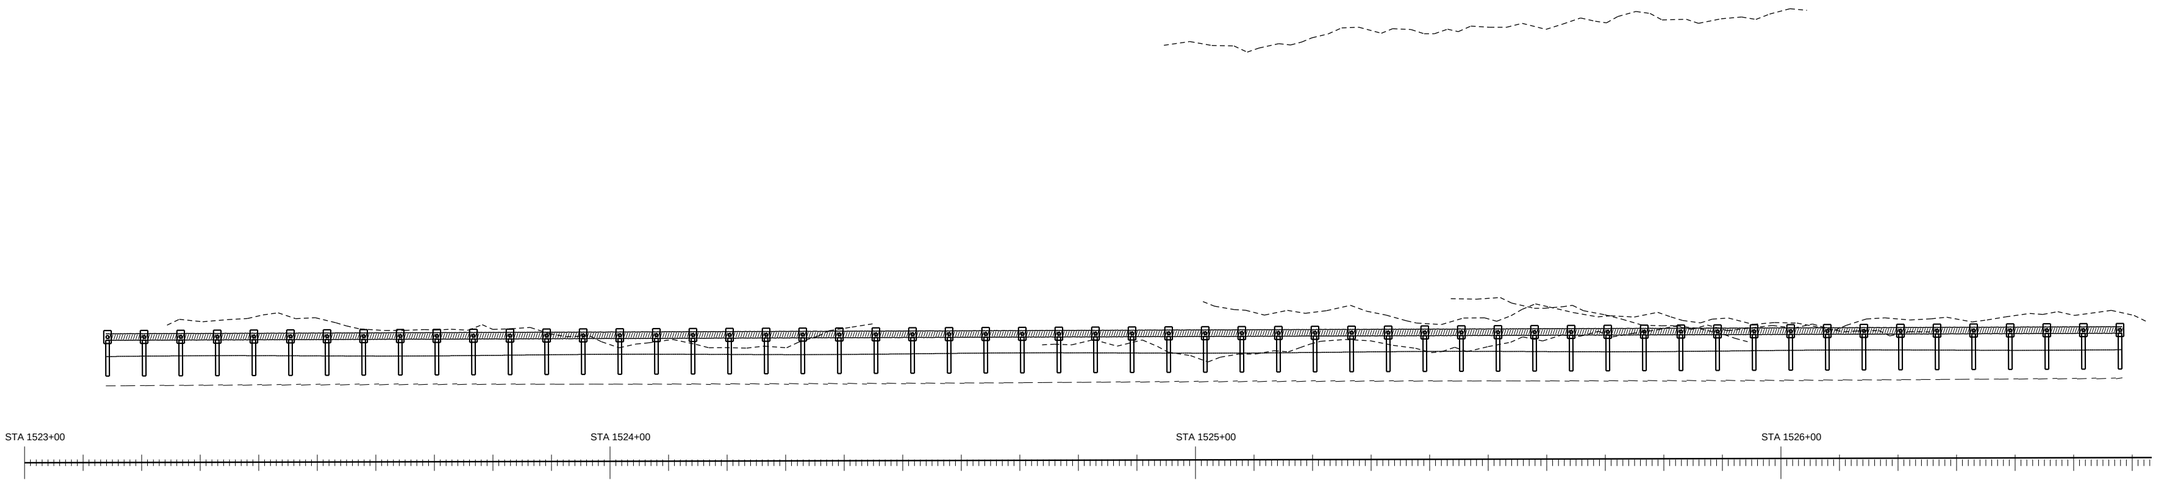


PAY ITEM 536-1-1 GUARDRAIL ROADWAY (TL-3)

PAY ITEM 536-85-24 END TREATMENT

GUARANTEED FENCE CORP

FIN. PROJ. ID 441234-1-52-01

SHEET 94 OF 120

SHEET NO. 194

ROADWAY PLAN SCALE: 1" = 20'

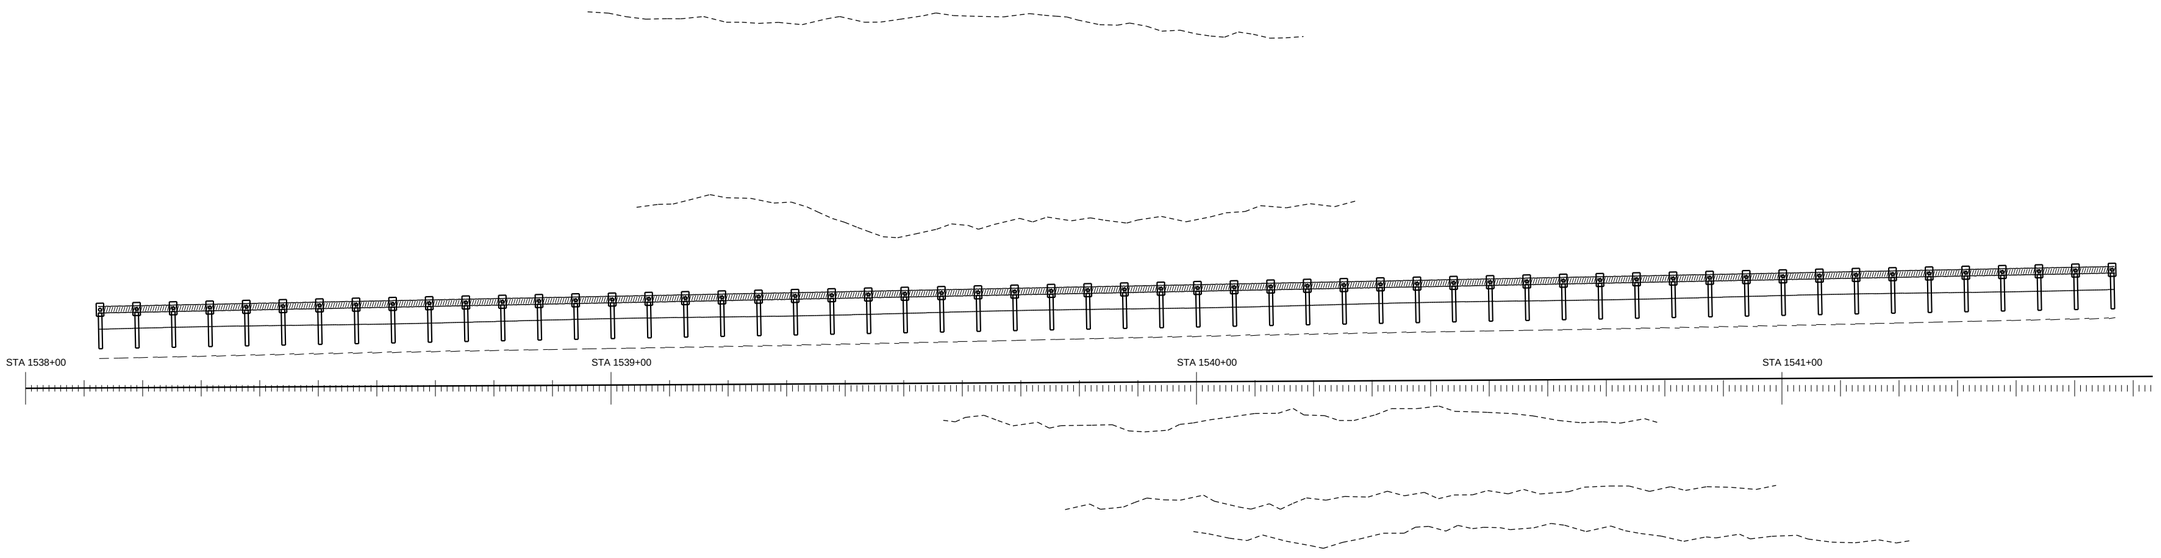


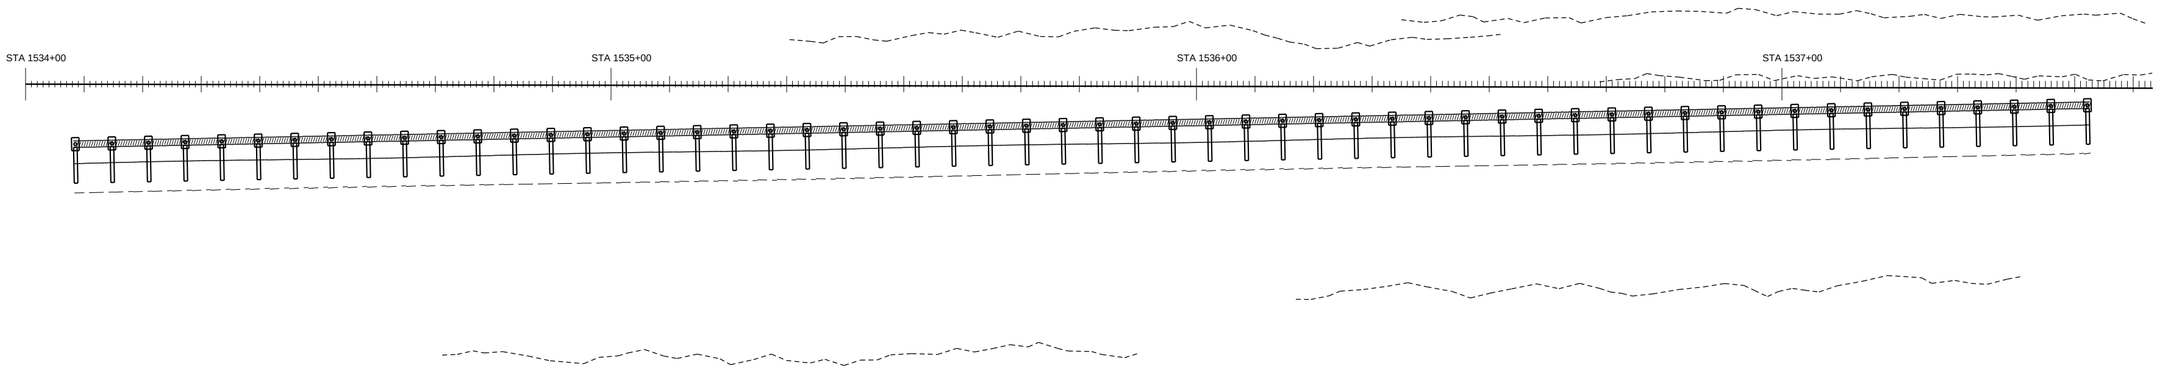


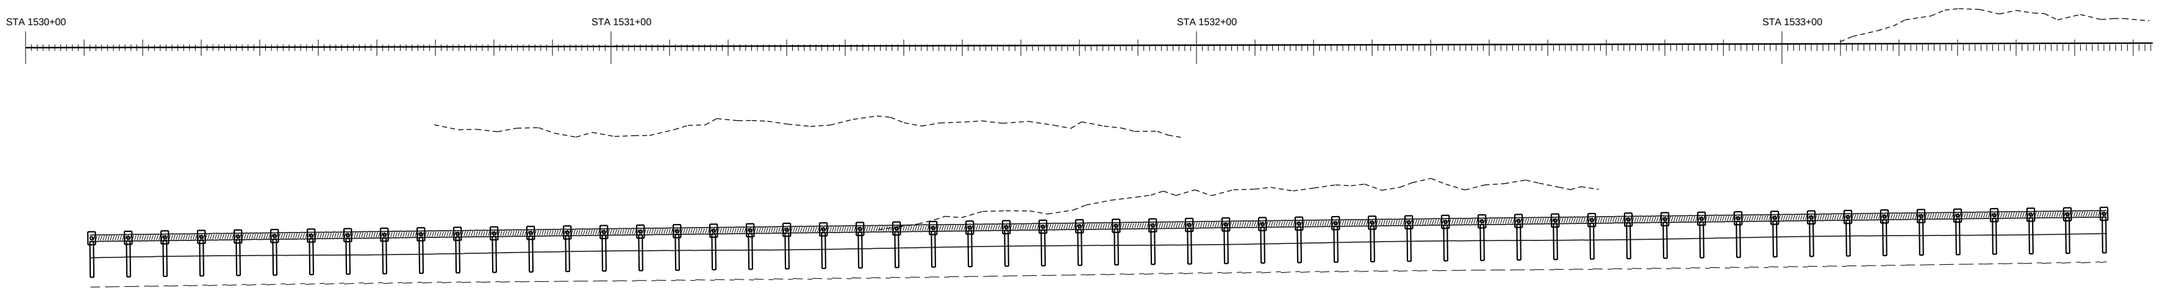


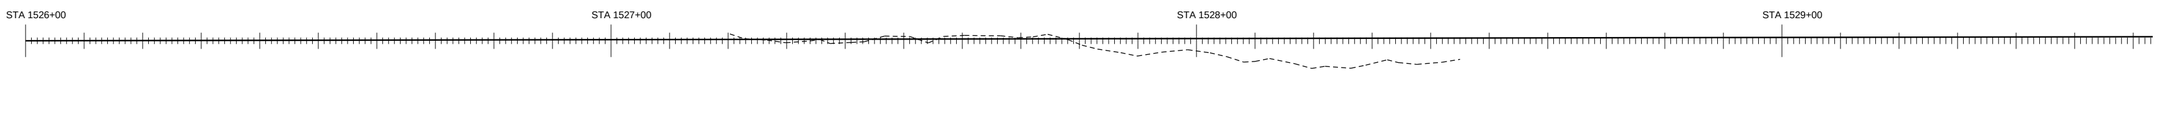


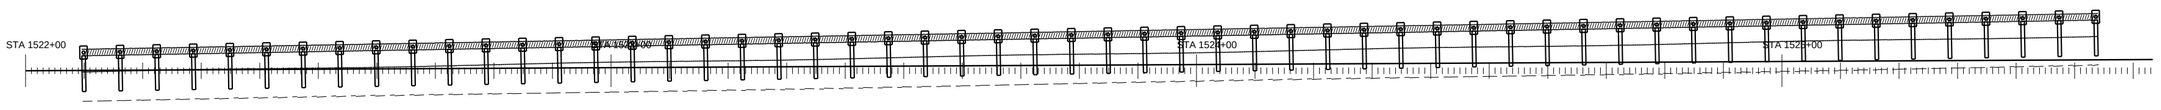


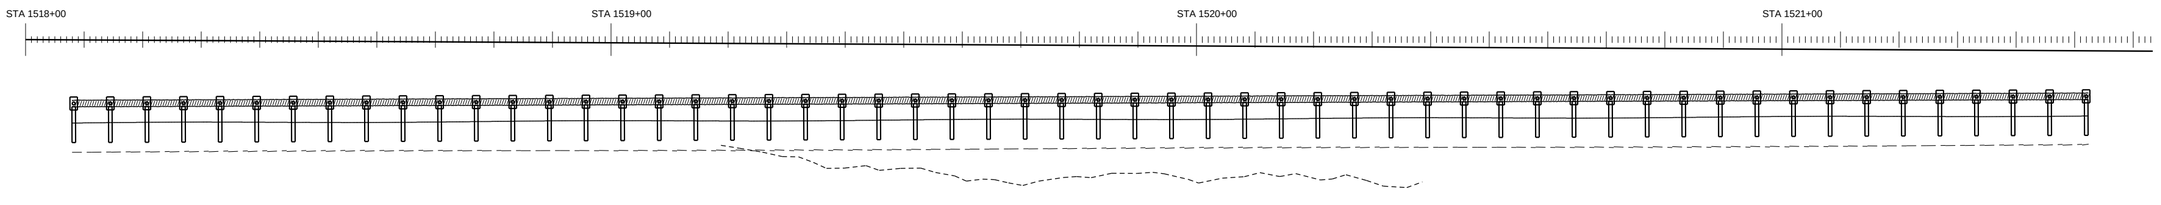

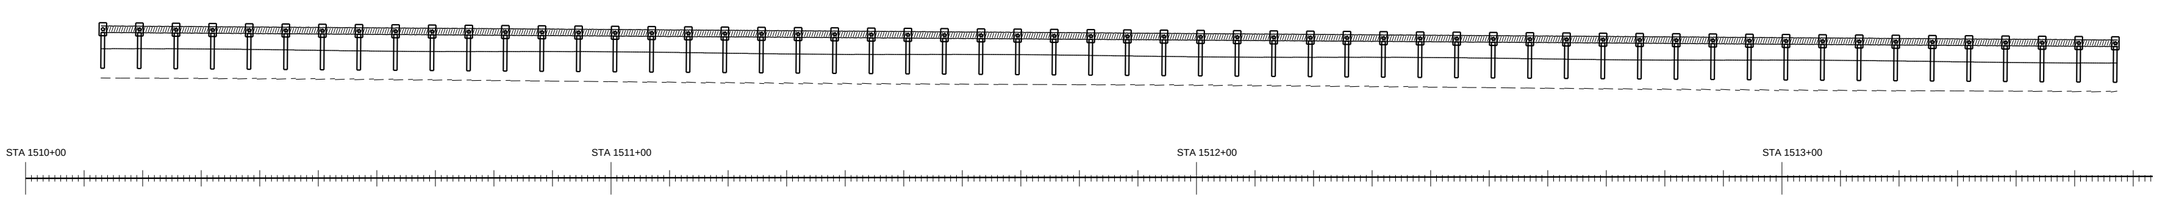


PAY ITEM 536-1-1 GUARDRAIL ROADWAY (TL-3)

PAY ITEM 536-85-24 END TREATMENT

GUARANTEED FENCE CORP

FIN. PROJ. ID 441234-1-52-01

SHEET 95 OF 120

SHEET NO. 195

ROADWAY PLAN SCALE: 1" = 20'

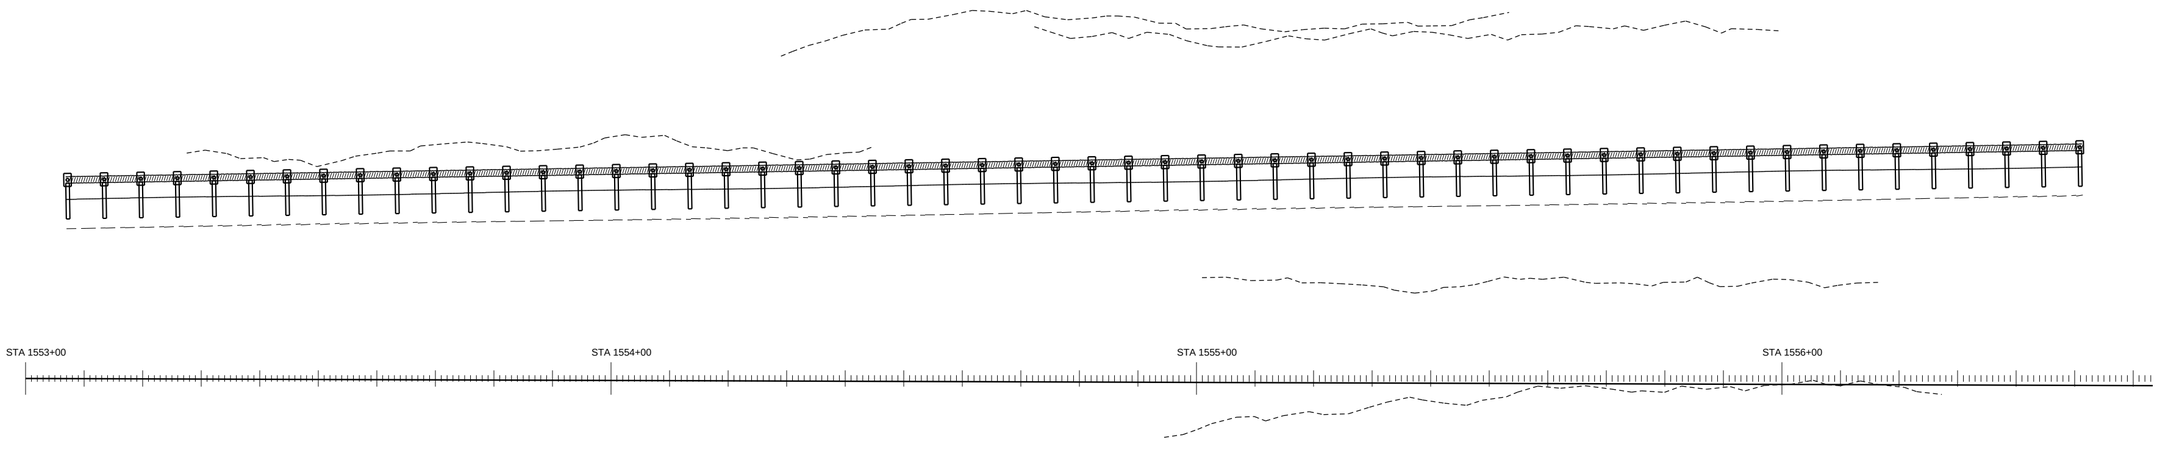


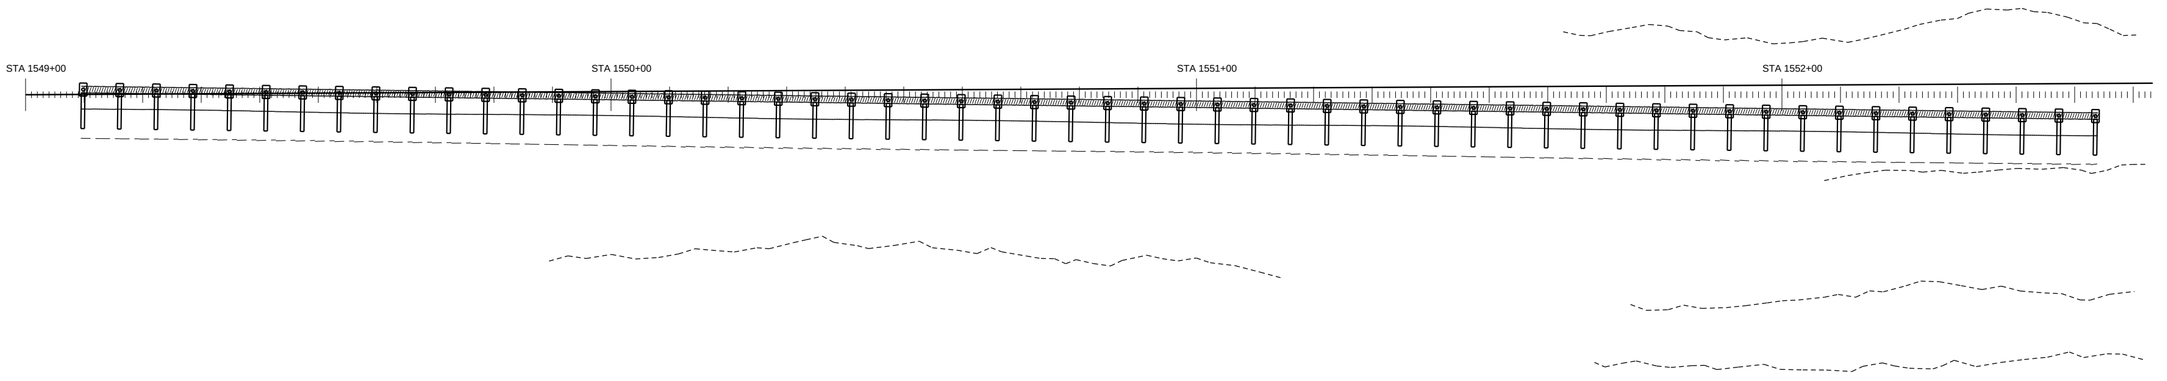


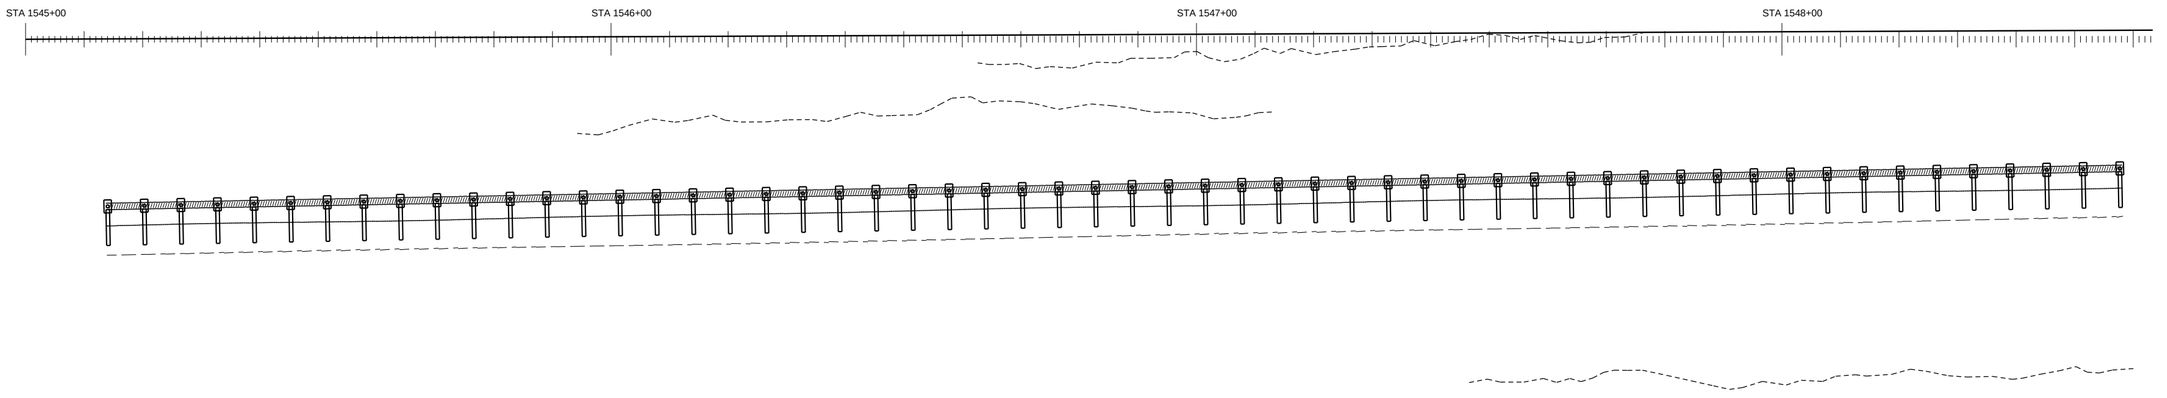


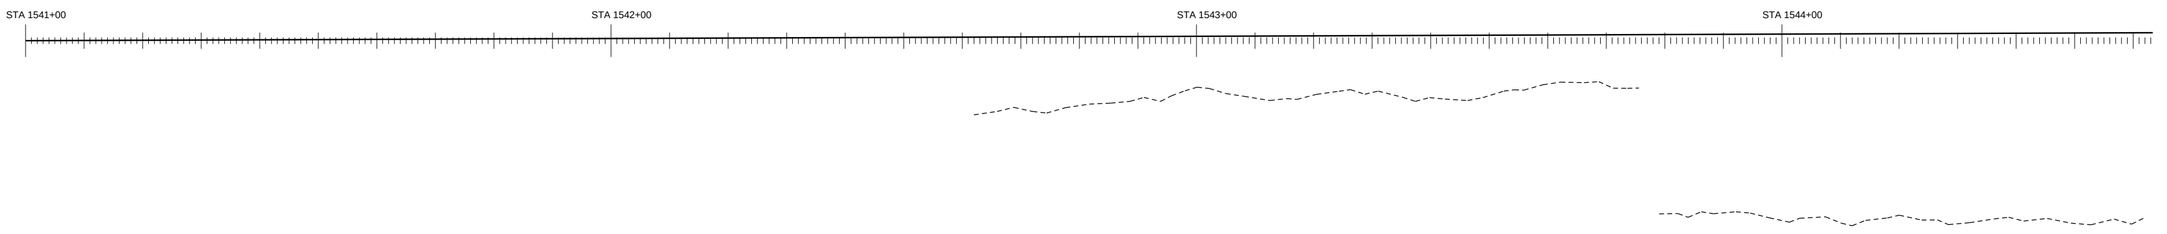


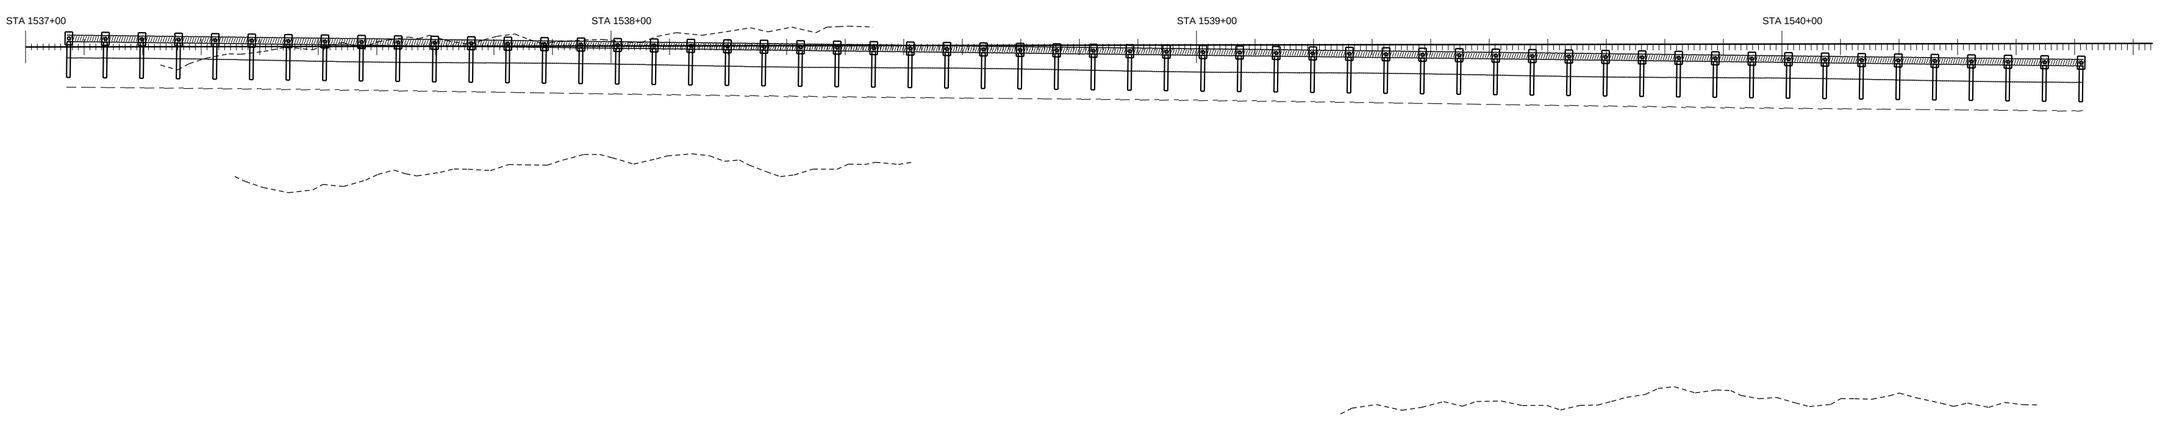


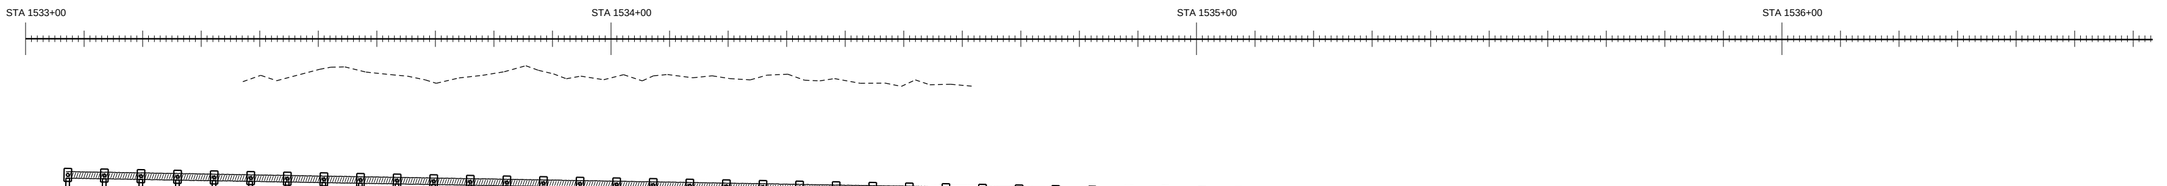


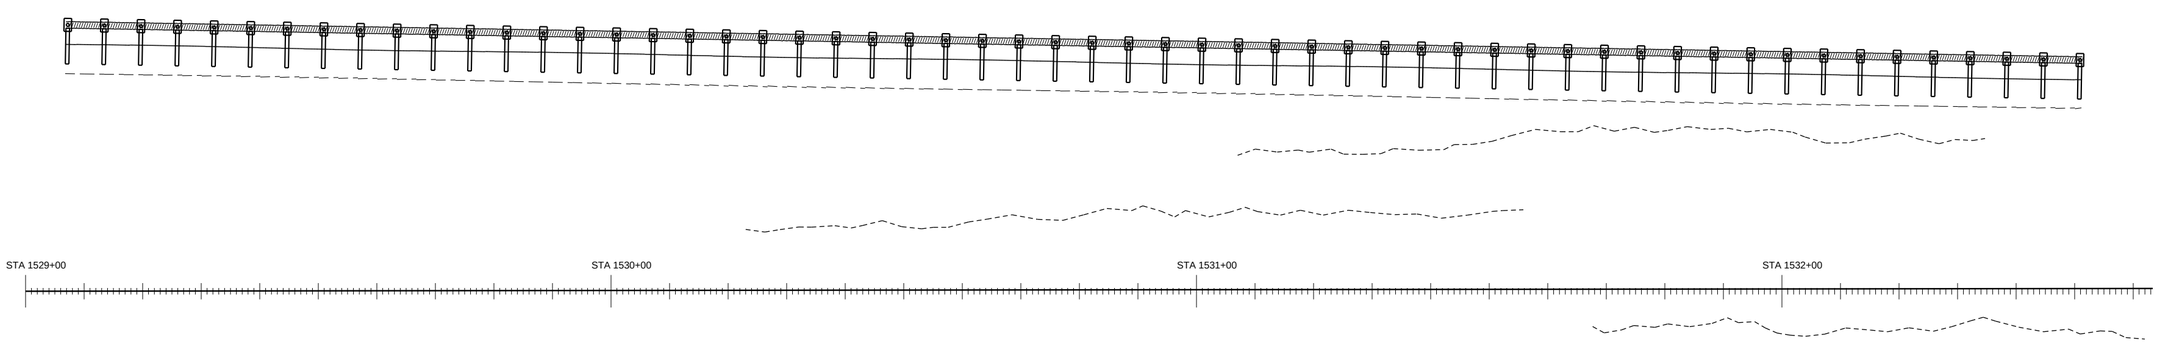


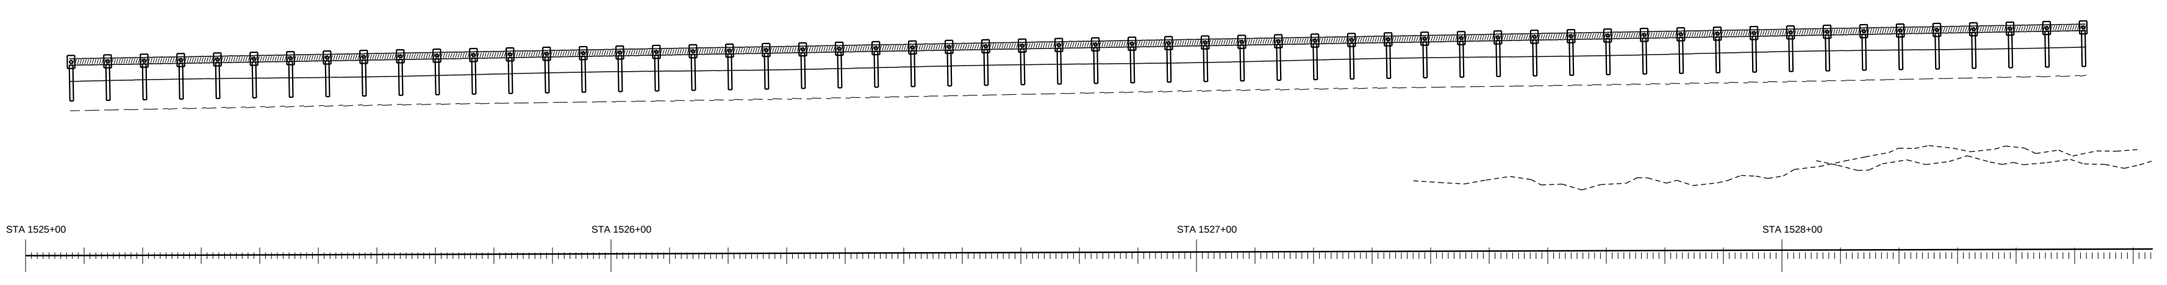


PAY ITEM 536-1-1 GUARDRAIL ROADWAY (TL-3)

PAY ITEM 536-85-24 END TREATMENT

GUARANTEED FENCE CORP

FIN. PROJ. ID 441234-1-52-01

SHEET 96 OF 120

SHEET NO. 196

ROADWAY PLAN SCALE: 1" = 20'

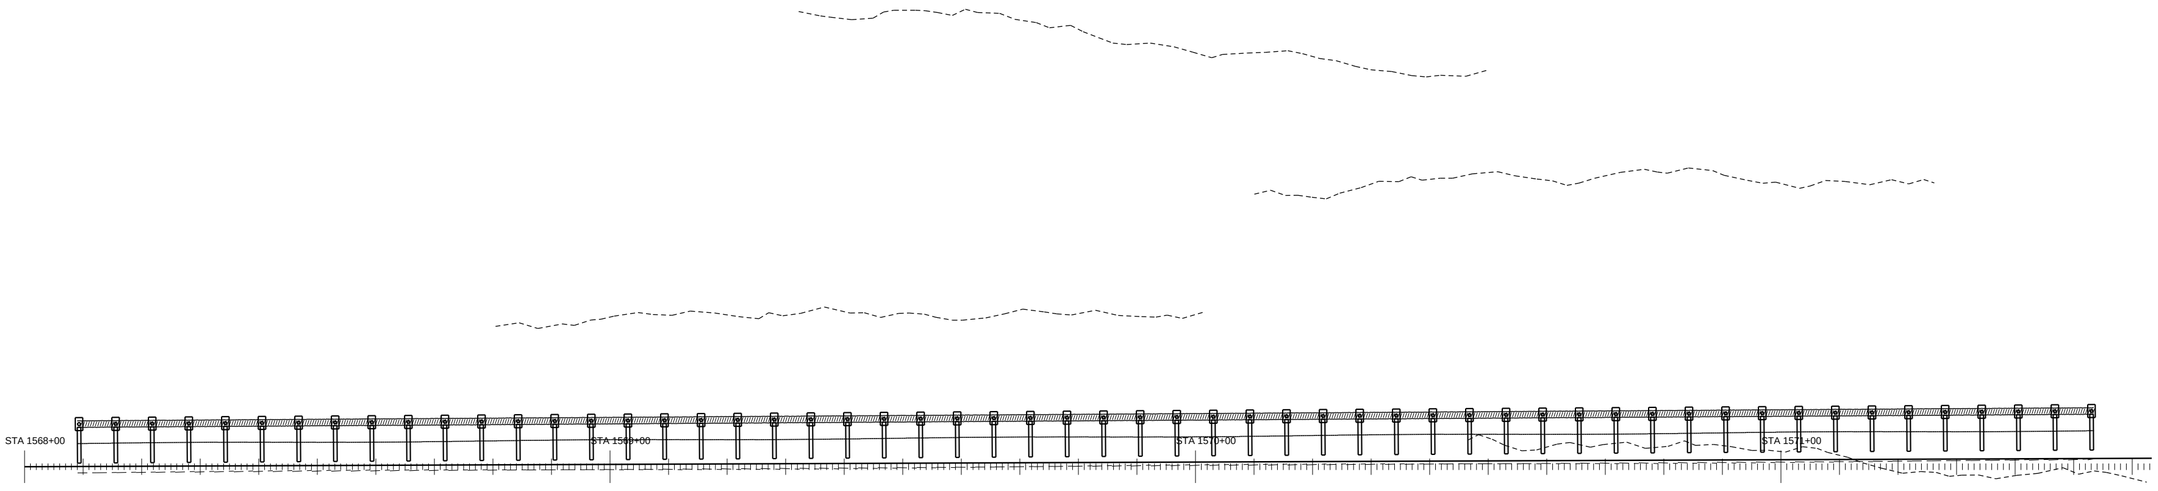


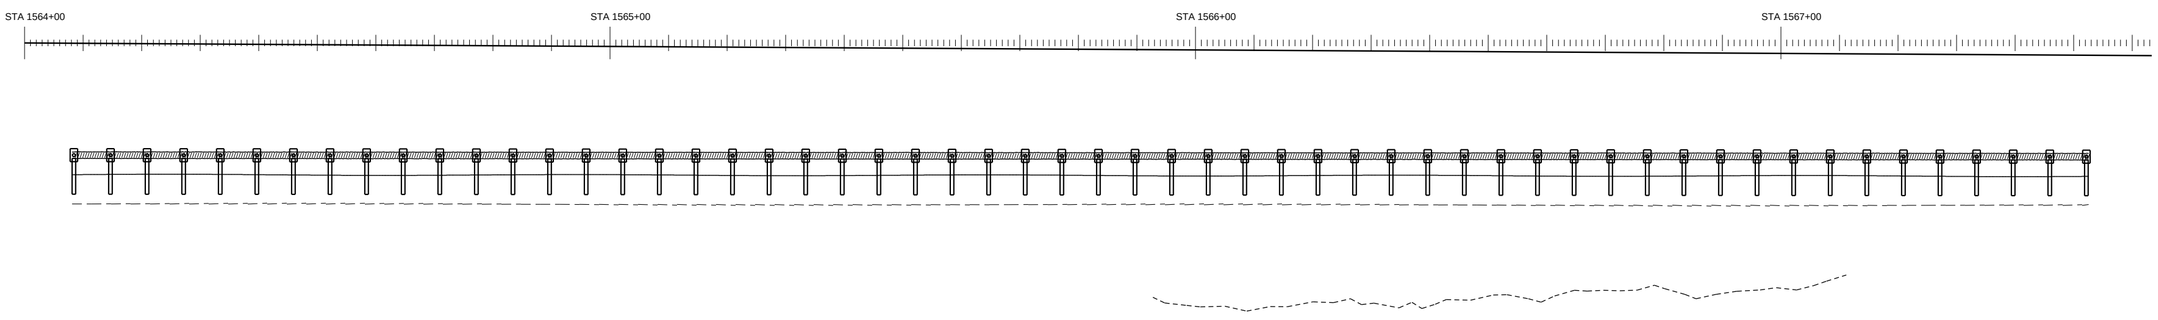


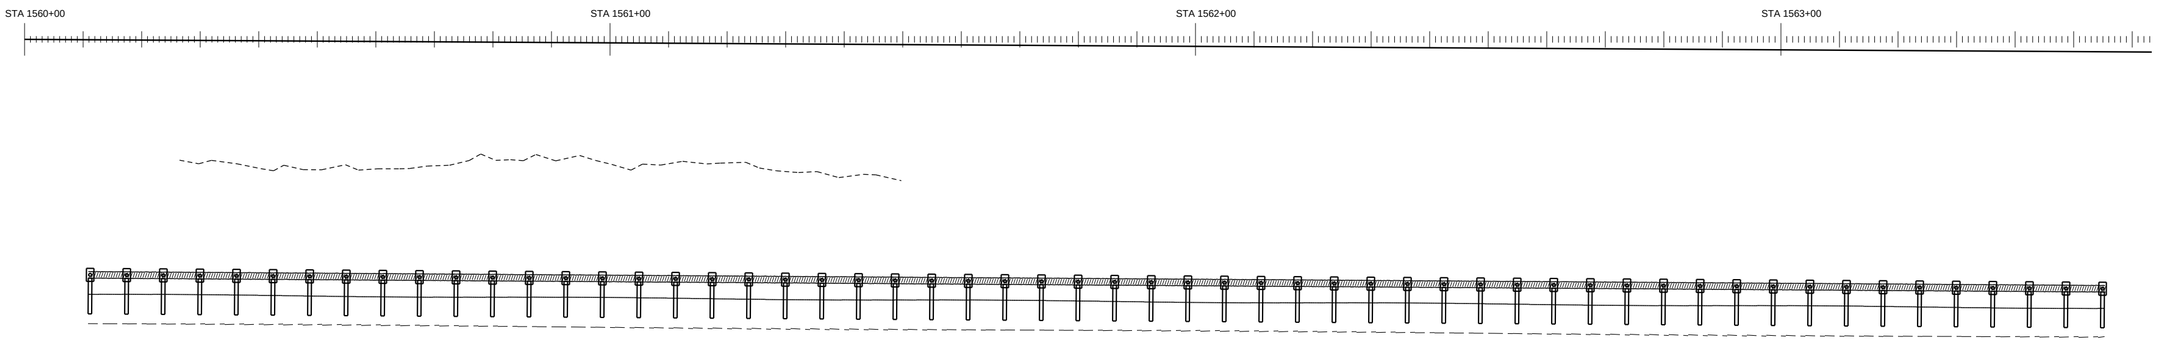


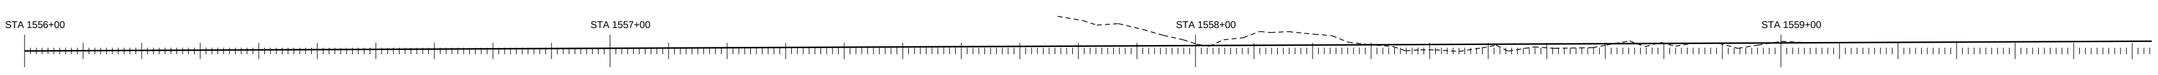


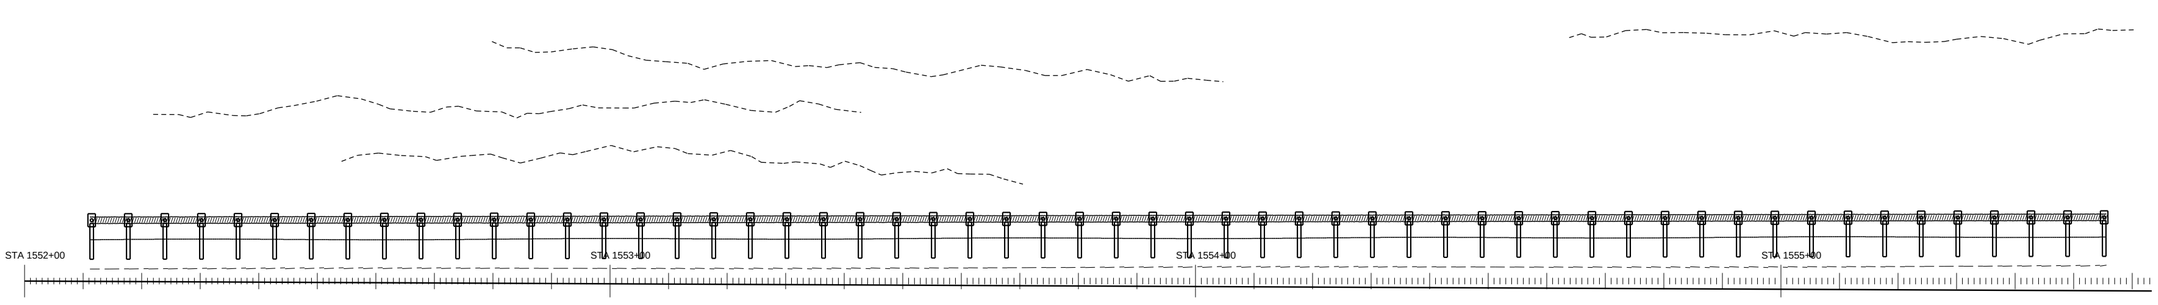


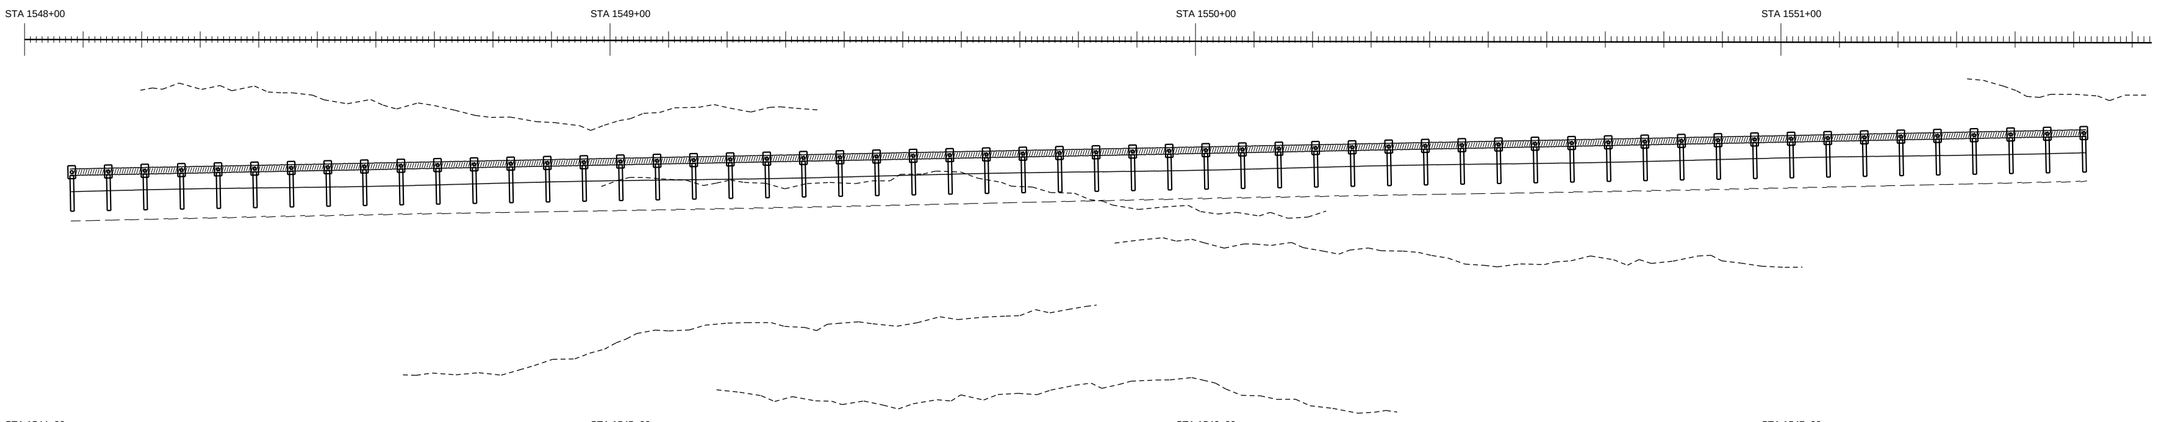


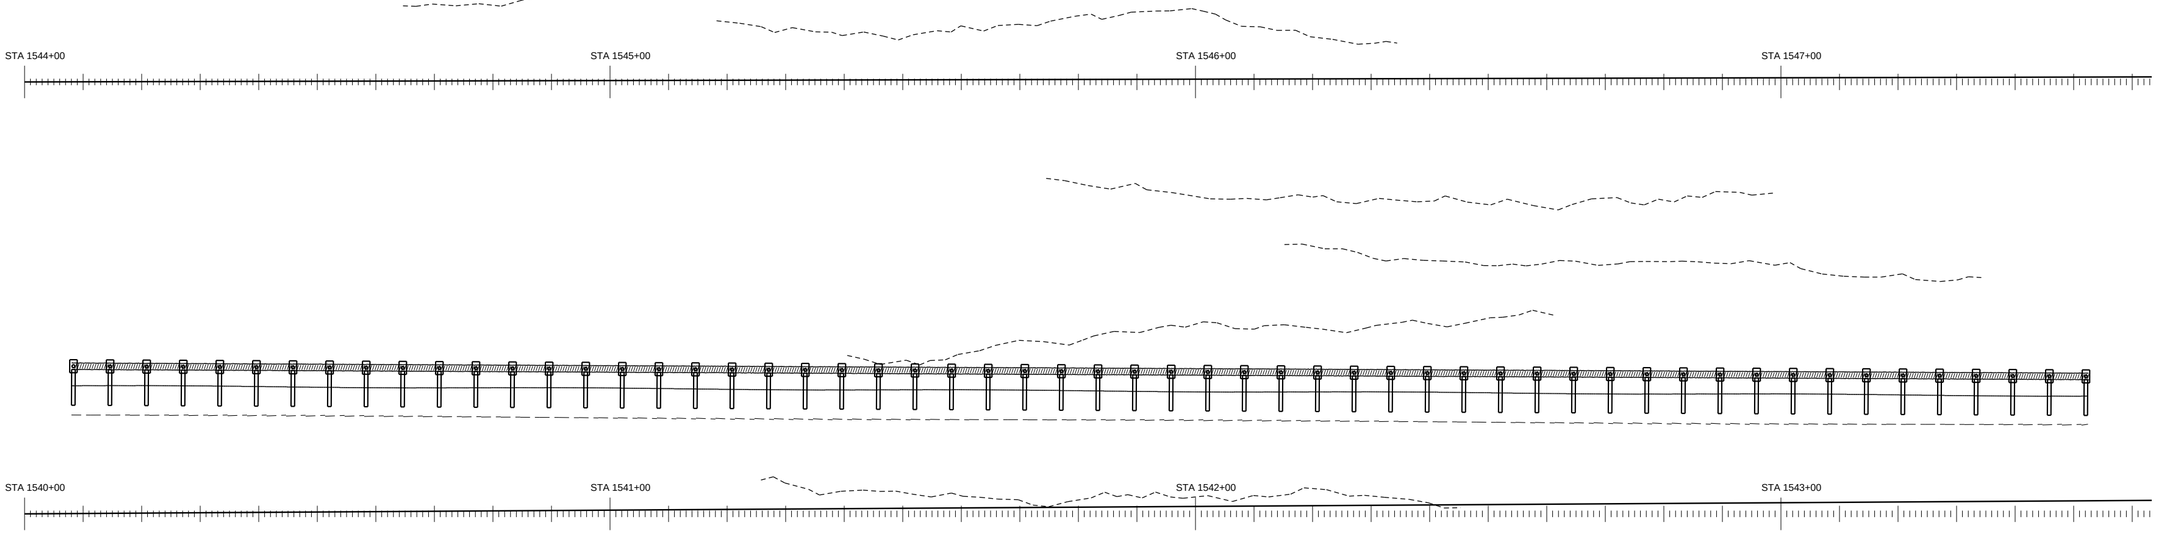





PAY ITEM 536-1-1 GUARDRAIL ROADWAY (TL-3)

PAY ITEM 536-85-24 END TREATMENT

GUARANTEED FENCE CORP

FIN. PROJ. ID 441234-1-52-01

SHEET 97 OF 120

SHEET NO. 197

ROADWAY PLAN SCALE: 1" = 20'




PAY ITEM 536-1-1 GUARDRAIL ROADWAY (TL-3)

PAY ITEM 536-85-24 END TREATMENT

GUARANTEED FENCE CORP

FIN. PROJ. ID 441234-1-52-01

SHEET 98 OF 120

SHEET NO. 198

ROADWAY PLAN SCALE: 1" = 20'

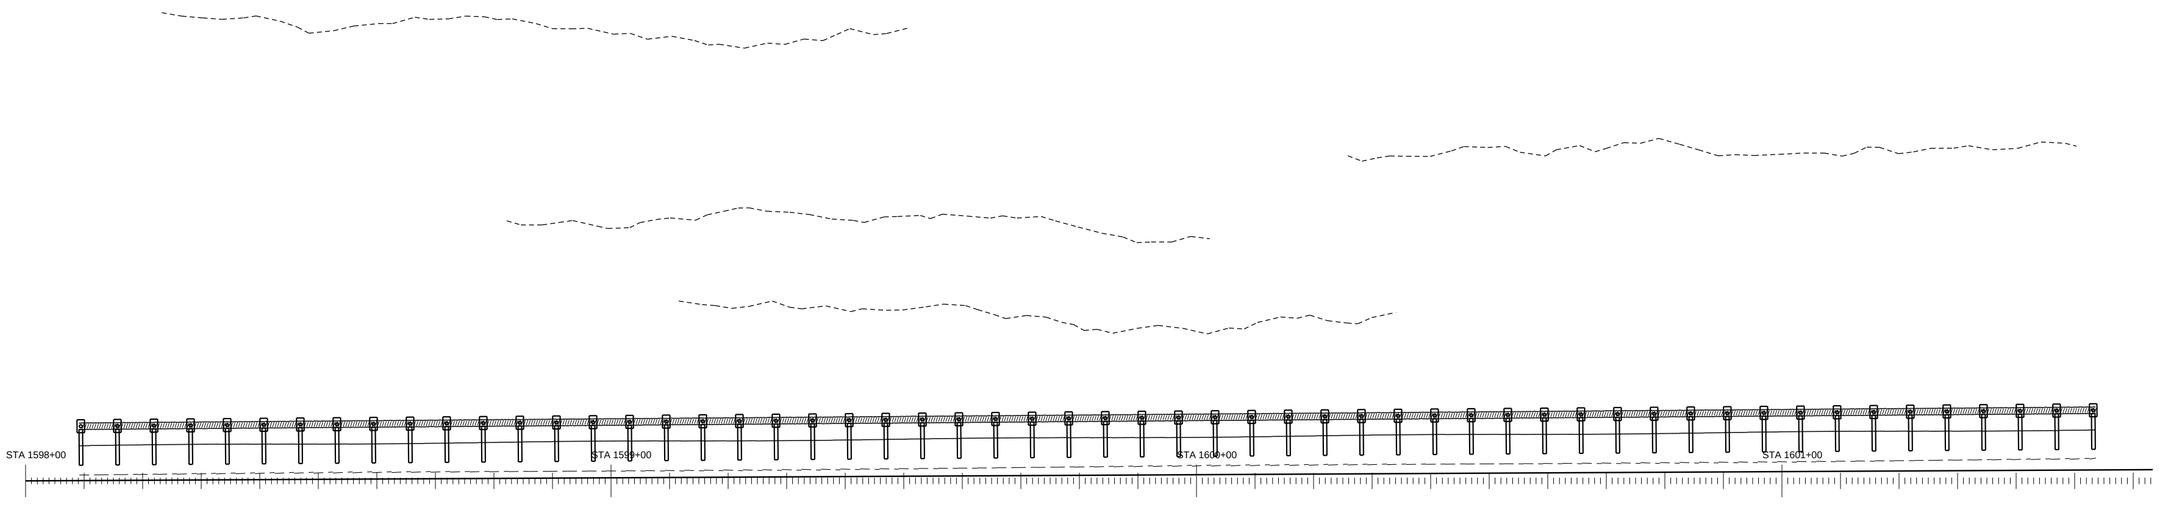


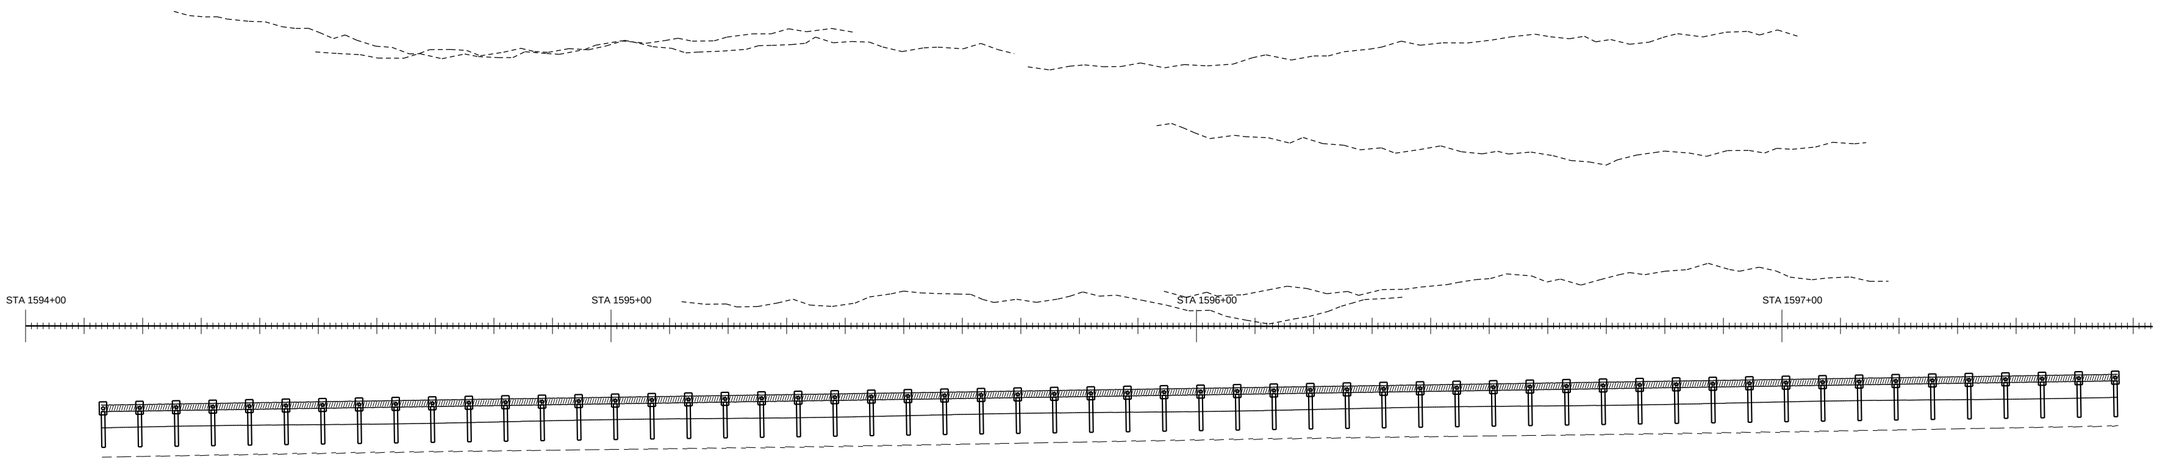


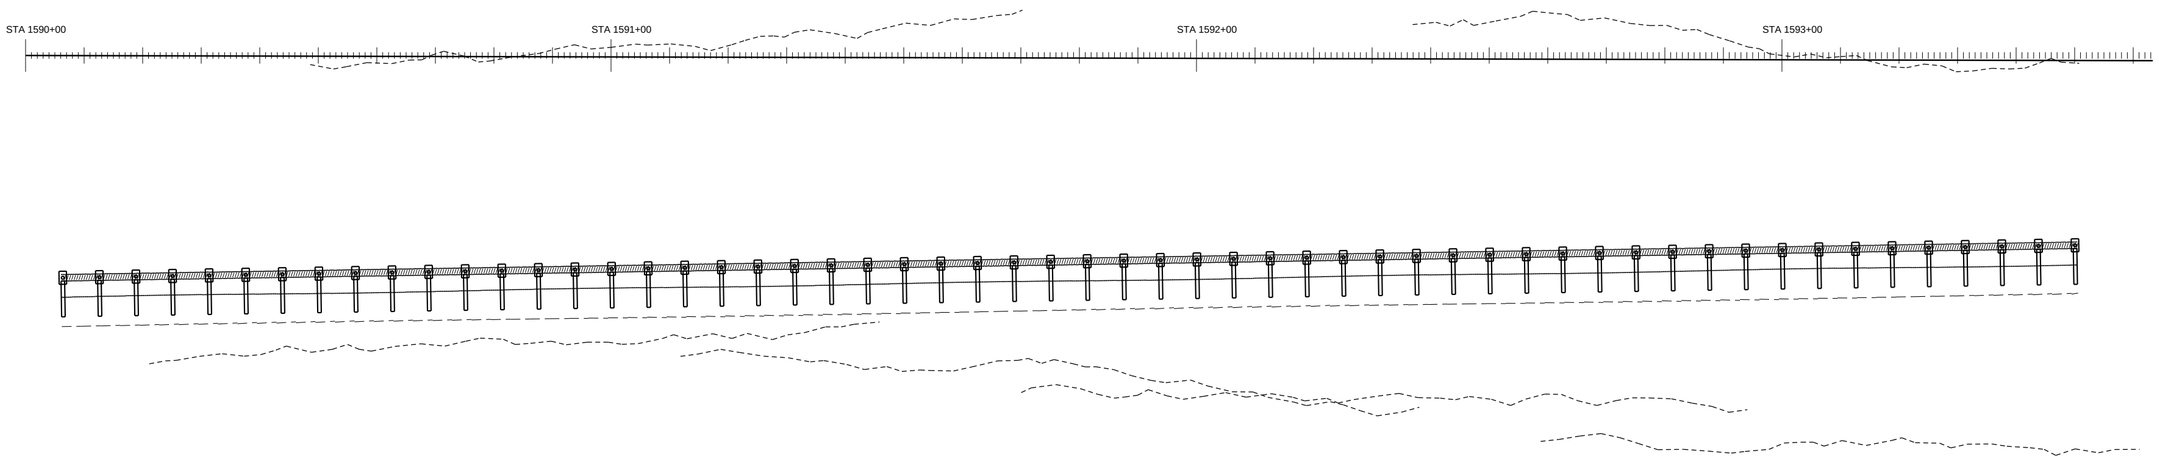





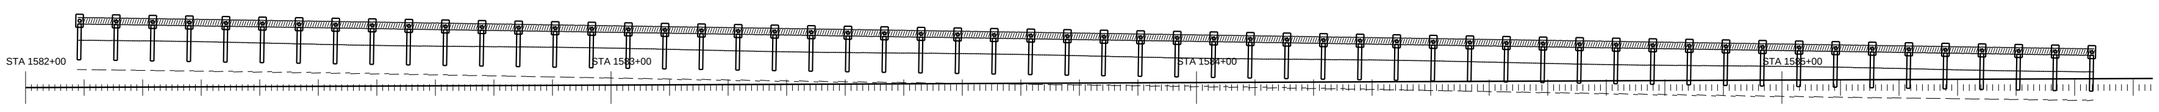


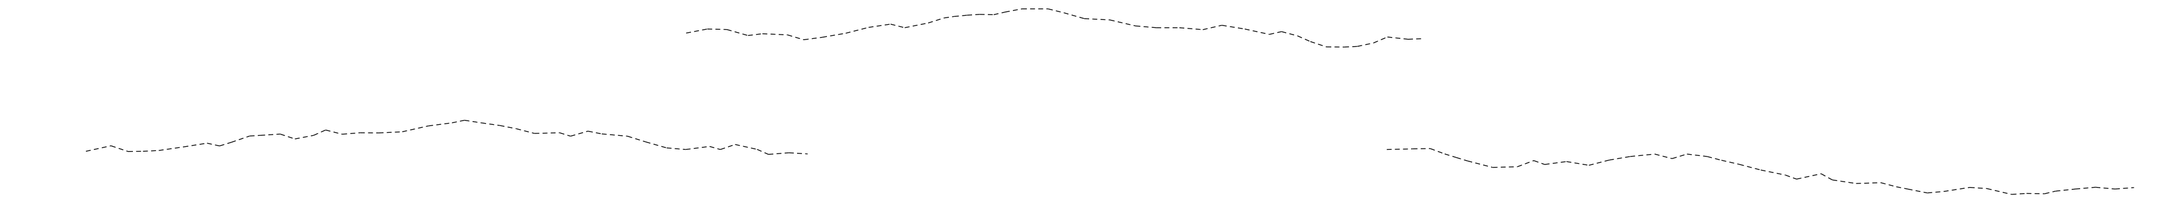


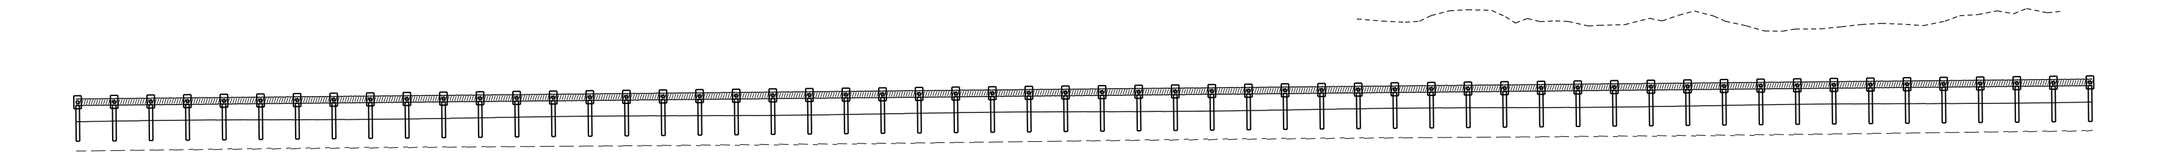

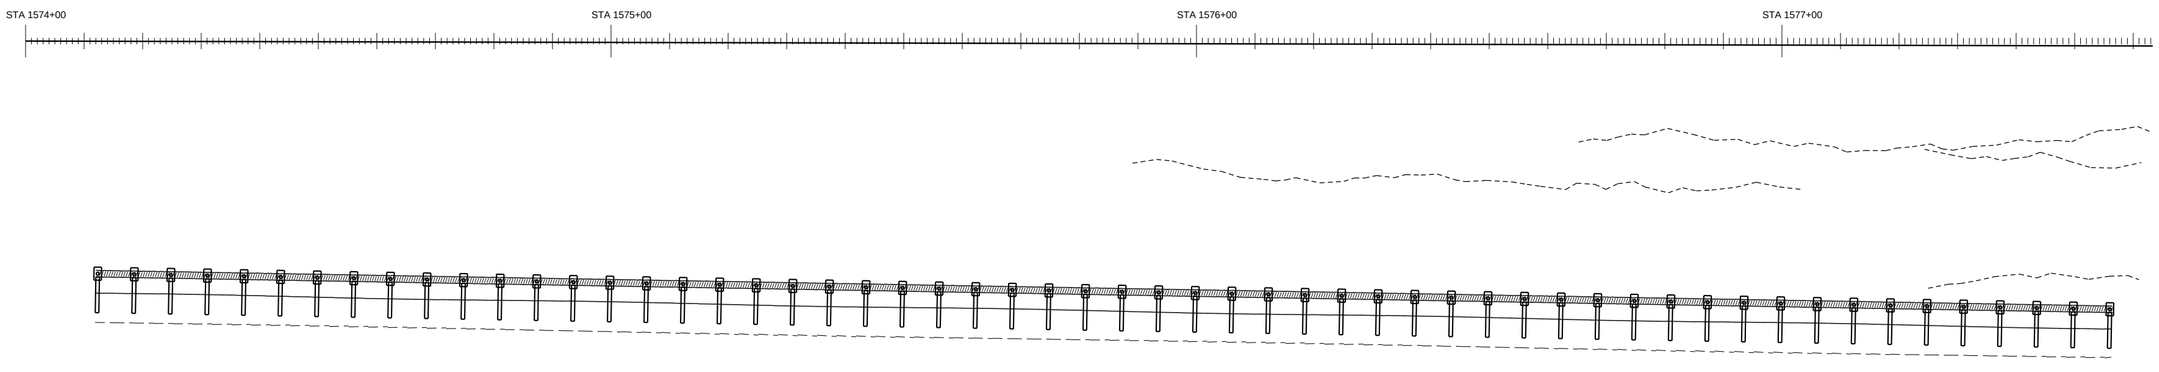


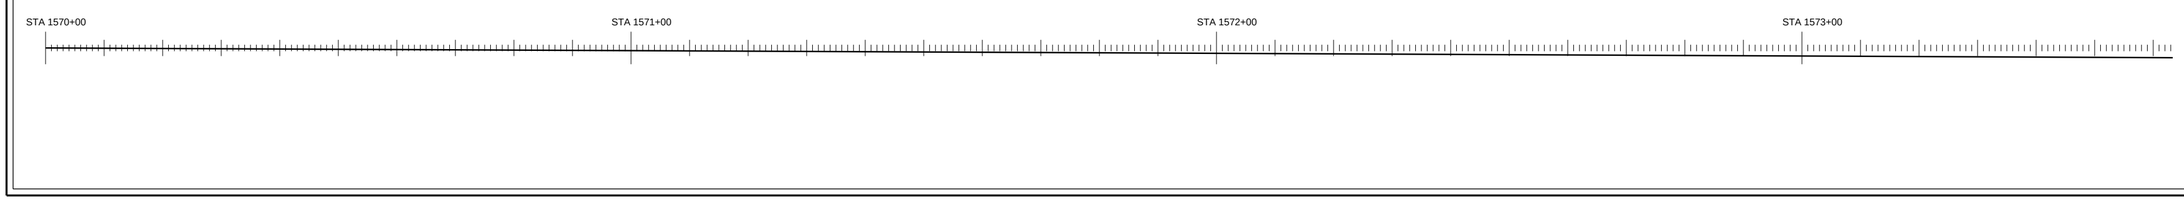


PAY ITEM 536-1-1 GUARDRAIL ROADWAY (TL-3)

PAY ITEM 536-85-24 END TREATMENT

GUARANTEED FENCE CORP

FIN. PROJ. ID 441234-1-52-01

SHEET 99 OF 120

SHEET NO. 199

ROADWAY PLAN SCALE: 1" = 20'

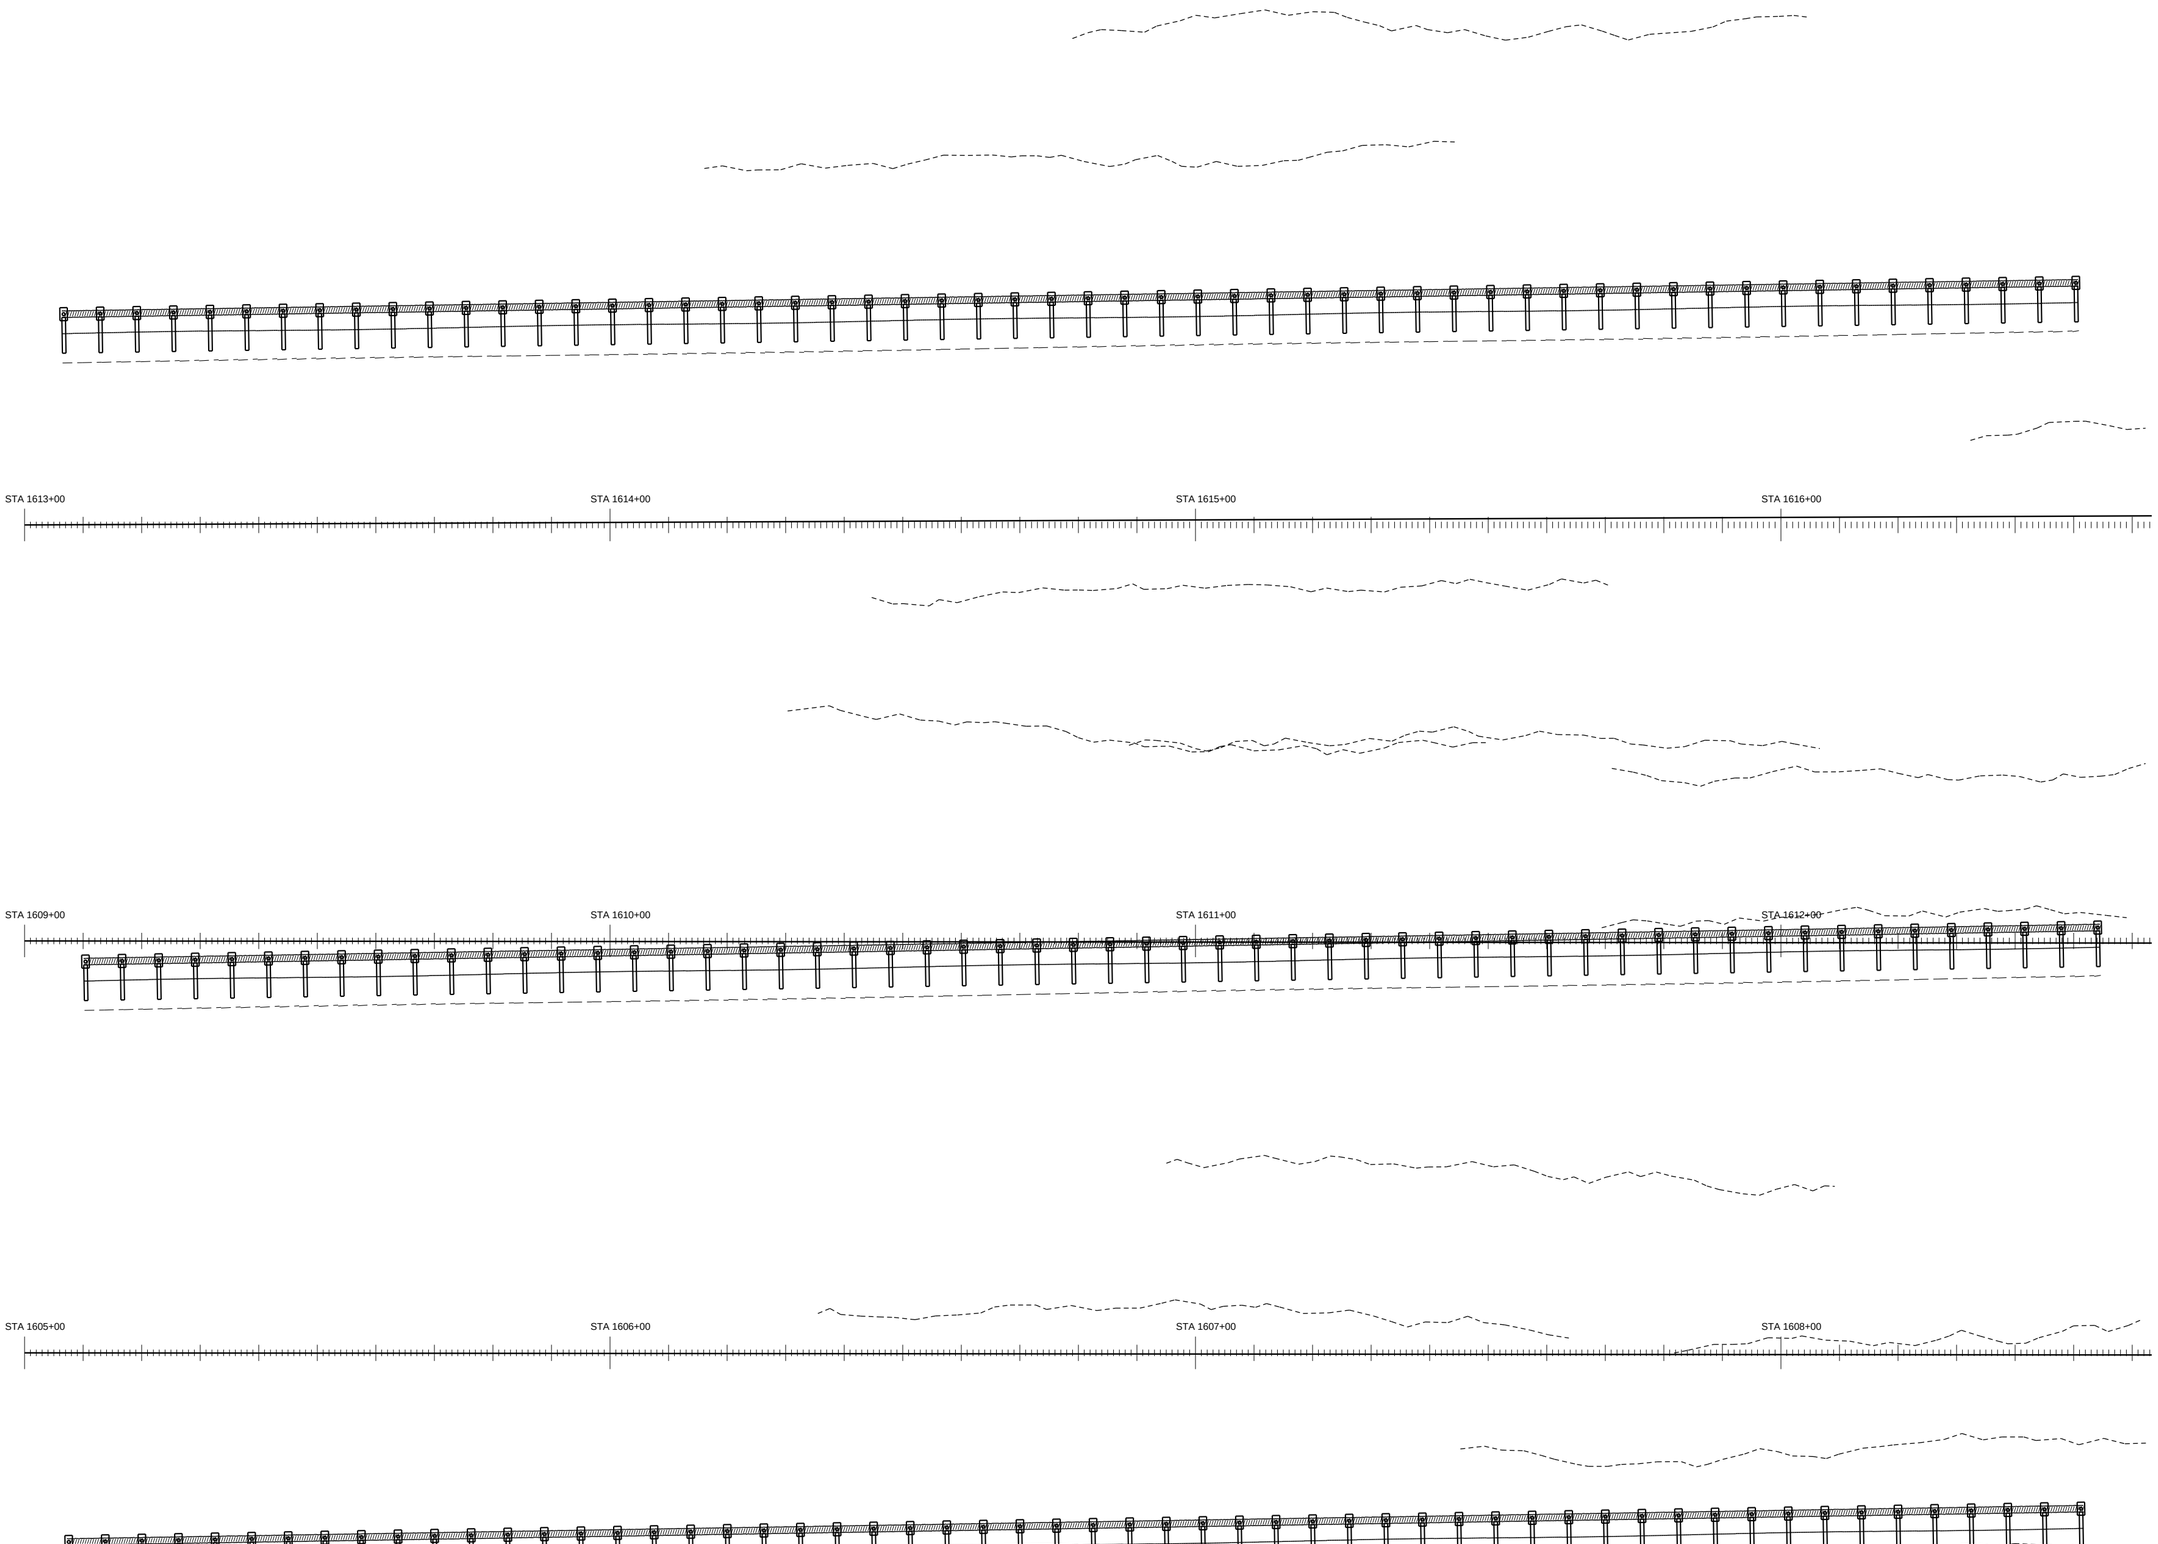


PAY ITEM 536-1-1 GUARDRAIL ROADWAY (T-3)

PAY ITEM 536-85-24 END TREATMENT

GUARANTEED FENCE CORP

FIN. PROJ. ID 441234-1-52-01

SHEET 100 OF 120

SHEET NO. 200

ROADWAY PLAN SCALE: 1" = 20'




PAY ITEM 536-1-1 GUARDRAIL ROADWAY (TL-3)

PAY ITEM 536-85-24 END TREATMENT

GUARANTEED FENCE CORP

FIN. PROJ. ID 441234-1-52-01

SHEET 101 OF 120

SHEET NO. 201

ROADWAY PLAN SCALE: 1" = 20'

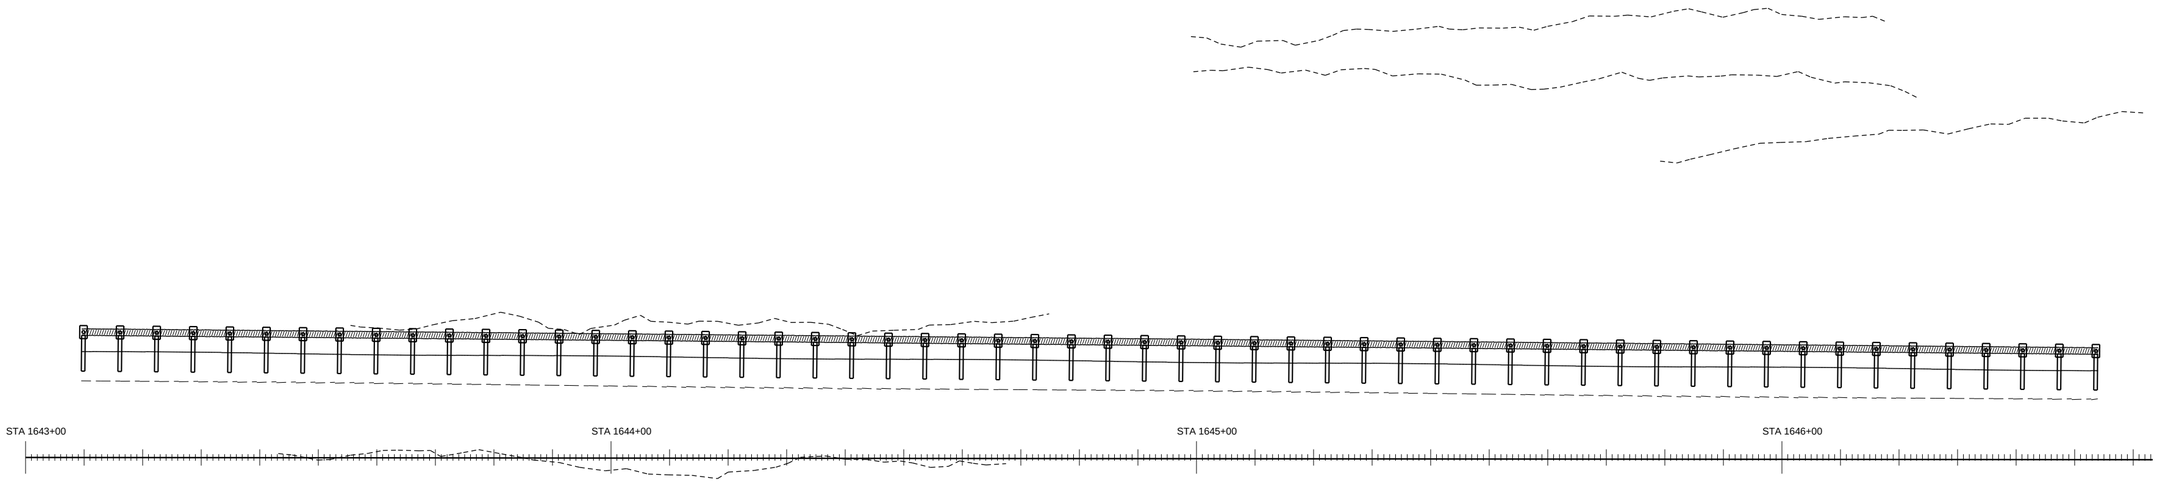


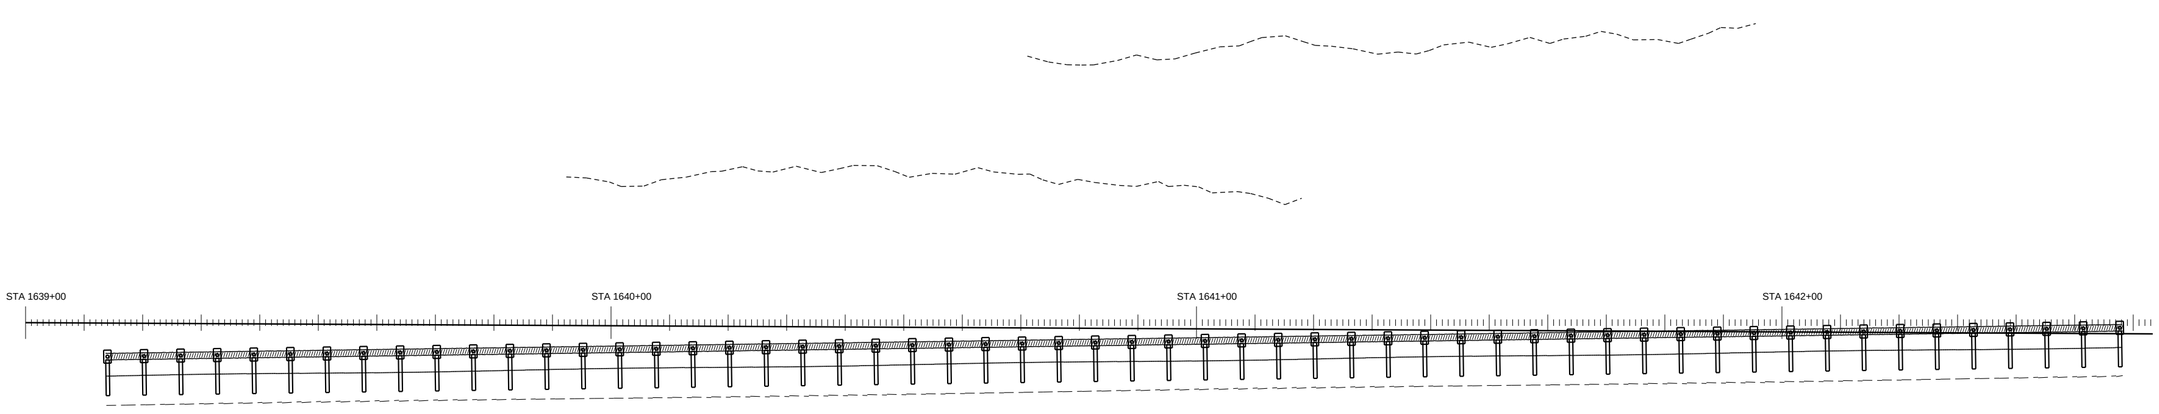


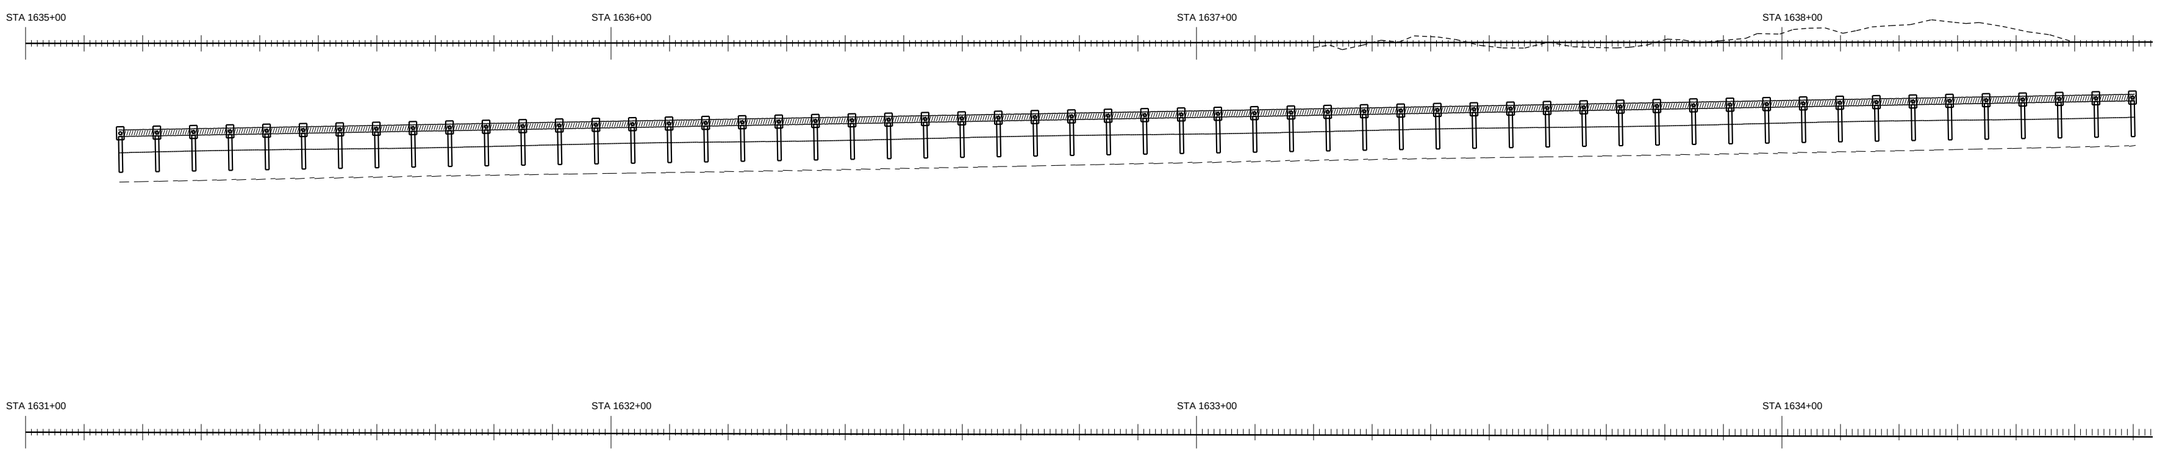


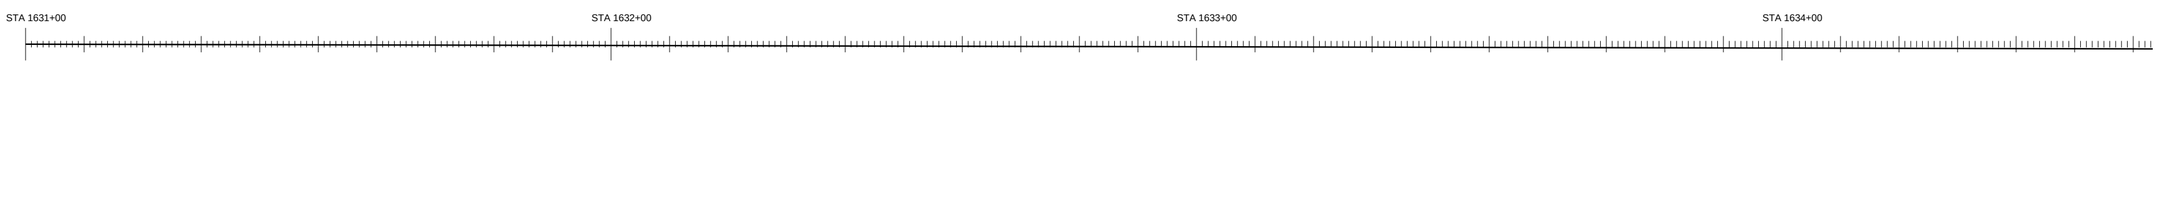


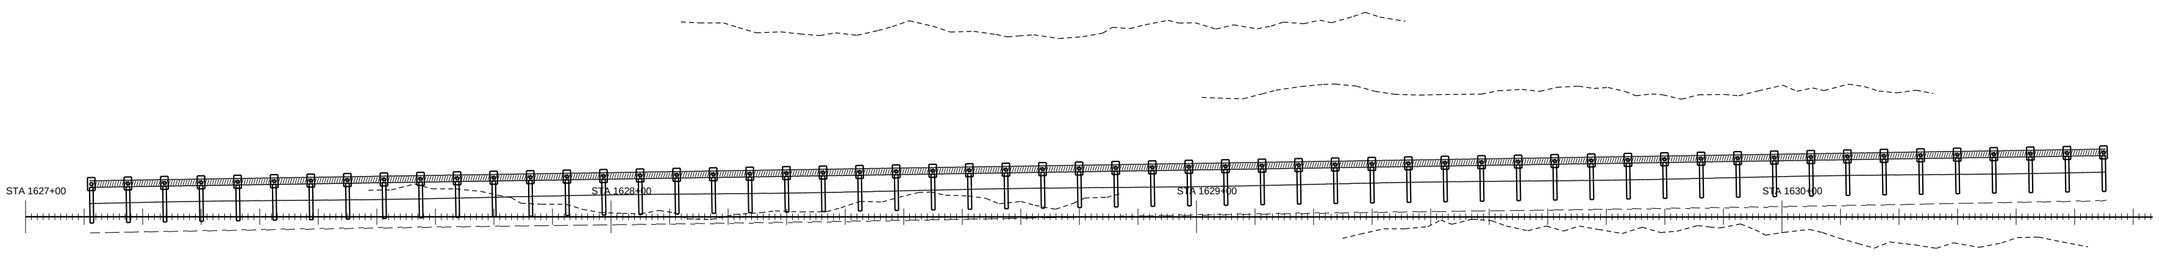


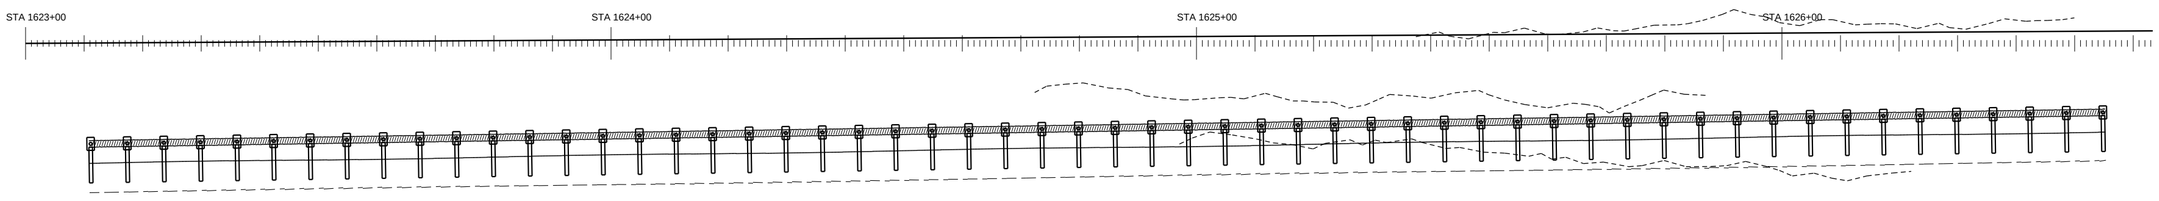


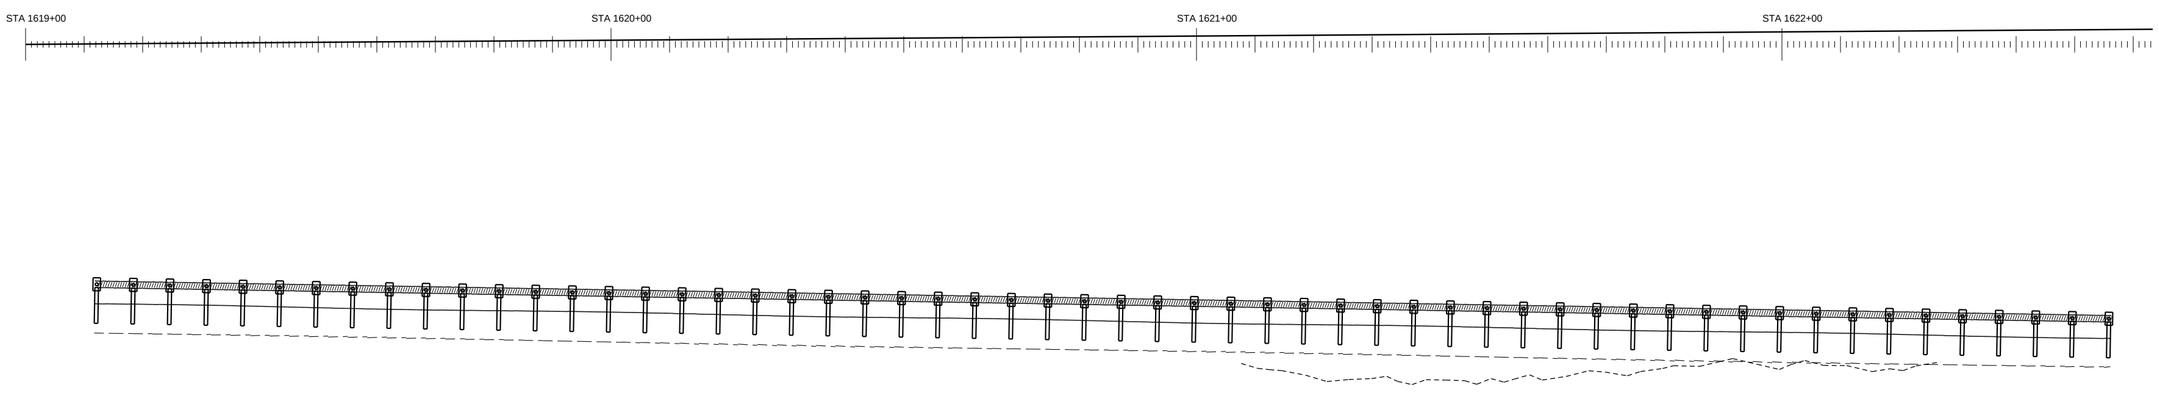


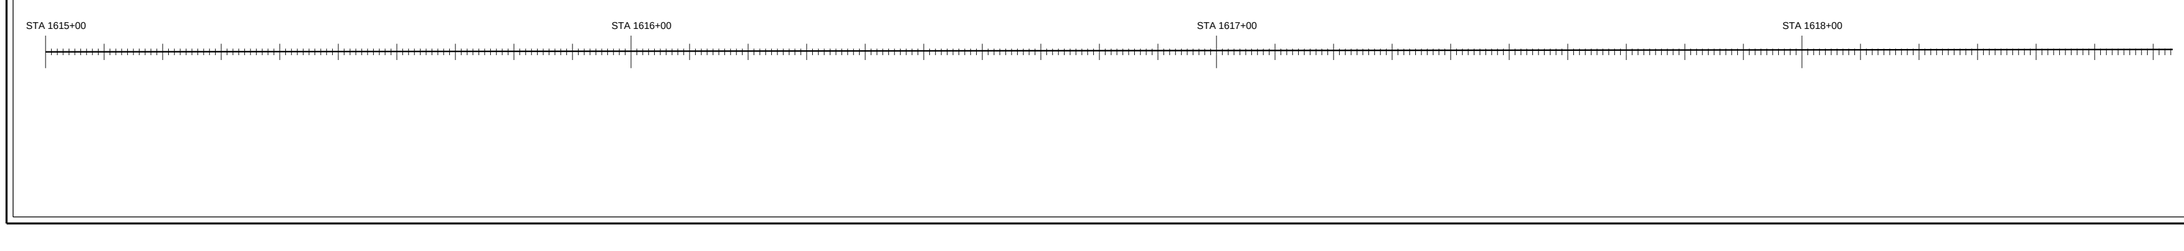


PAY ITEM 536-1-1 GUARDRAIL ROADWAY (TL-3)

PAY ITEM 536-85-24 END TREATMENT

GUARANTEED FENCE CORP

FIN. PROJ. ID 441234-1-52-01

SHEET 102 OF 120

SHEET NO. 202

ROADWAY PLAN SCALE: 1" = 20'

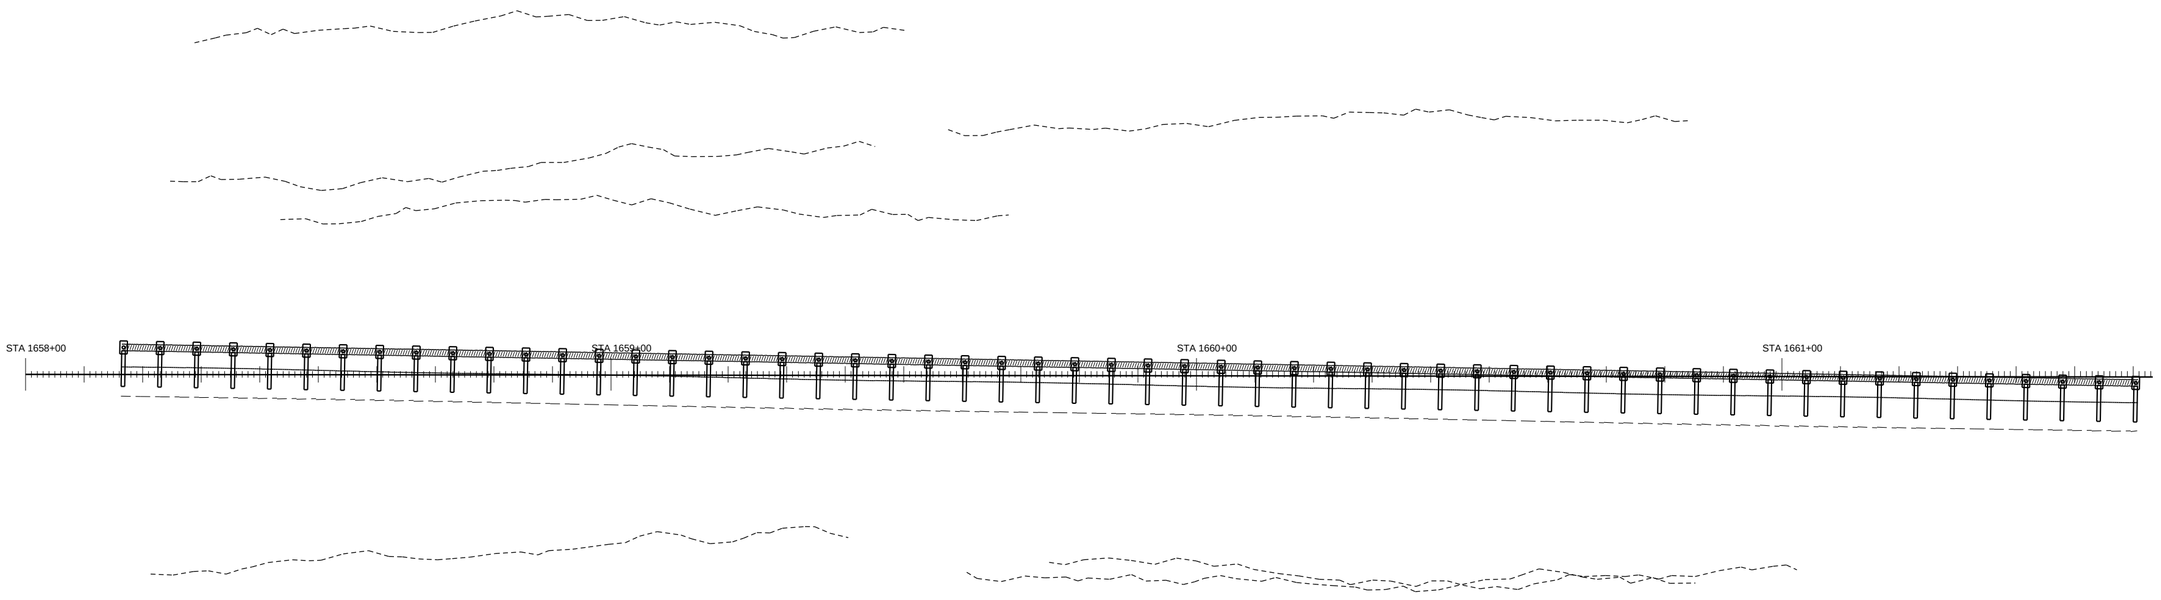


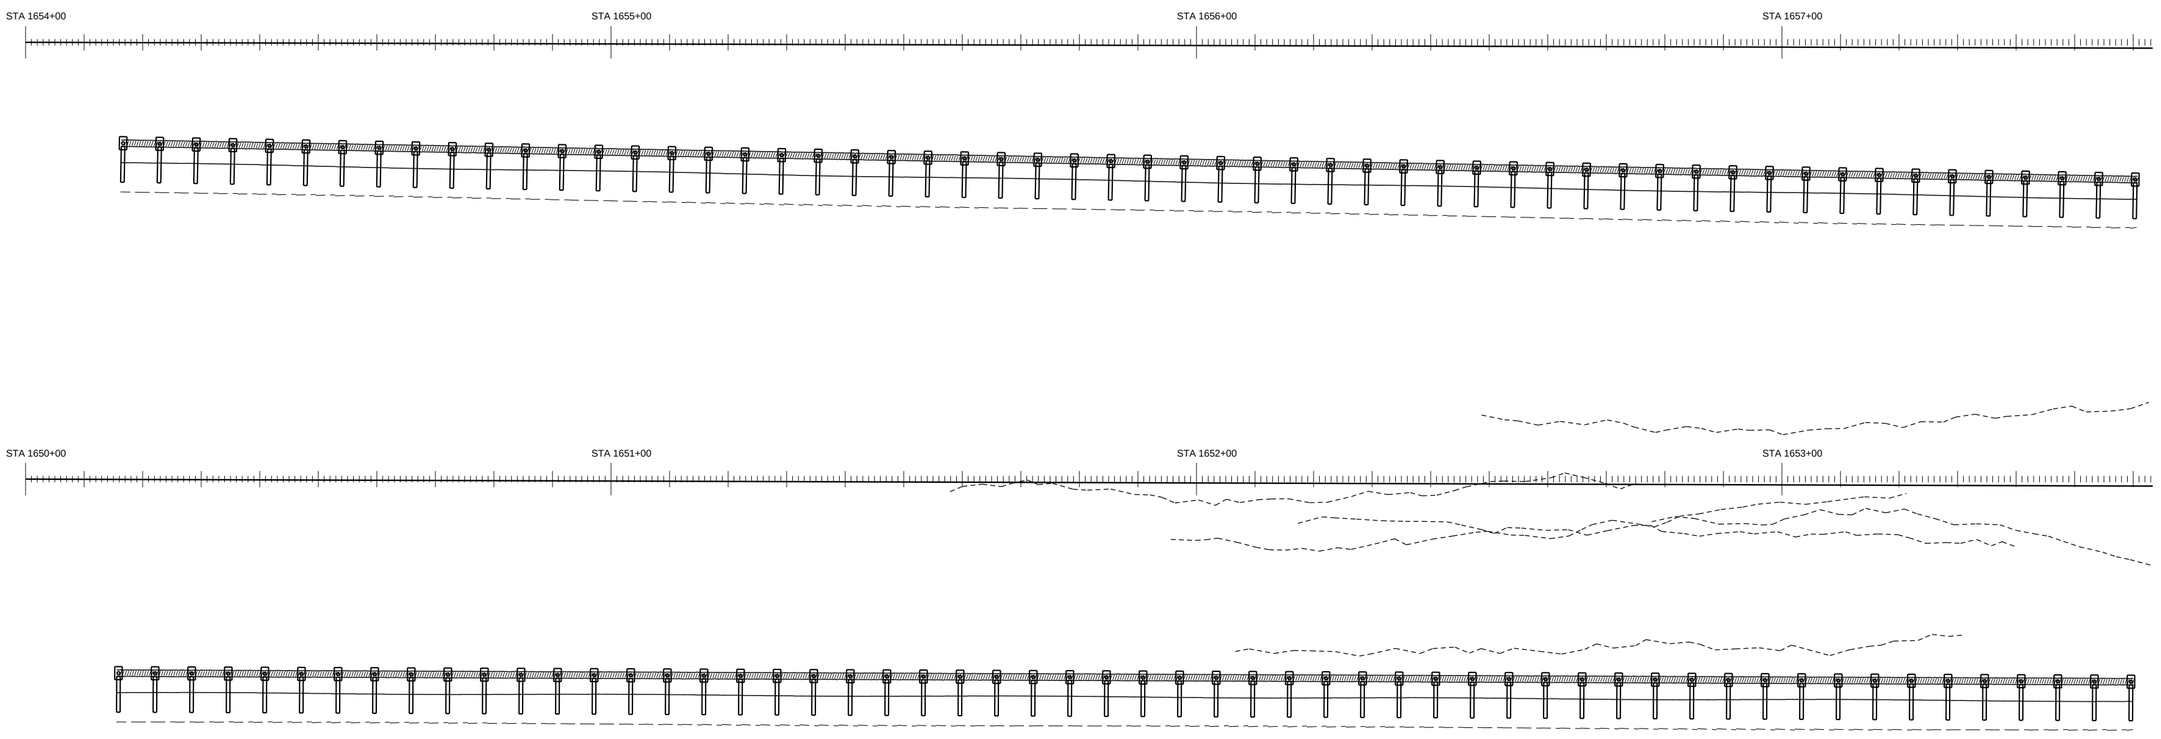


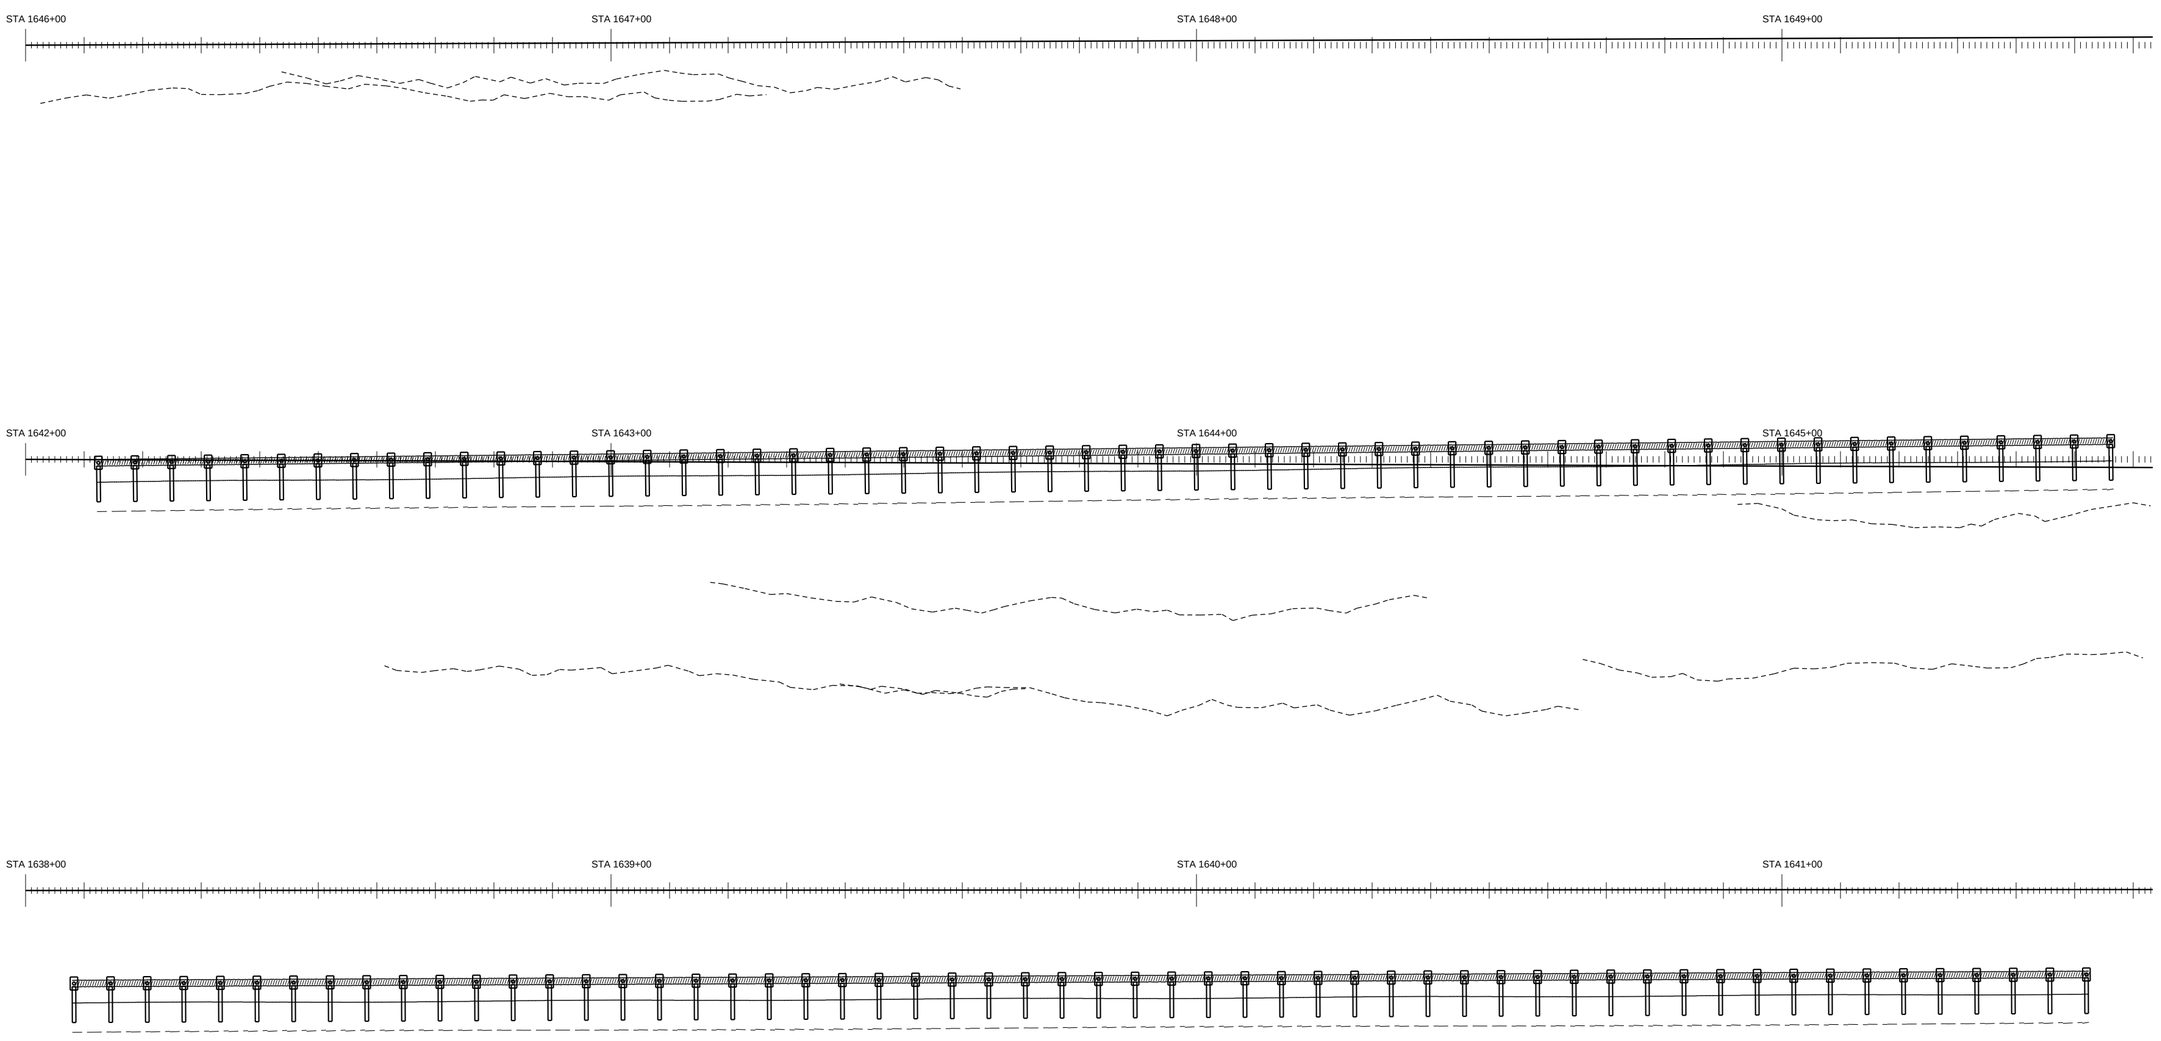


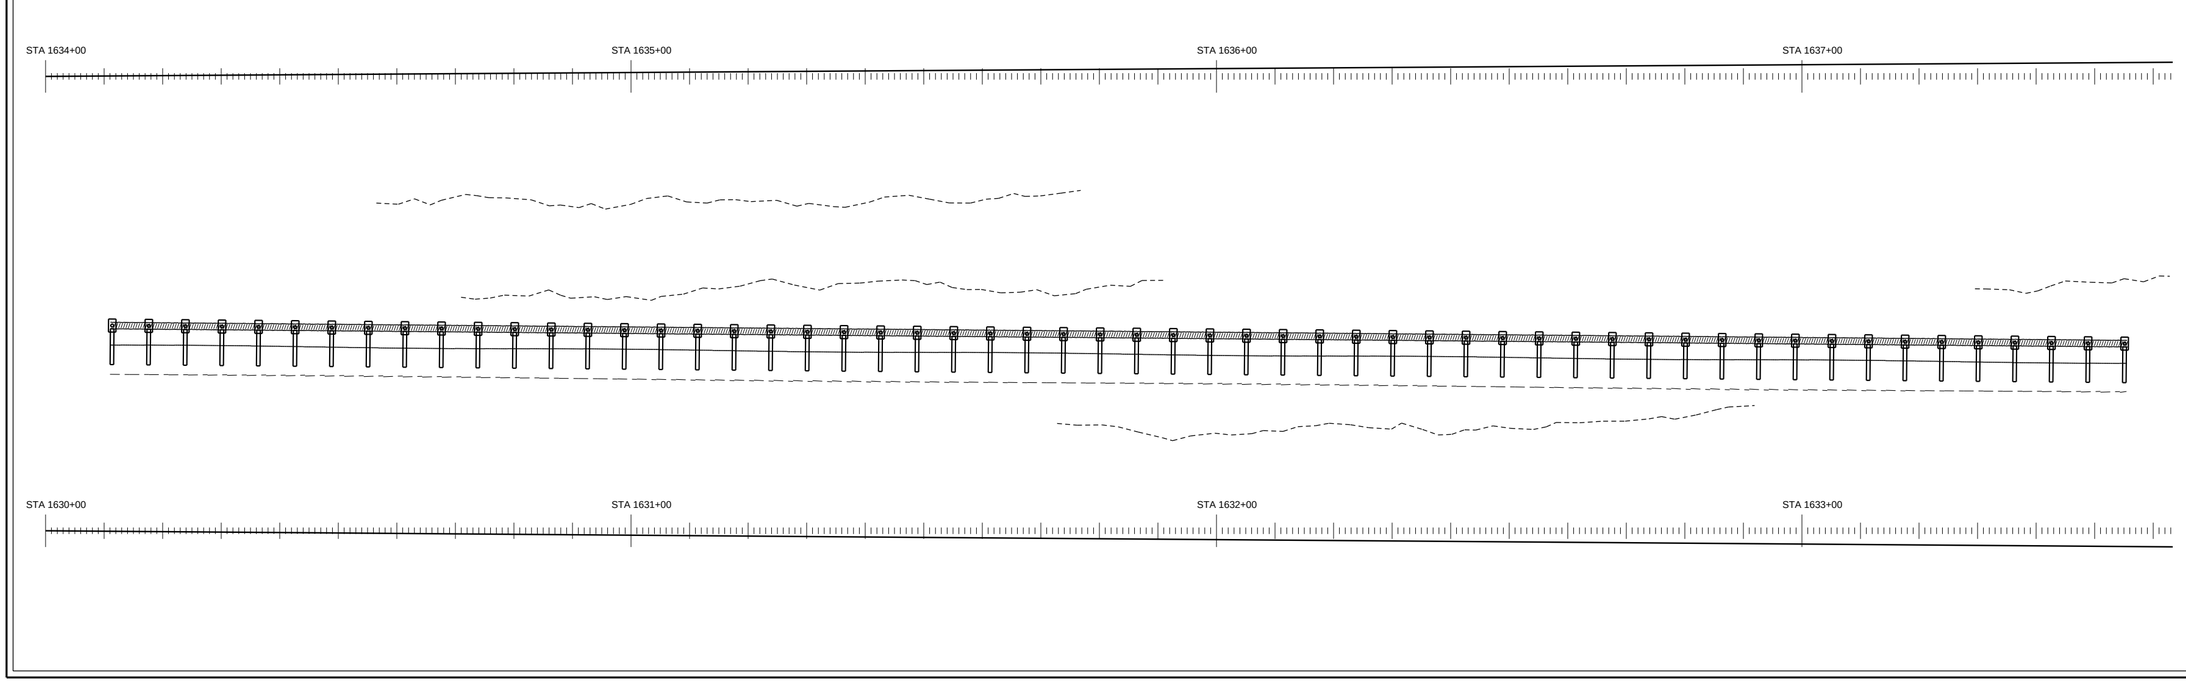


PAY ITEM 536-1-1 GUARDRAIL ROADWAY (TL-3)

PAY ITEM 536-85-24 END TREATMENT

GUARANTEED FENCE CORP

FIN. PROJ. ID 441234-1-52-01

SHEET 103 OF 120

SHEET NO. 203

ROADWAY PLAN SCALE: 1" = 20'

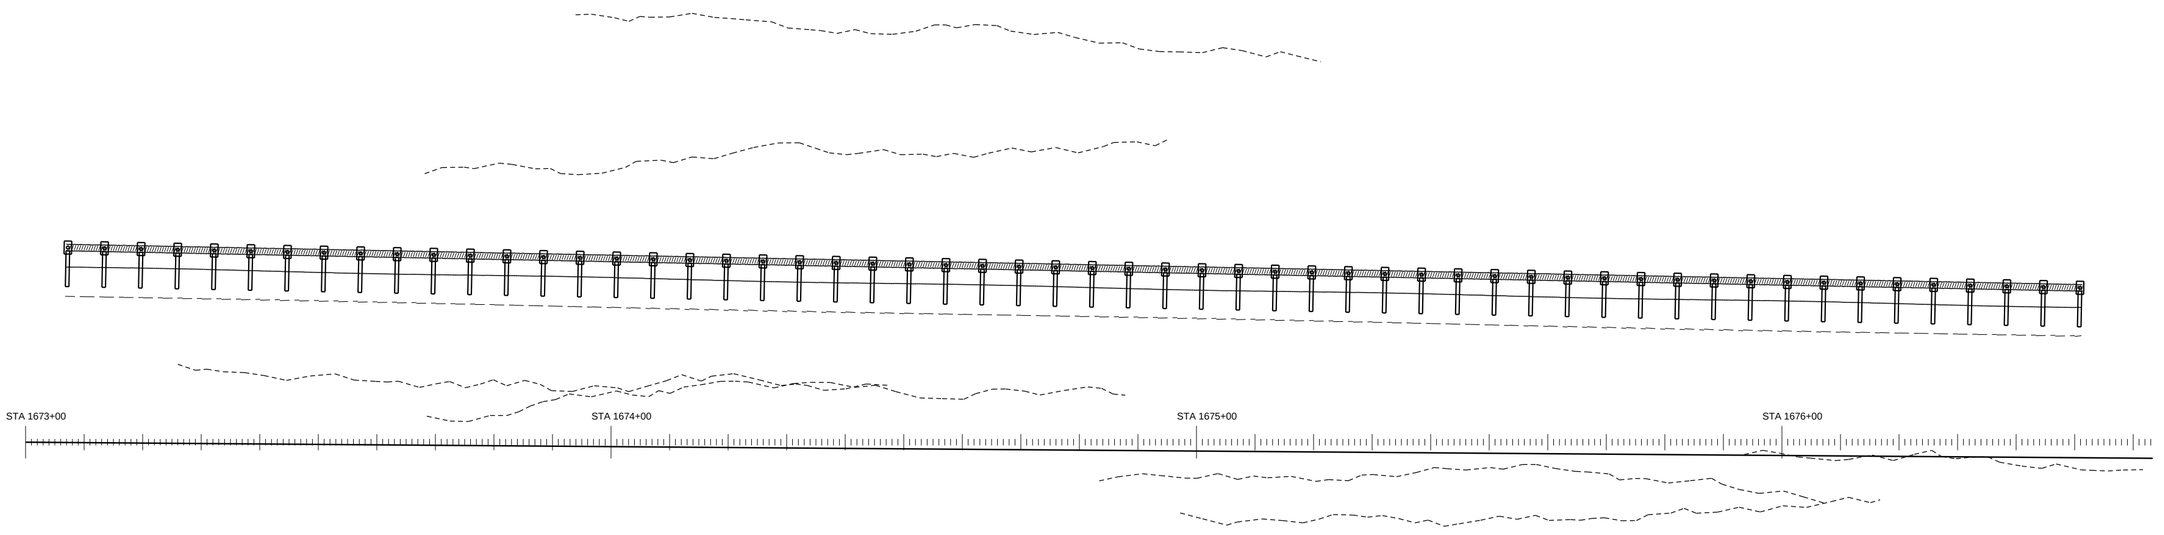


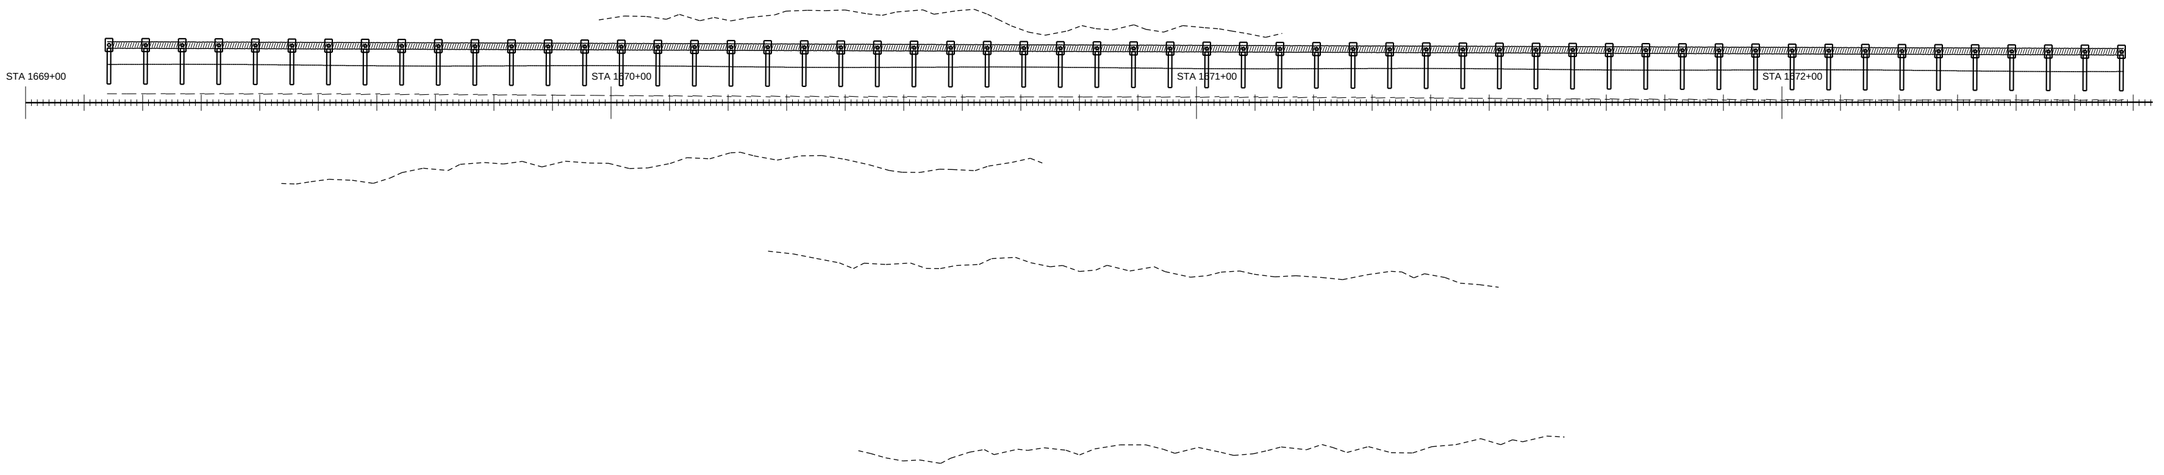


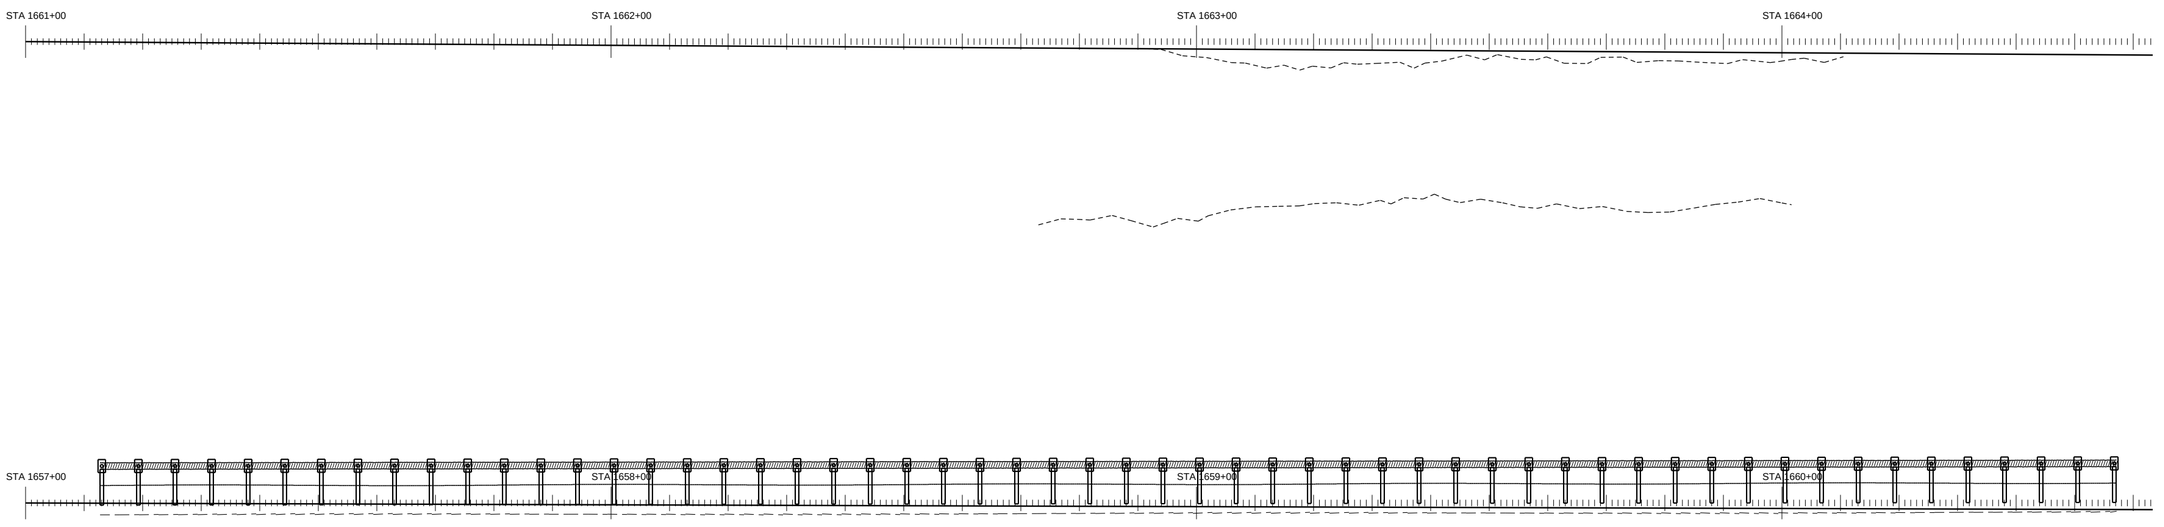


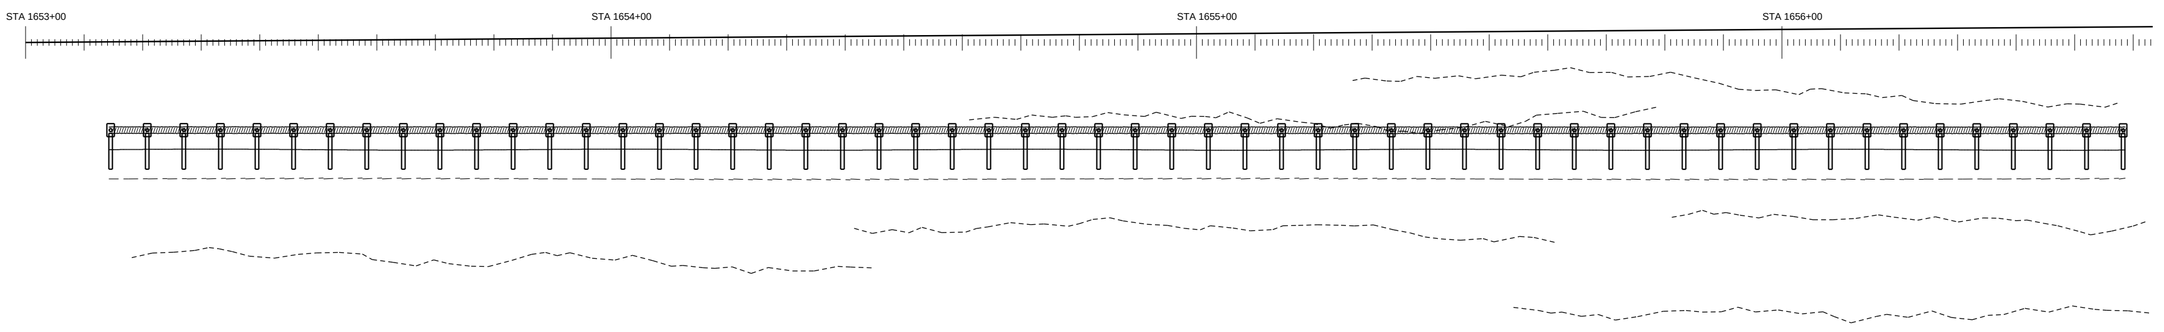


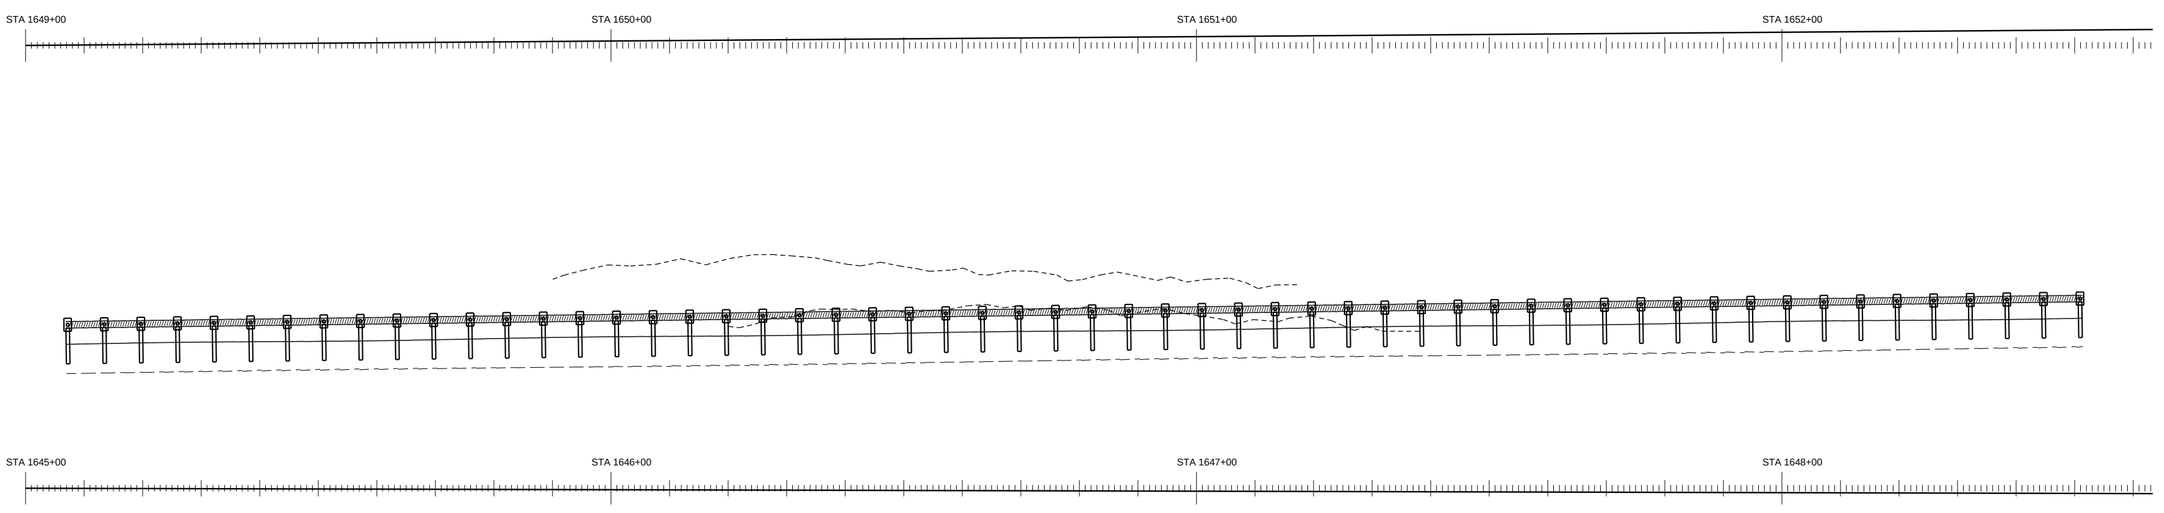


PAY ITEM 536-1-1 GUARDRAIL ROADWAY (TL-3)

PAY ITEM 536-85-24 END TREATMENT

GUARANTEED FENCE CORP

FIN. PROJ. ID 441234-1-52-01

SHEET 104 OF 120

SHEET NO. 204

ROADWAY PLAN SCALE: 1" = 20'

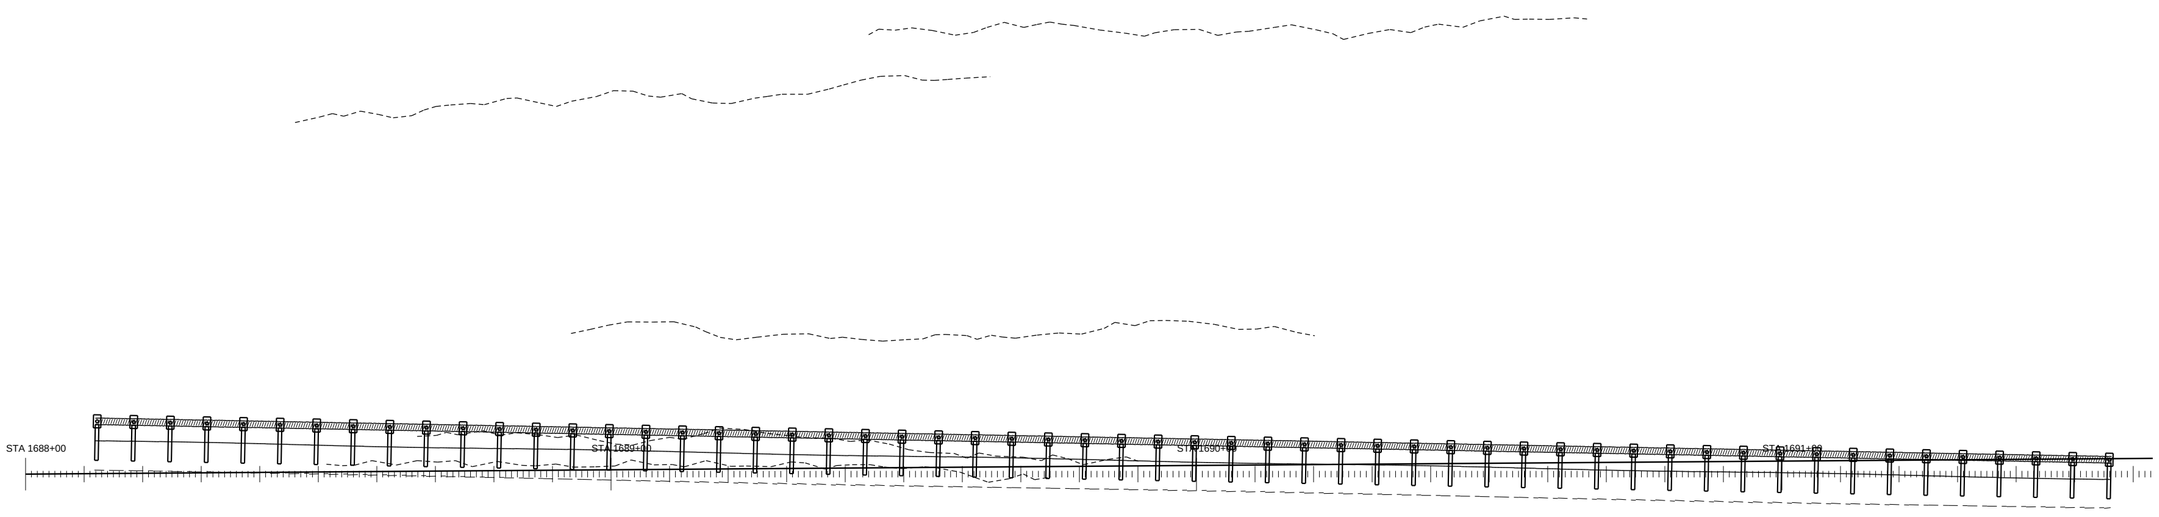


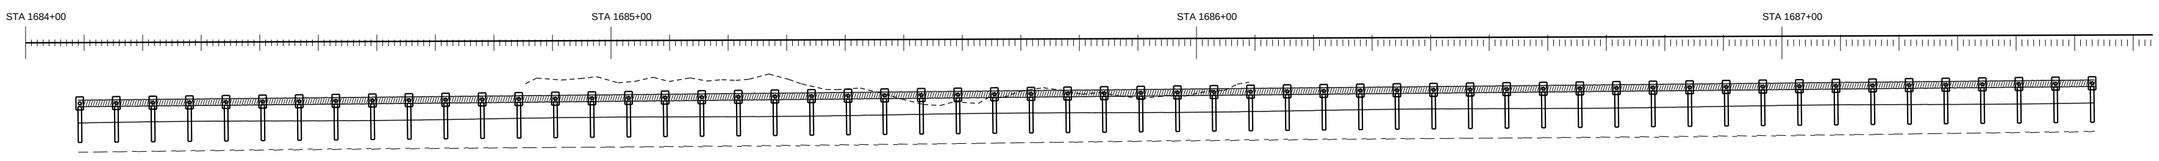


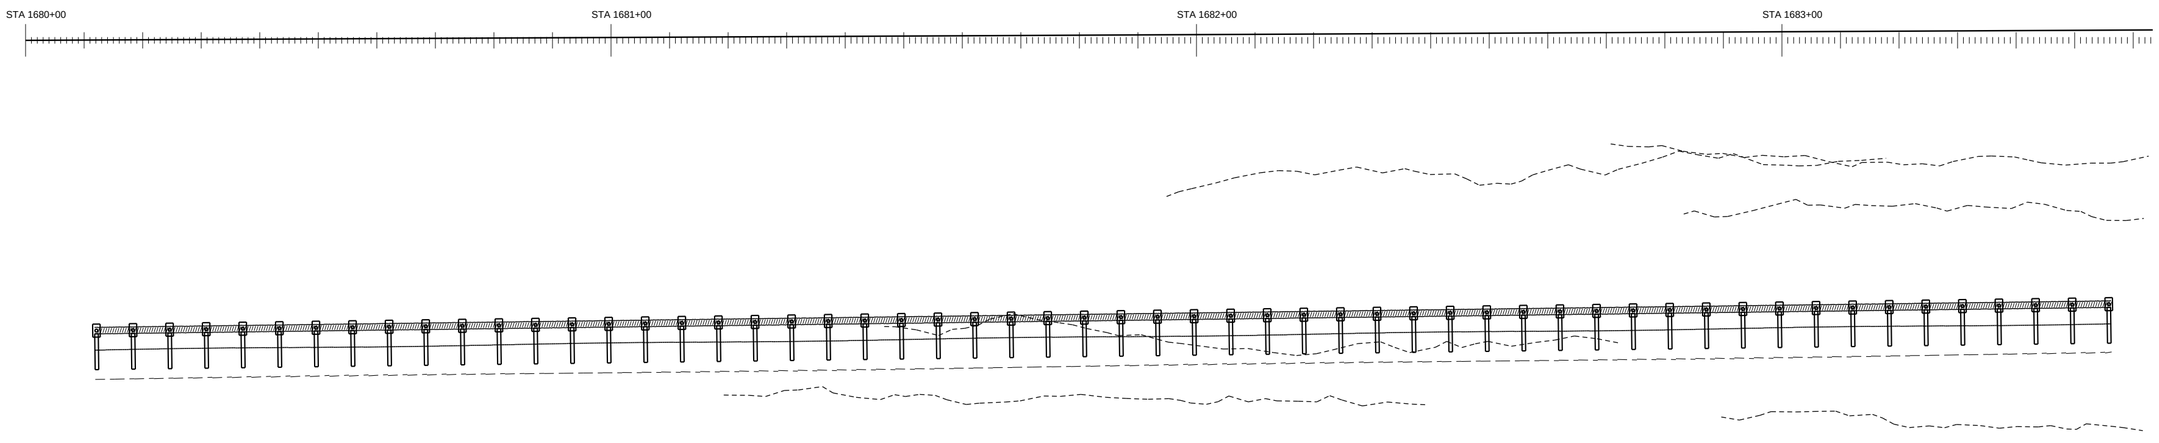


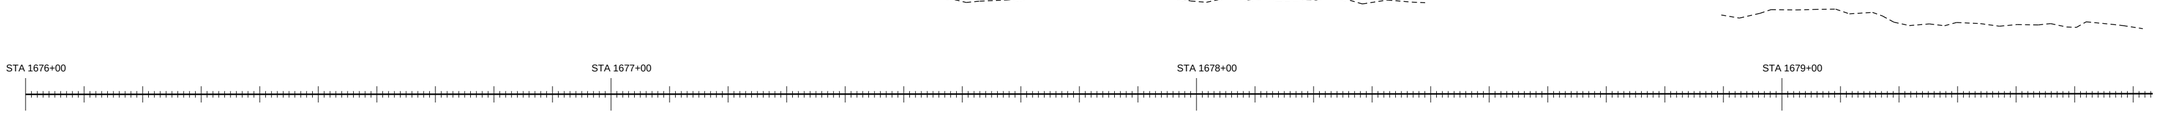


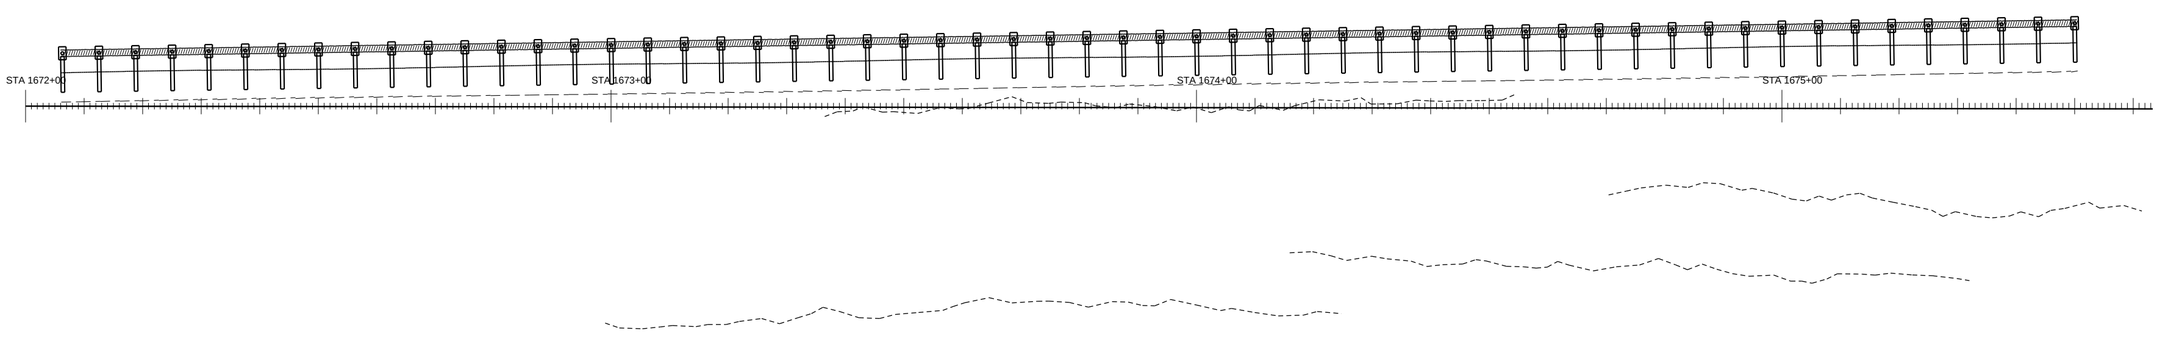


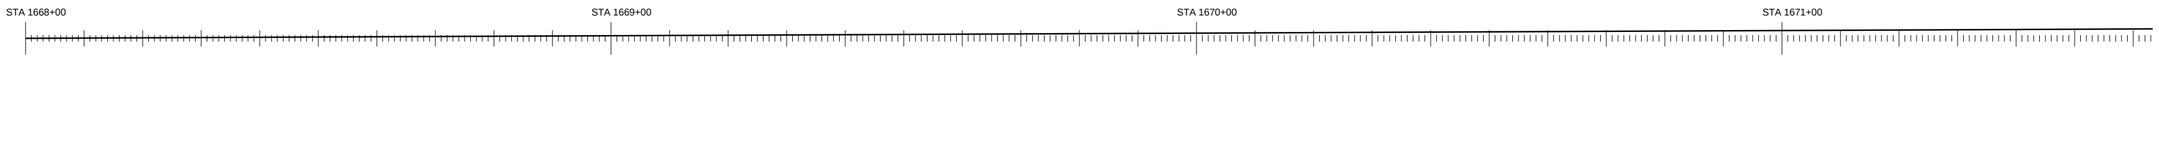


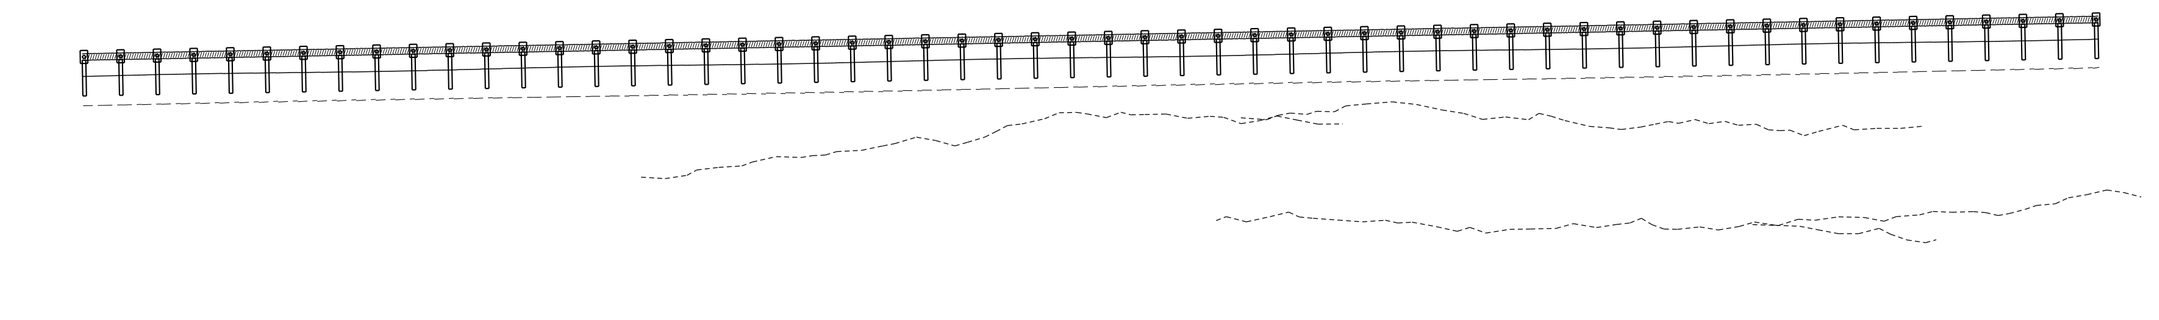


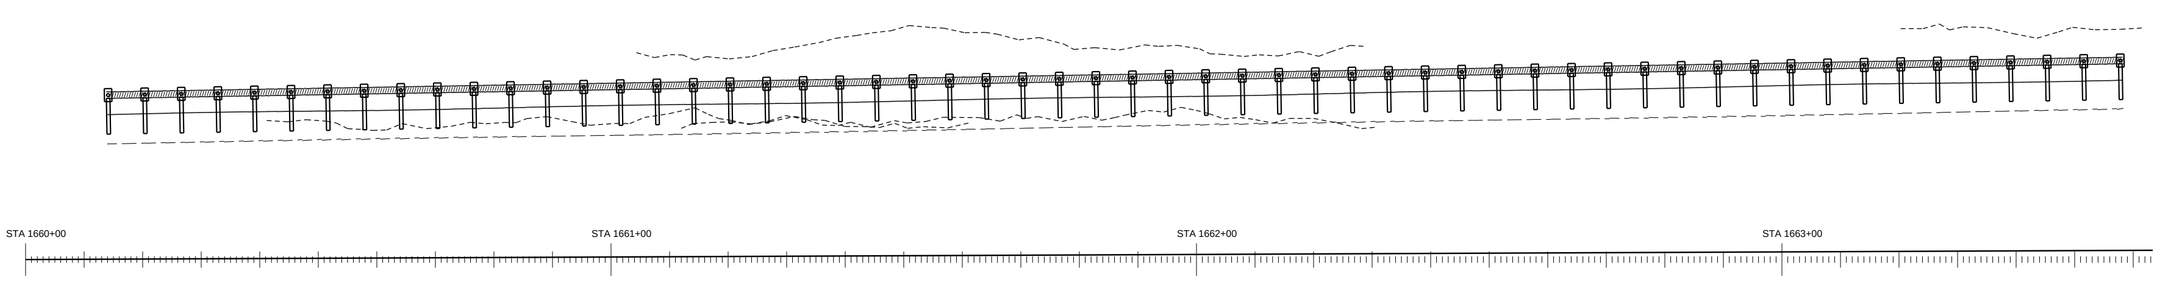


PAY ITEM 536-1-1 GUARDRAIL ROADWAY (TL-3)

PAY ITEM 536-85-24 END TREATMENT

GUARANTEED FENCE CORP

FIN. PROJ. ID 441234-1-52-01

SHEET 105 OF 120

SHEET NO. 205

ROADWAY PLAN SCALE: 1" = 20'

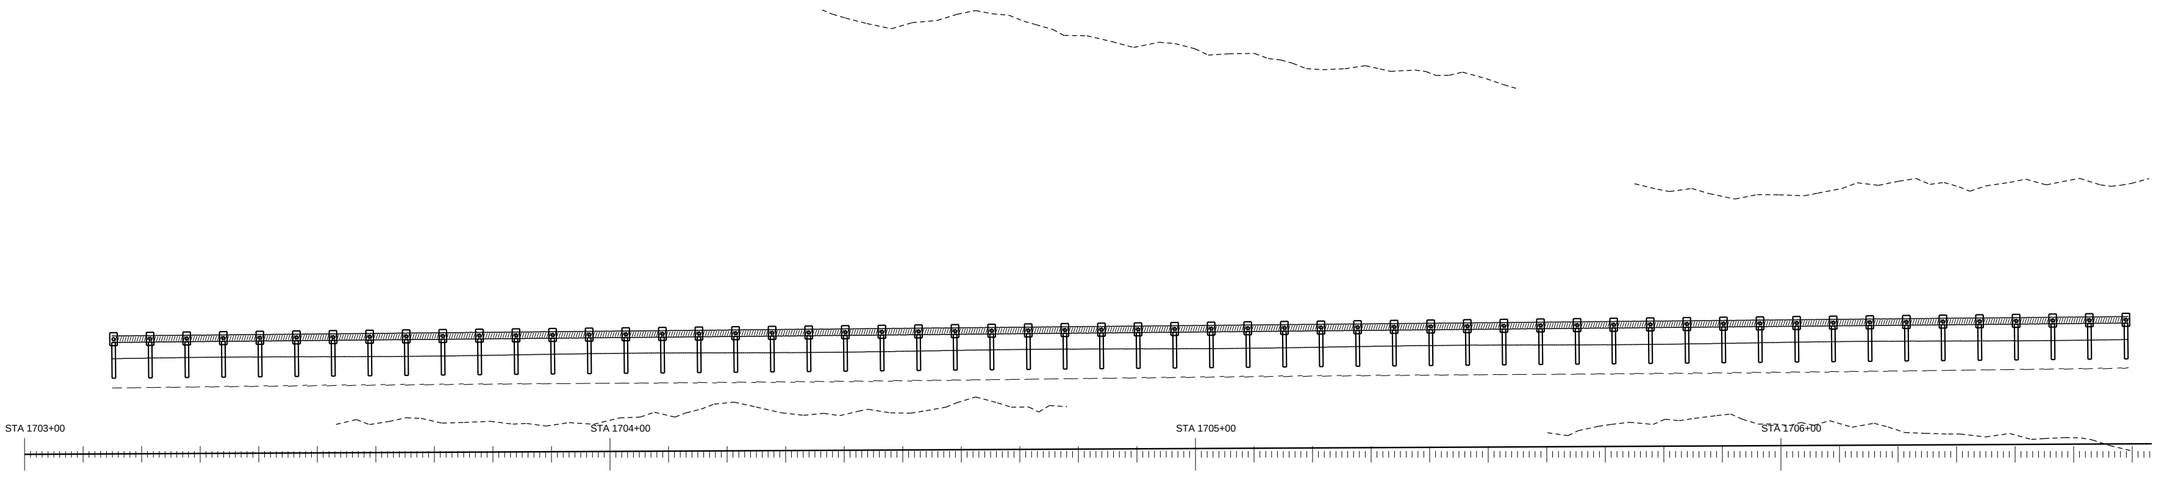


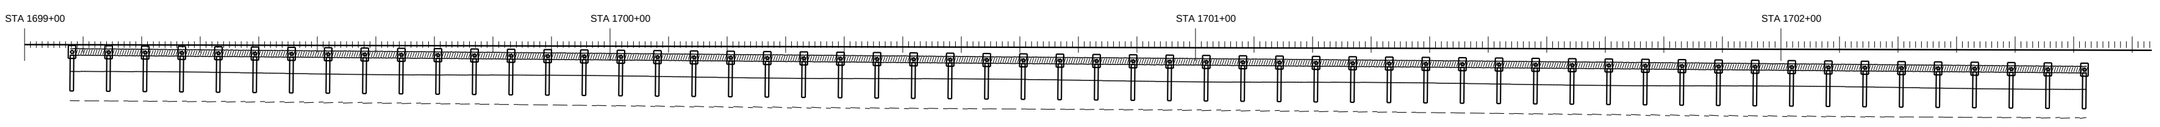


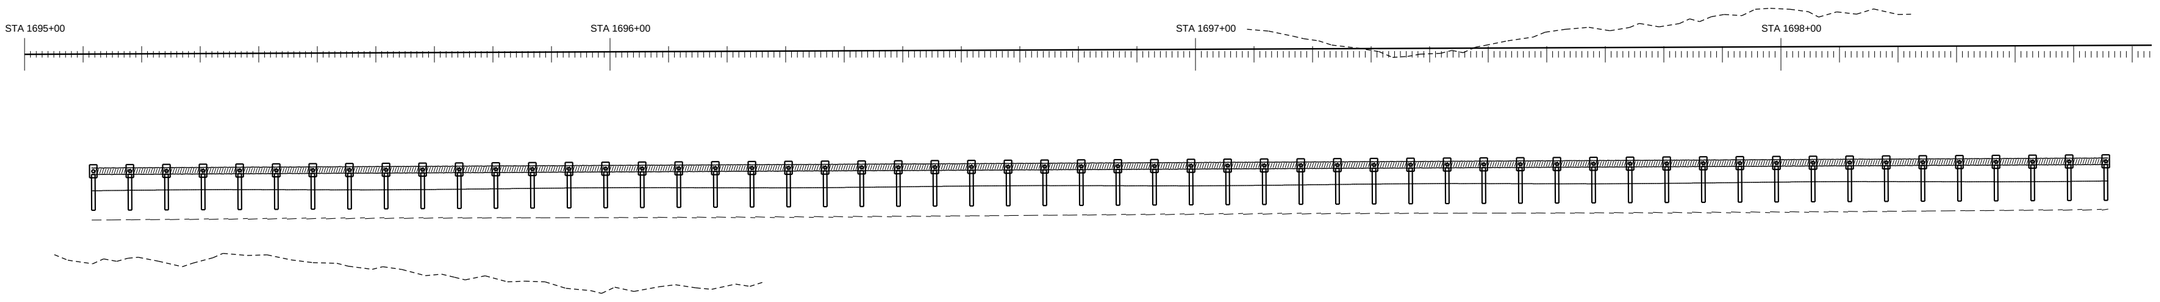


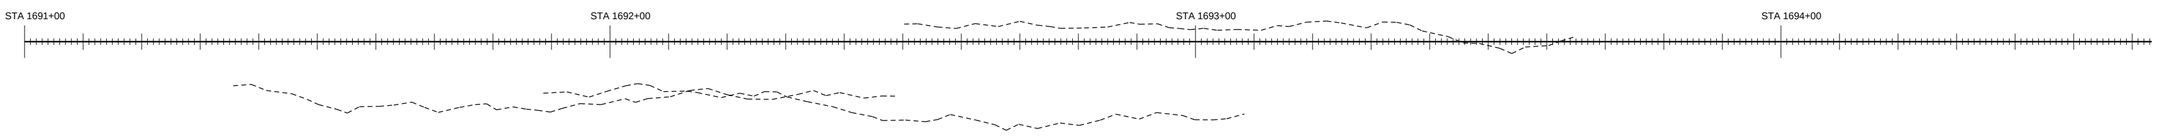


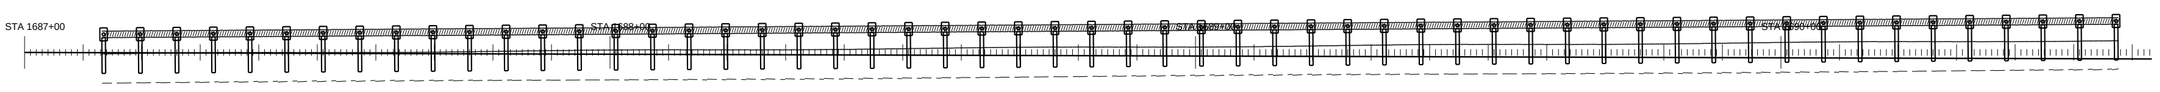


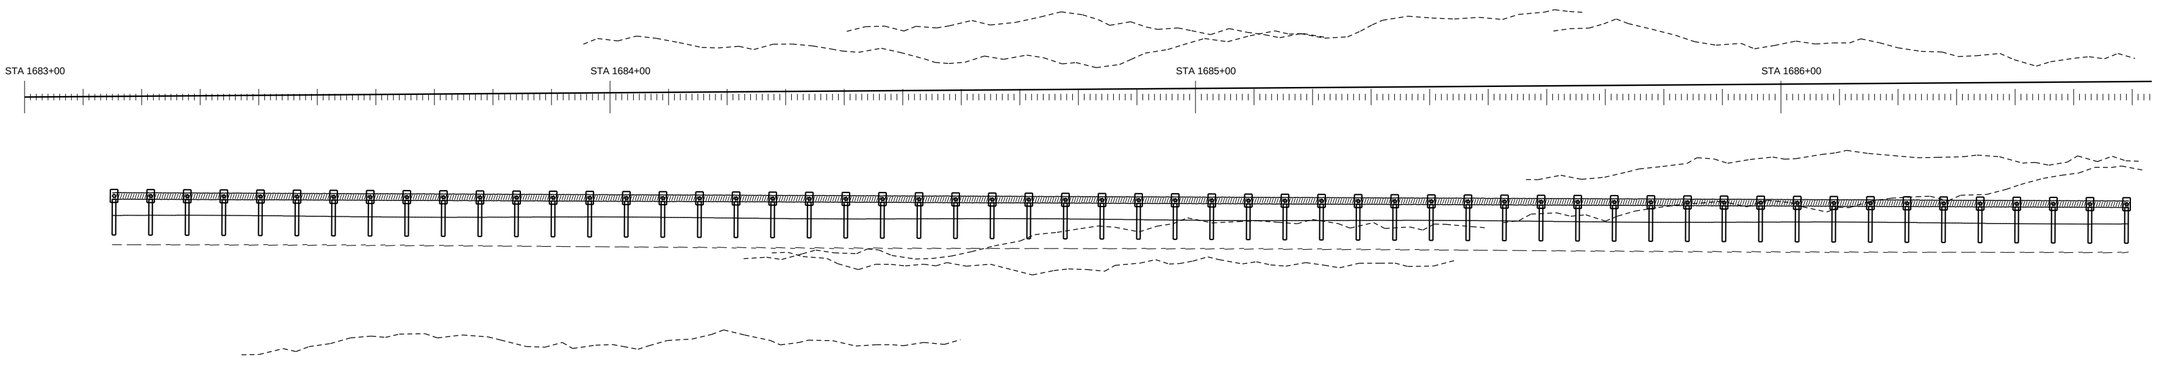


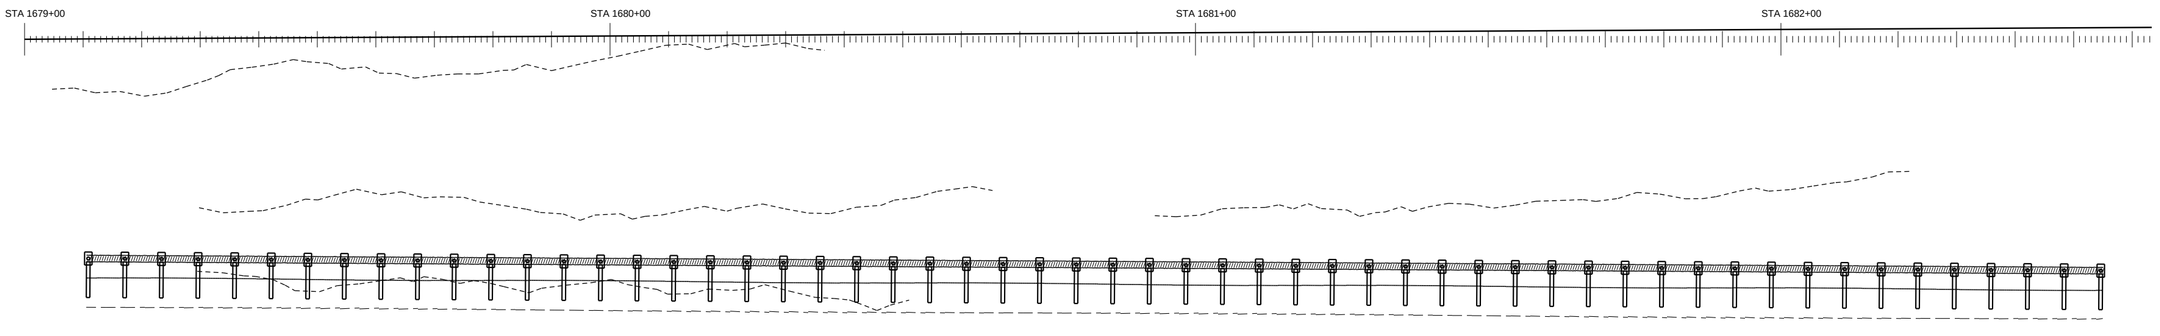


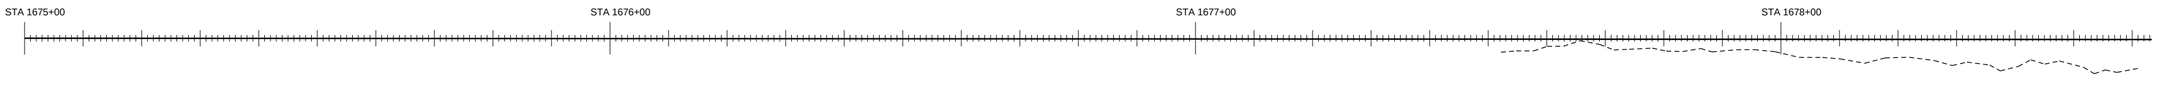


PAY ITEM 536-1-1 GUARDRAIL ROADWAY (TL-3)

PAY ITEM 536-85-24 END TREATMENT

GUARANTEED FENCE CORP

FIN. PROJ. ID 441234-1-52-01

SHEET 106 OF 120

SHEET NO. 206

ROADWAY PLAN SCALE: 1" = 20'

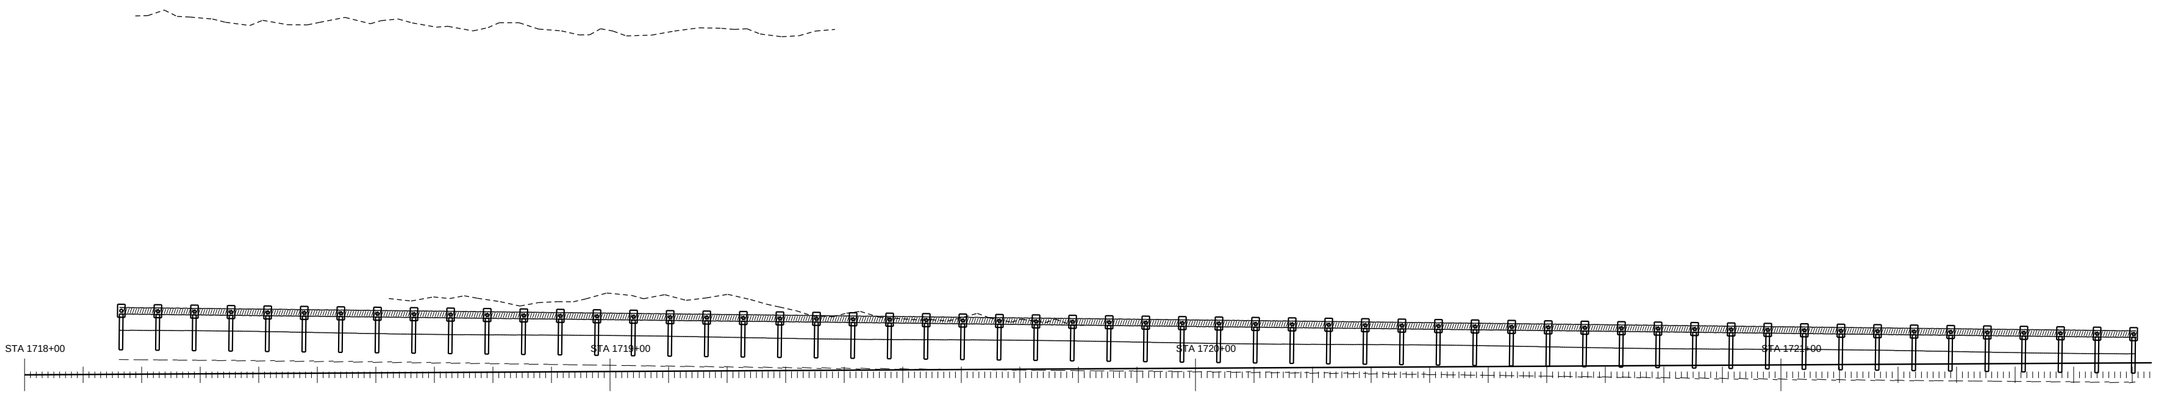


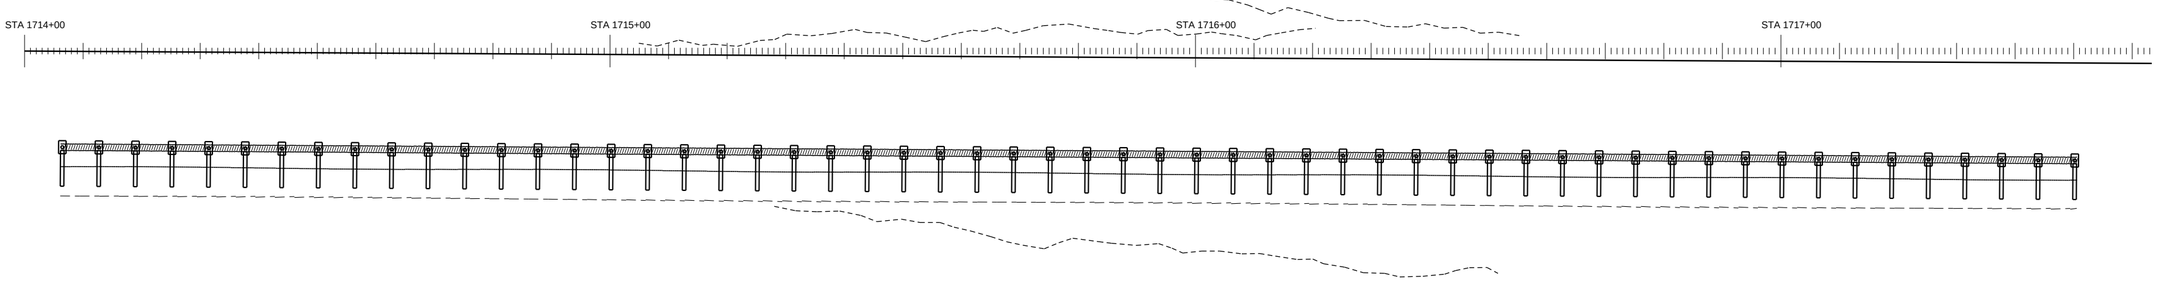


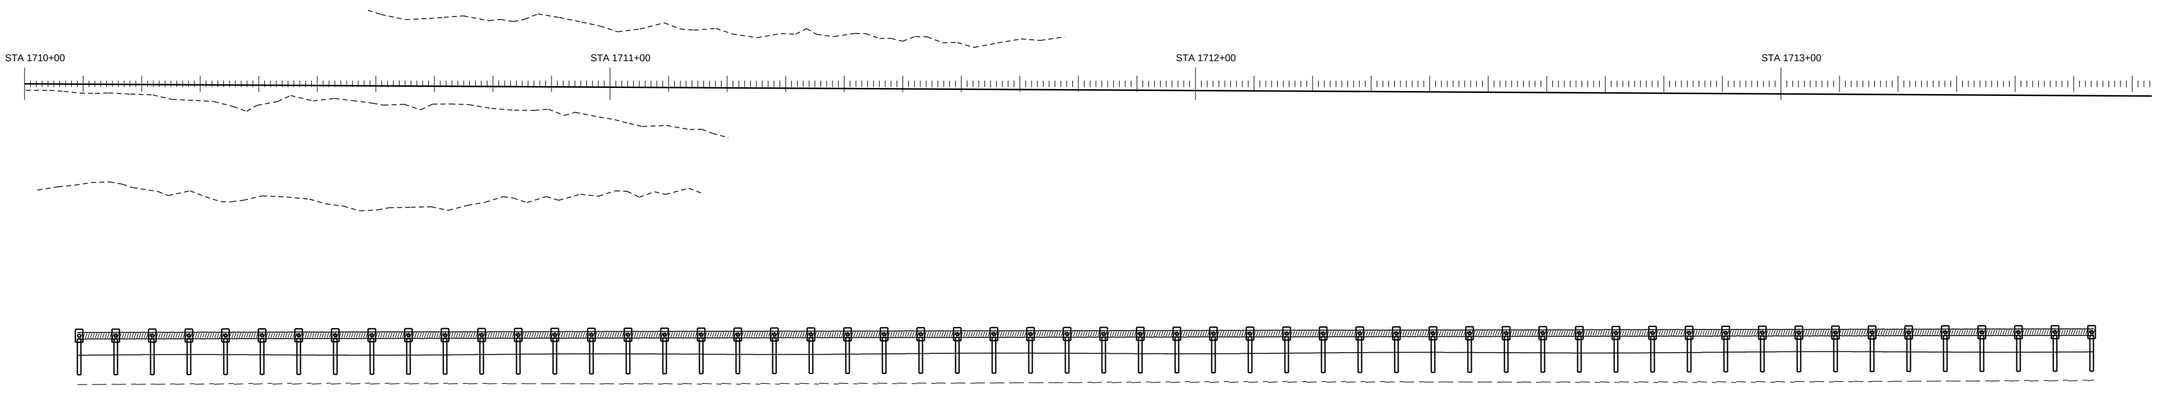


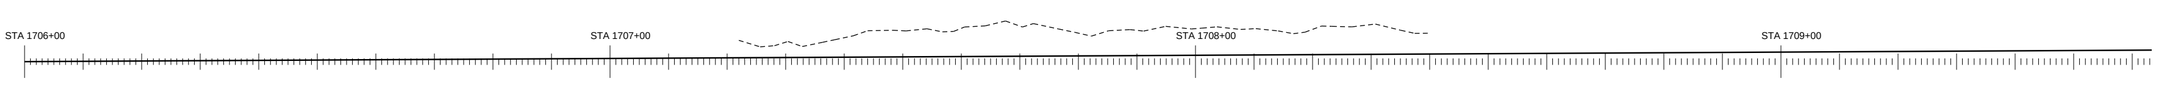


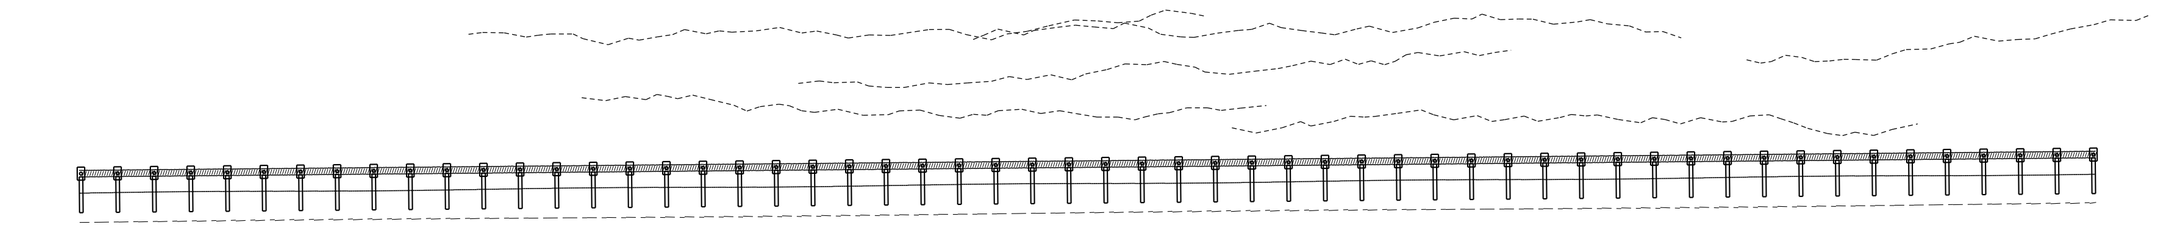


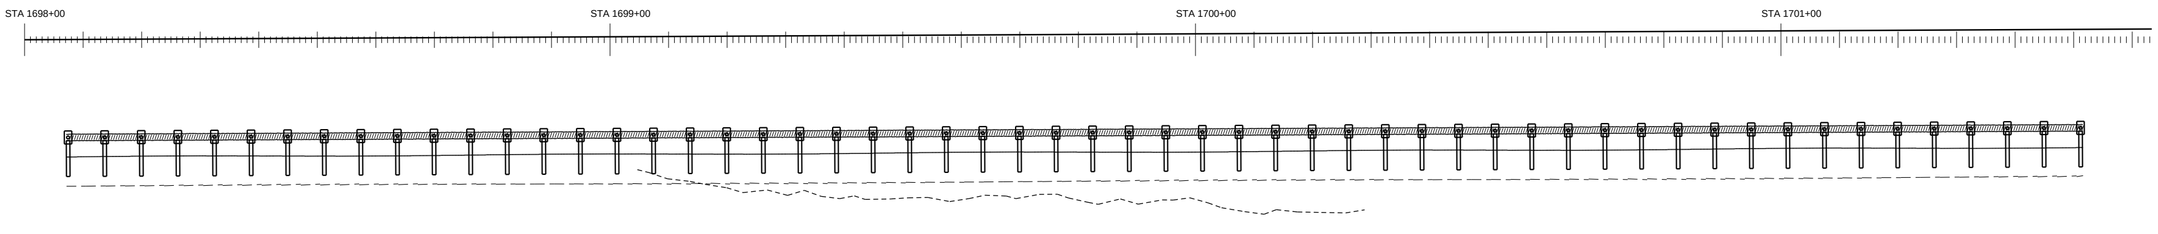


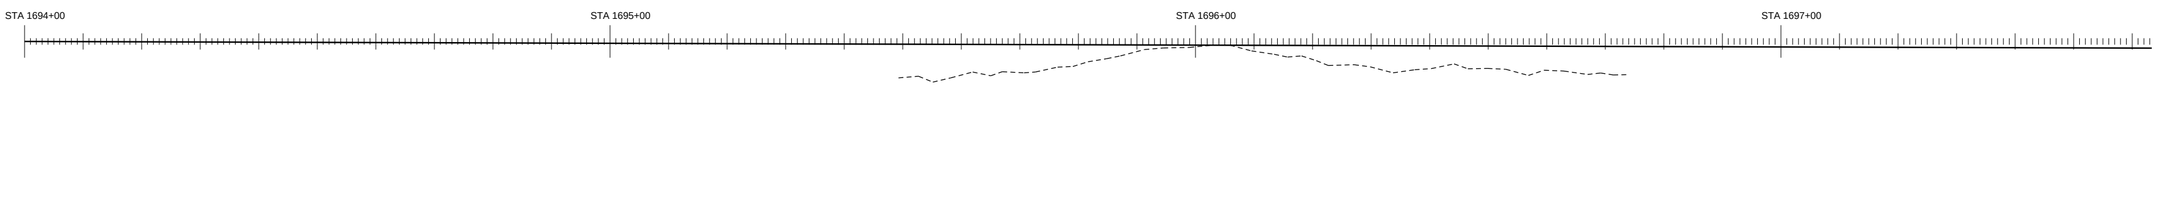


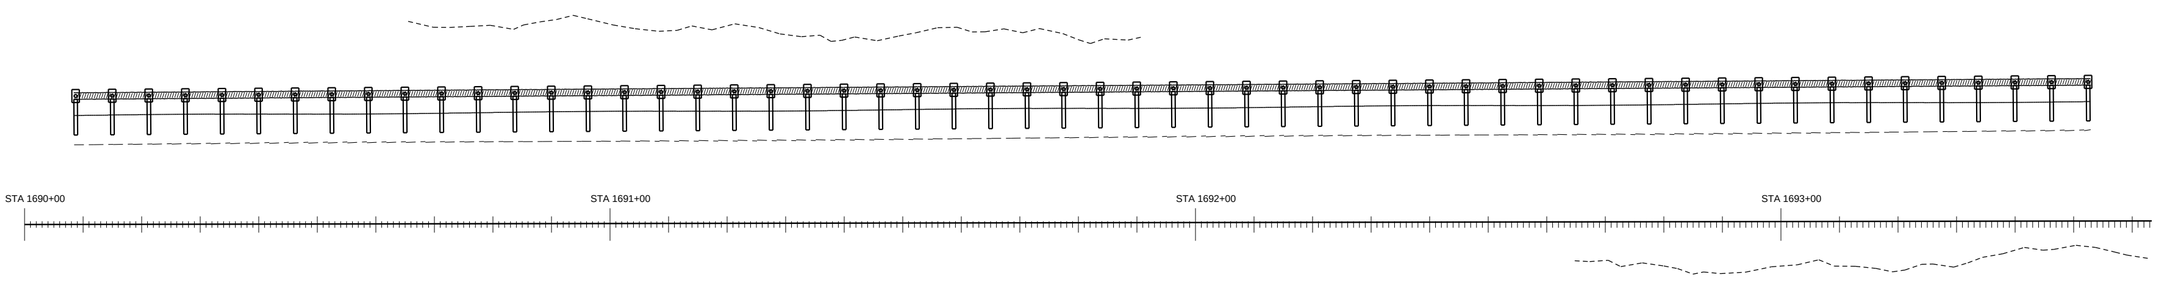


PAY ITEM 536-1-1 GUARDRAIL ROADWAY (TL-3)

PAY ITEM 536-85-24 END TREATMENT

GUARANTEED FENCE CORP

FIN. PROJ. ID 441234-1-52-01

SHEET 107 OF 120

SHEET NO. 207

ROADWAY PLAN SCALE: 1" = 20'




PAY ITEM 536-1-1 GUARDRAIL ROADWAY (TL-3)

PAY ITEM 536-85-24 END TREATMENT

GUARANTEED FENCE CORP

FIN. PROJ. ID 441234-1-52-01

SHEET 108 OF 120

SHEET NO. 208

ROADWAY PLAN SCALE: 1" = 20'

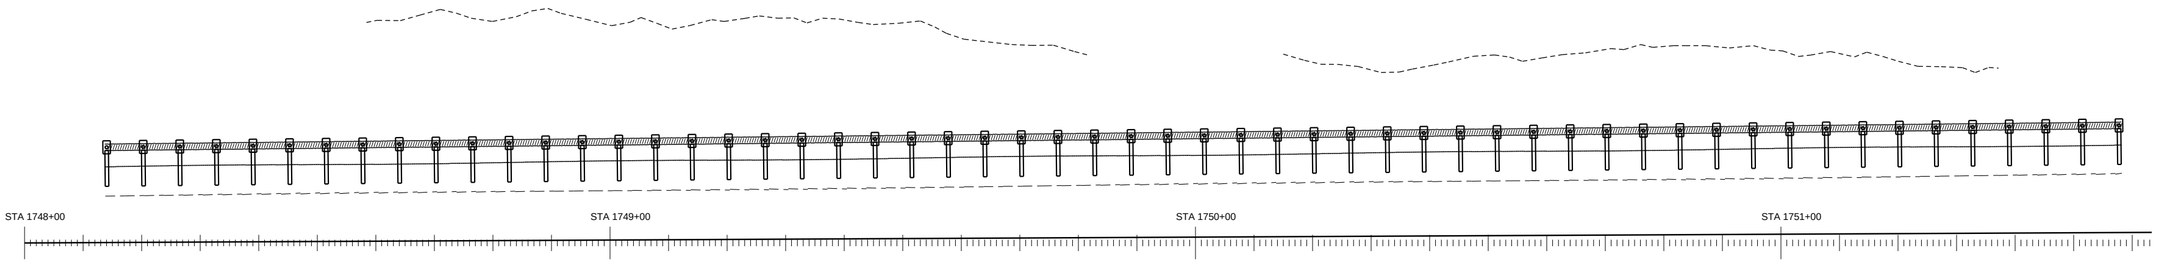


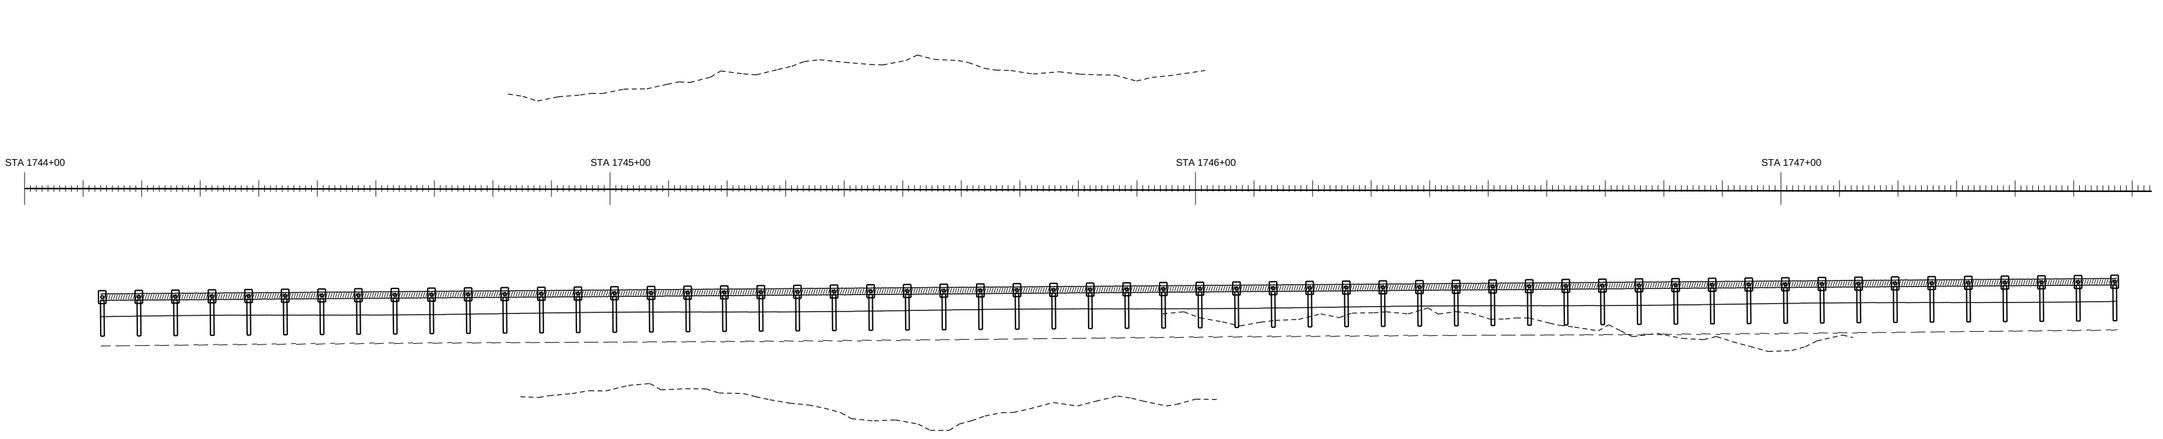


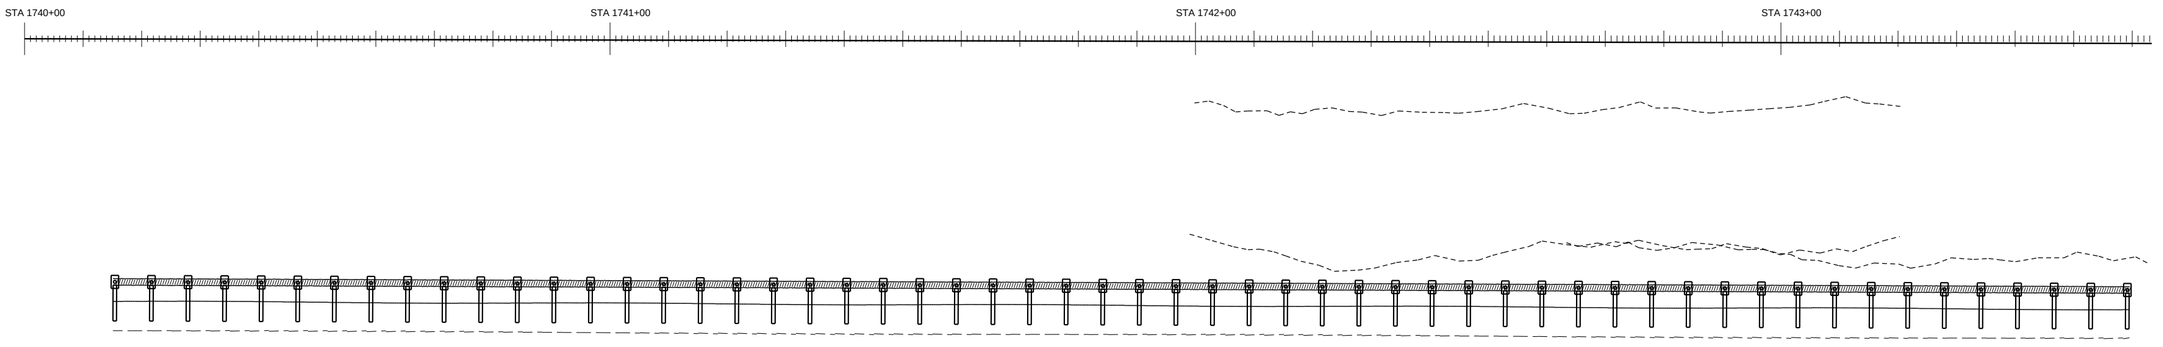


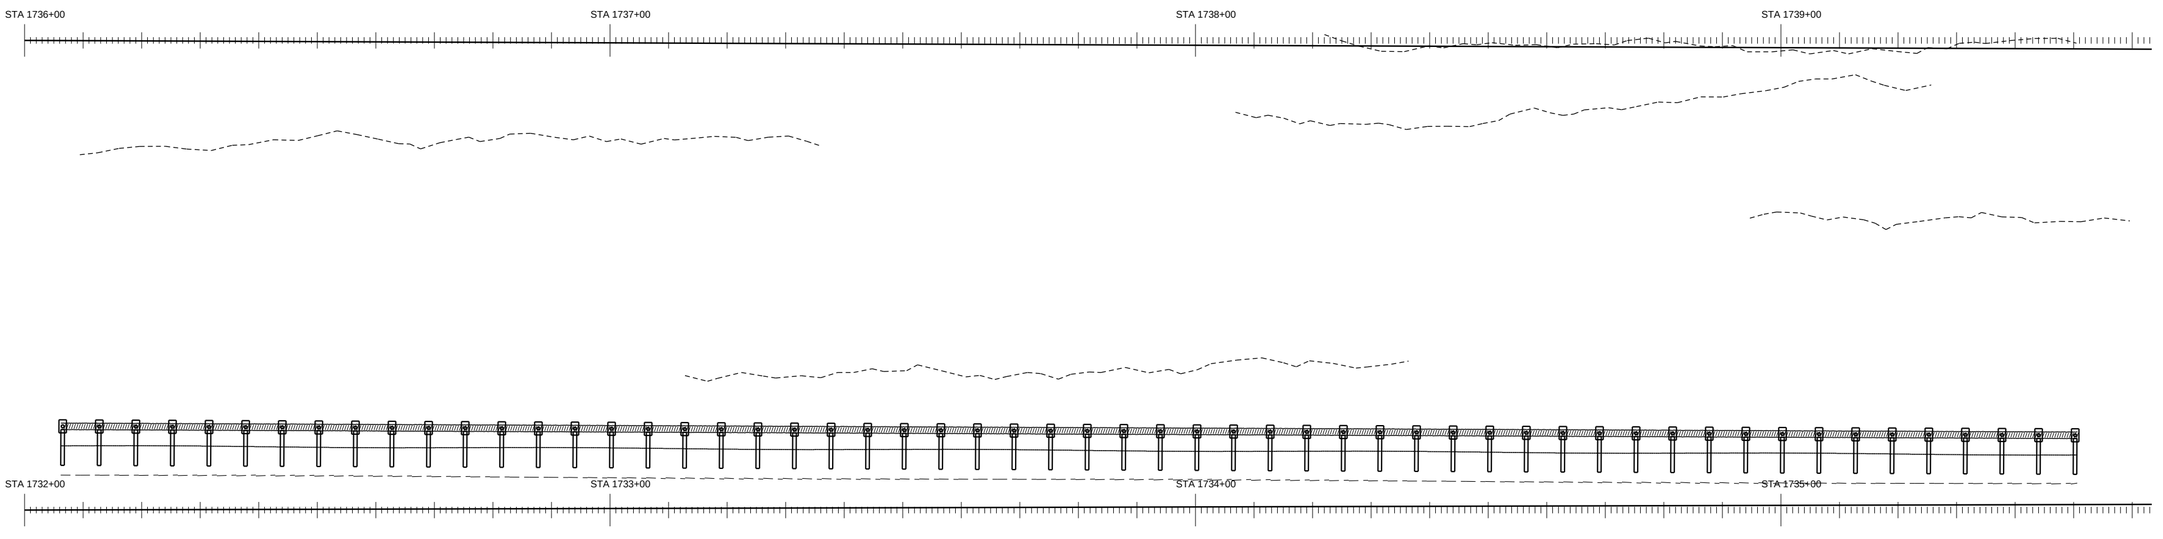


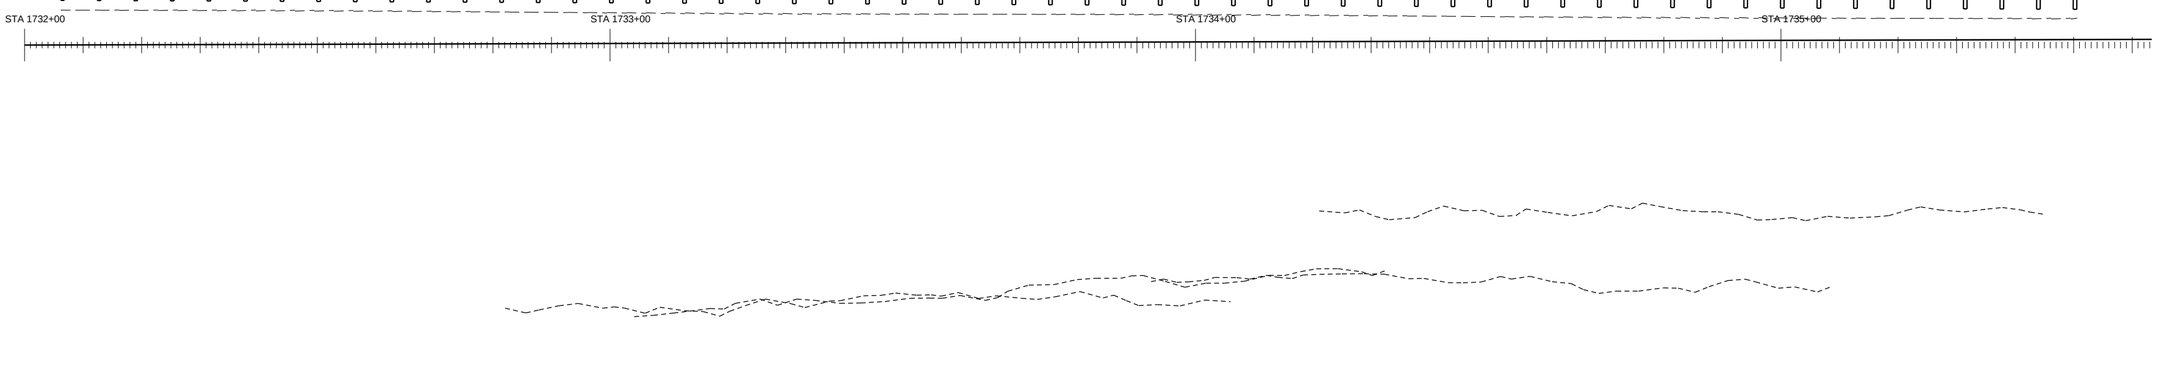


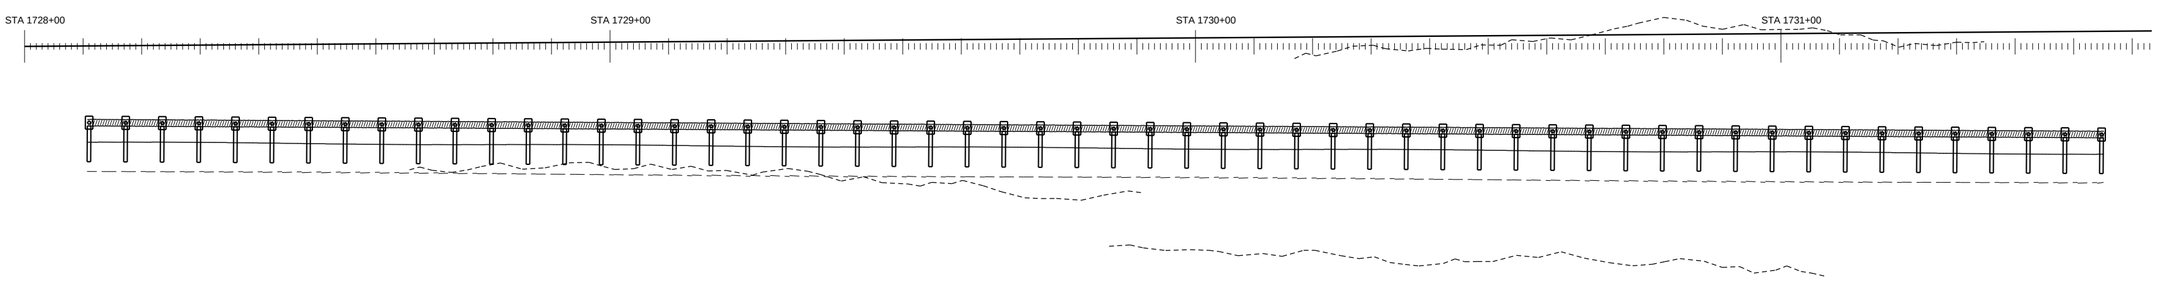


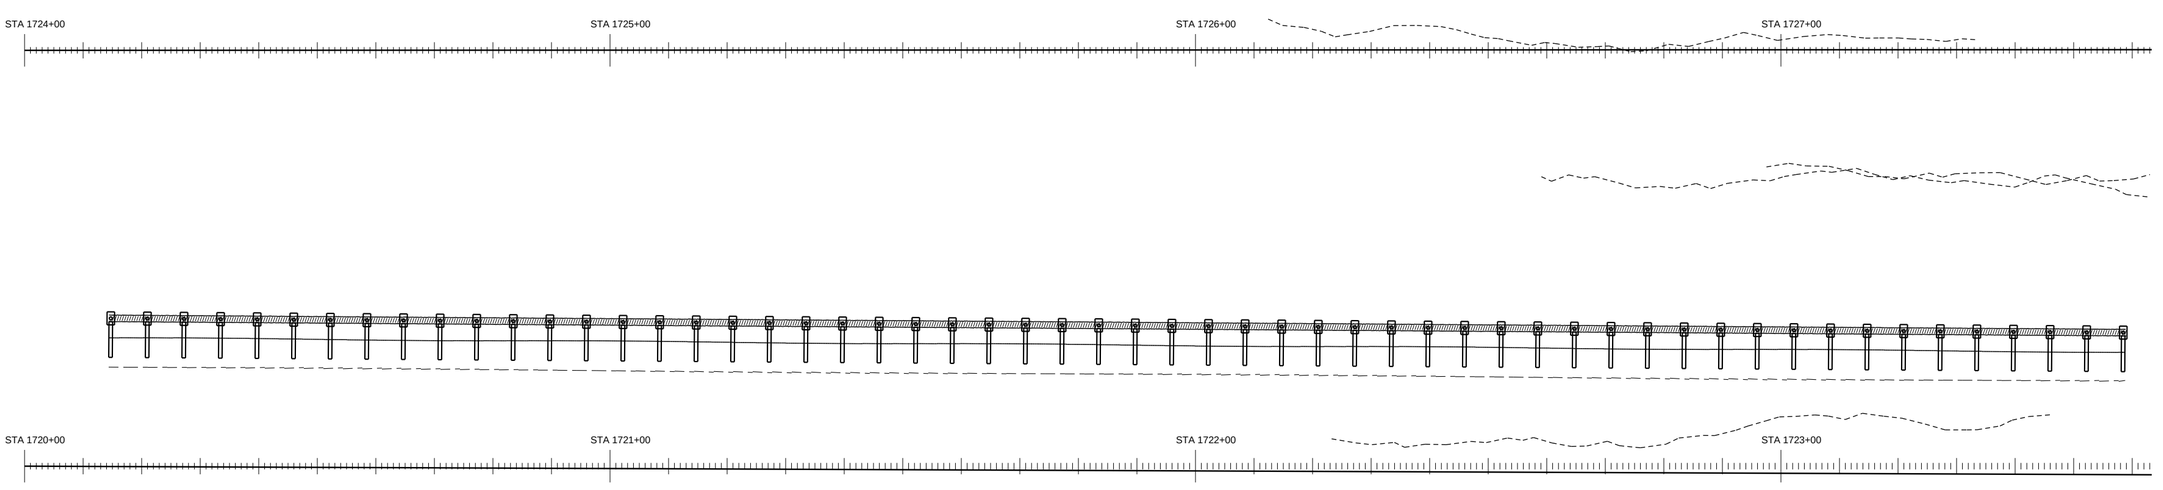


PAY ITEM 536-1-1 GUARDRAIL ROADWAY (TL-3)

PAY ITEM 536-85-24 END TREATMENT

GUARANTEED FENCE CORP

FIN. PROJ. ID 441234-1-52-01

SHEET 109 OF 120

SHEET NO. 209

ROADWAY PLAN SCALE: 1" = 20'




PAY ITEM 536-1-1 GUARDRAIL ROADWAY (TL-3)

PAY ITEM 536-85-24 END TREATMENT

GUARANTEED FENCE CORP

FIN. PROJ. ID 441234-1-52-01

SHEET 110 OF 120

SHEET NO. 210

ROADWAY PLAN SCALE: 1" = 20'

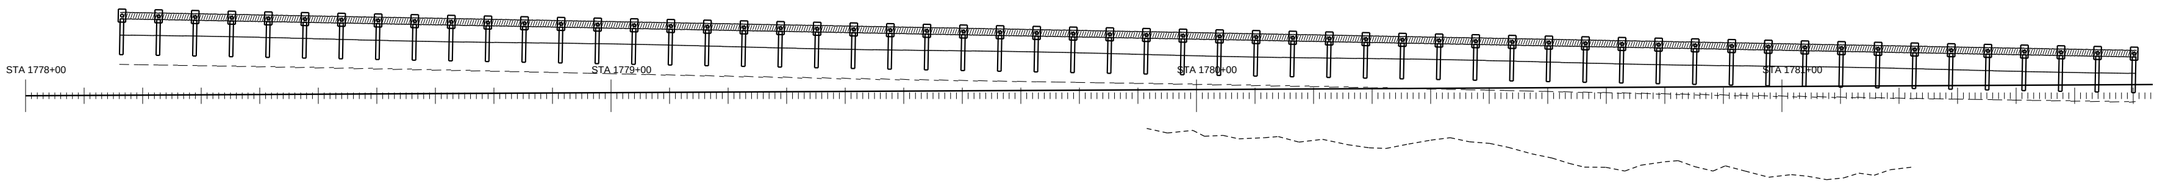


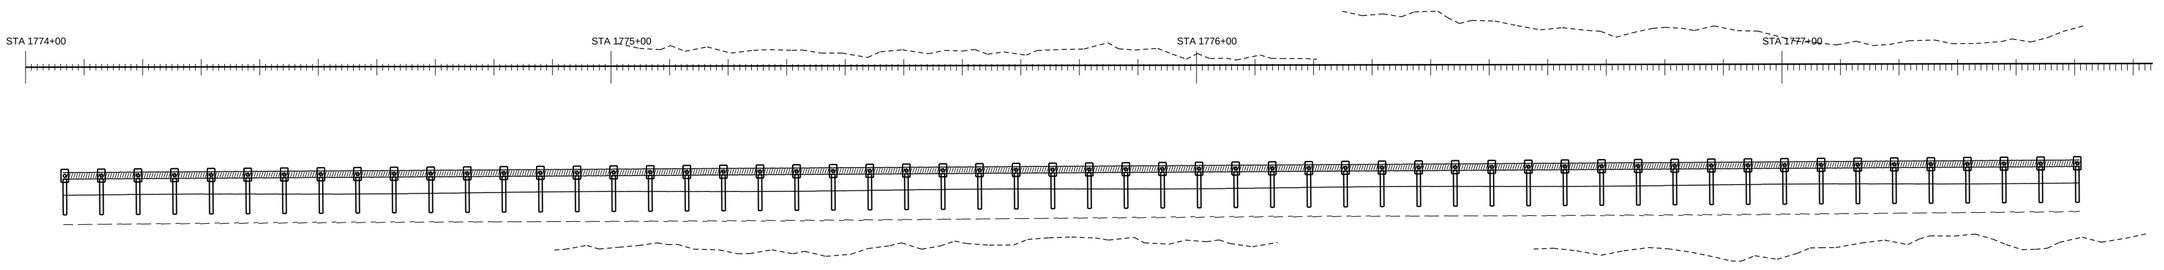


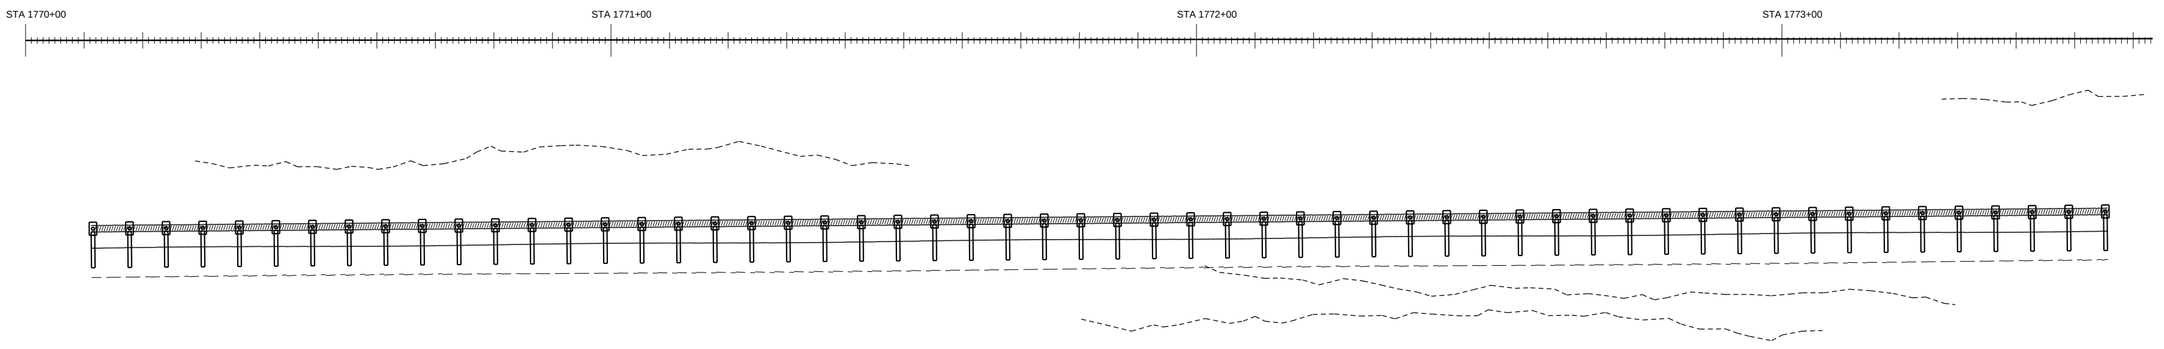


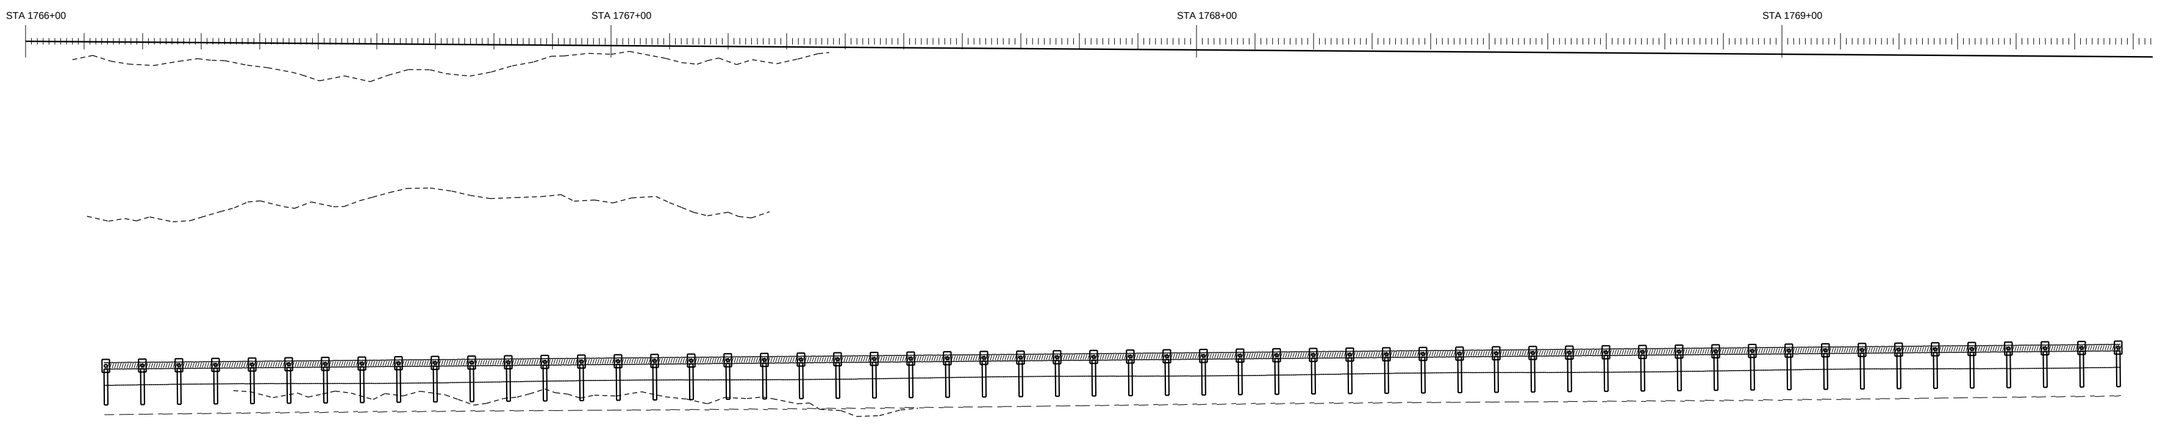


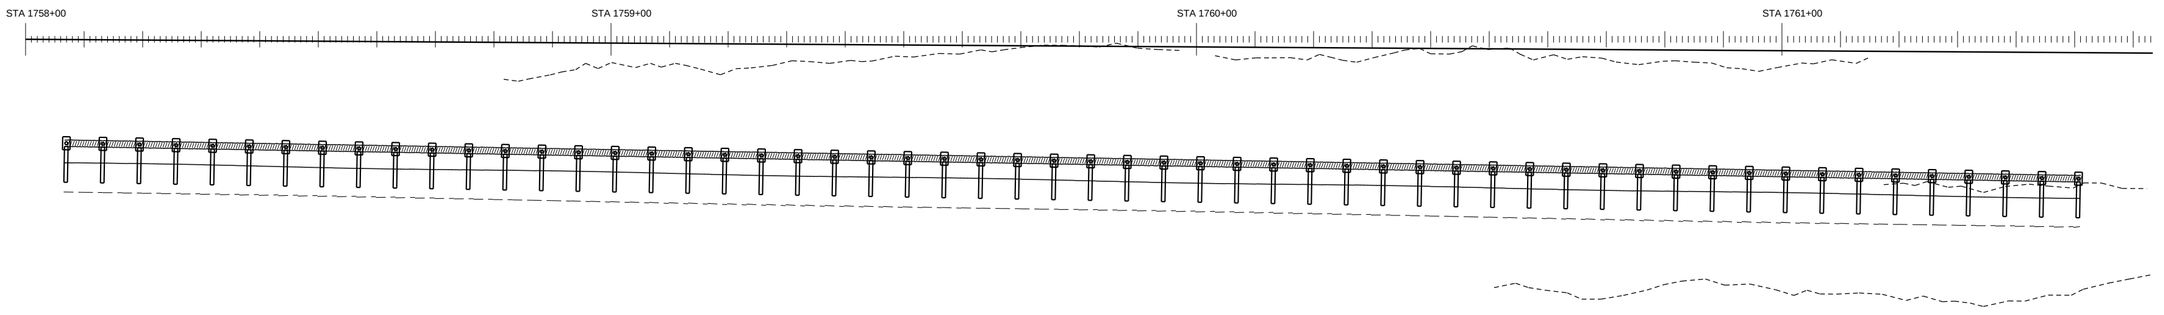


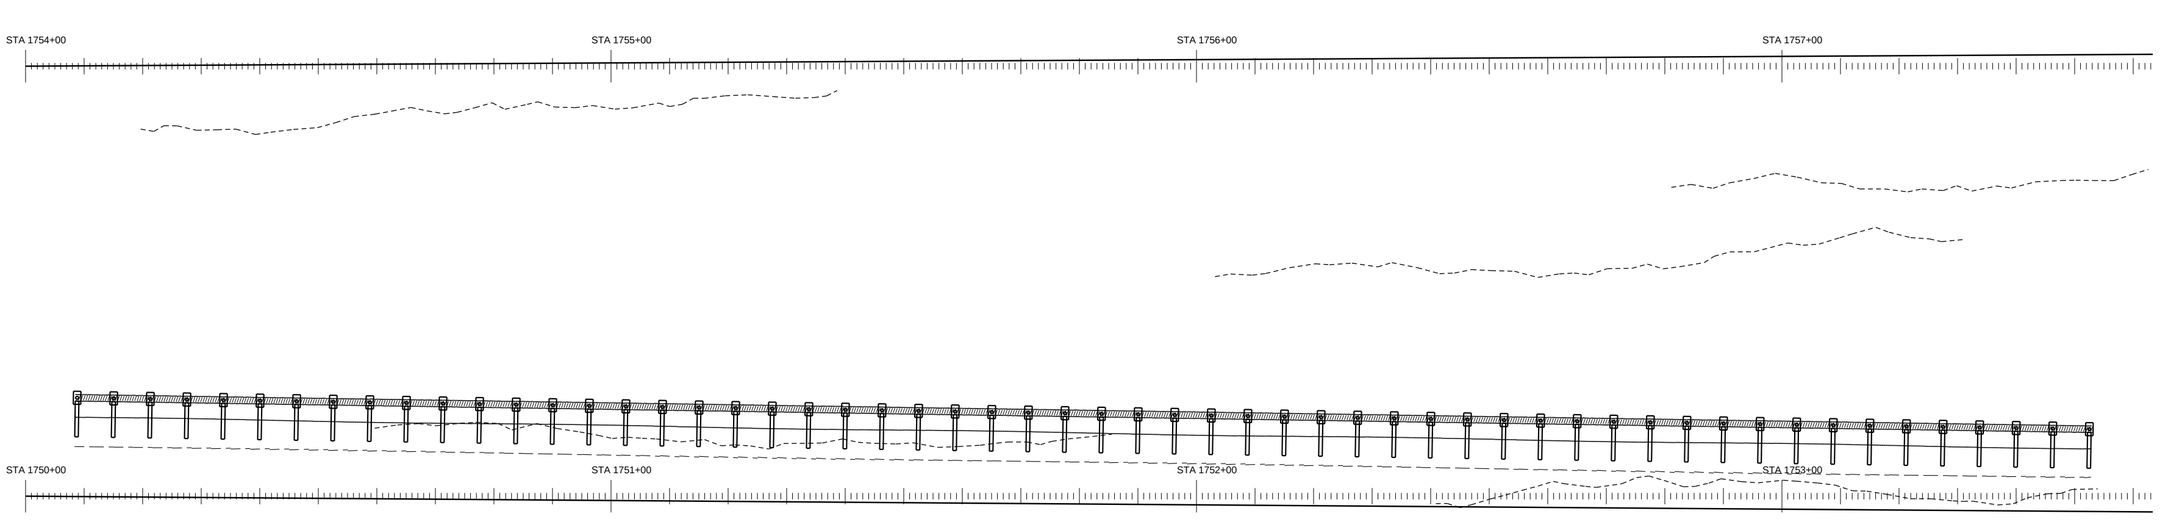


PAY ITEM 536-1-1 GUARDRAIL ROADWAY (TL-3)

PAY ITEM 536-85-24 END TREATMENT

GUARANTEED FENCE CORP

FIN. PROJ. ID 441234-1-52-01

SHEET 111 OF 120

SHEET NO. 211

ROADWAY PLAN SCALE: 1" = 20'




PAY ITEM 536-1-1 GUARDRAIL ROADWAY (TL-3)

PAY ITEM 536-85-24 END TREATMENT

GUARANTEED FENCE CORP

FIN. PROJ. ID 441234-1-52-01

SHEET 112 OF 120

SHEET NO. 212

ROADWAY PLAN SCALE: 1" = 20'

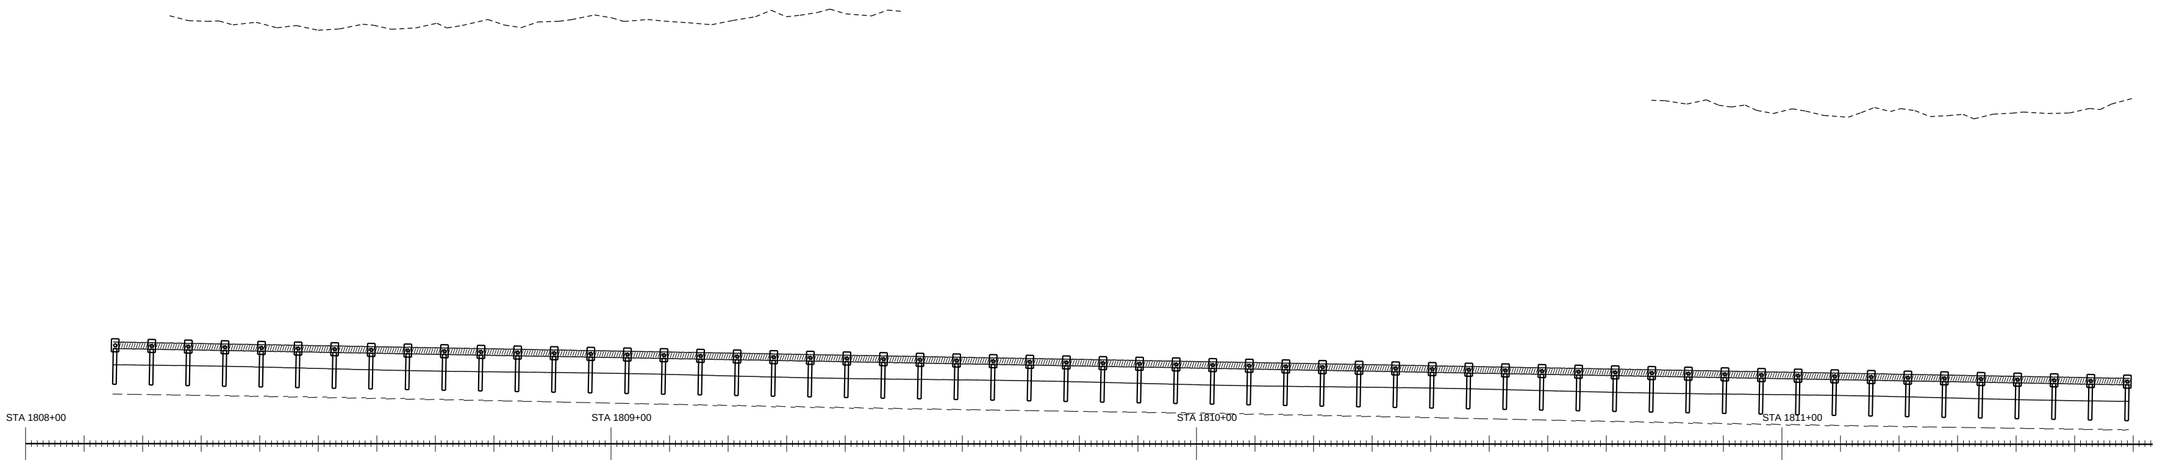


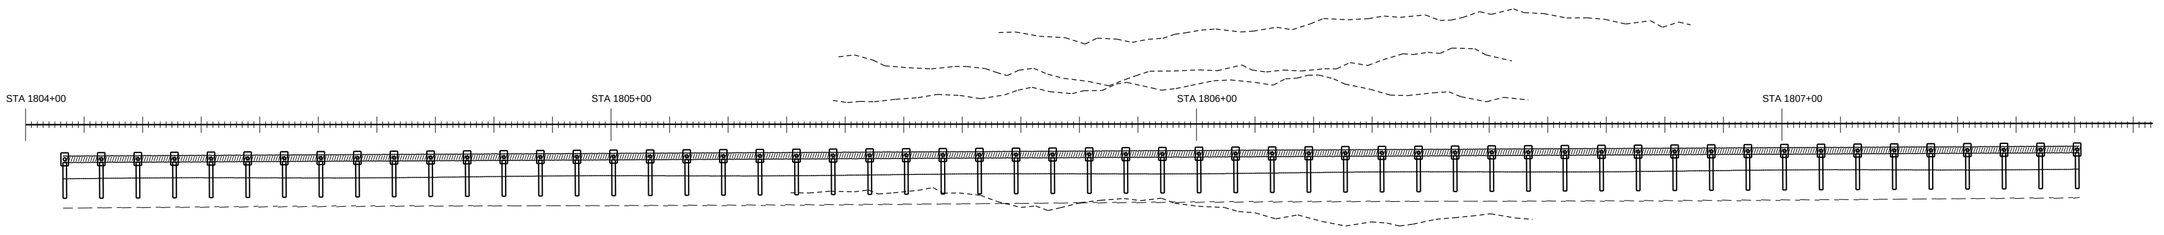


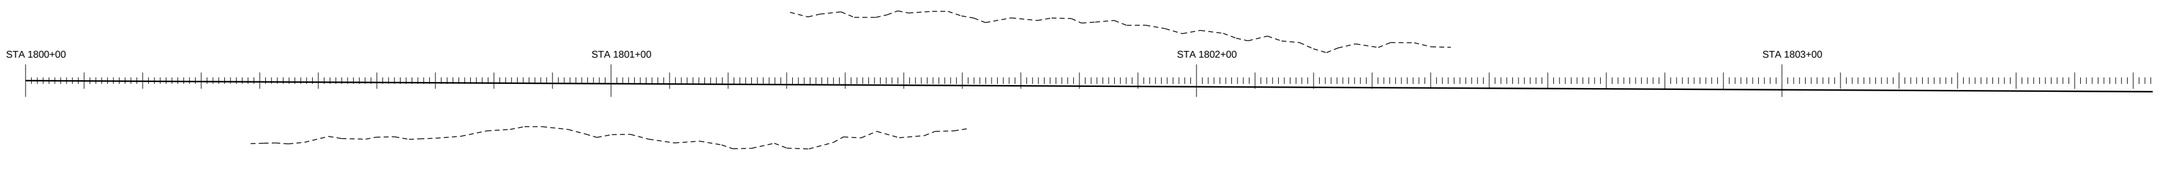


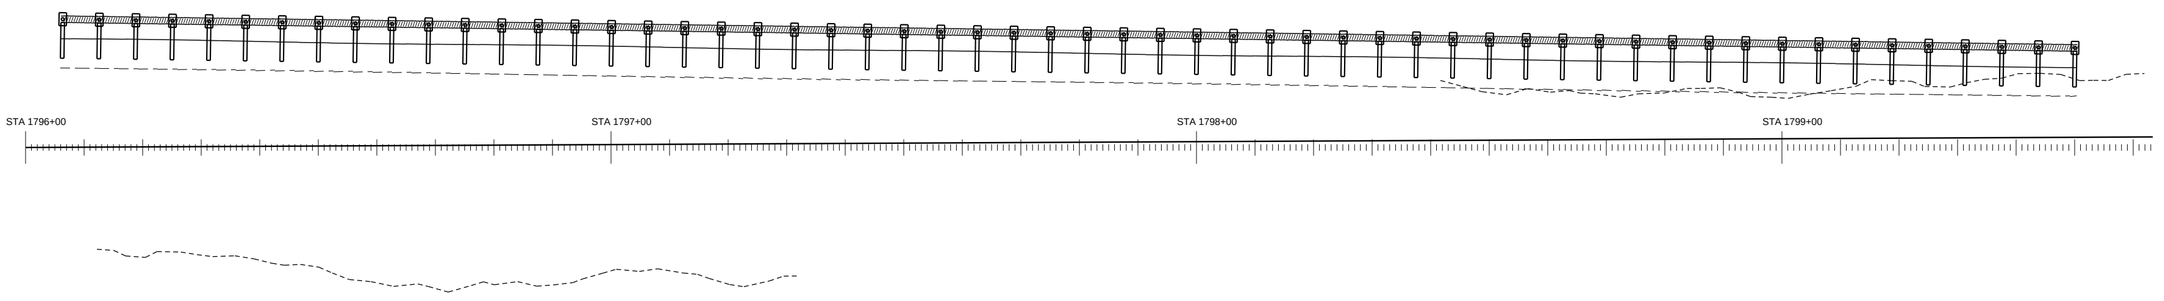


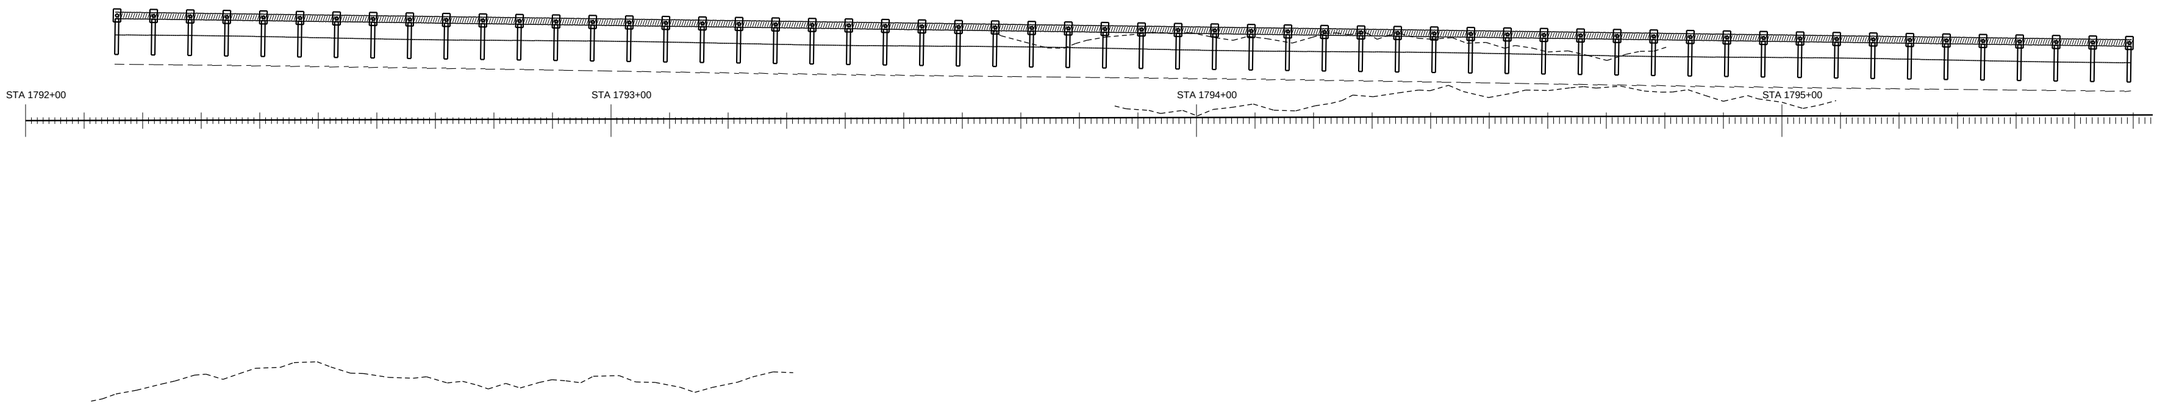


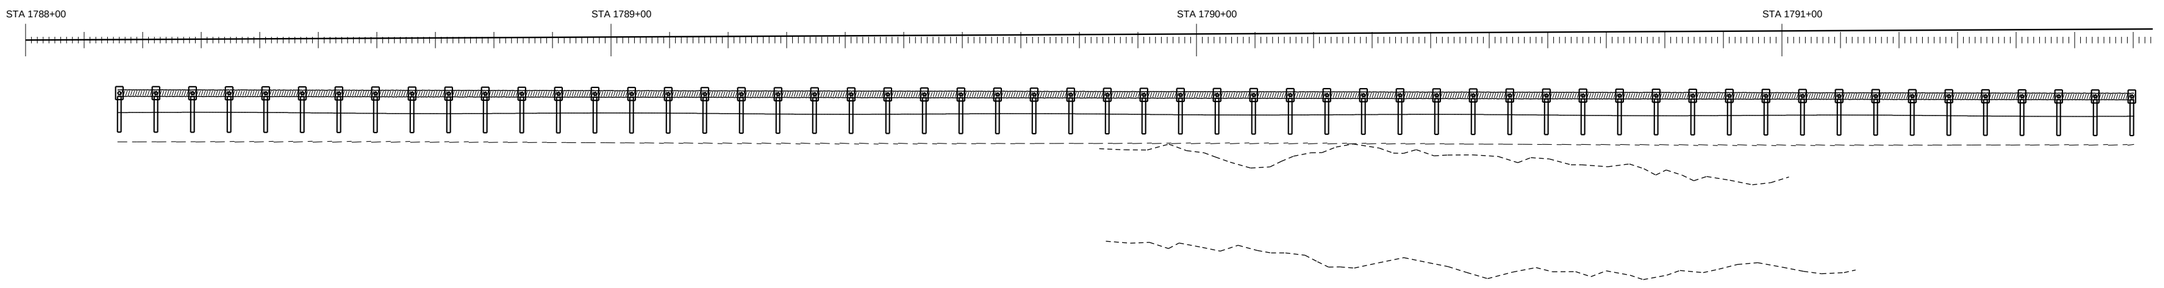


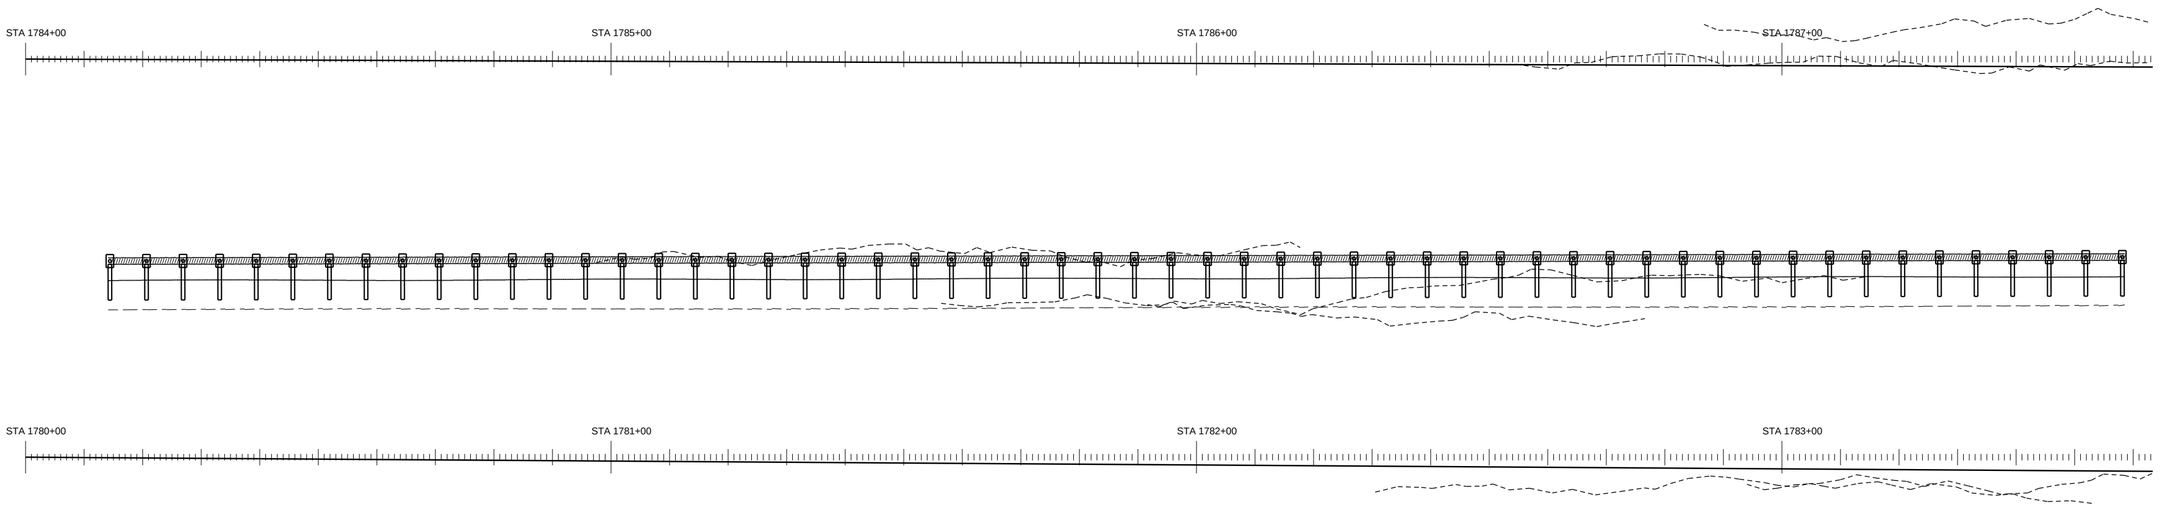





PAY ITEM 536-1-1 GUARDRAIL ROADWAY (TL-3)

PAY ITEM 536-85-24 END TREATMENT

GUARANTEED FENCE CORP

FIN. PROJ. ID 441234-1-52-01

SHEET 113 OF 120

SHEET NO. 213

ROADWAY PLAN SCALE: 1" = 20'

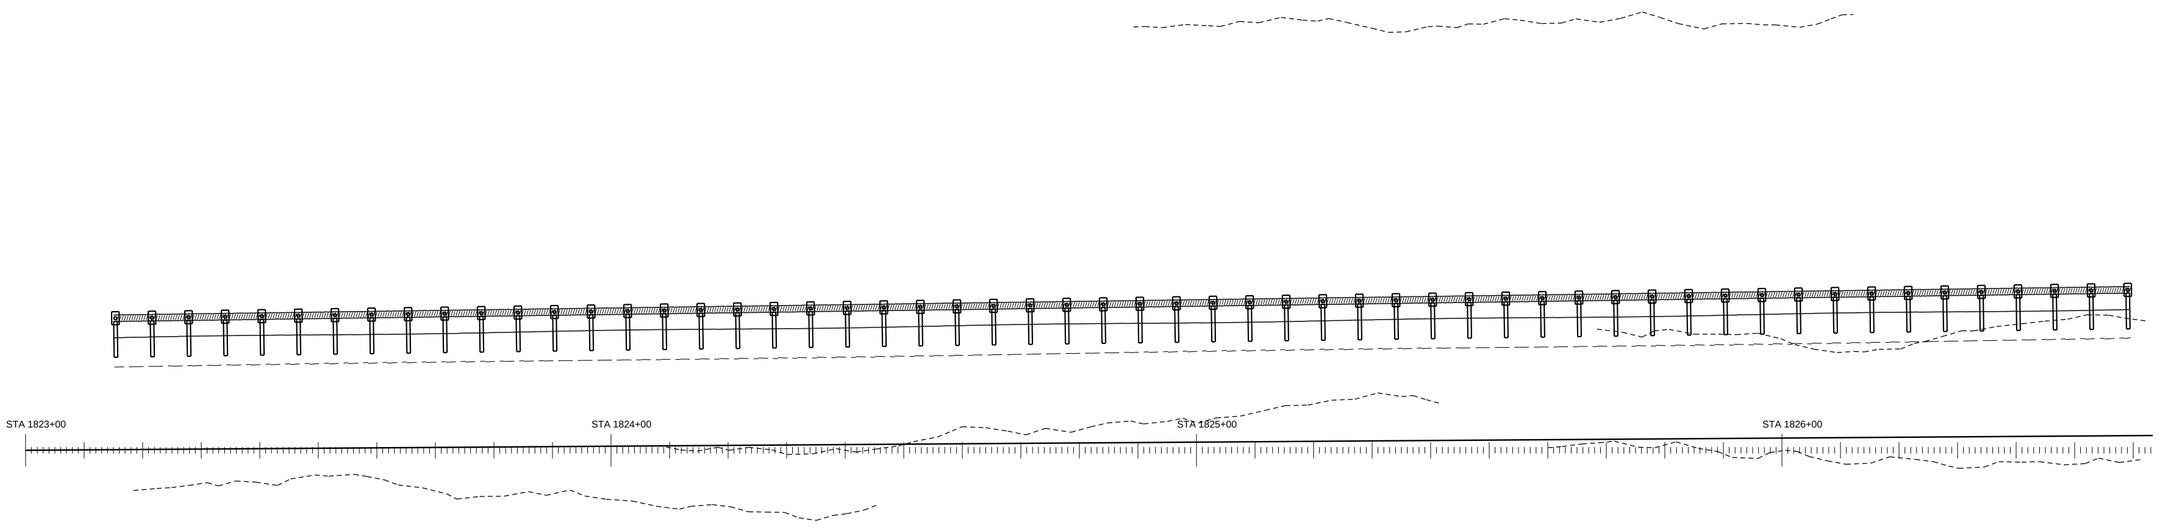


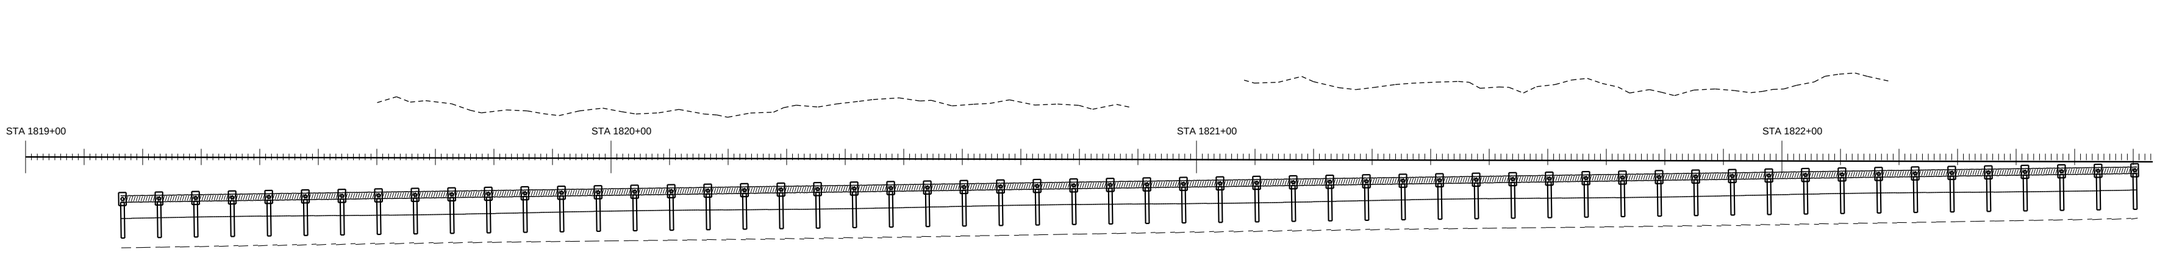


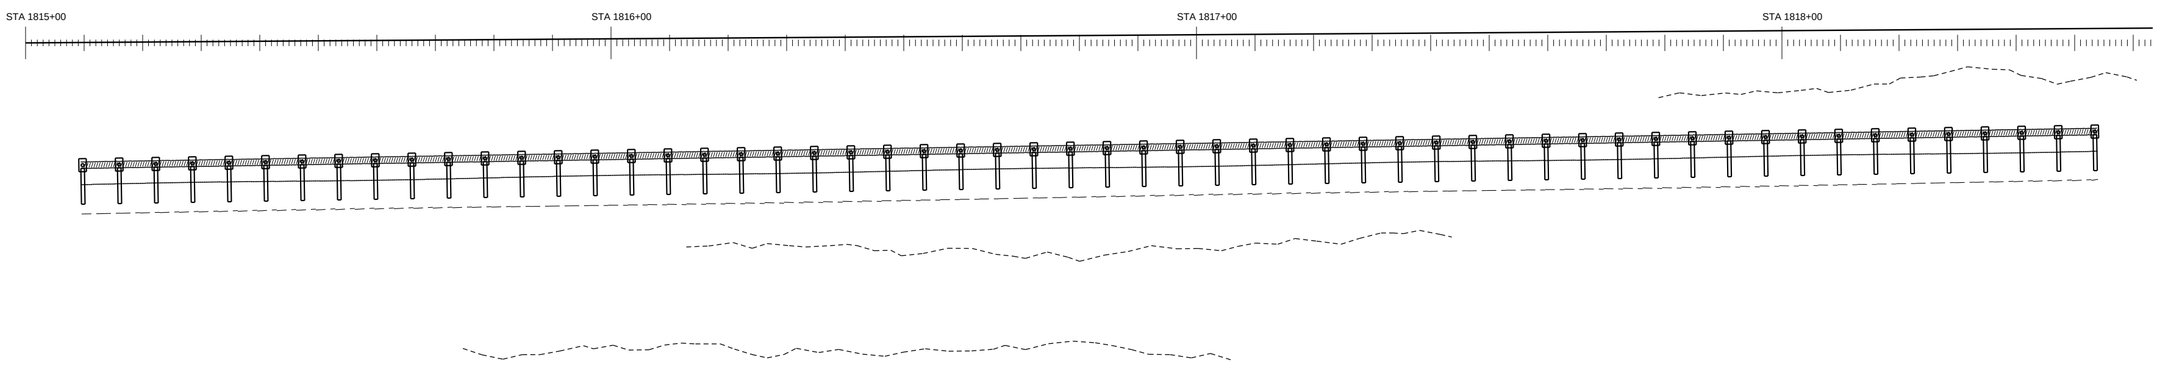


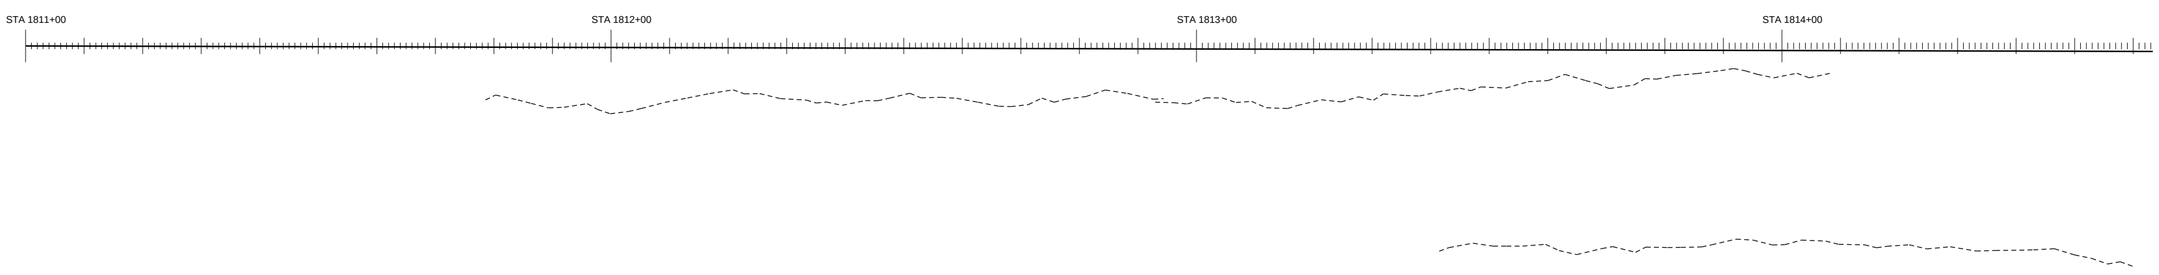


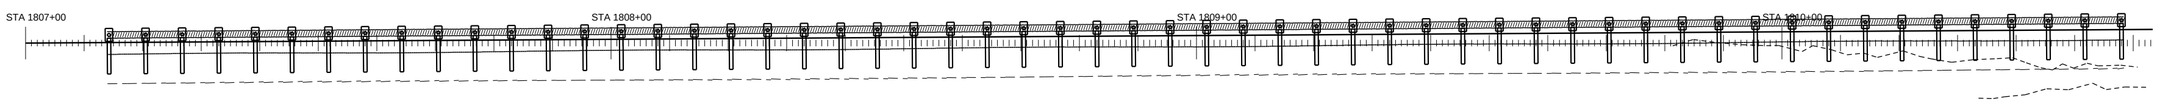


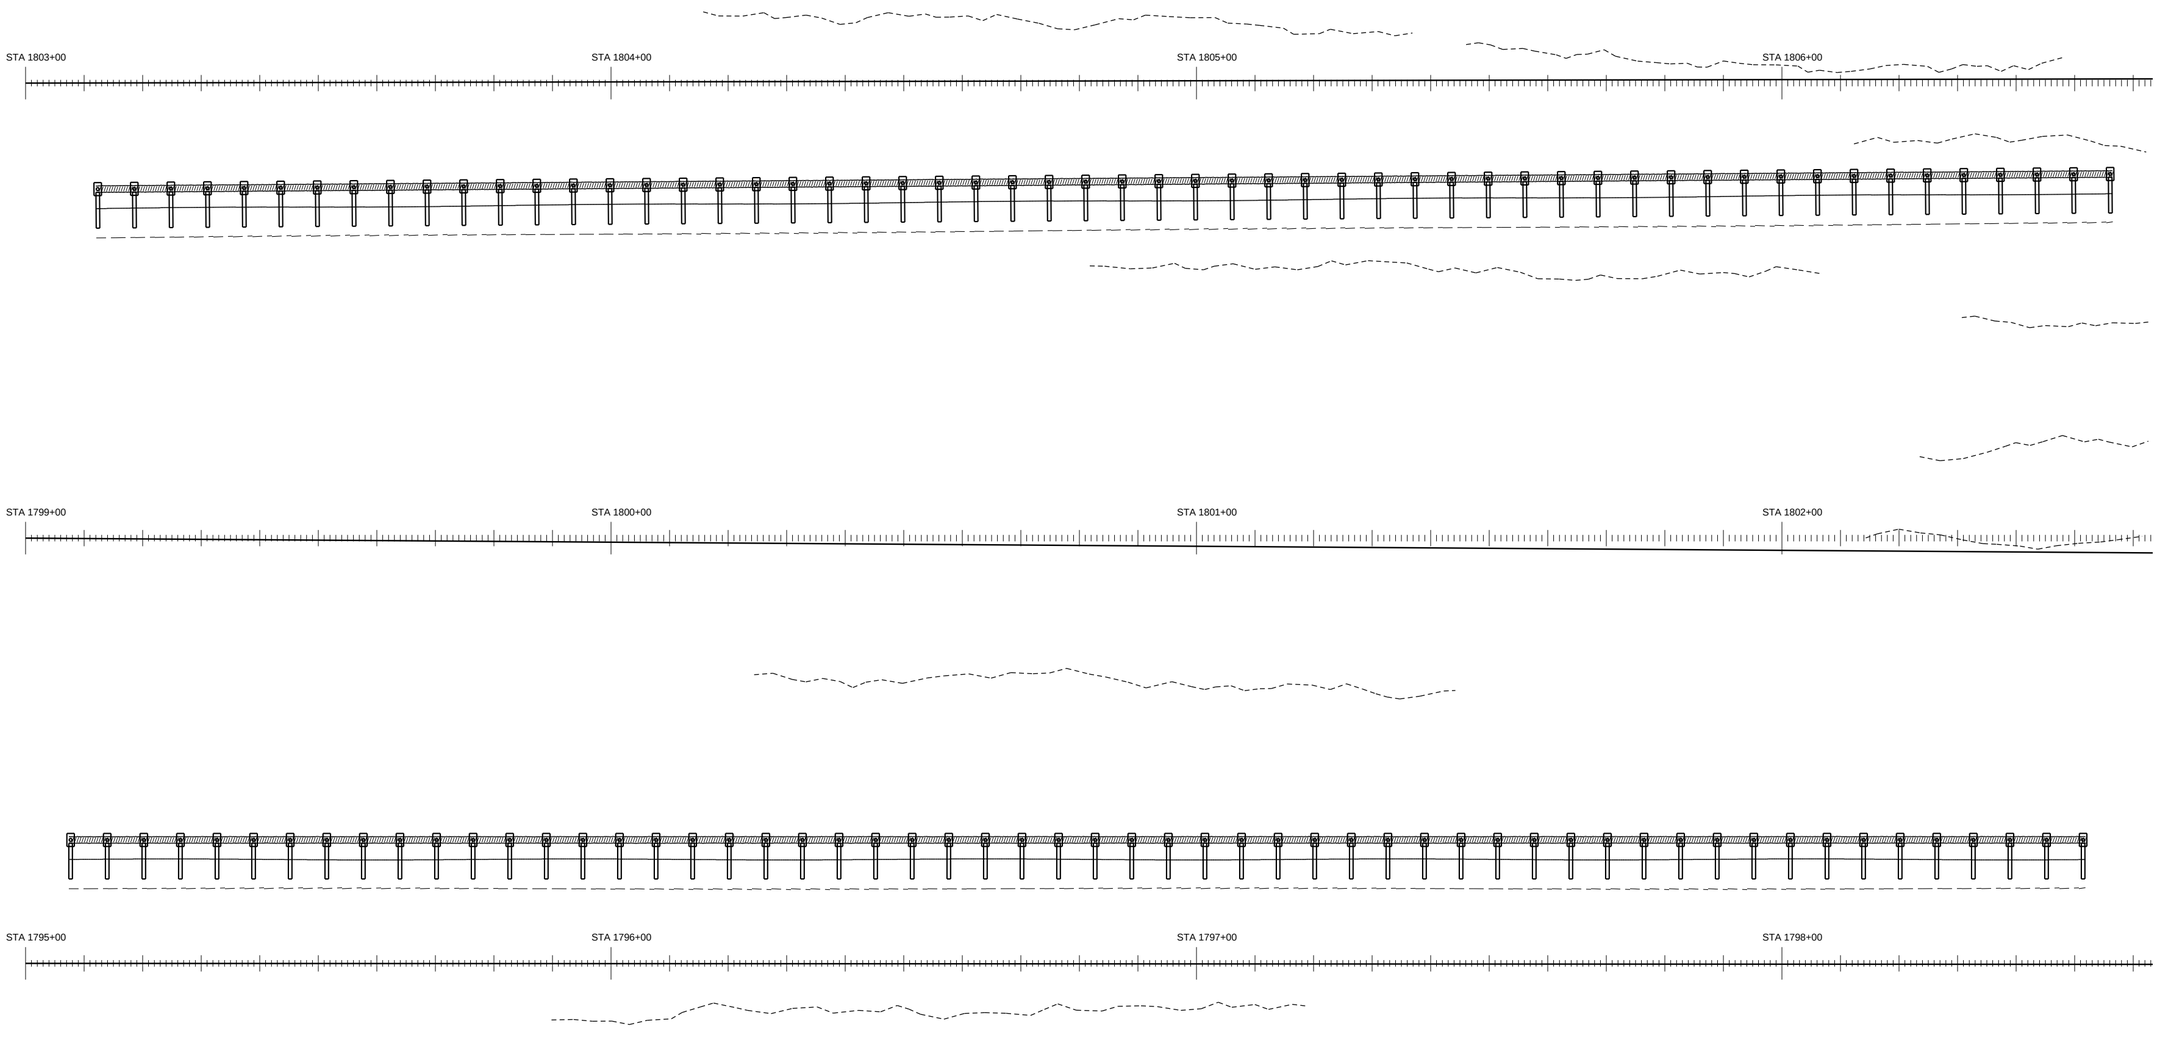








PAY ITEM 536-1-1 GUARDRAIL ROADWAY (TL-3)

PAY ITEM 536-85-24 END TREATMENT

GUARANTEED FENCE CORP

FIN. PROJ. ID 441234-1-52-01

SHEET 114 OF 120

SHEET NO. 214

ROADWAY PLAN SCALE: 1" = 20'

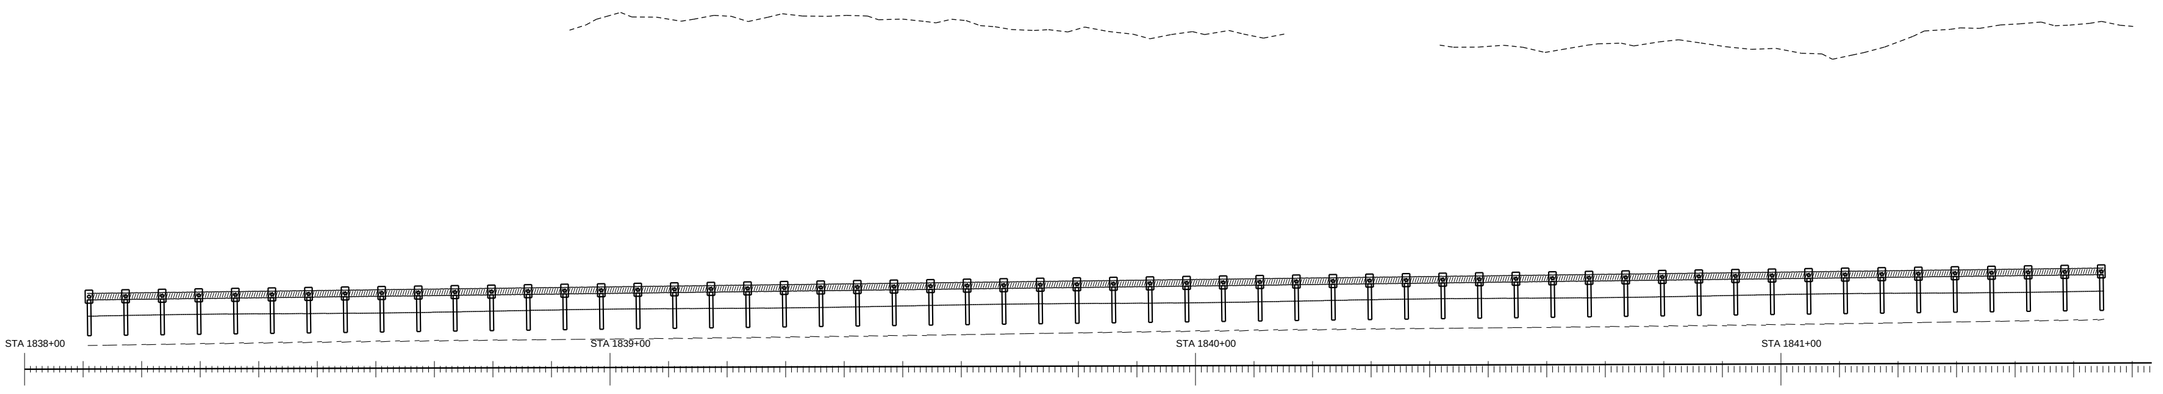


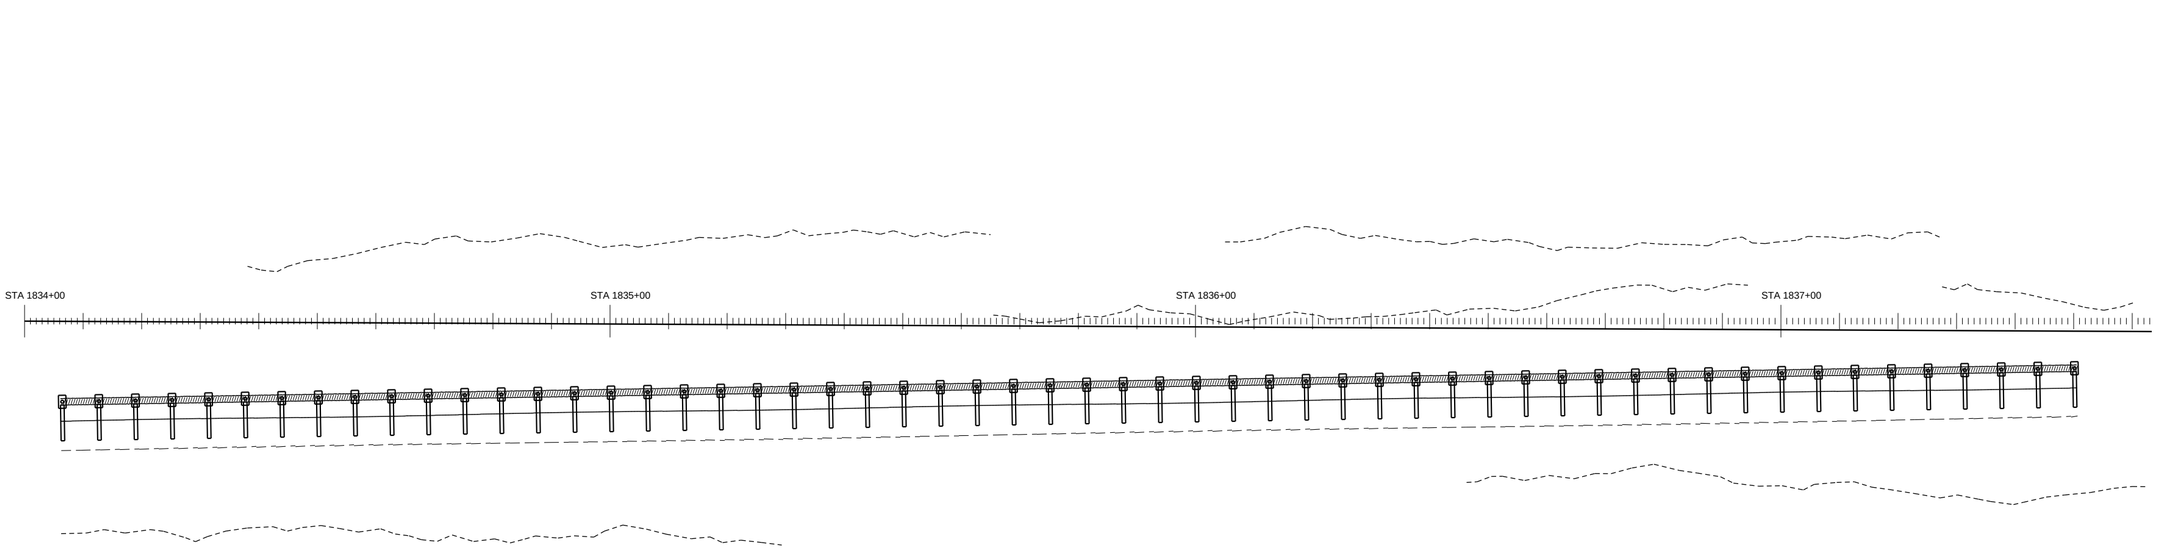


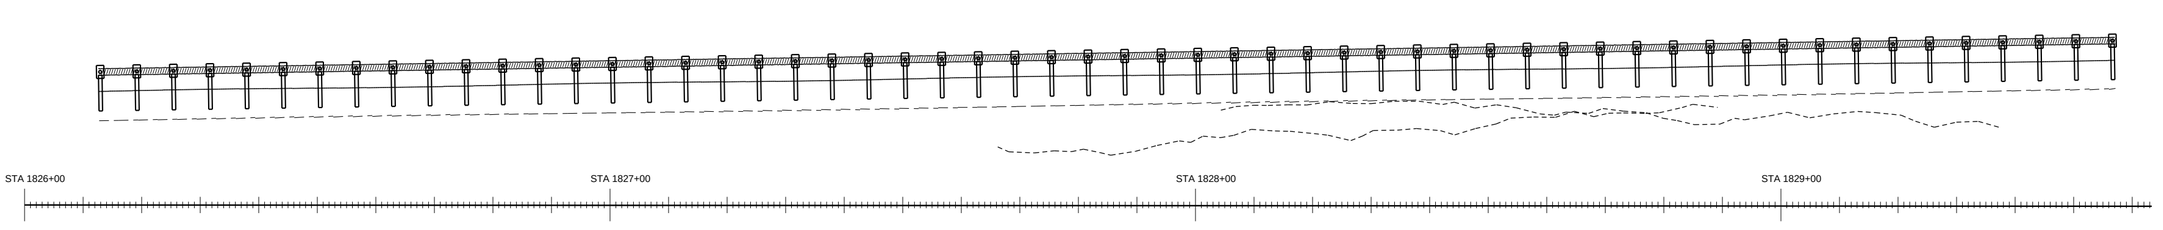


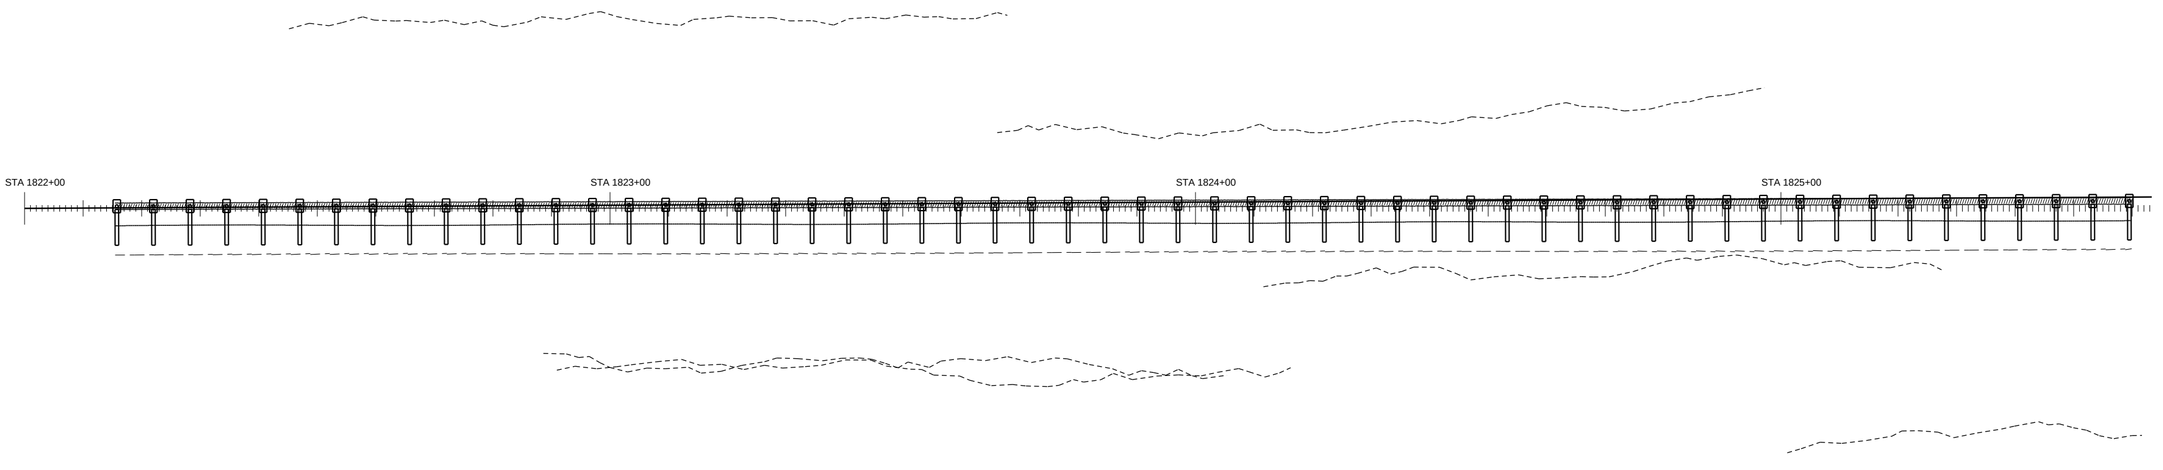


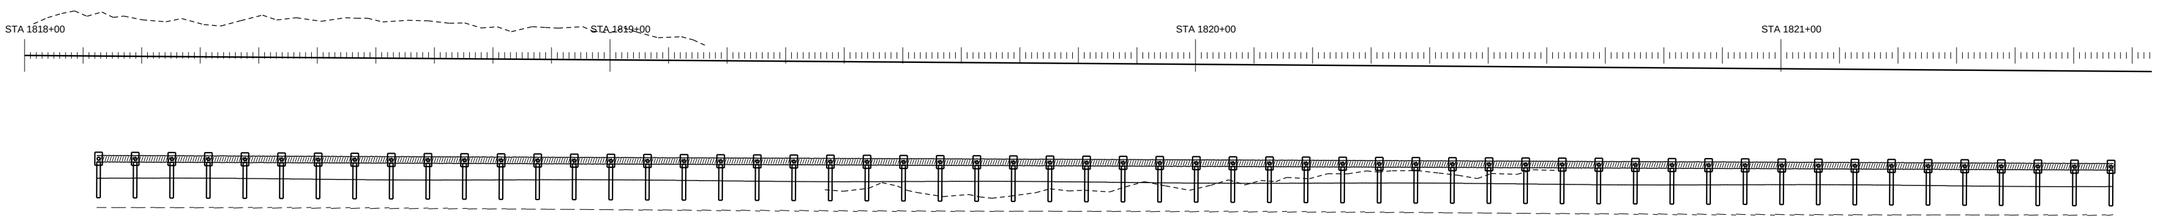


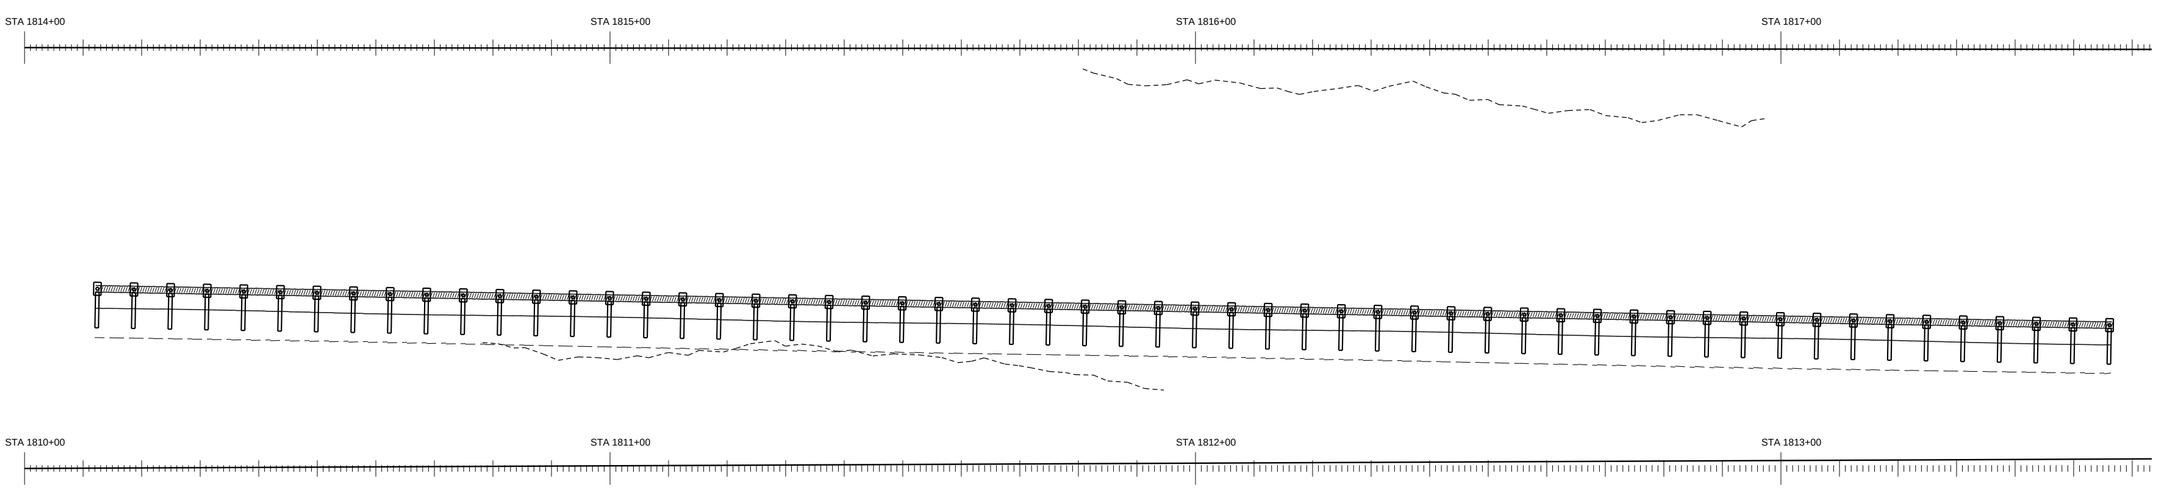


PAY ITEM 536-1-1 GUARDRAIL ROADWAY (TL-3)

PAY ITEM 536-85-24 END TREATMENT

GUARANTEED FENCE CORP

FIN. PROJ. ID 441234-1-52-01

SHEET 115 OF 120

SHEET NO. 215

ROADWAY PLAN SCALE: 1" = 20'

GUARANTEED FENCE CORP

FIN. PROJ. ID 441234-1-52-01

SHEET 116 OF 120

SHEET NO. 216

ROADWAY PLAN SCALE: 1" = 20'

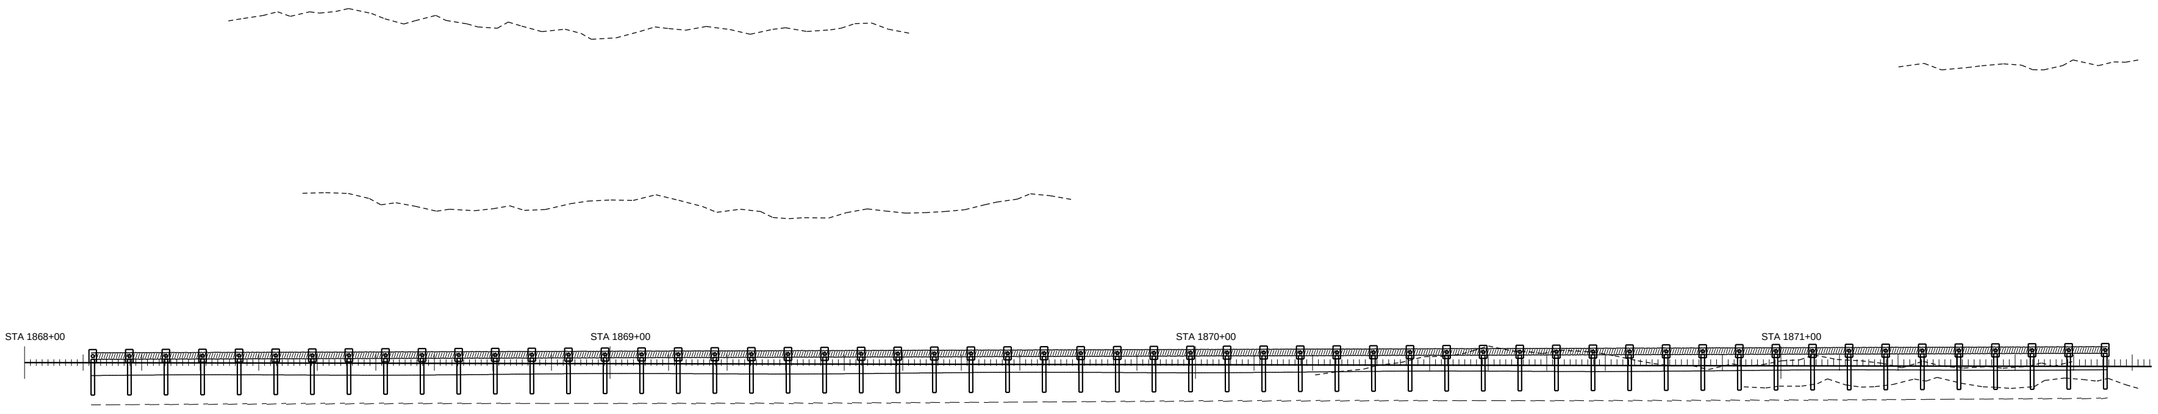


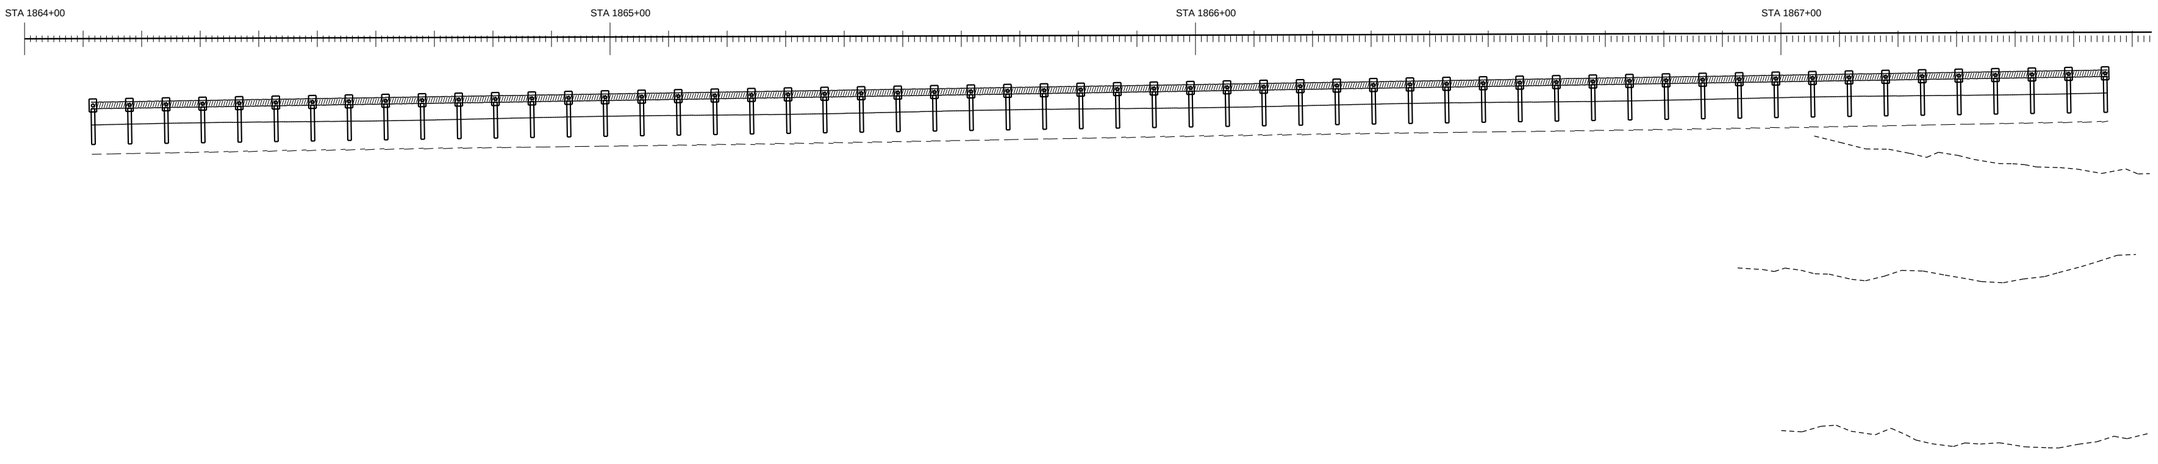


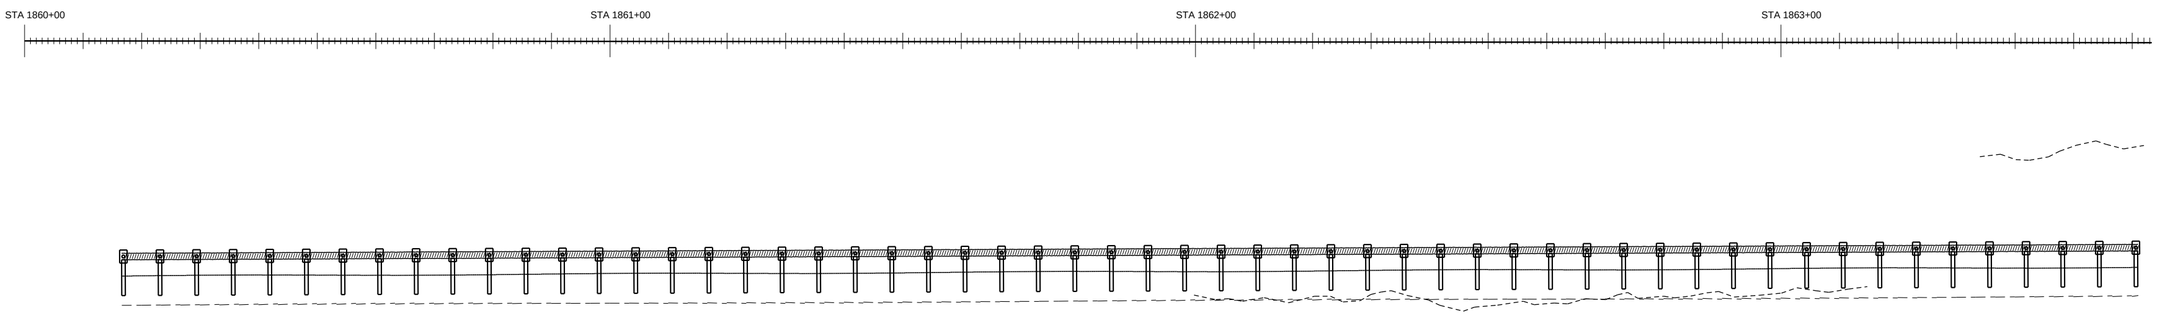


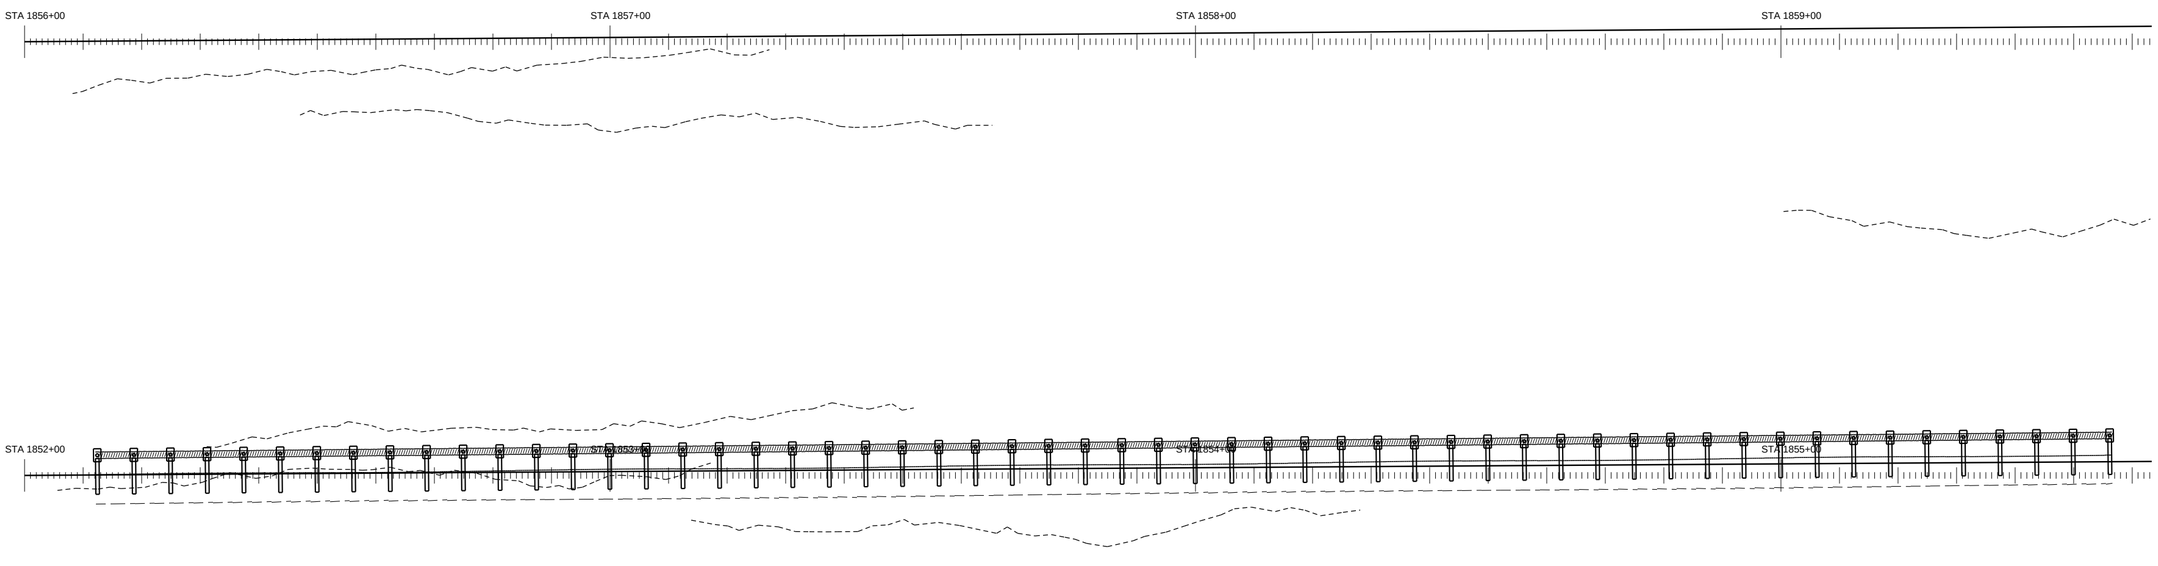


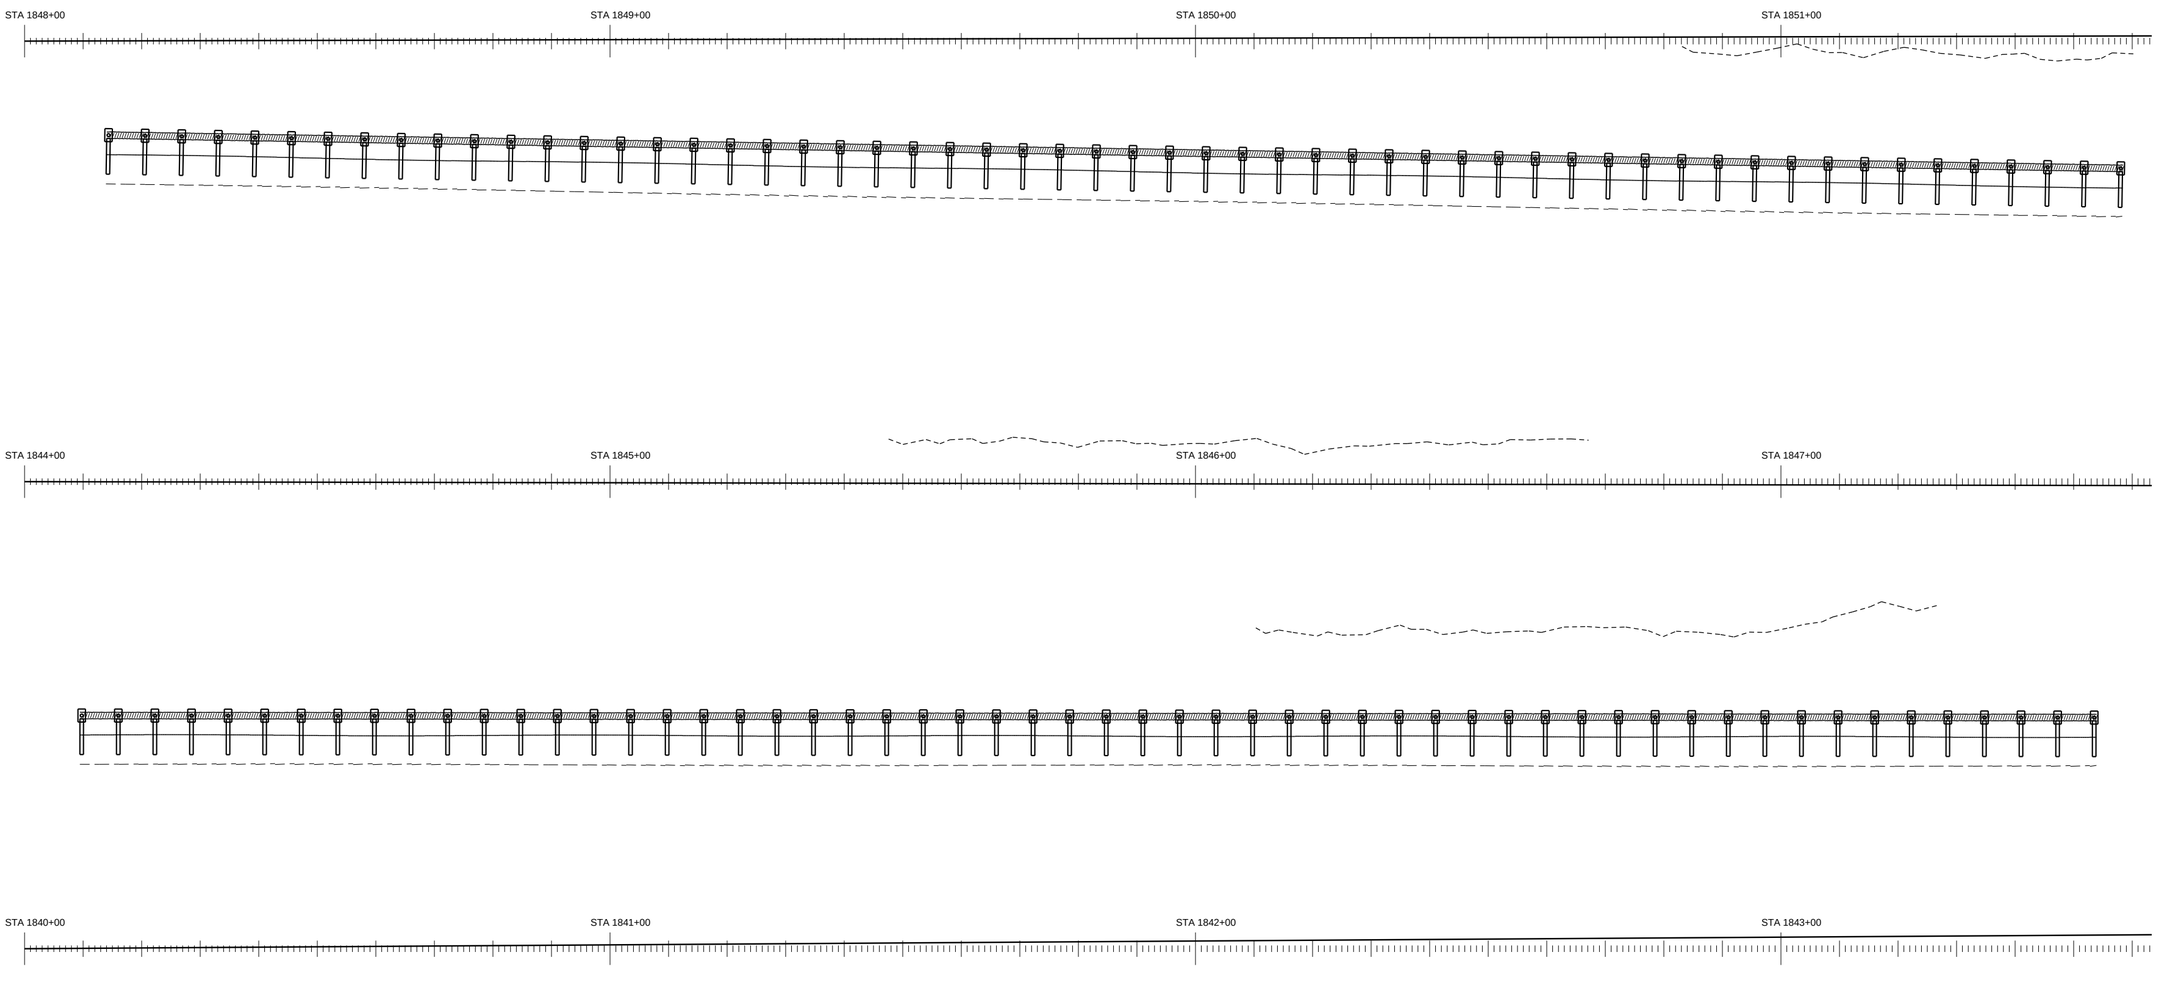

PAY ITEM 536-1-1 GUARDRAIL ROADWAY (TL-3)

PAY ITEM 536-85-24 END TREATMENT

GUARANTEED FENCE CORP

FIN. PROJ. ID 441234-1-52-01

SHEET 117 OF 120

SHEET NO. 217

ROADWAY PLAN SCALE: 1" = 20'

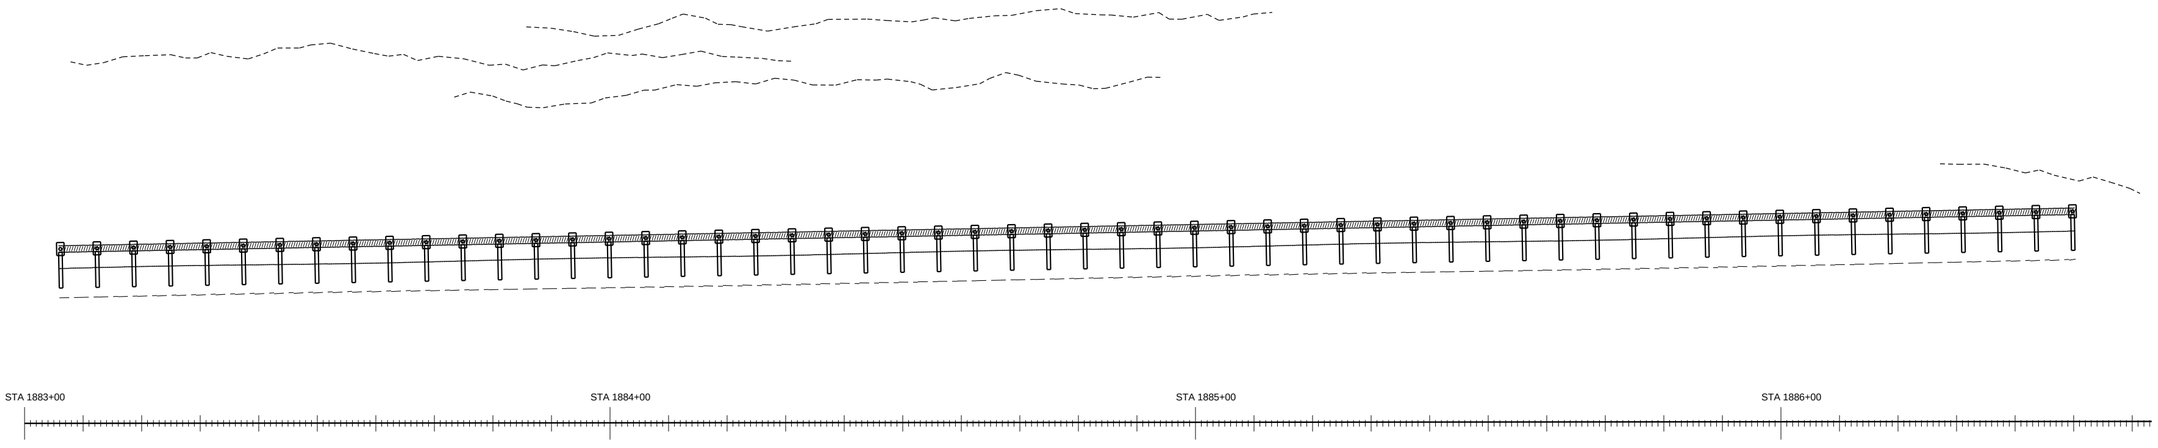


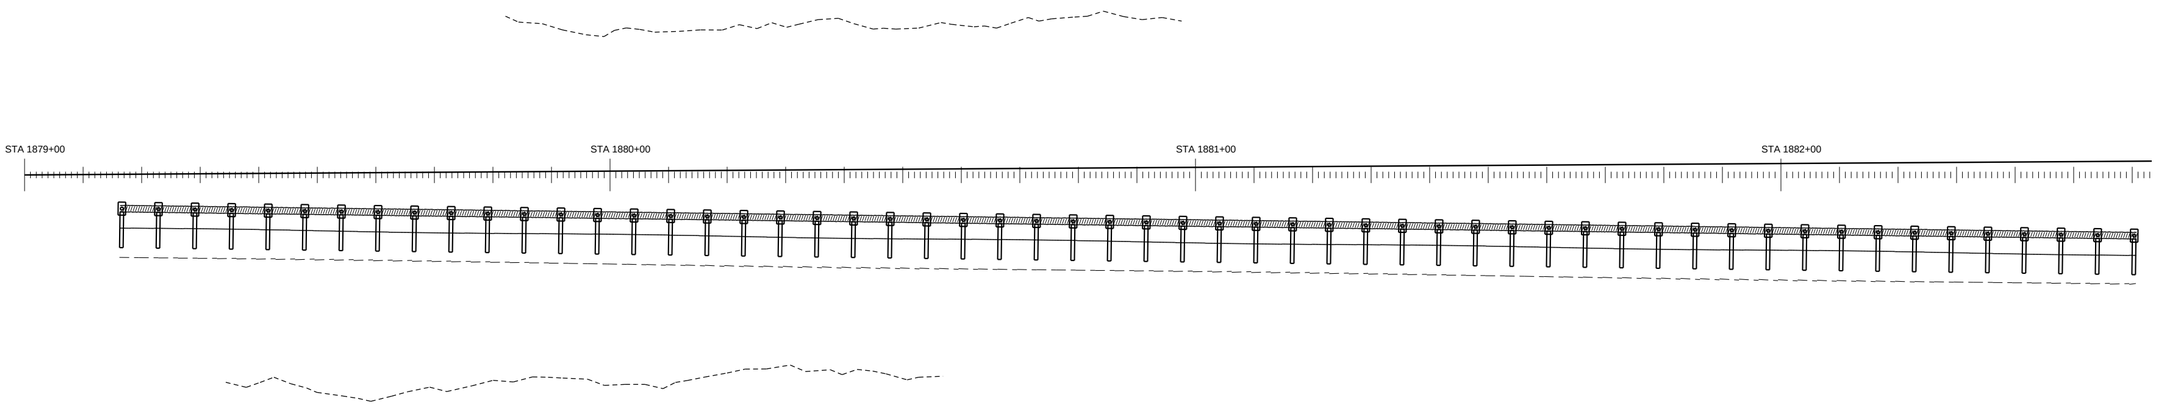


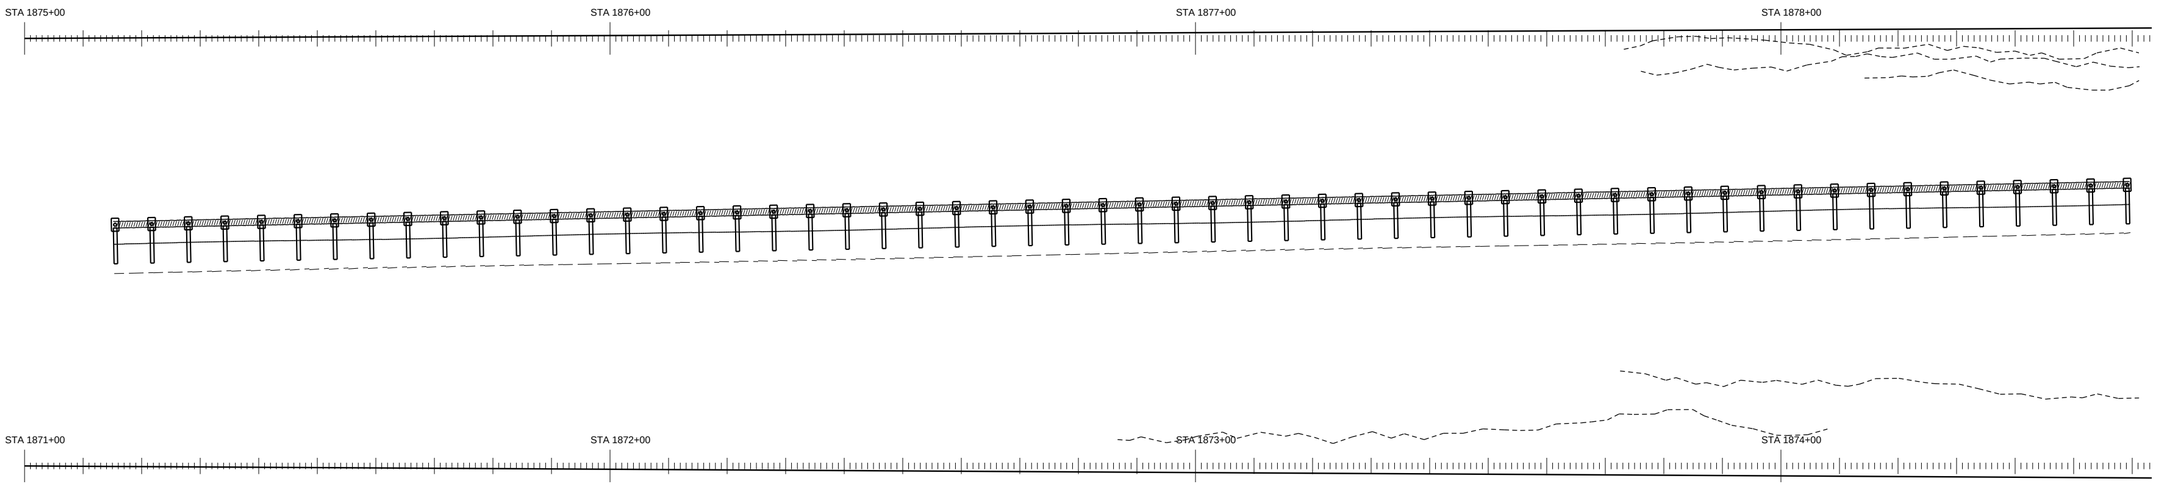


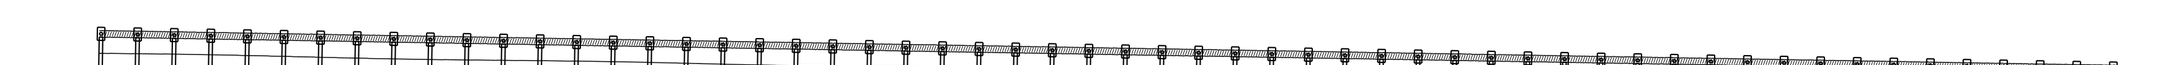


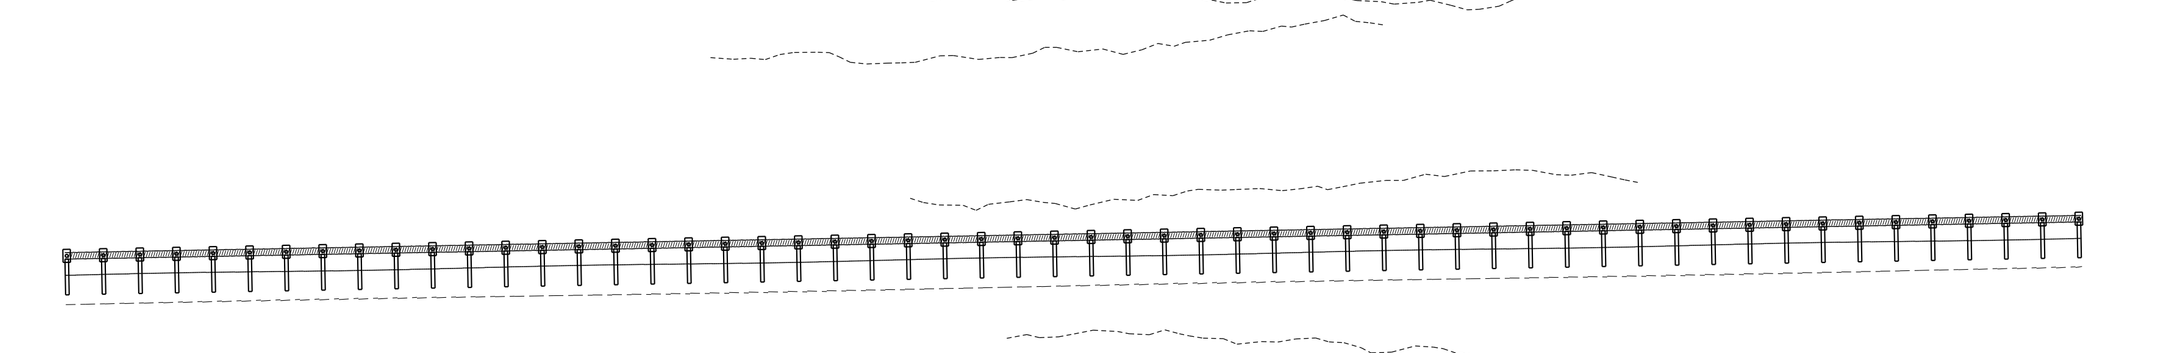











PAY ITEM 536-1-1 GUARDRAIL ROADWAY (TL-3)

PAY ITEM 536-85-24 END TREATMENT

GUARANTEED FENCE CORP

FIN. PROJ. ID 441234-1-52-01

SHEET 118 OF 120

SHEET NO. 218

ROADWAY PLAN SCALE: 1" = 20'

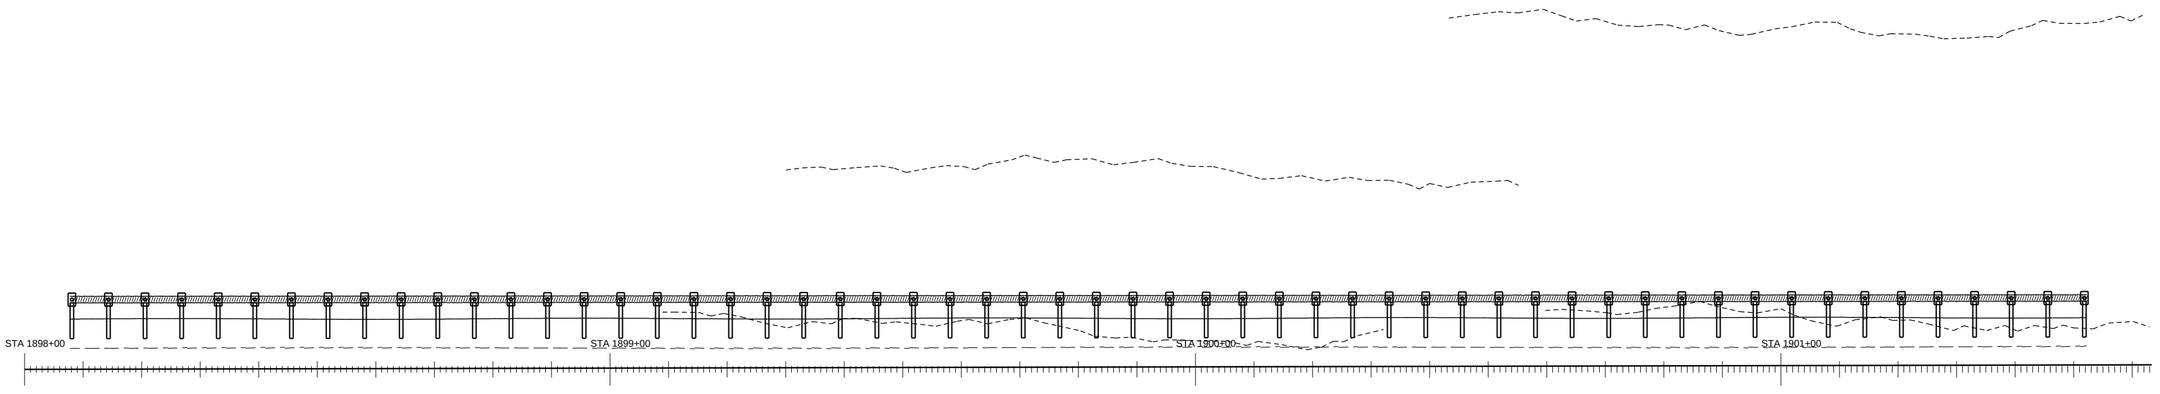


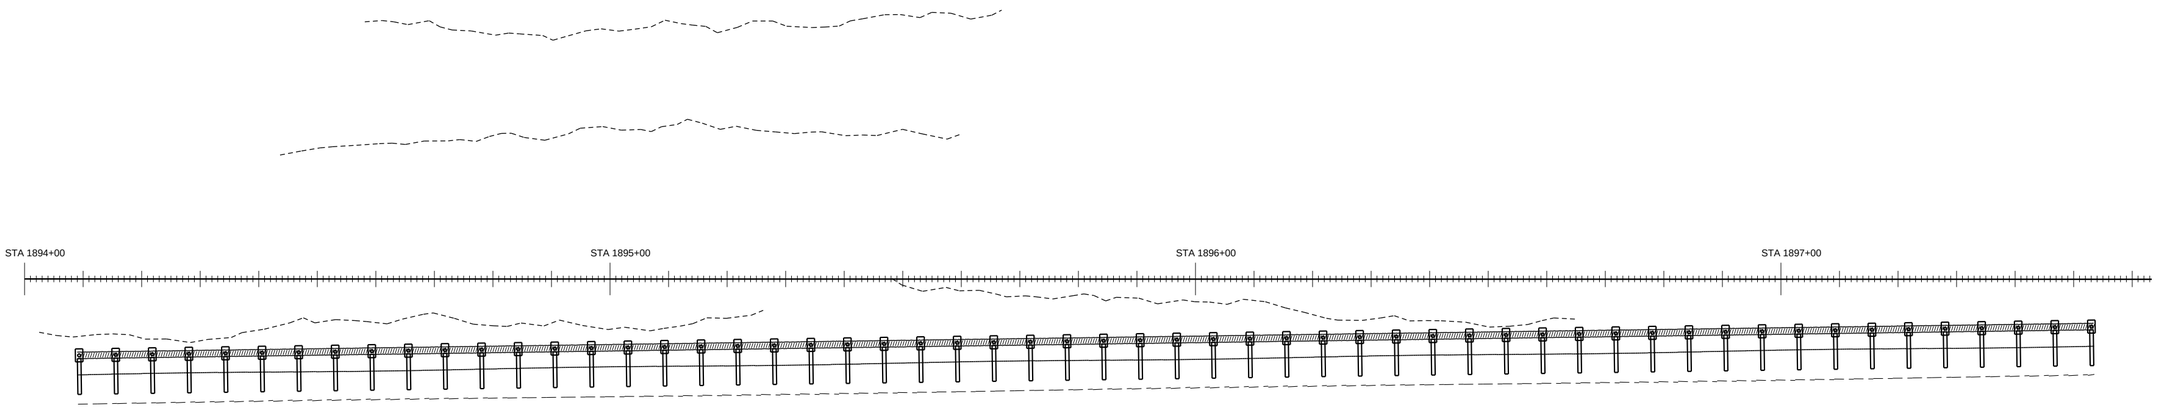


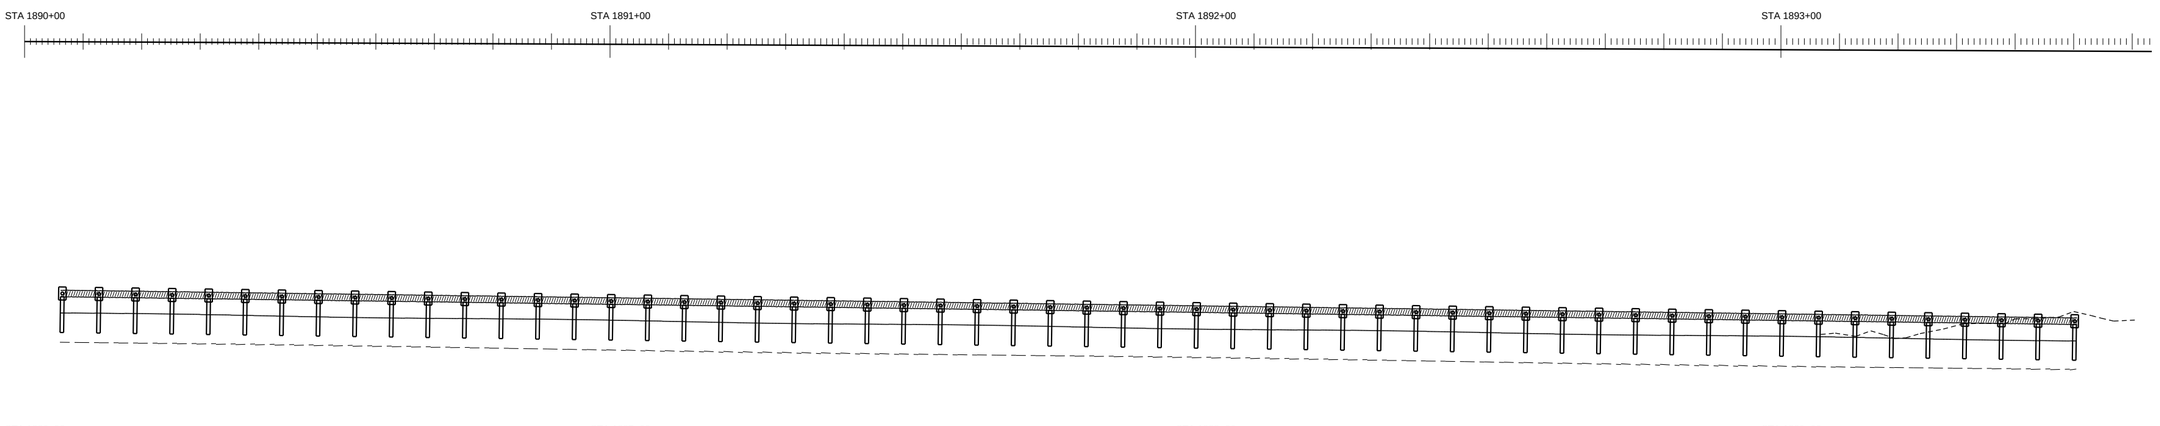

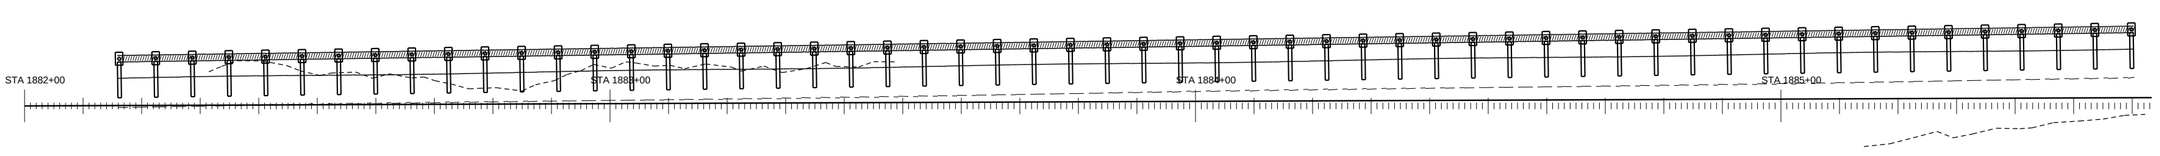


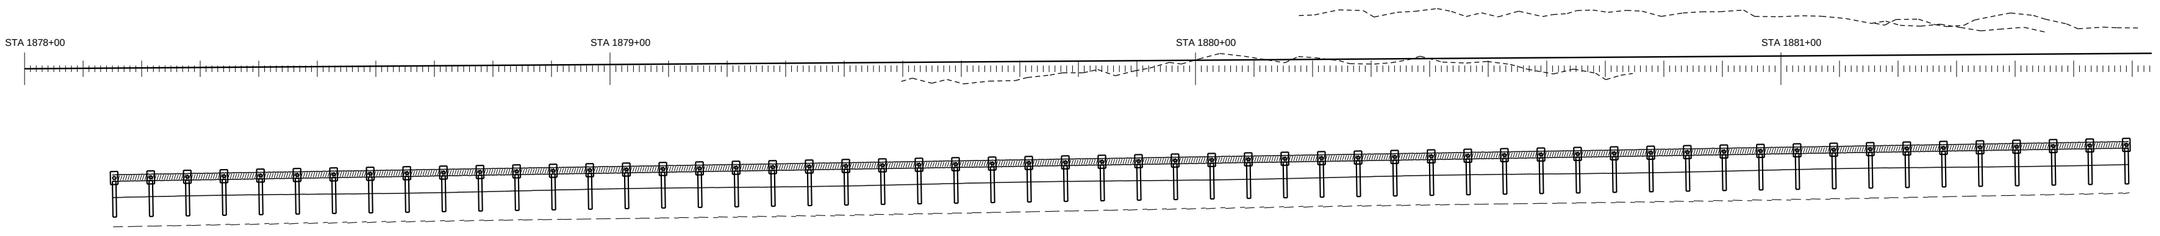


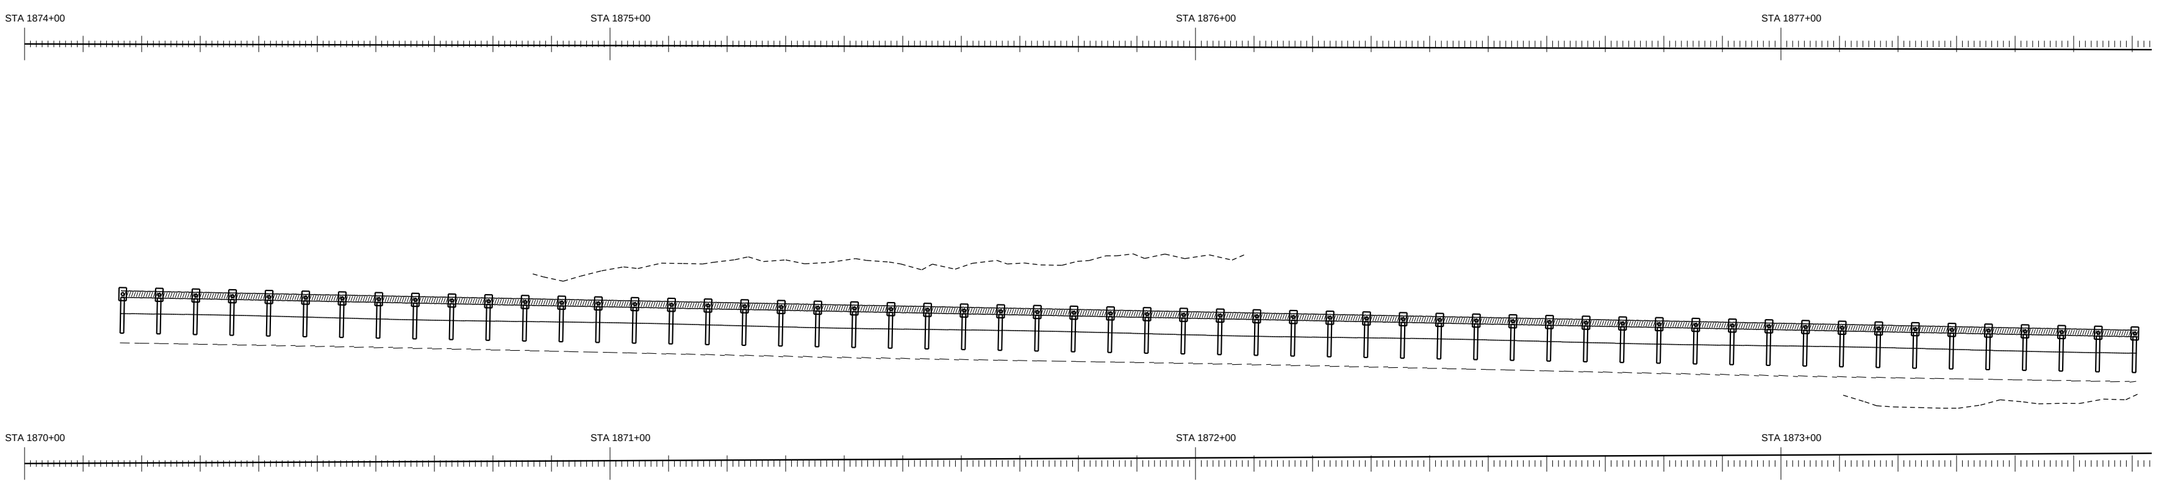


PAY ITEM 536-1-1 GUARDRAIL ROADWAY (TL-3)

PAY ITEM 536-85-24 END TREATMENT

GUARANTEED FENCE CORP

FIN. PROJ. ID 441234-1-52-01

SHEET 119 OF 120

SHEET NO. 219

ROADWAY PLAN SCALE: 1" = 20'




PAY ITEM 536-1-1 GUARDRAIL ROADWAY (TL-3)

PAY ITEM 536-85-24 END TREATMENT

GUARANTEED FENCE CORP

FIN. PROJ. ID 441234-1-52-01

SHEET 120 OF 120

SHEET NO. 220

ROADWAY PLAN SCALE: 1" = 20'

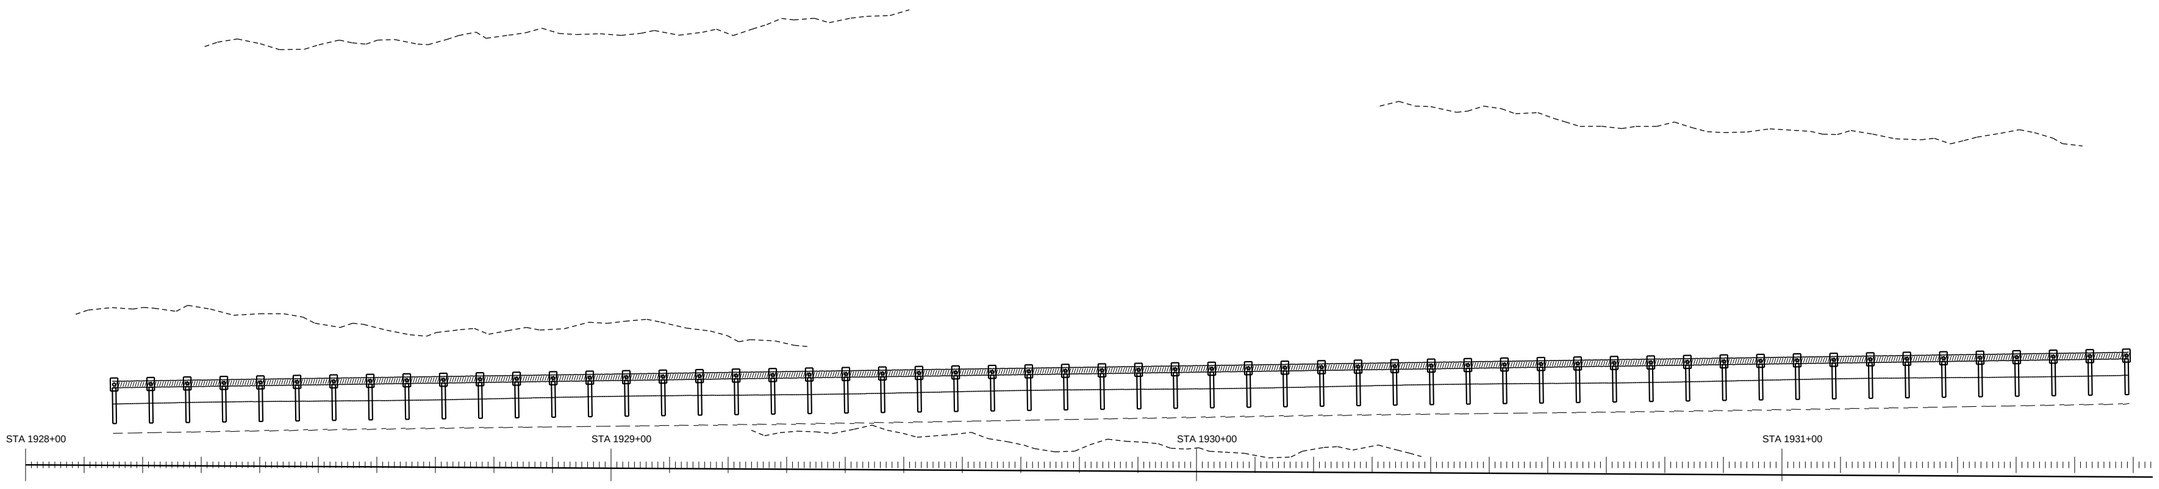


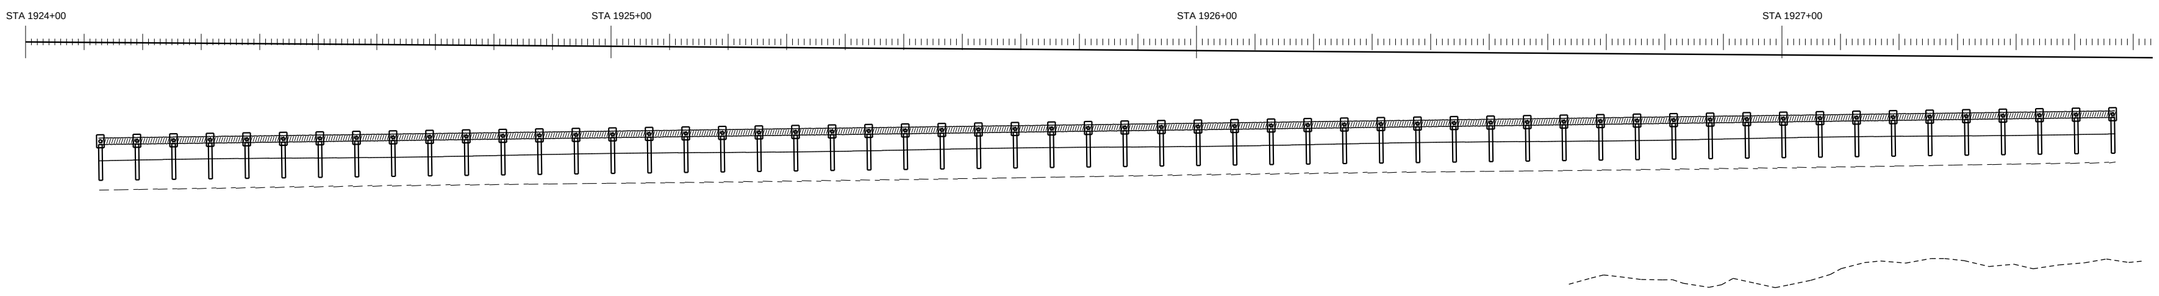


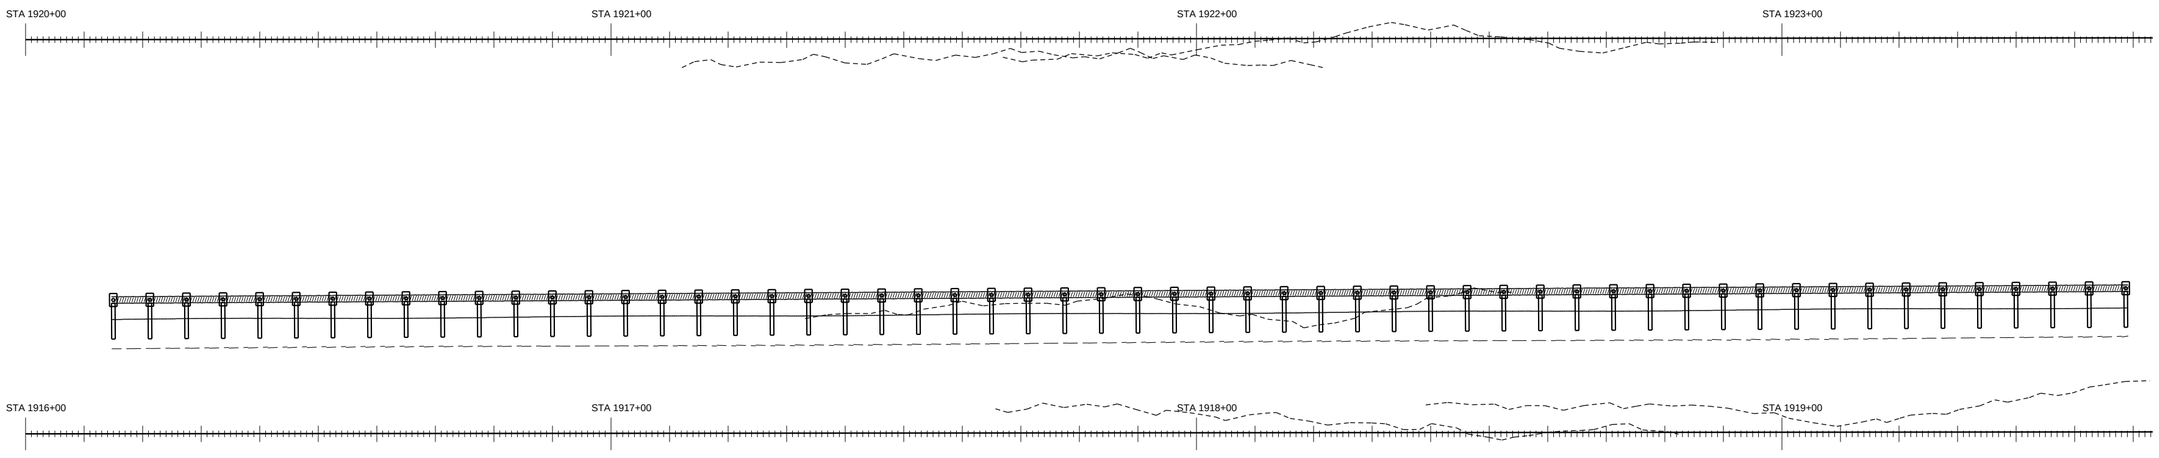





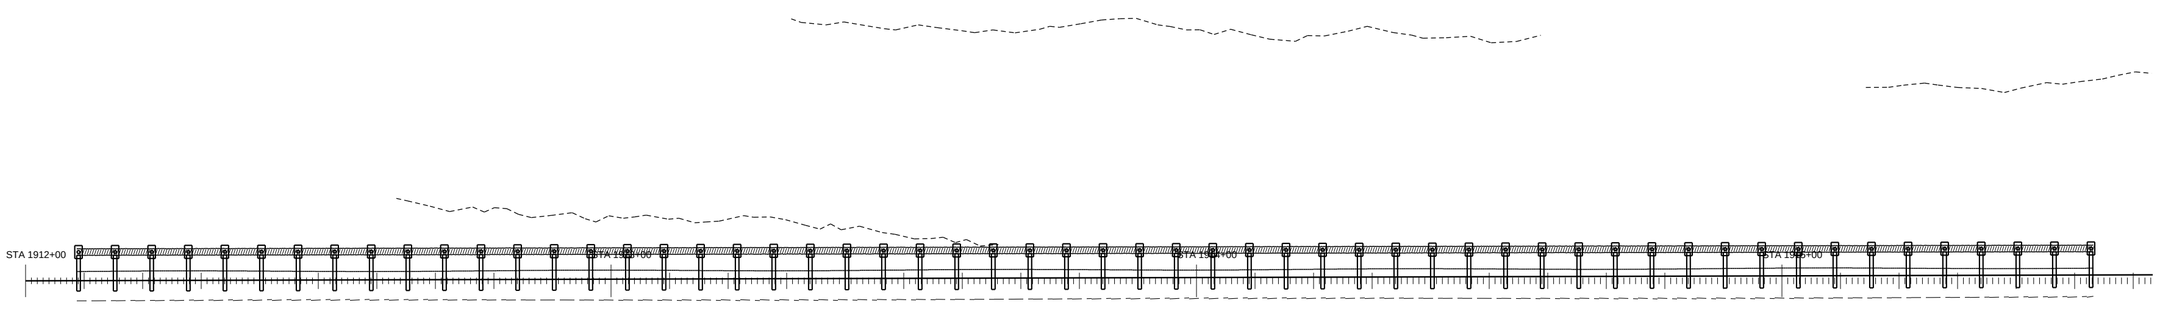


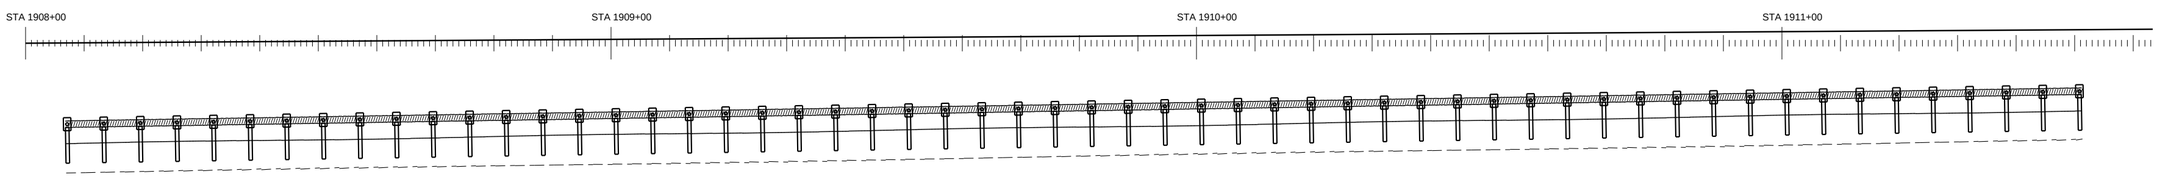


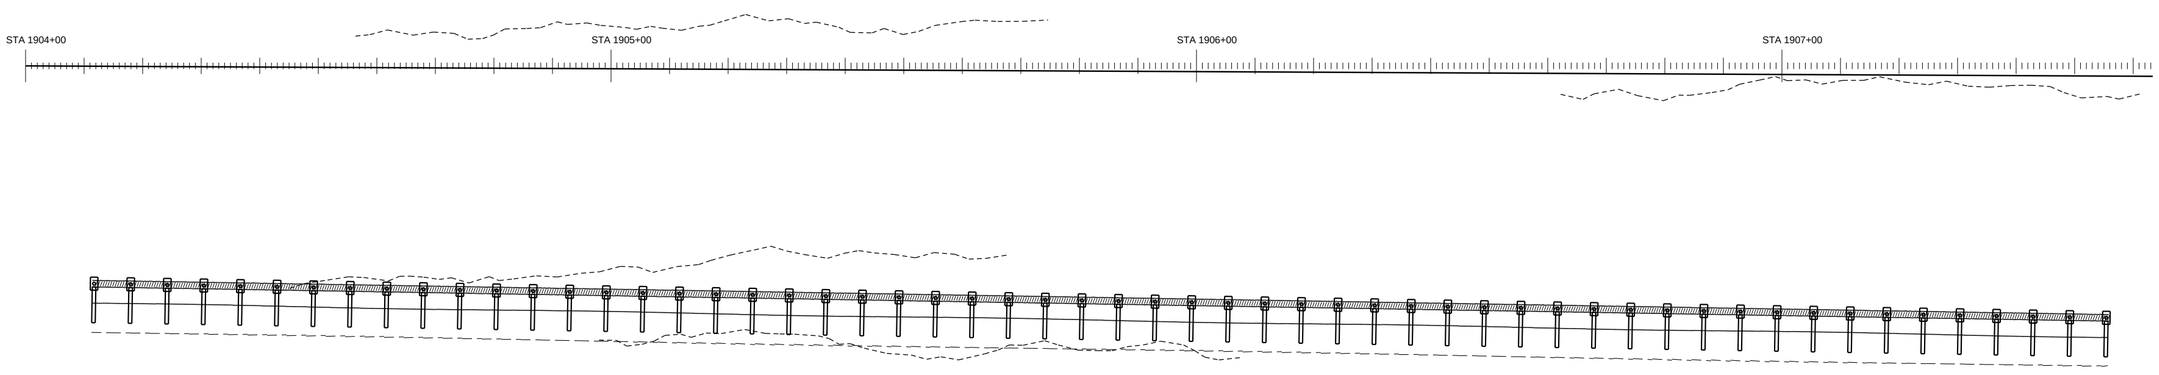

PAY ITEM 536-1-1 GUARDRAIL ROADWAY (TL-3)

PAY ITEM 536-85-24 END TREATMENT